


CONSTRUCTION DRAWINGS


INTERIOR DESIGN | ARCHITECTURE

RESIDENTIAL PROJECTS


Across India

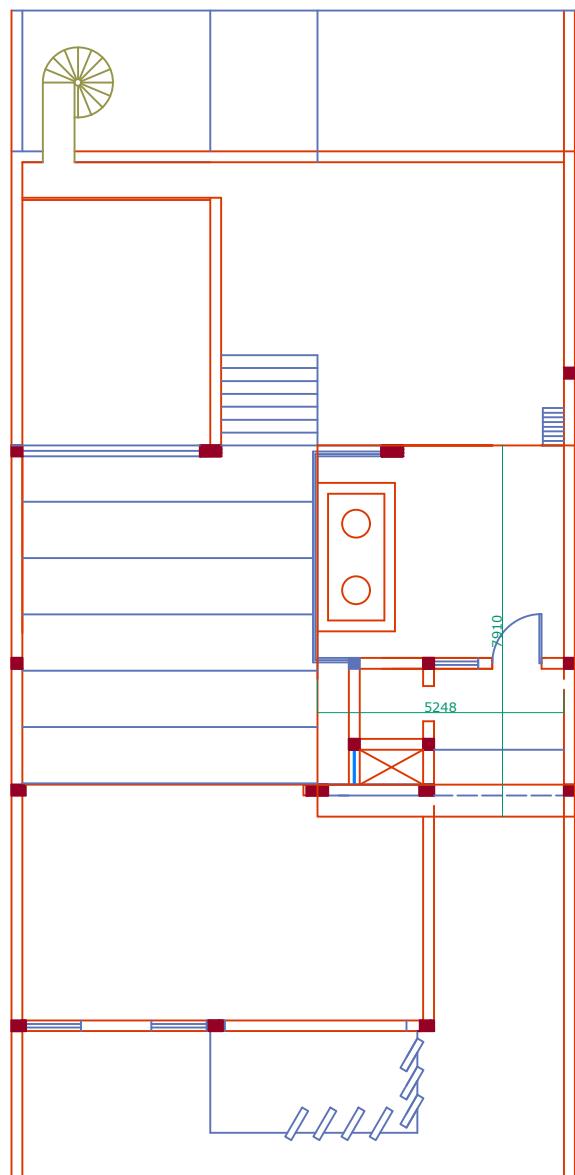


UPPER TERRACE

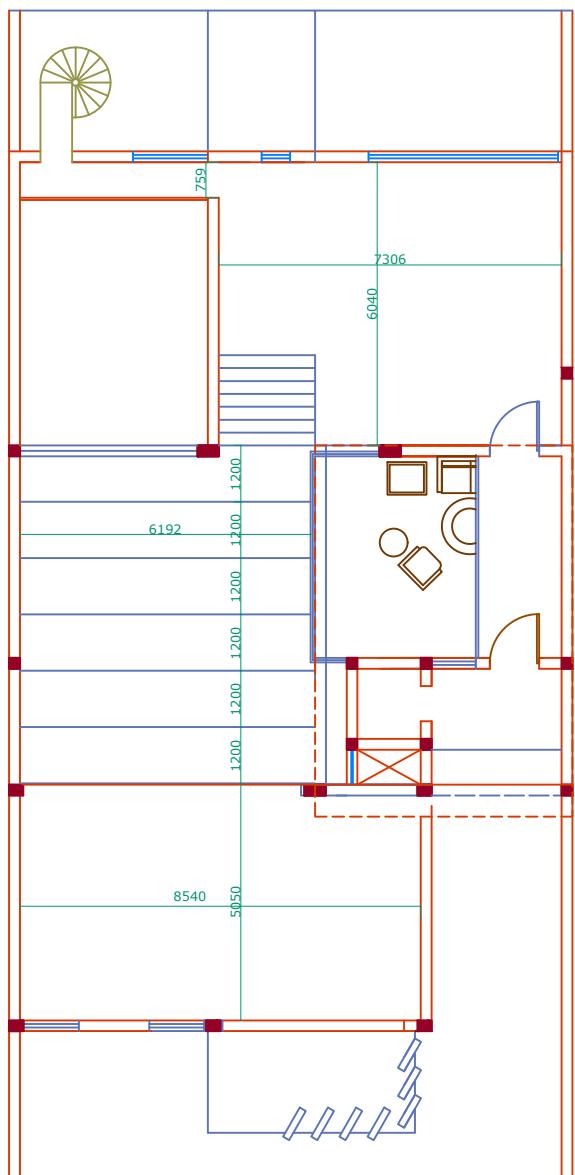


TERRACE FLOOR

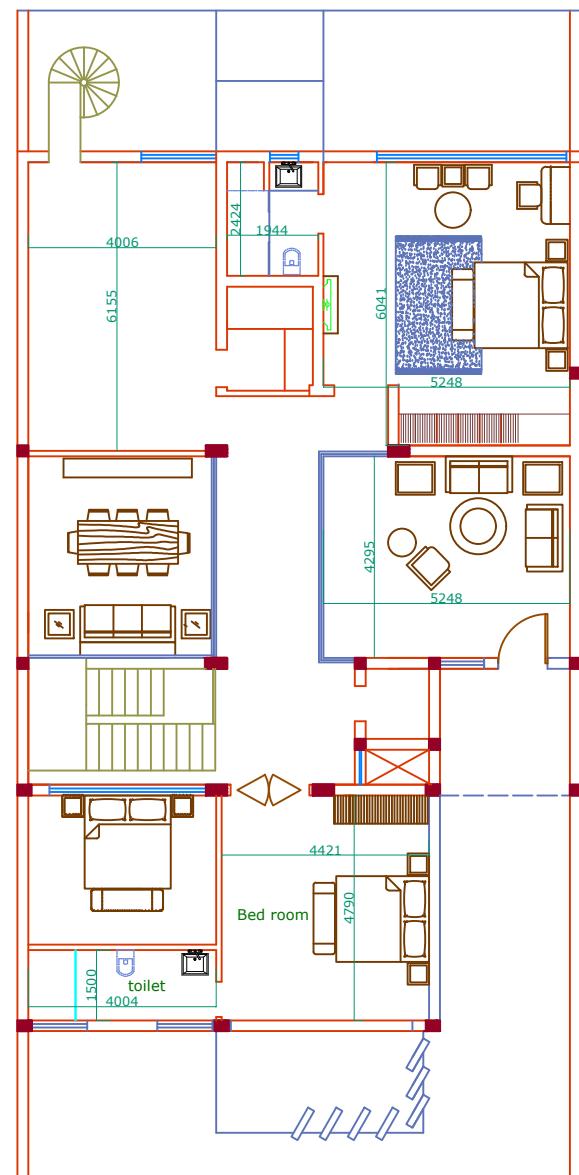


SECOND FLOOR

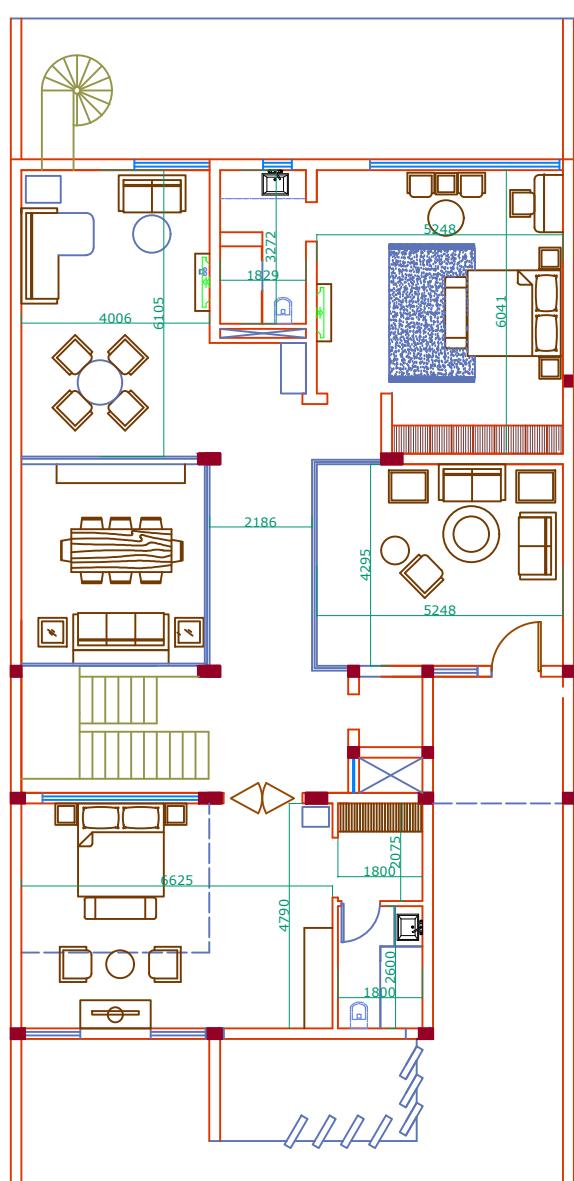


FIRST FLOOR

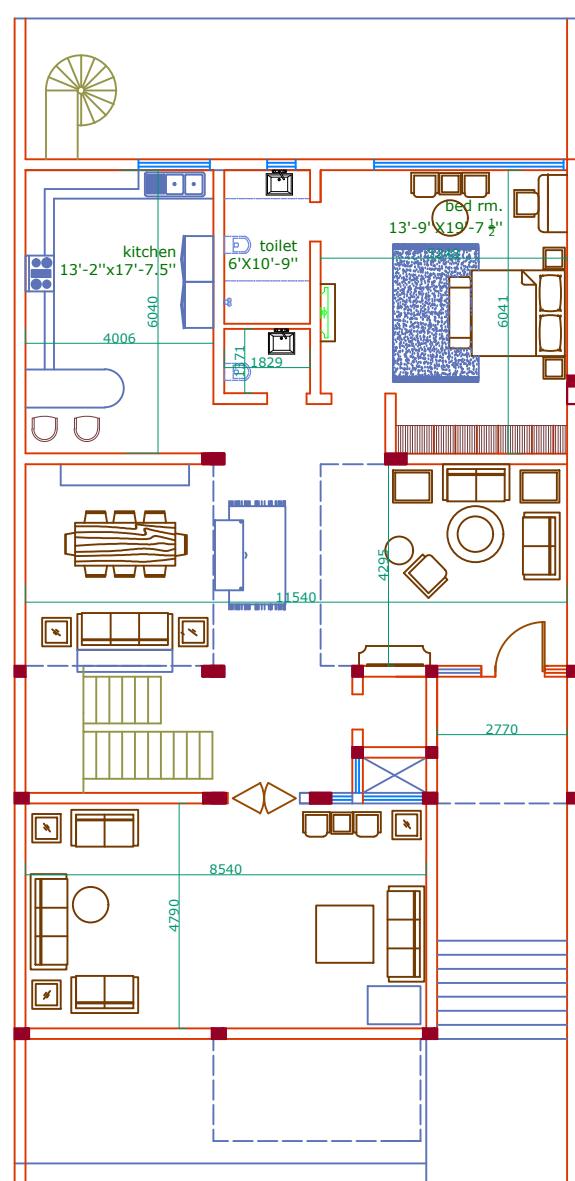



GROUND FLOOR

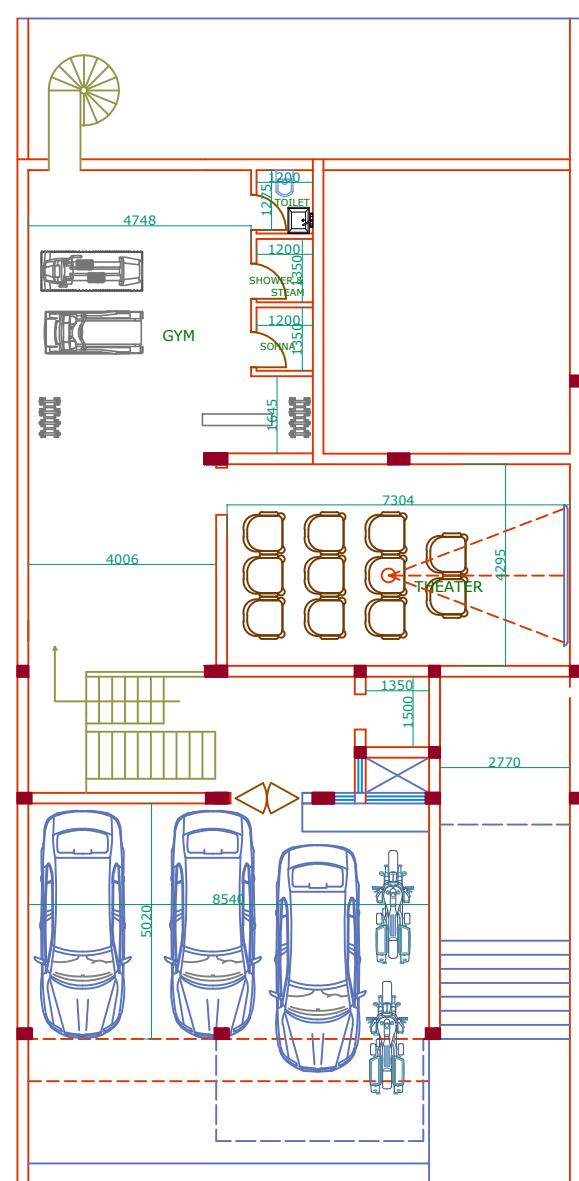



BASEMENT

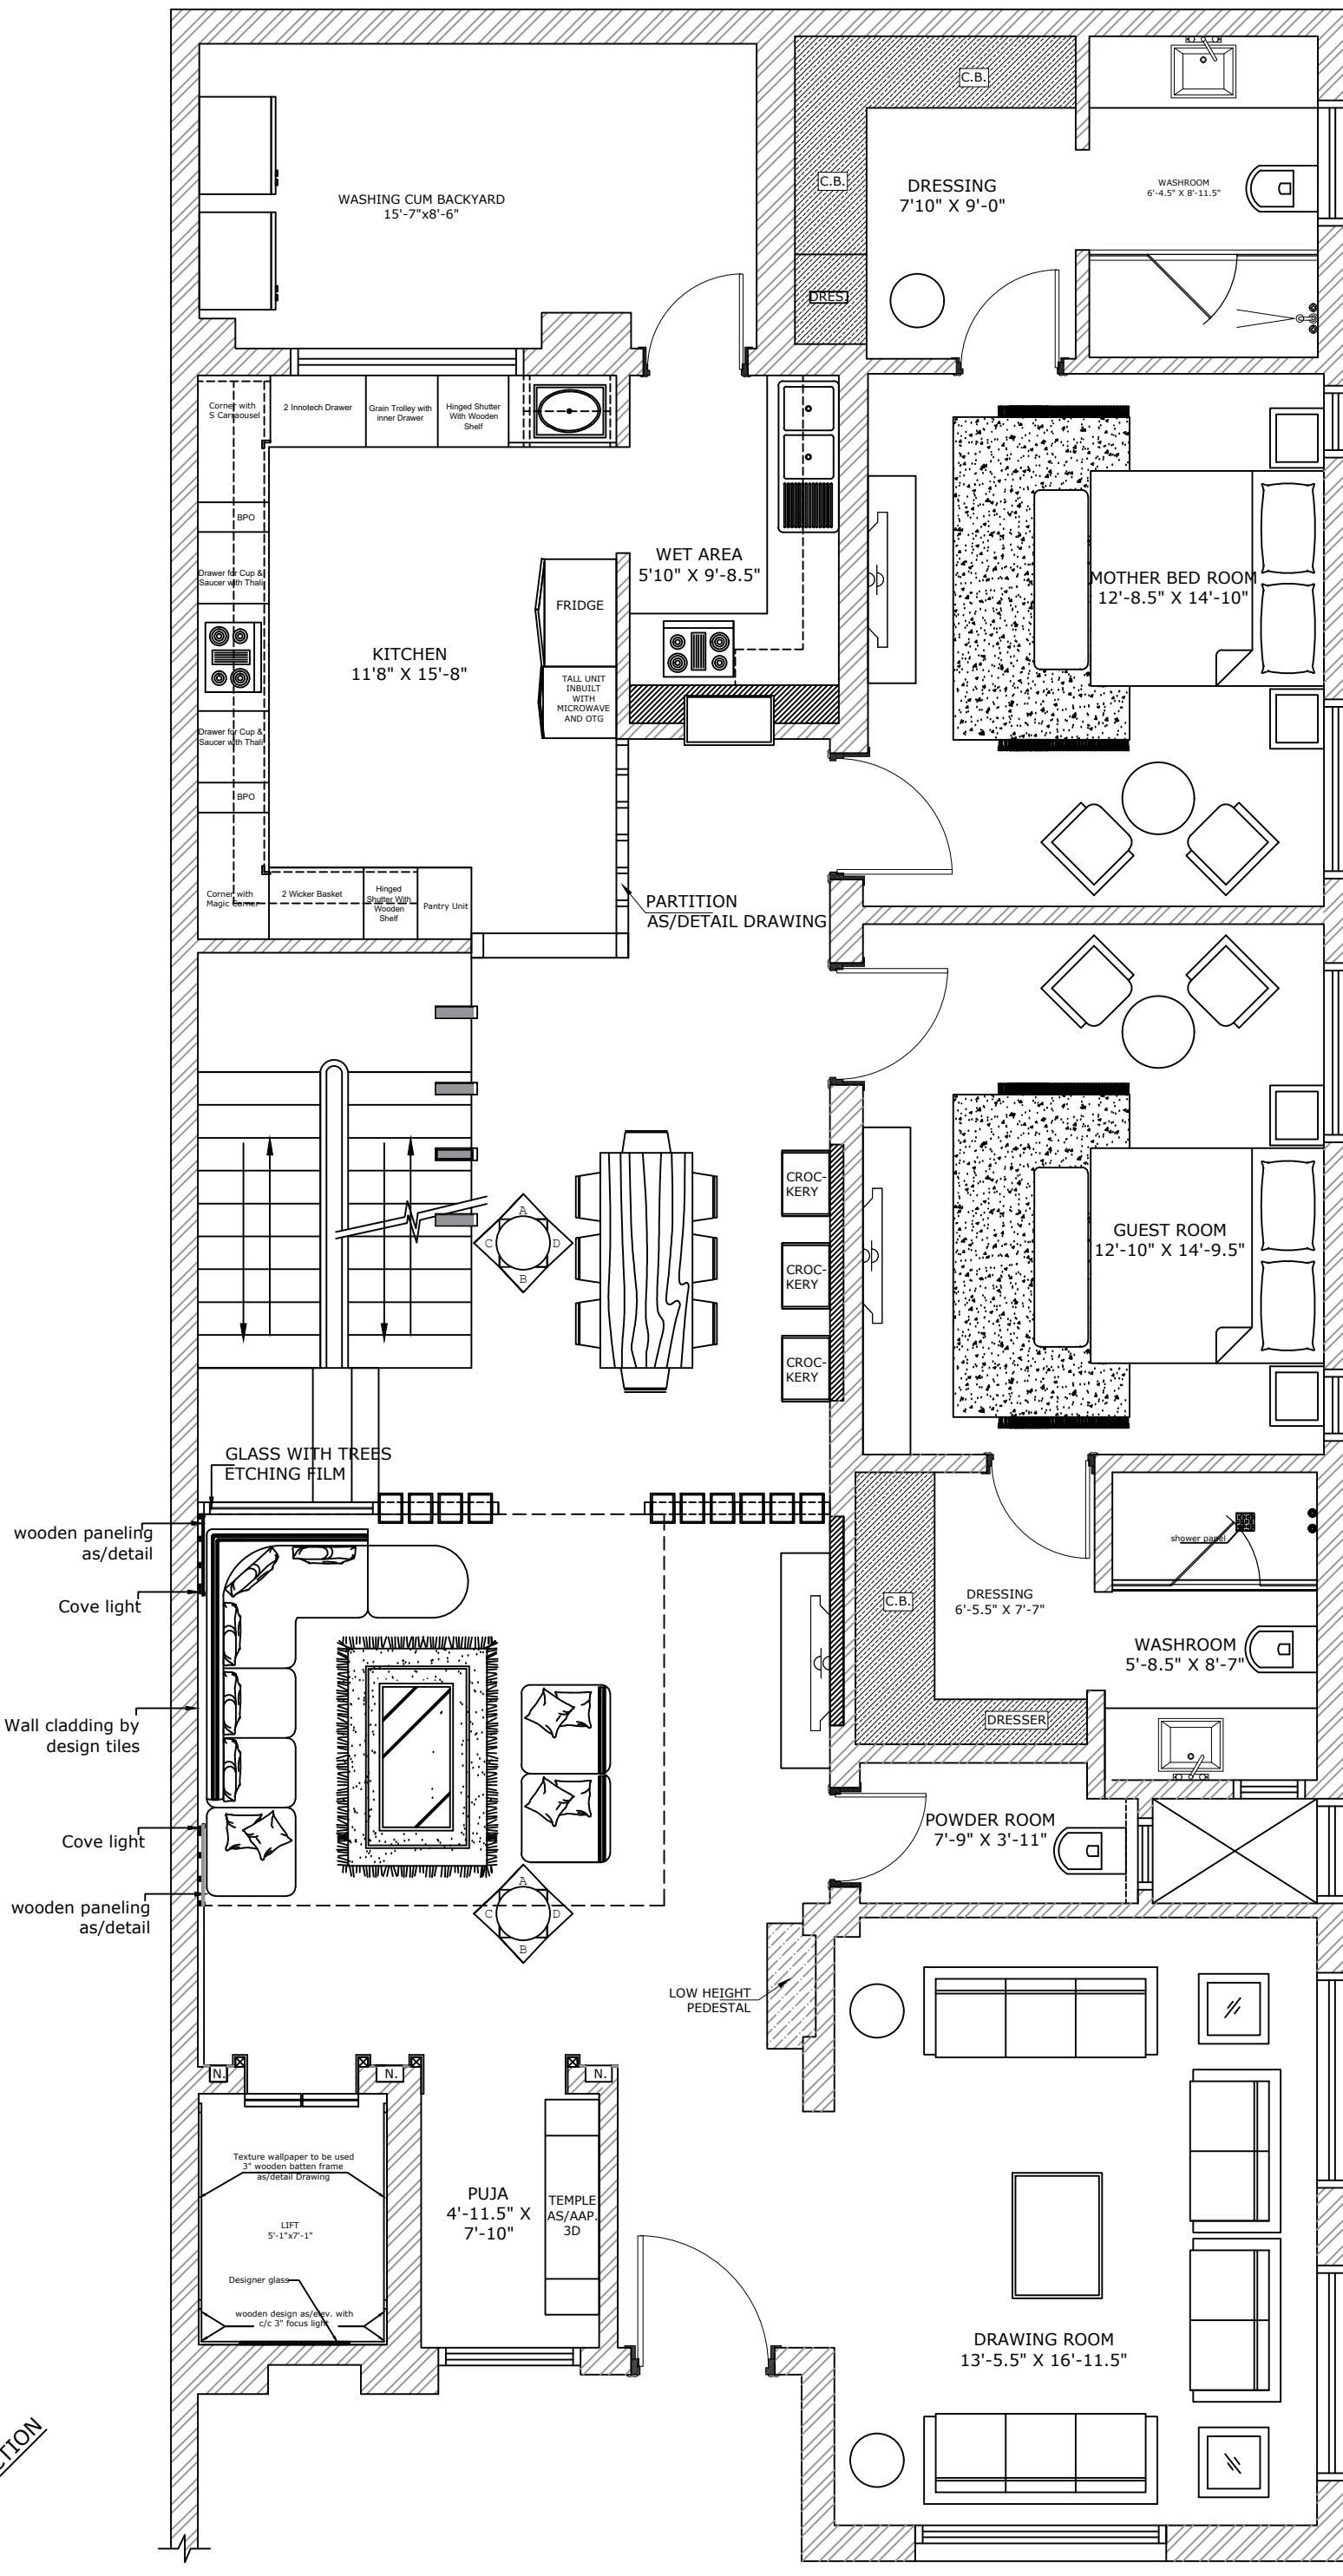


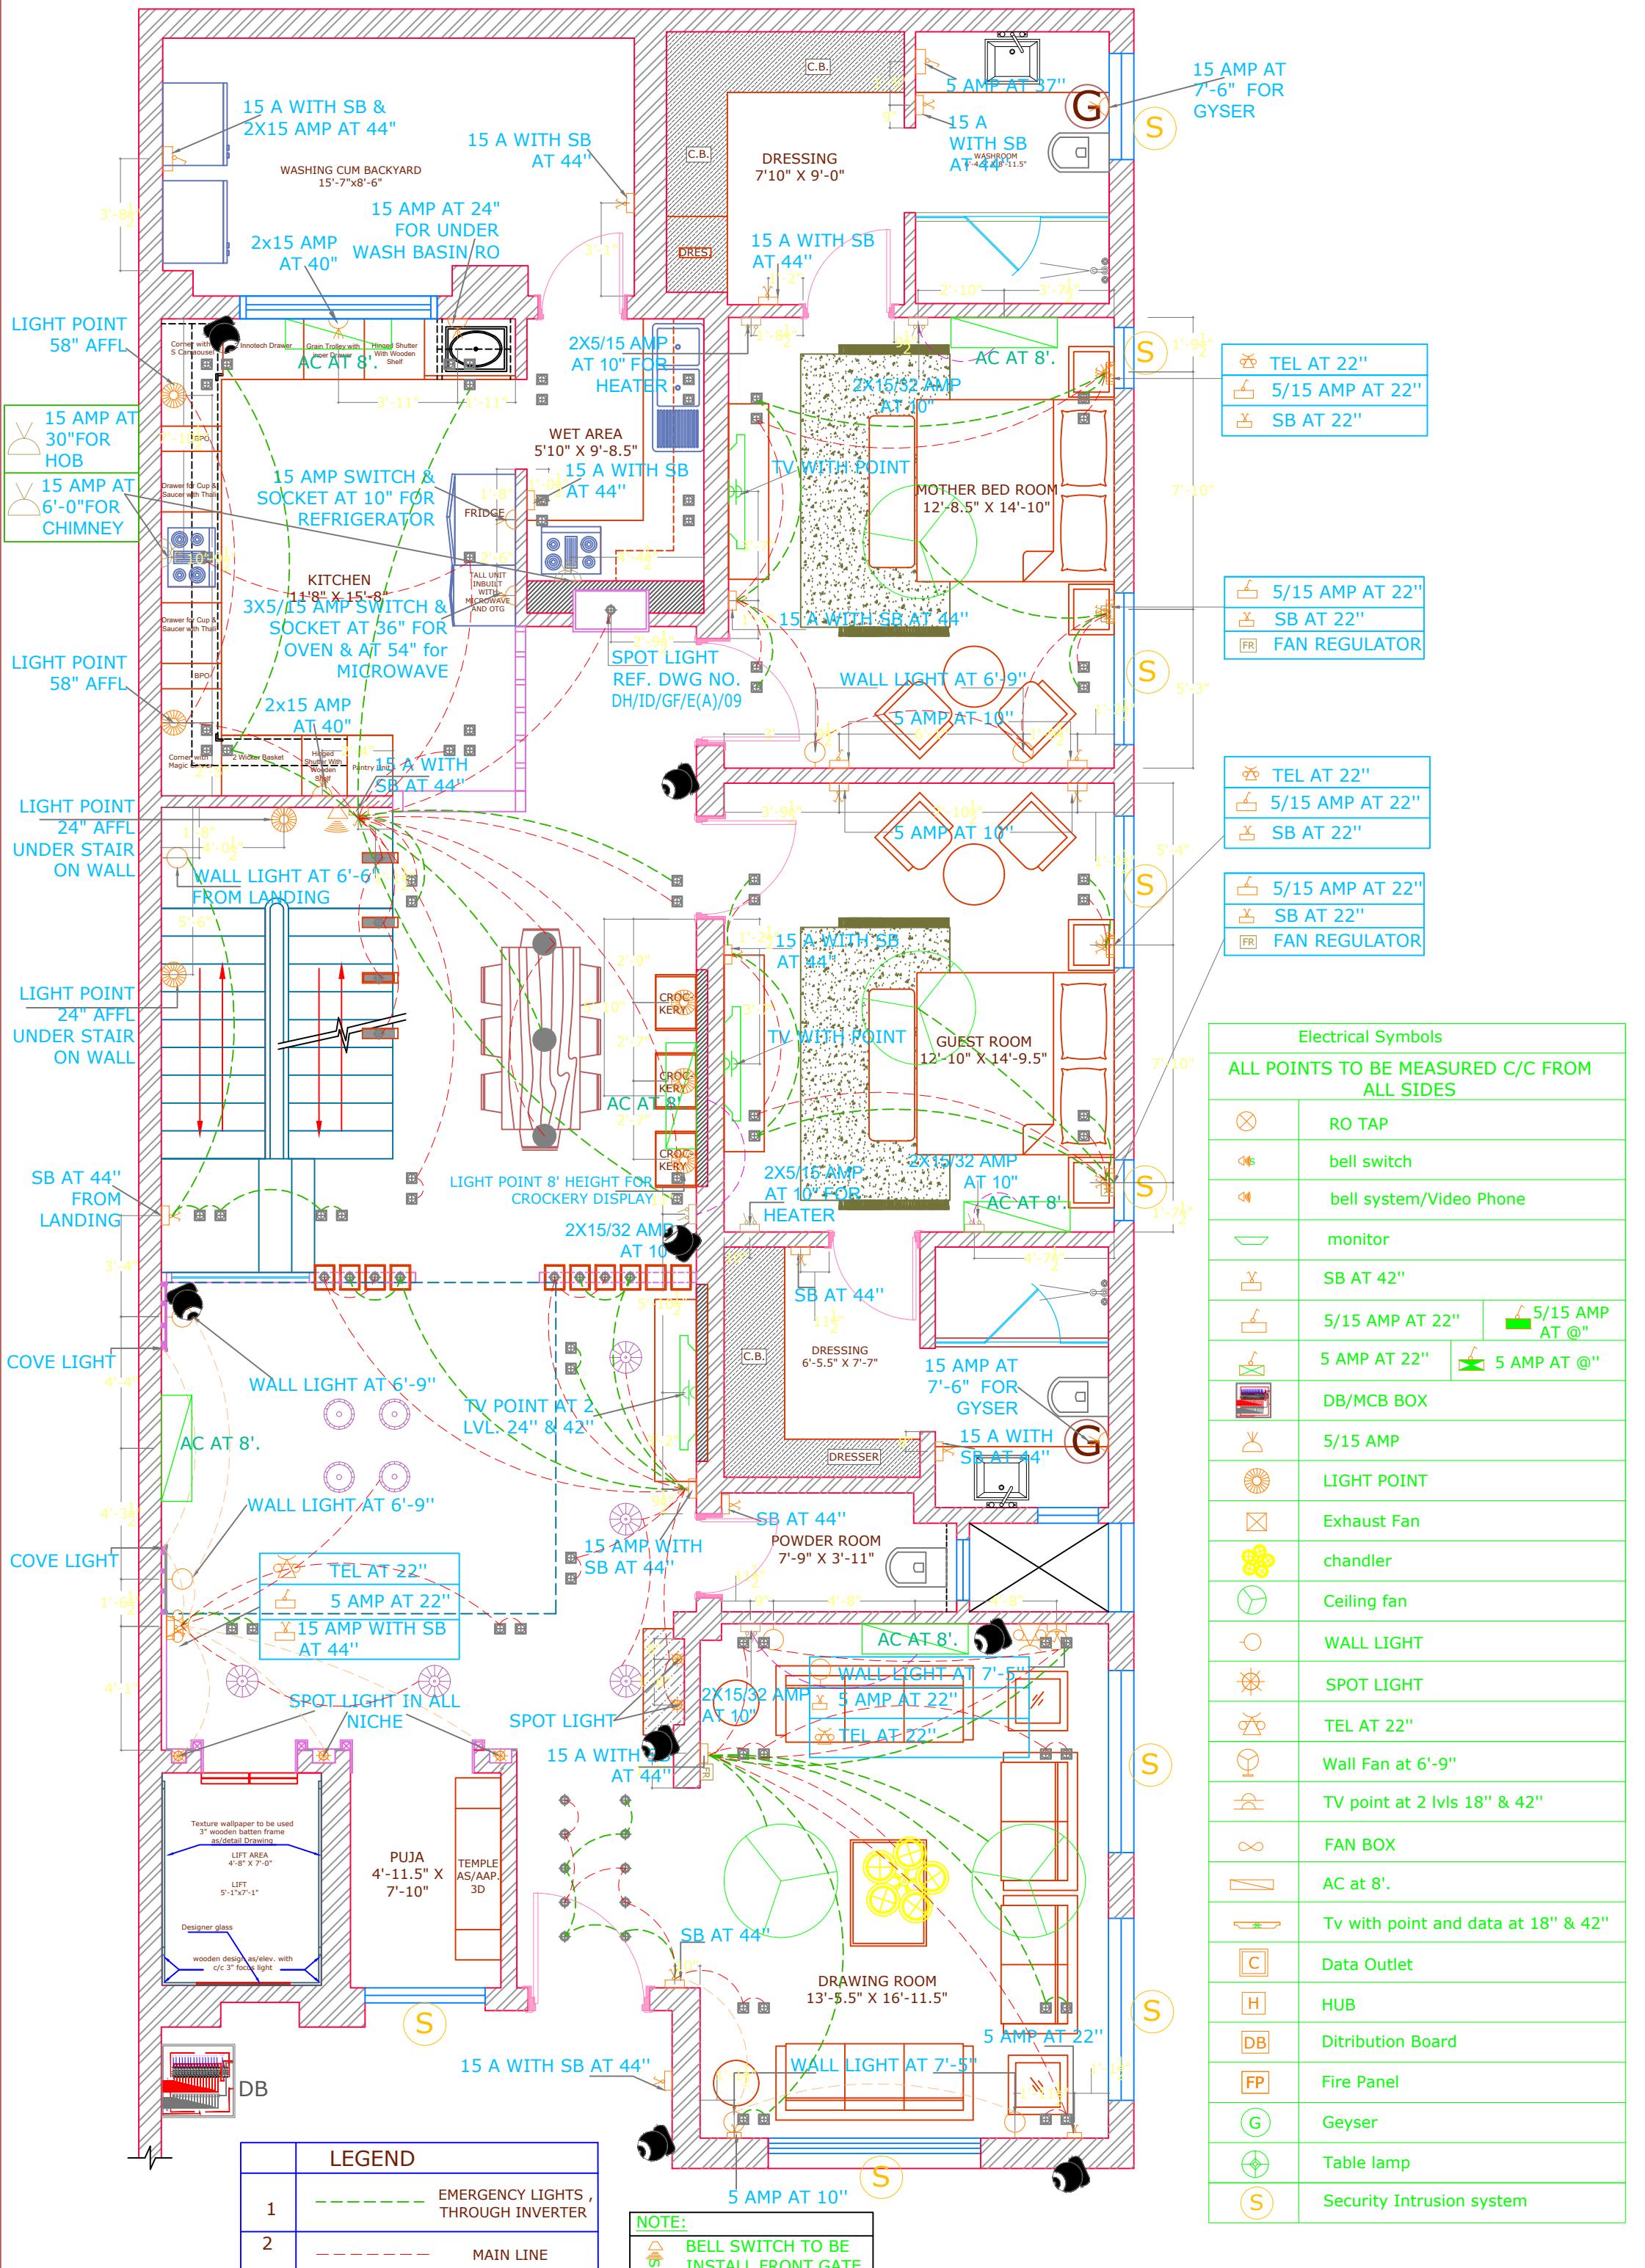

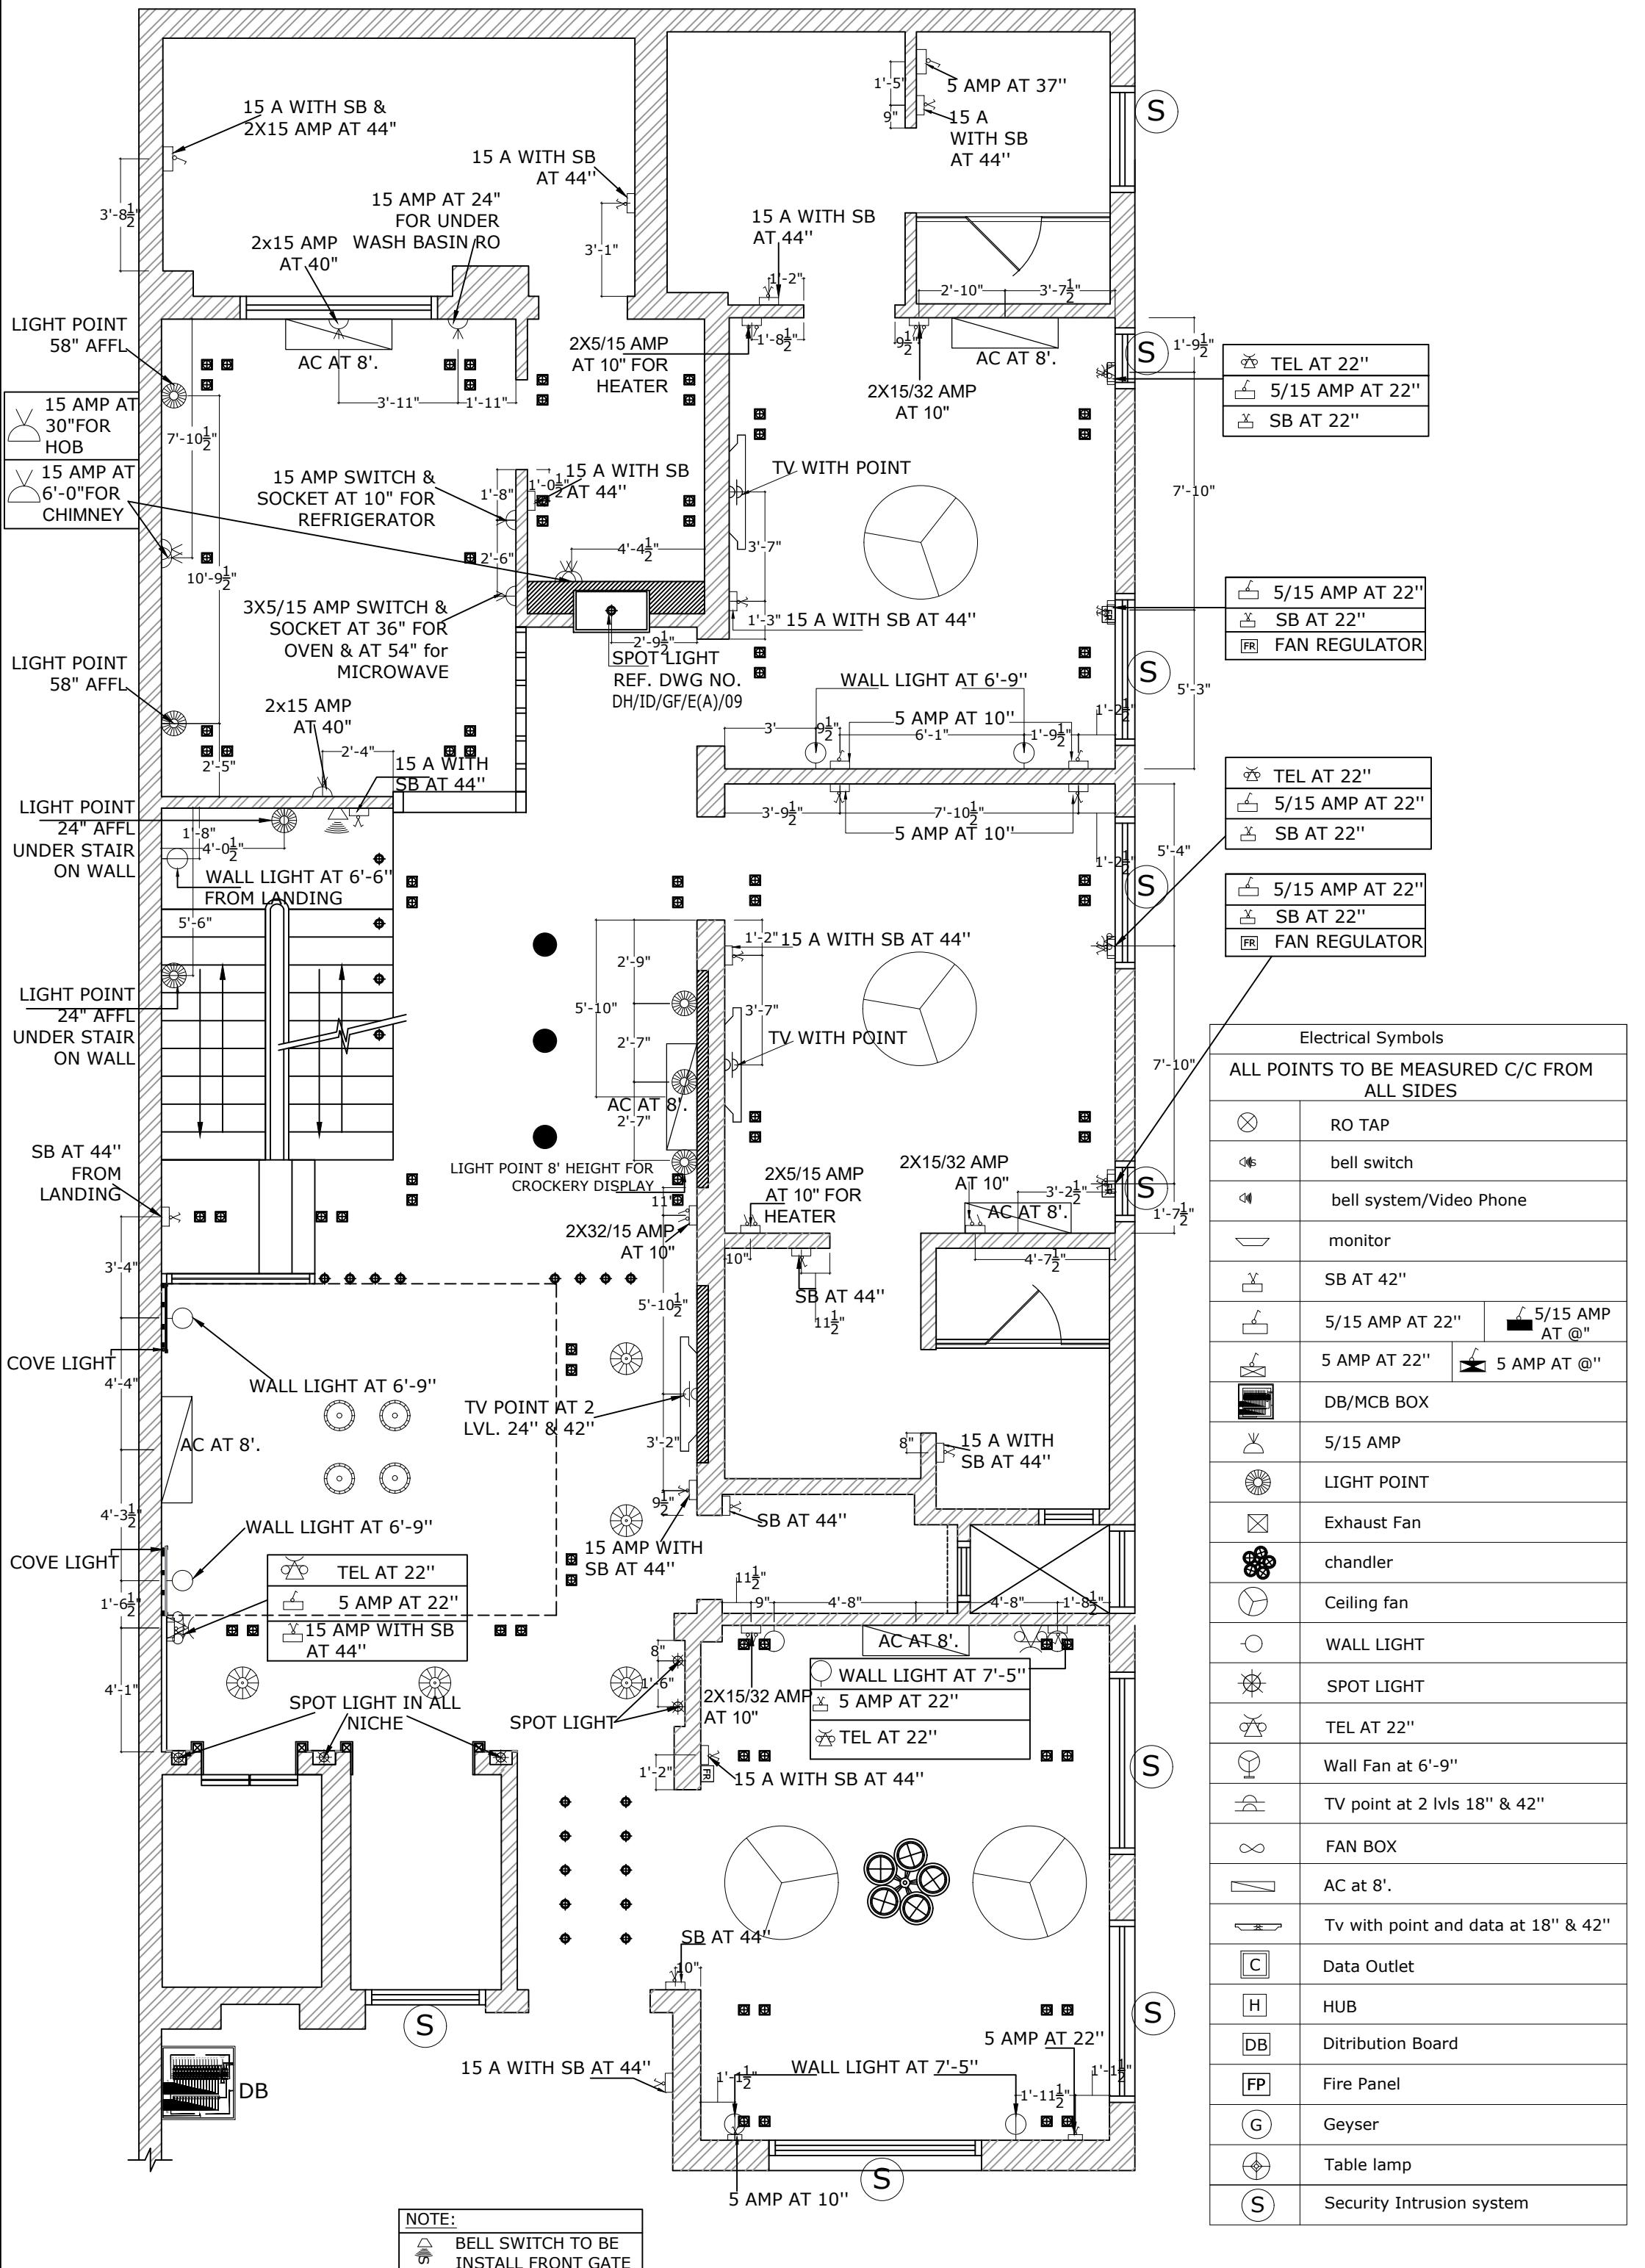


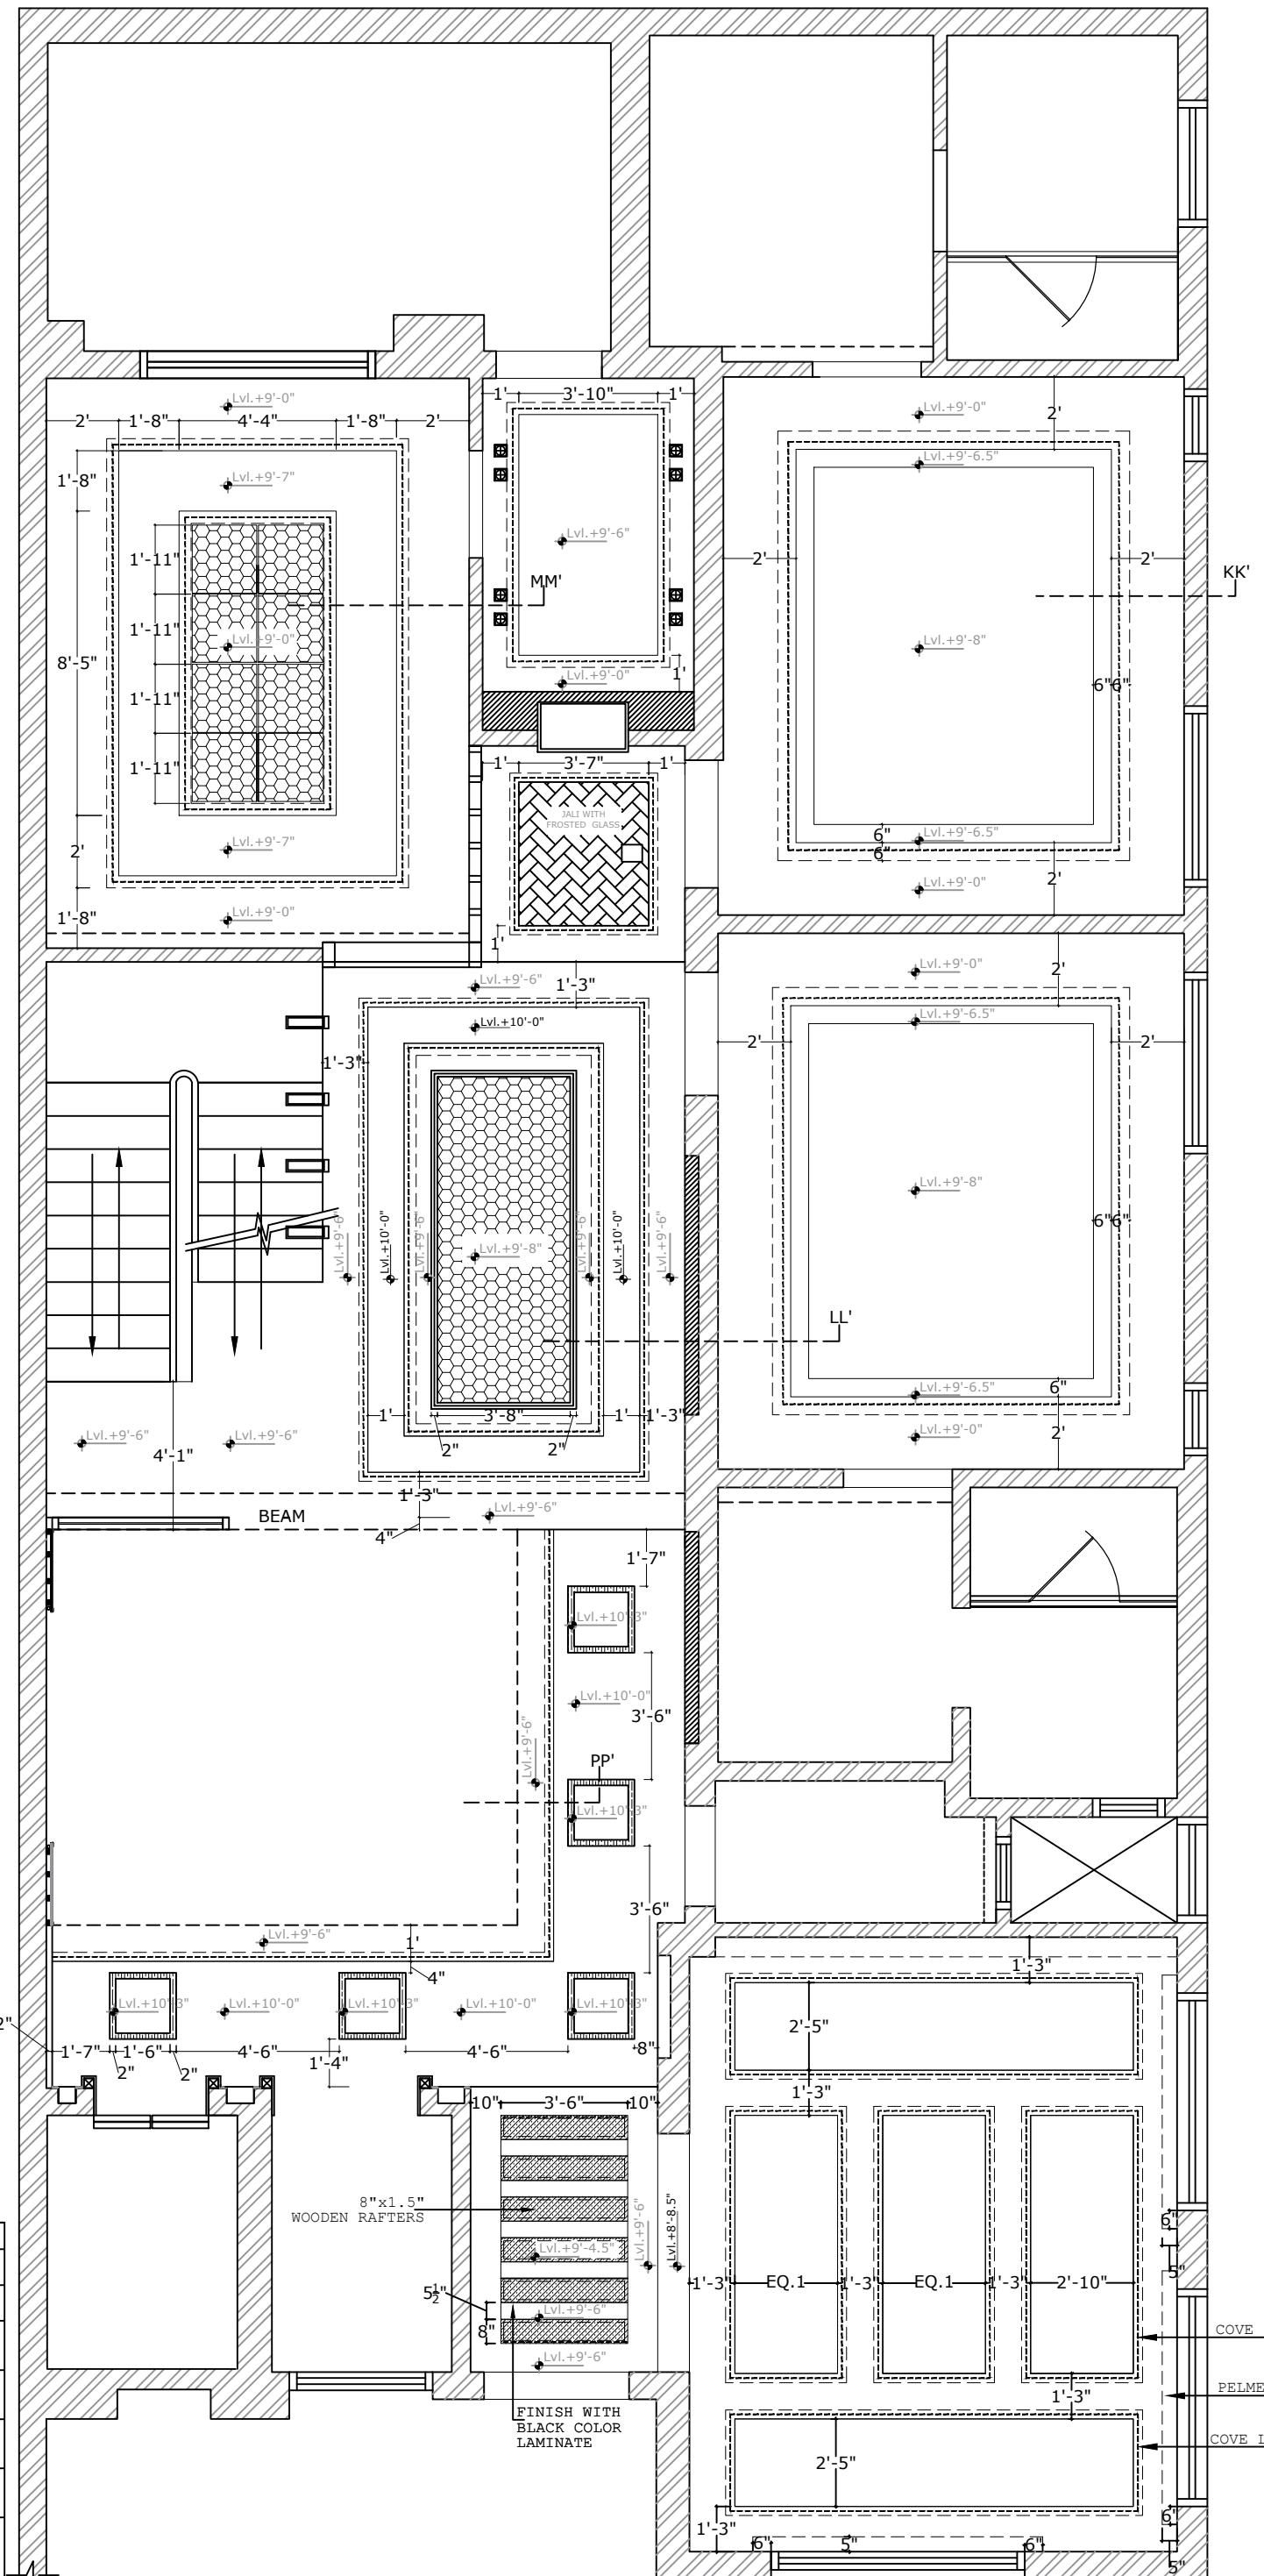


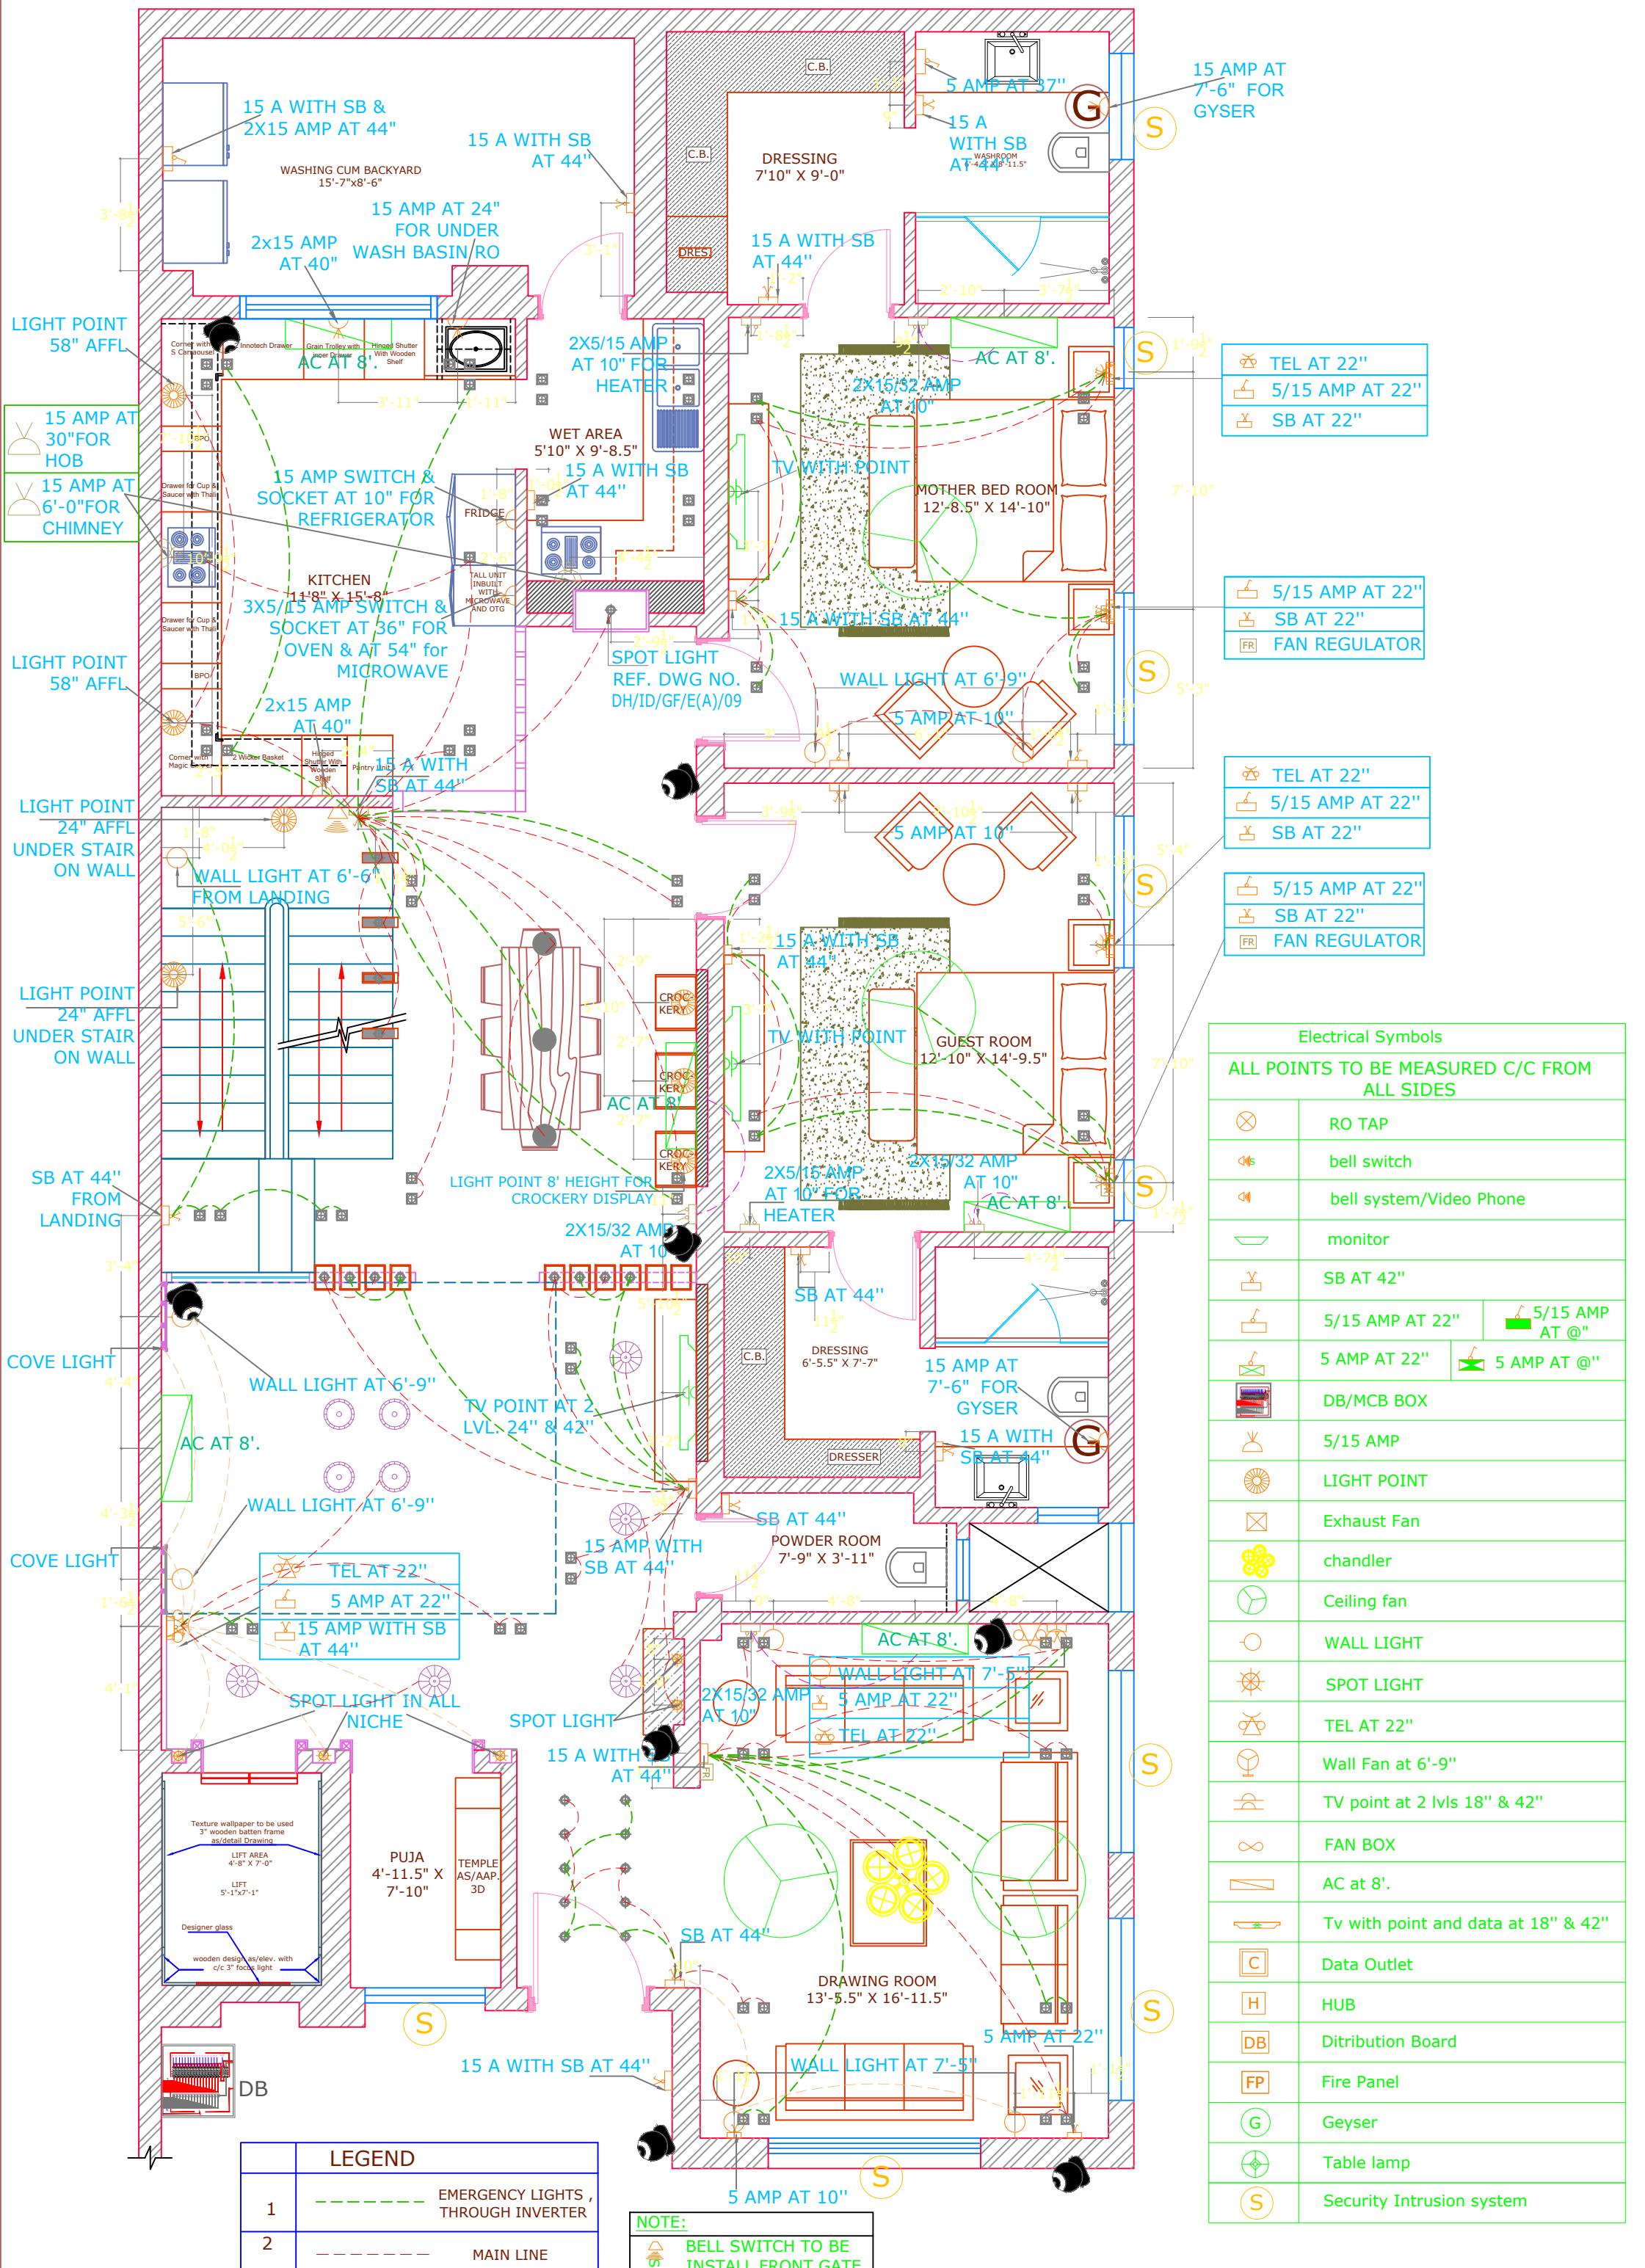


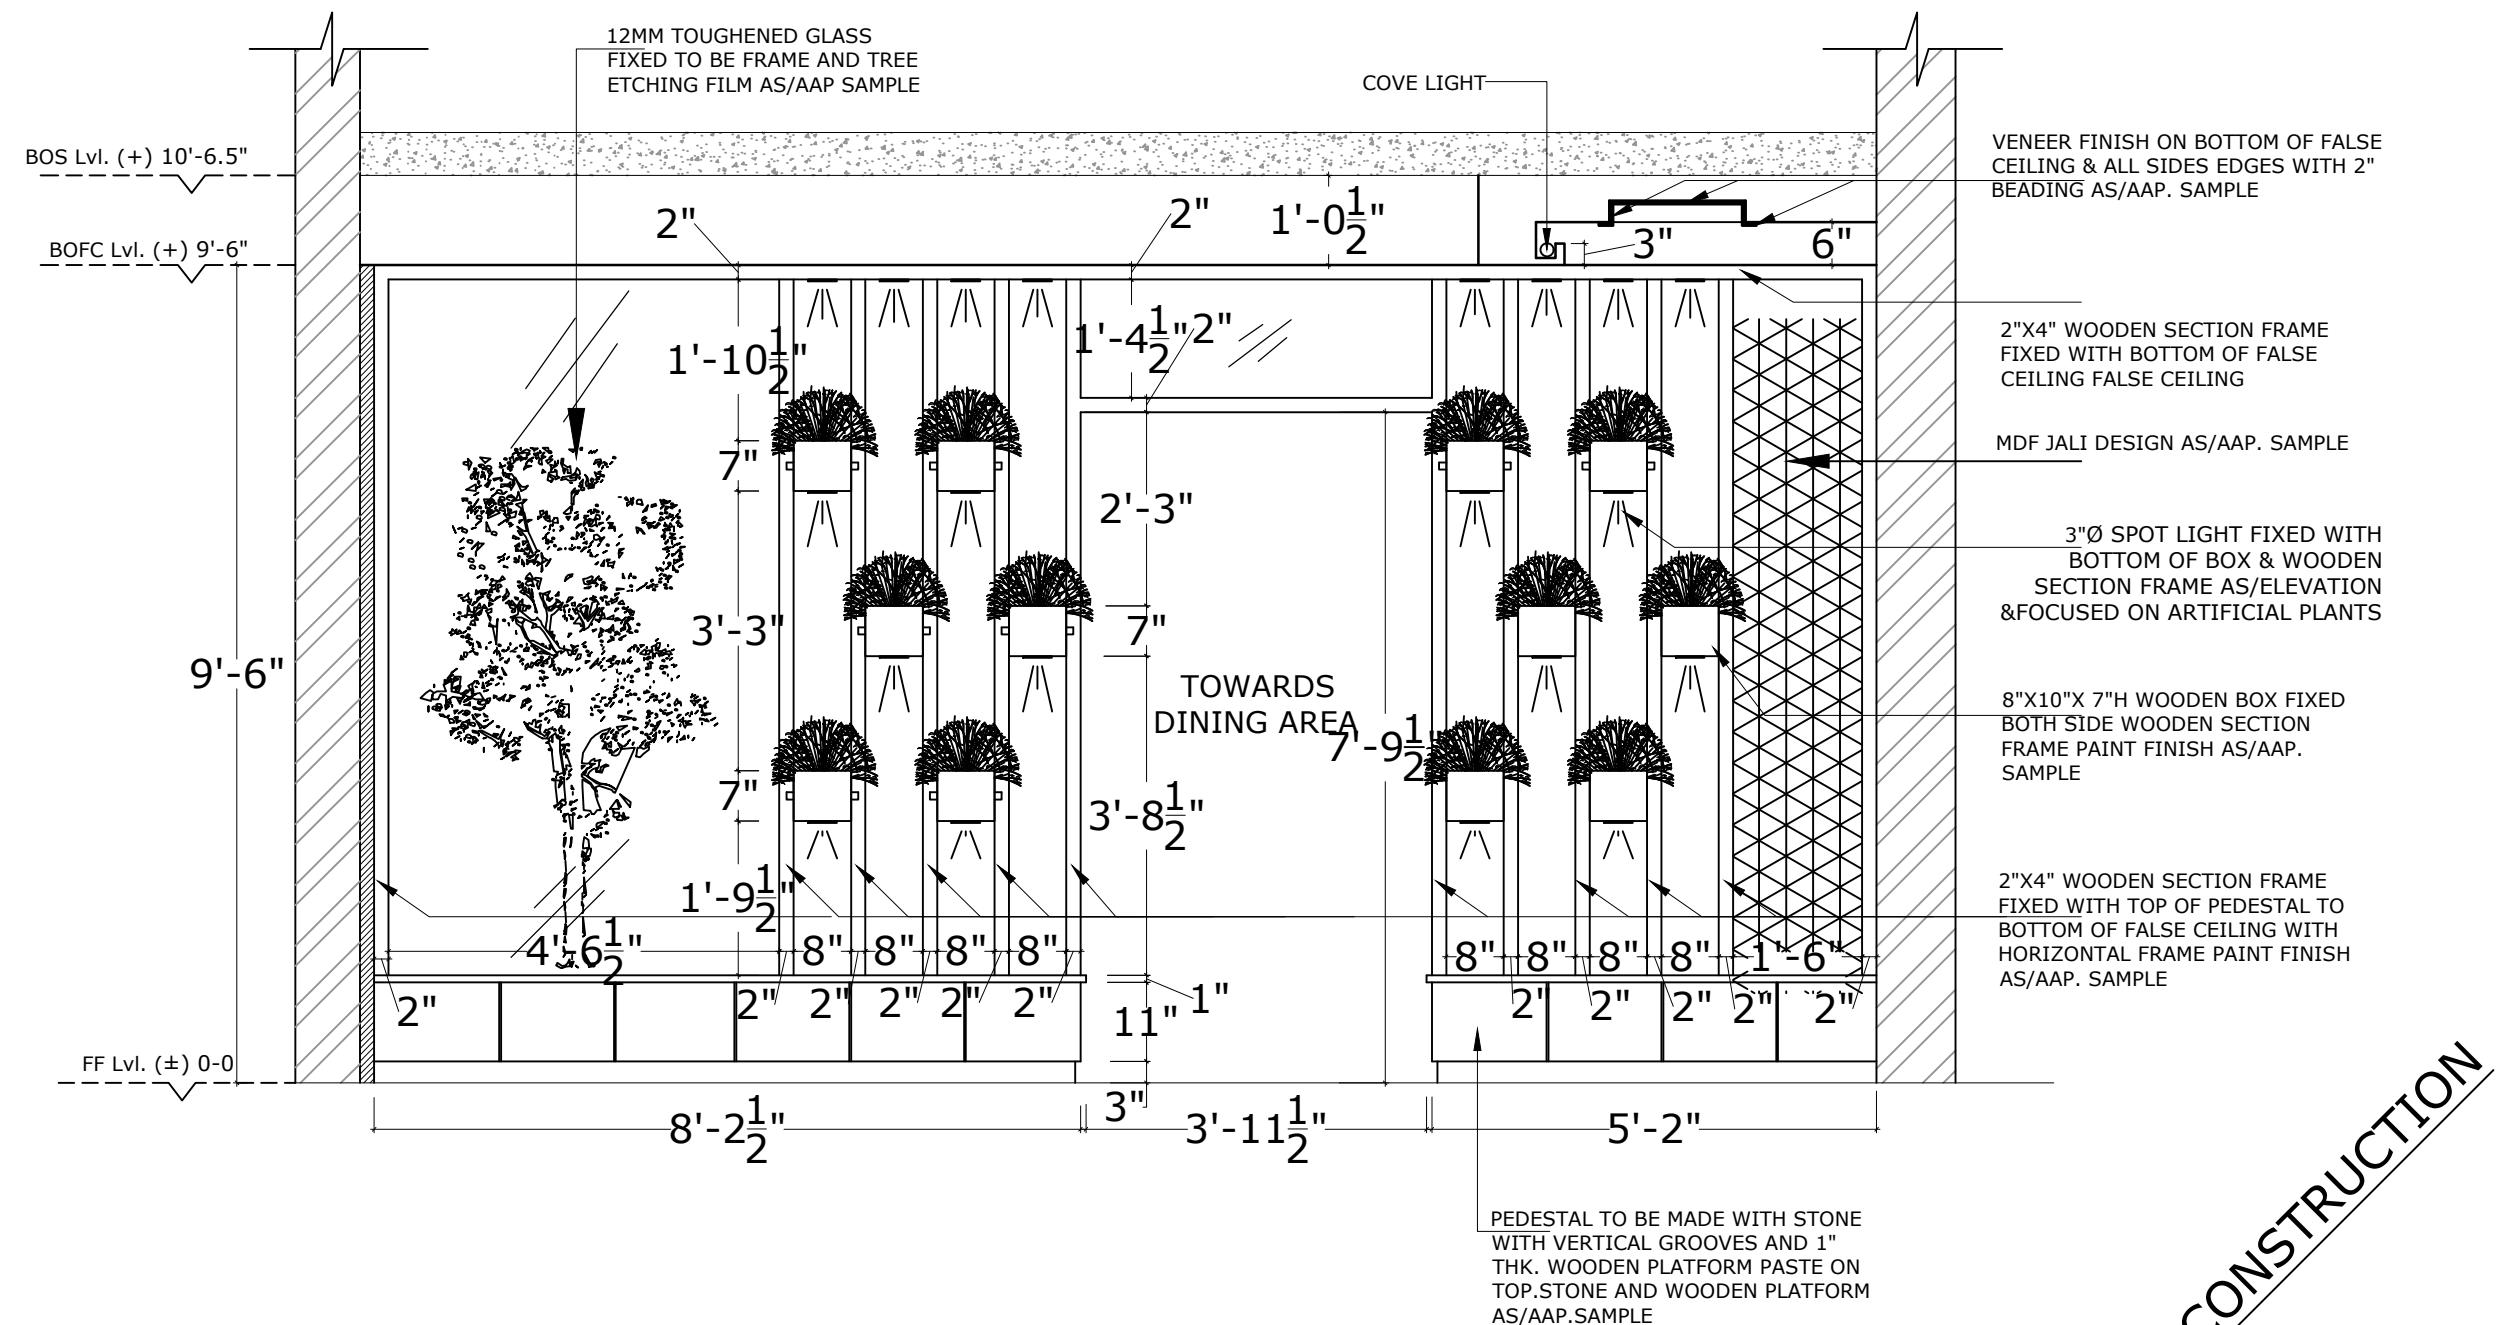



GOOD FOR CONSTRUCTION


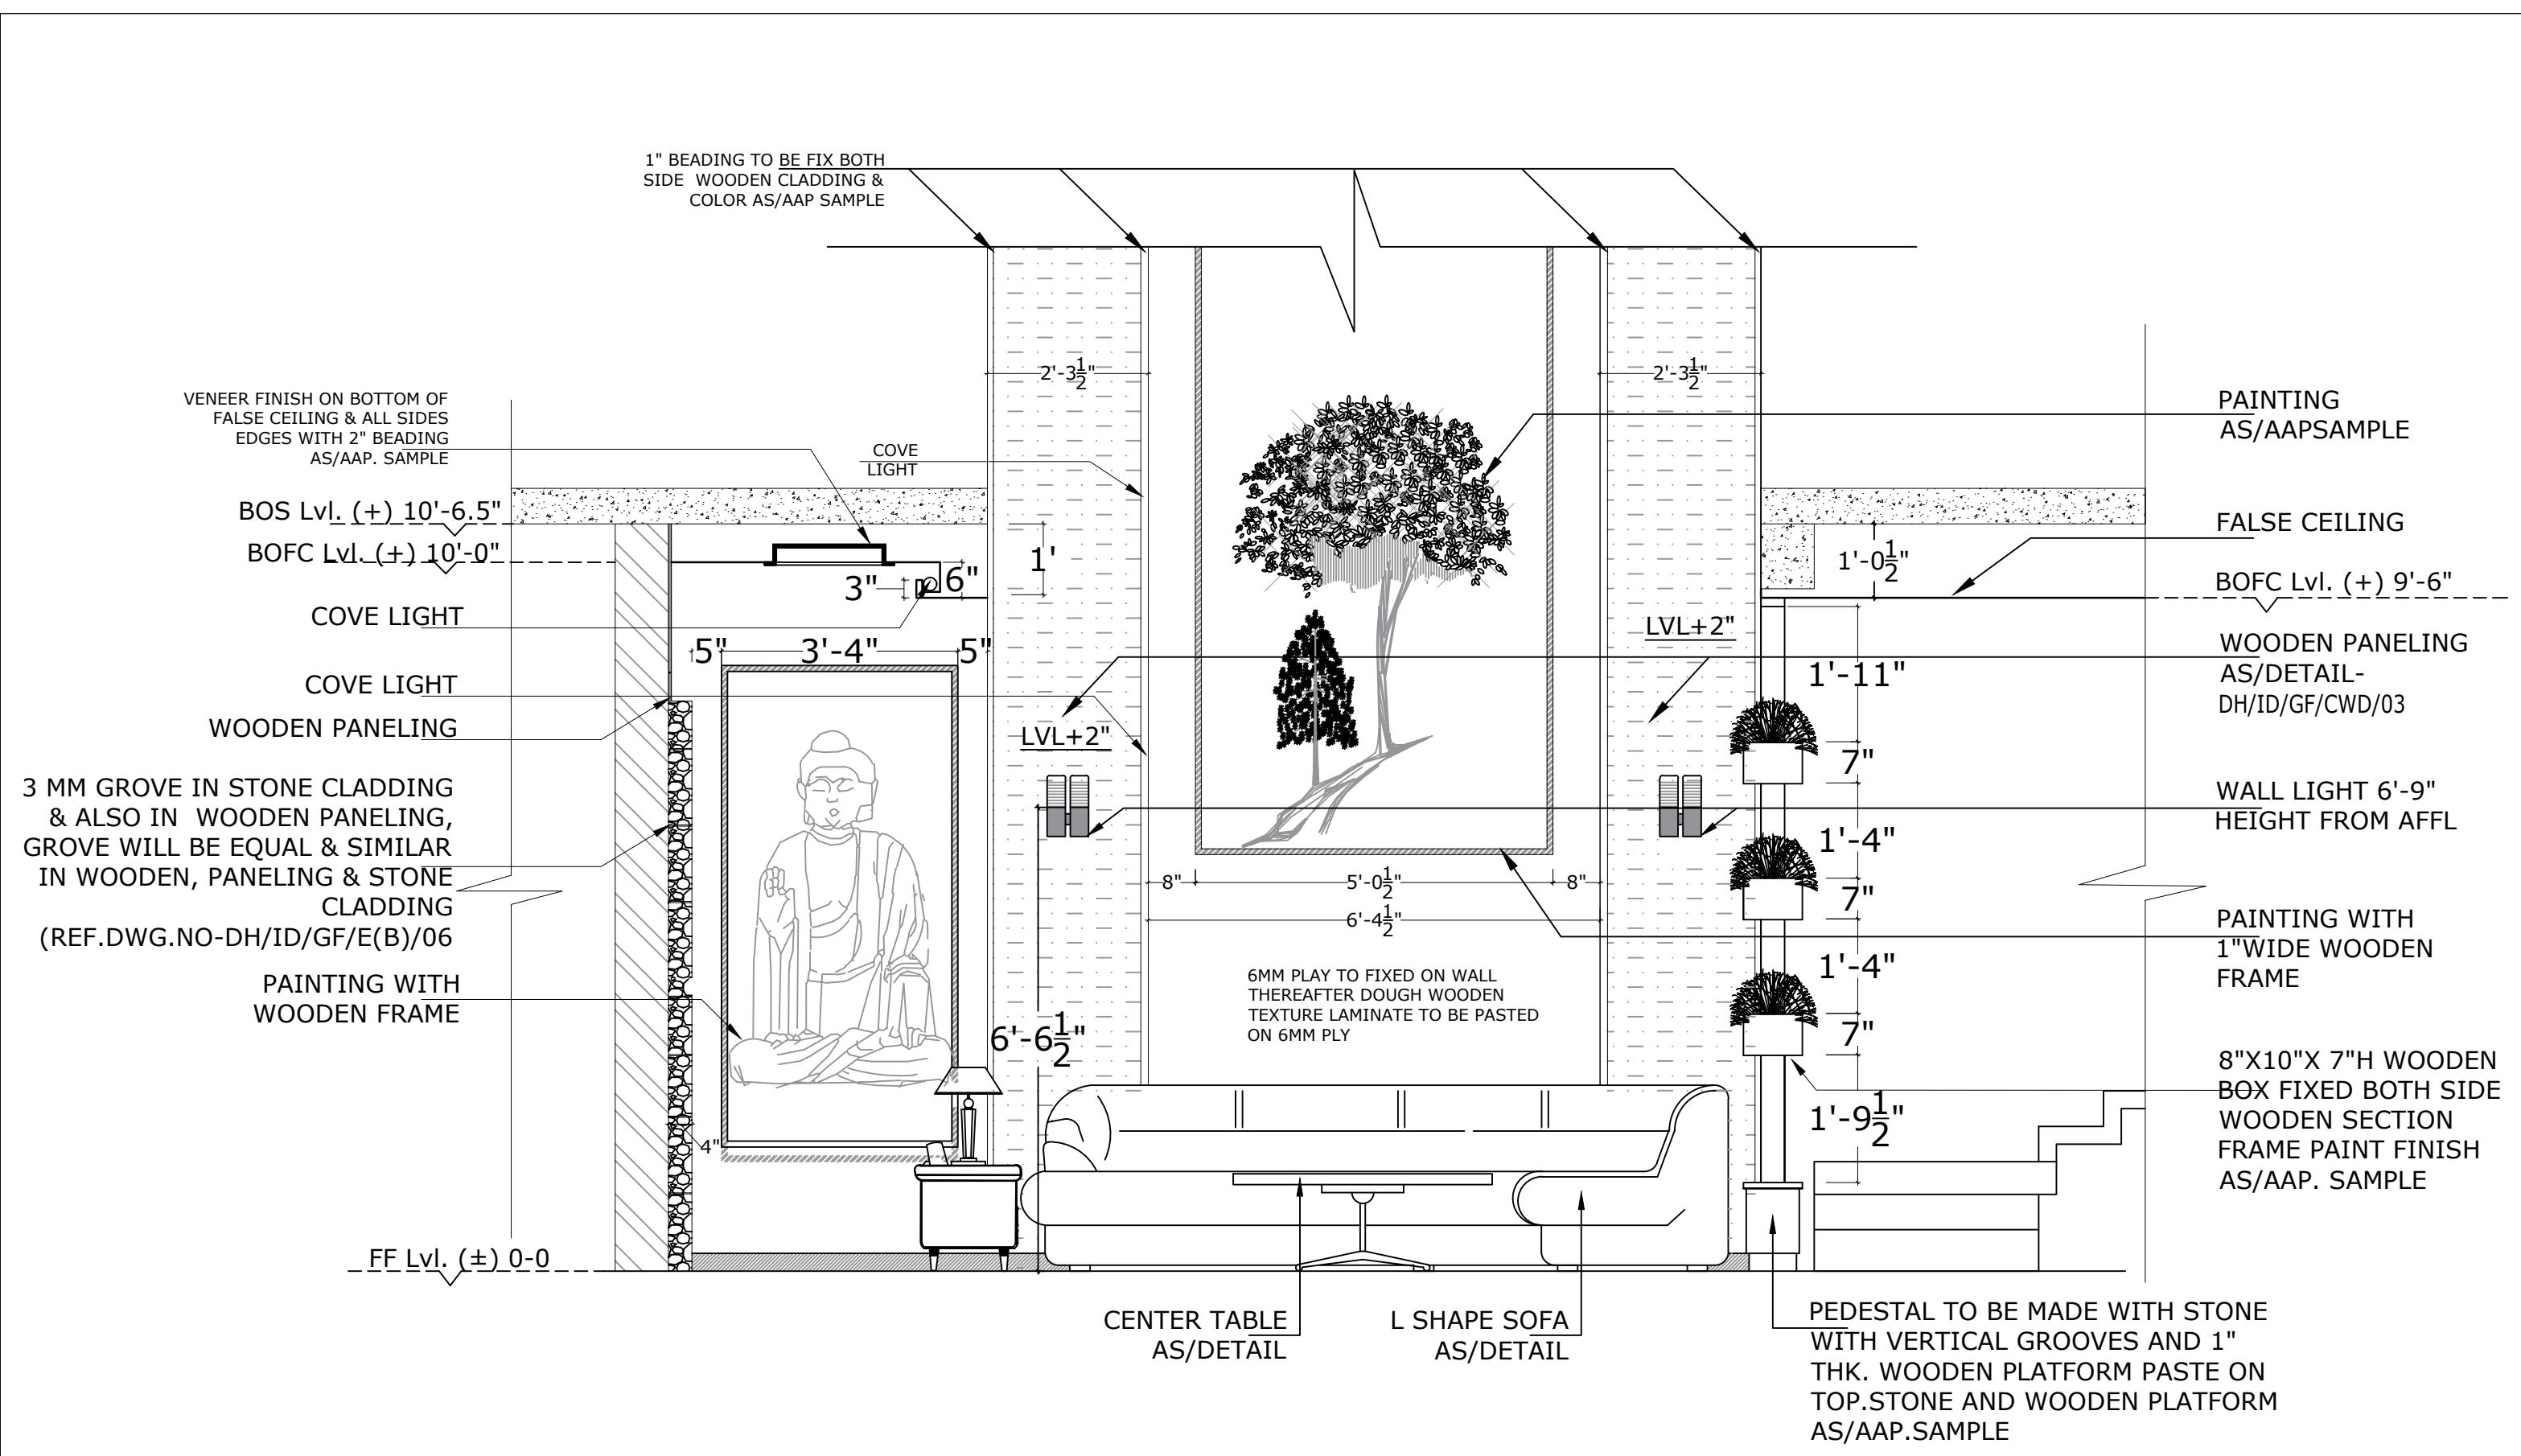


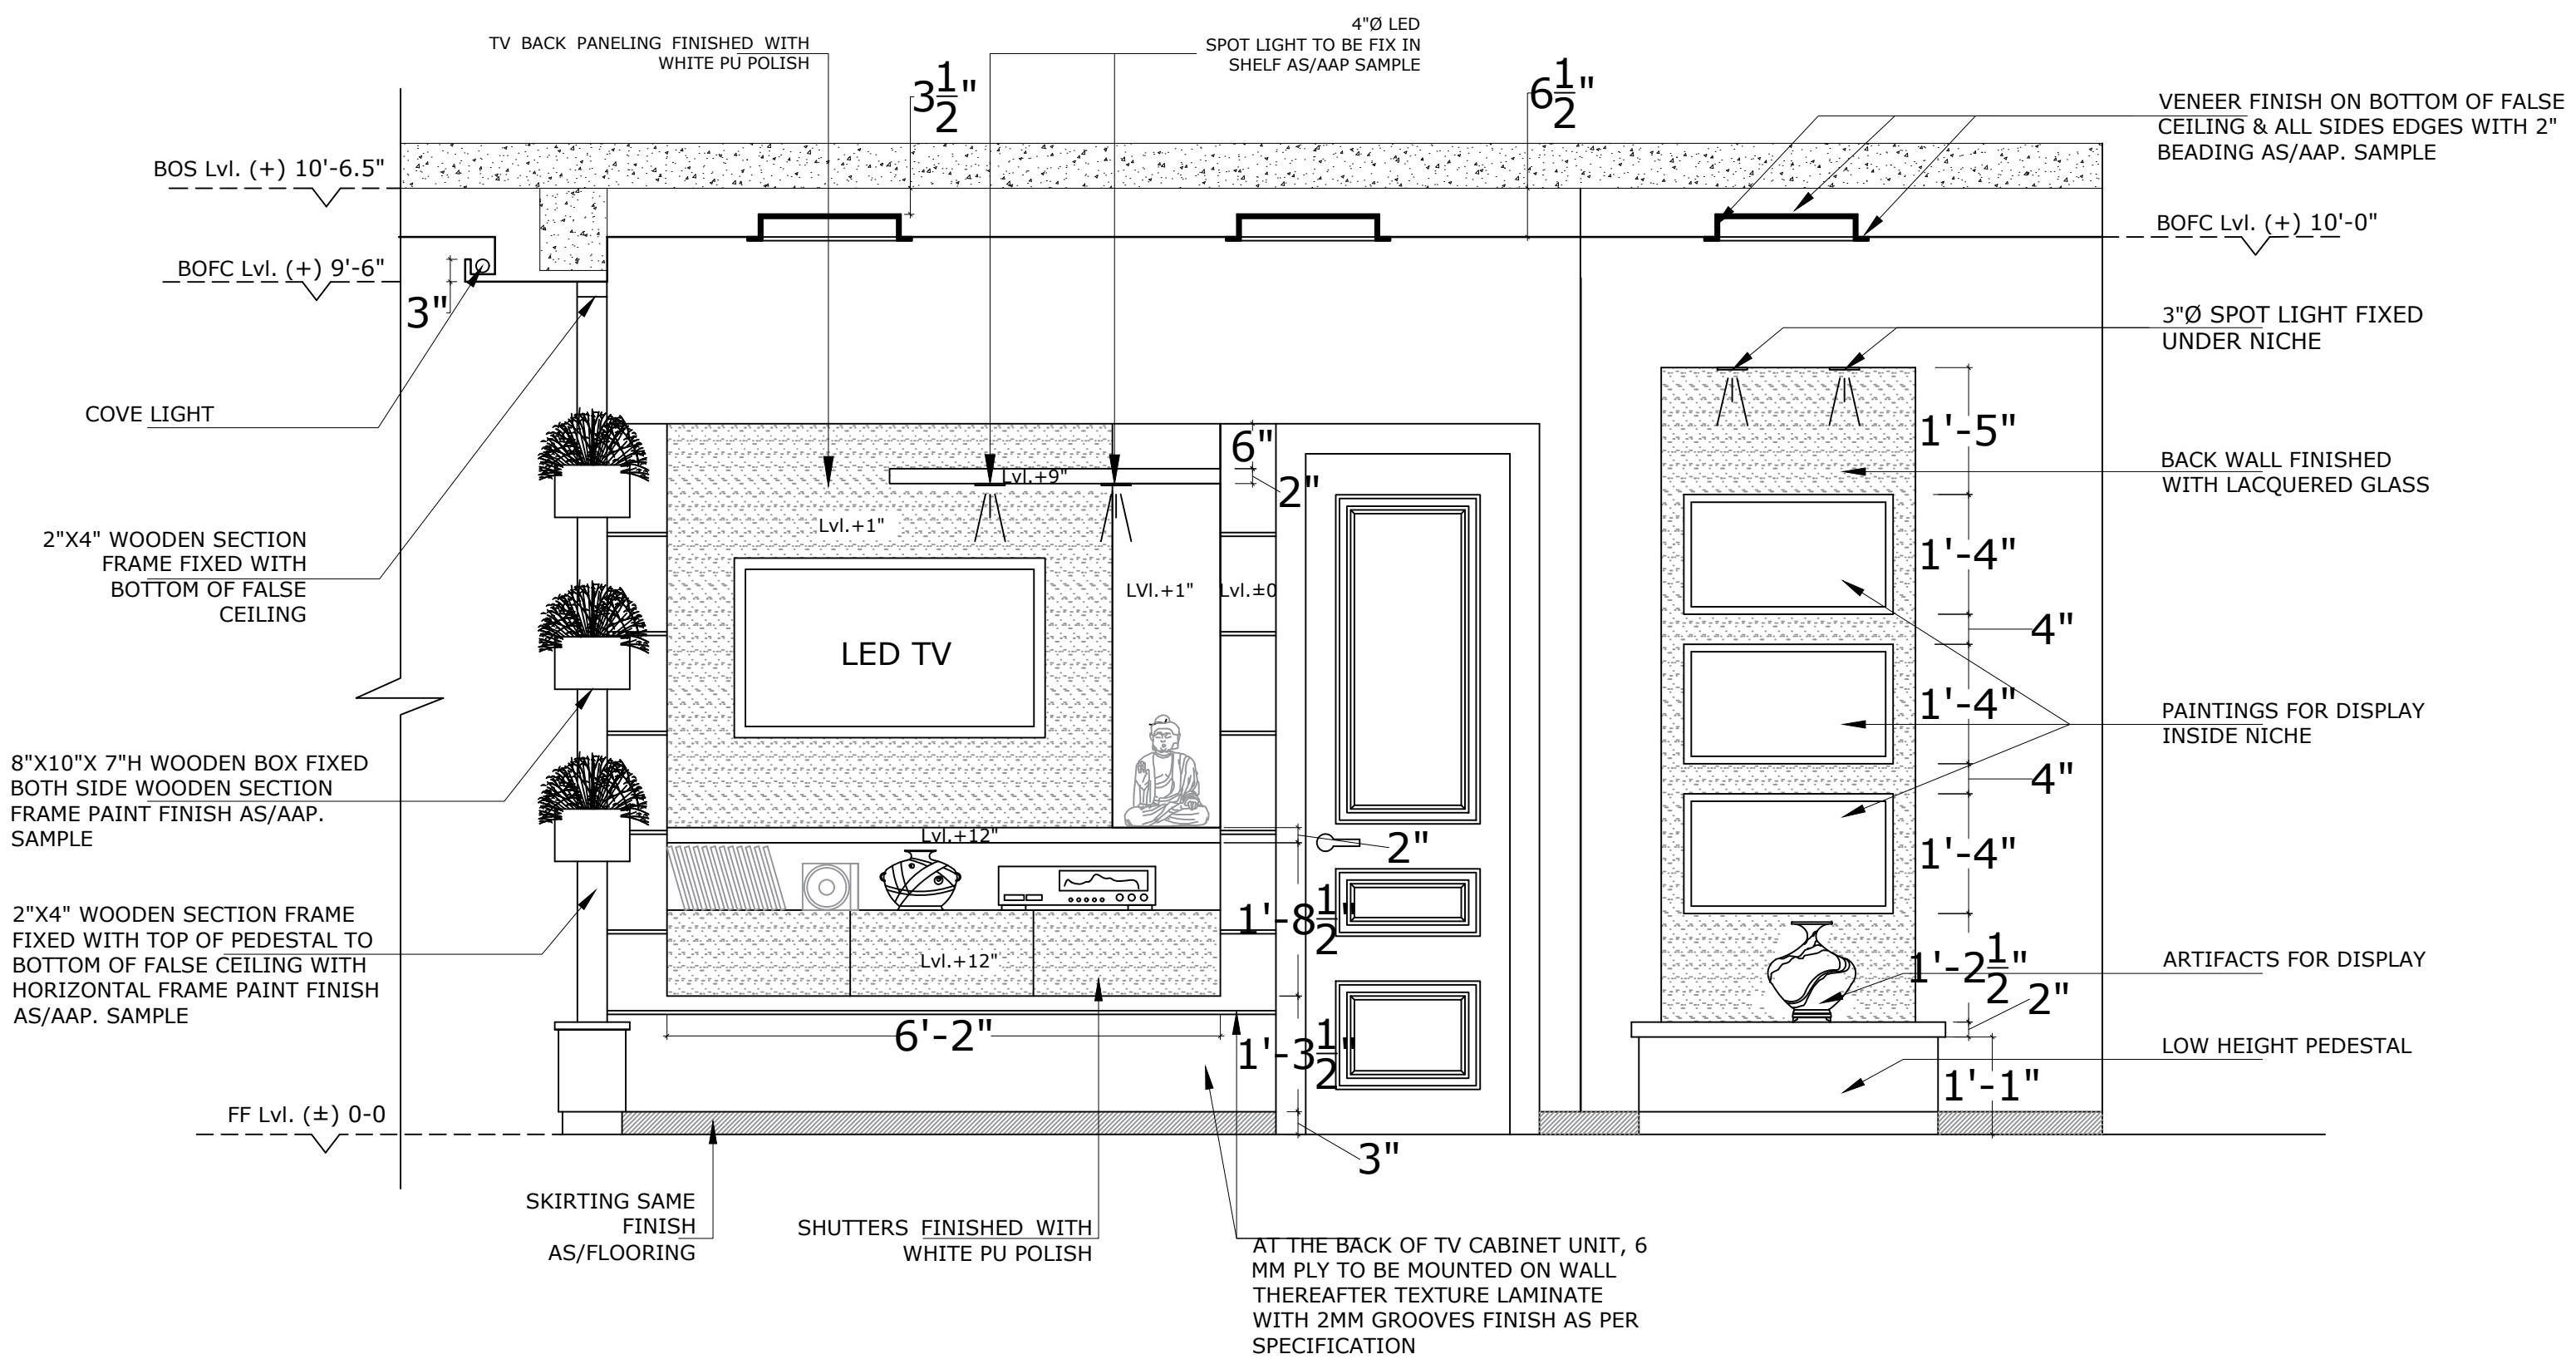

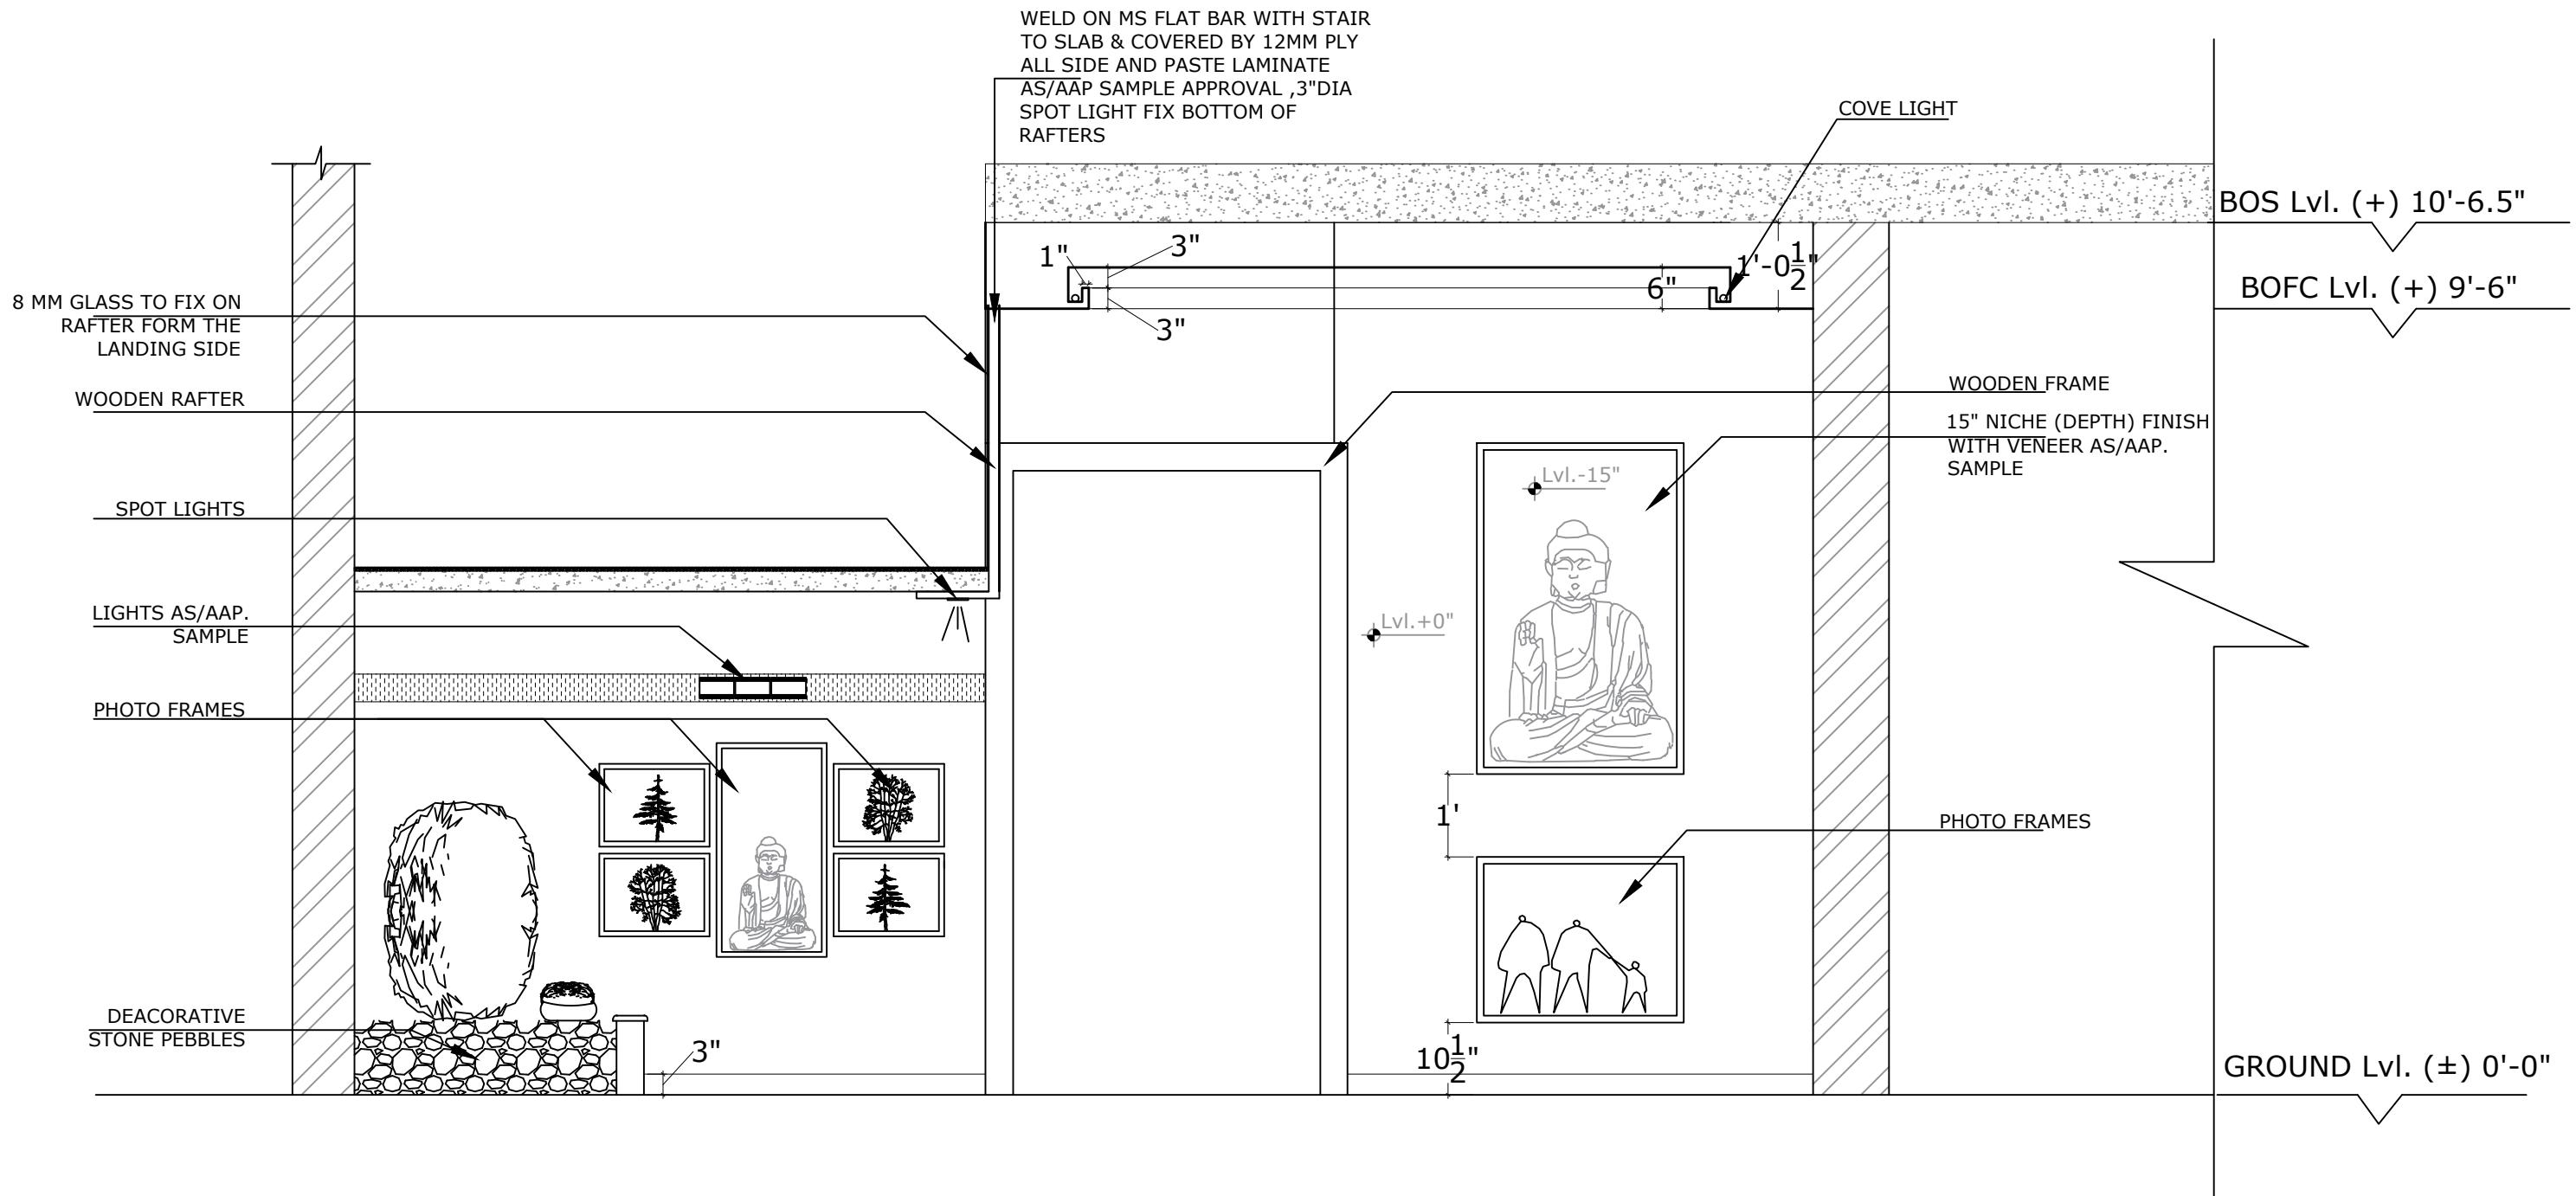


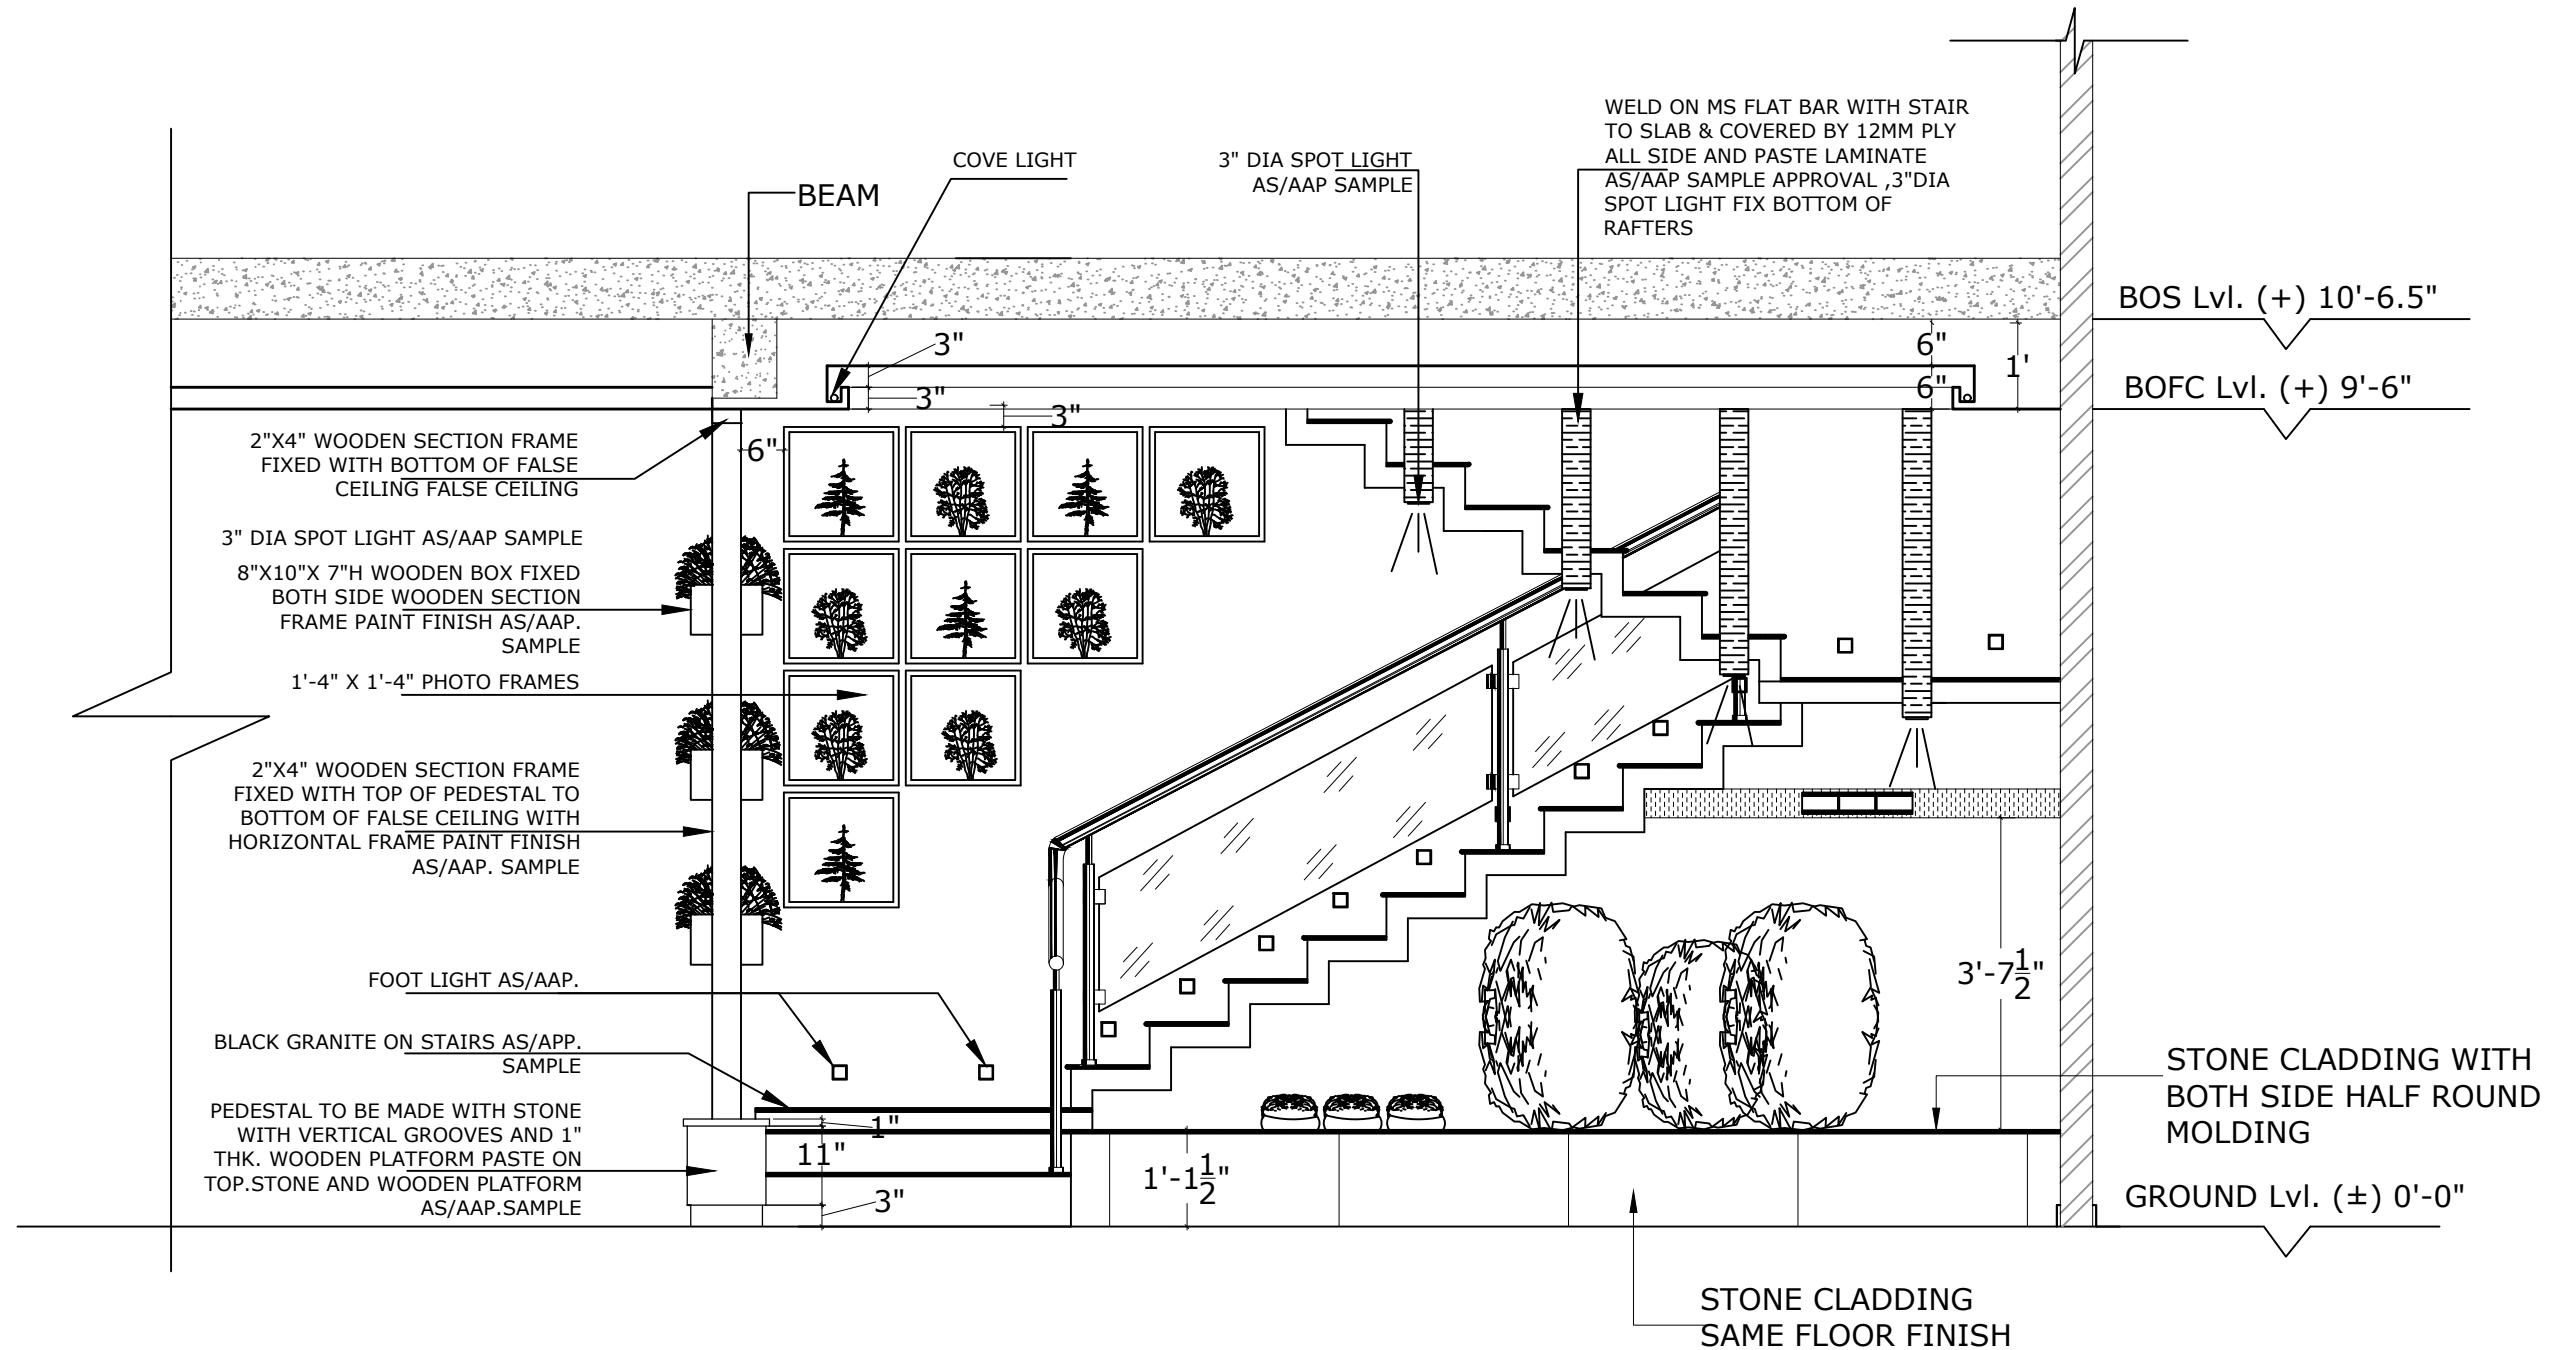

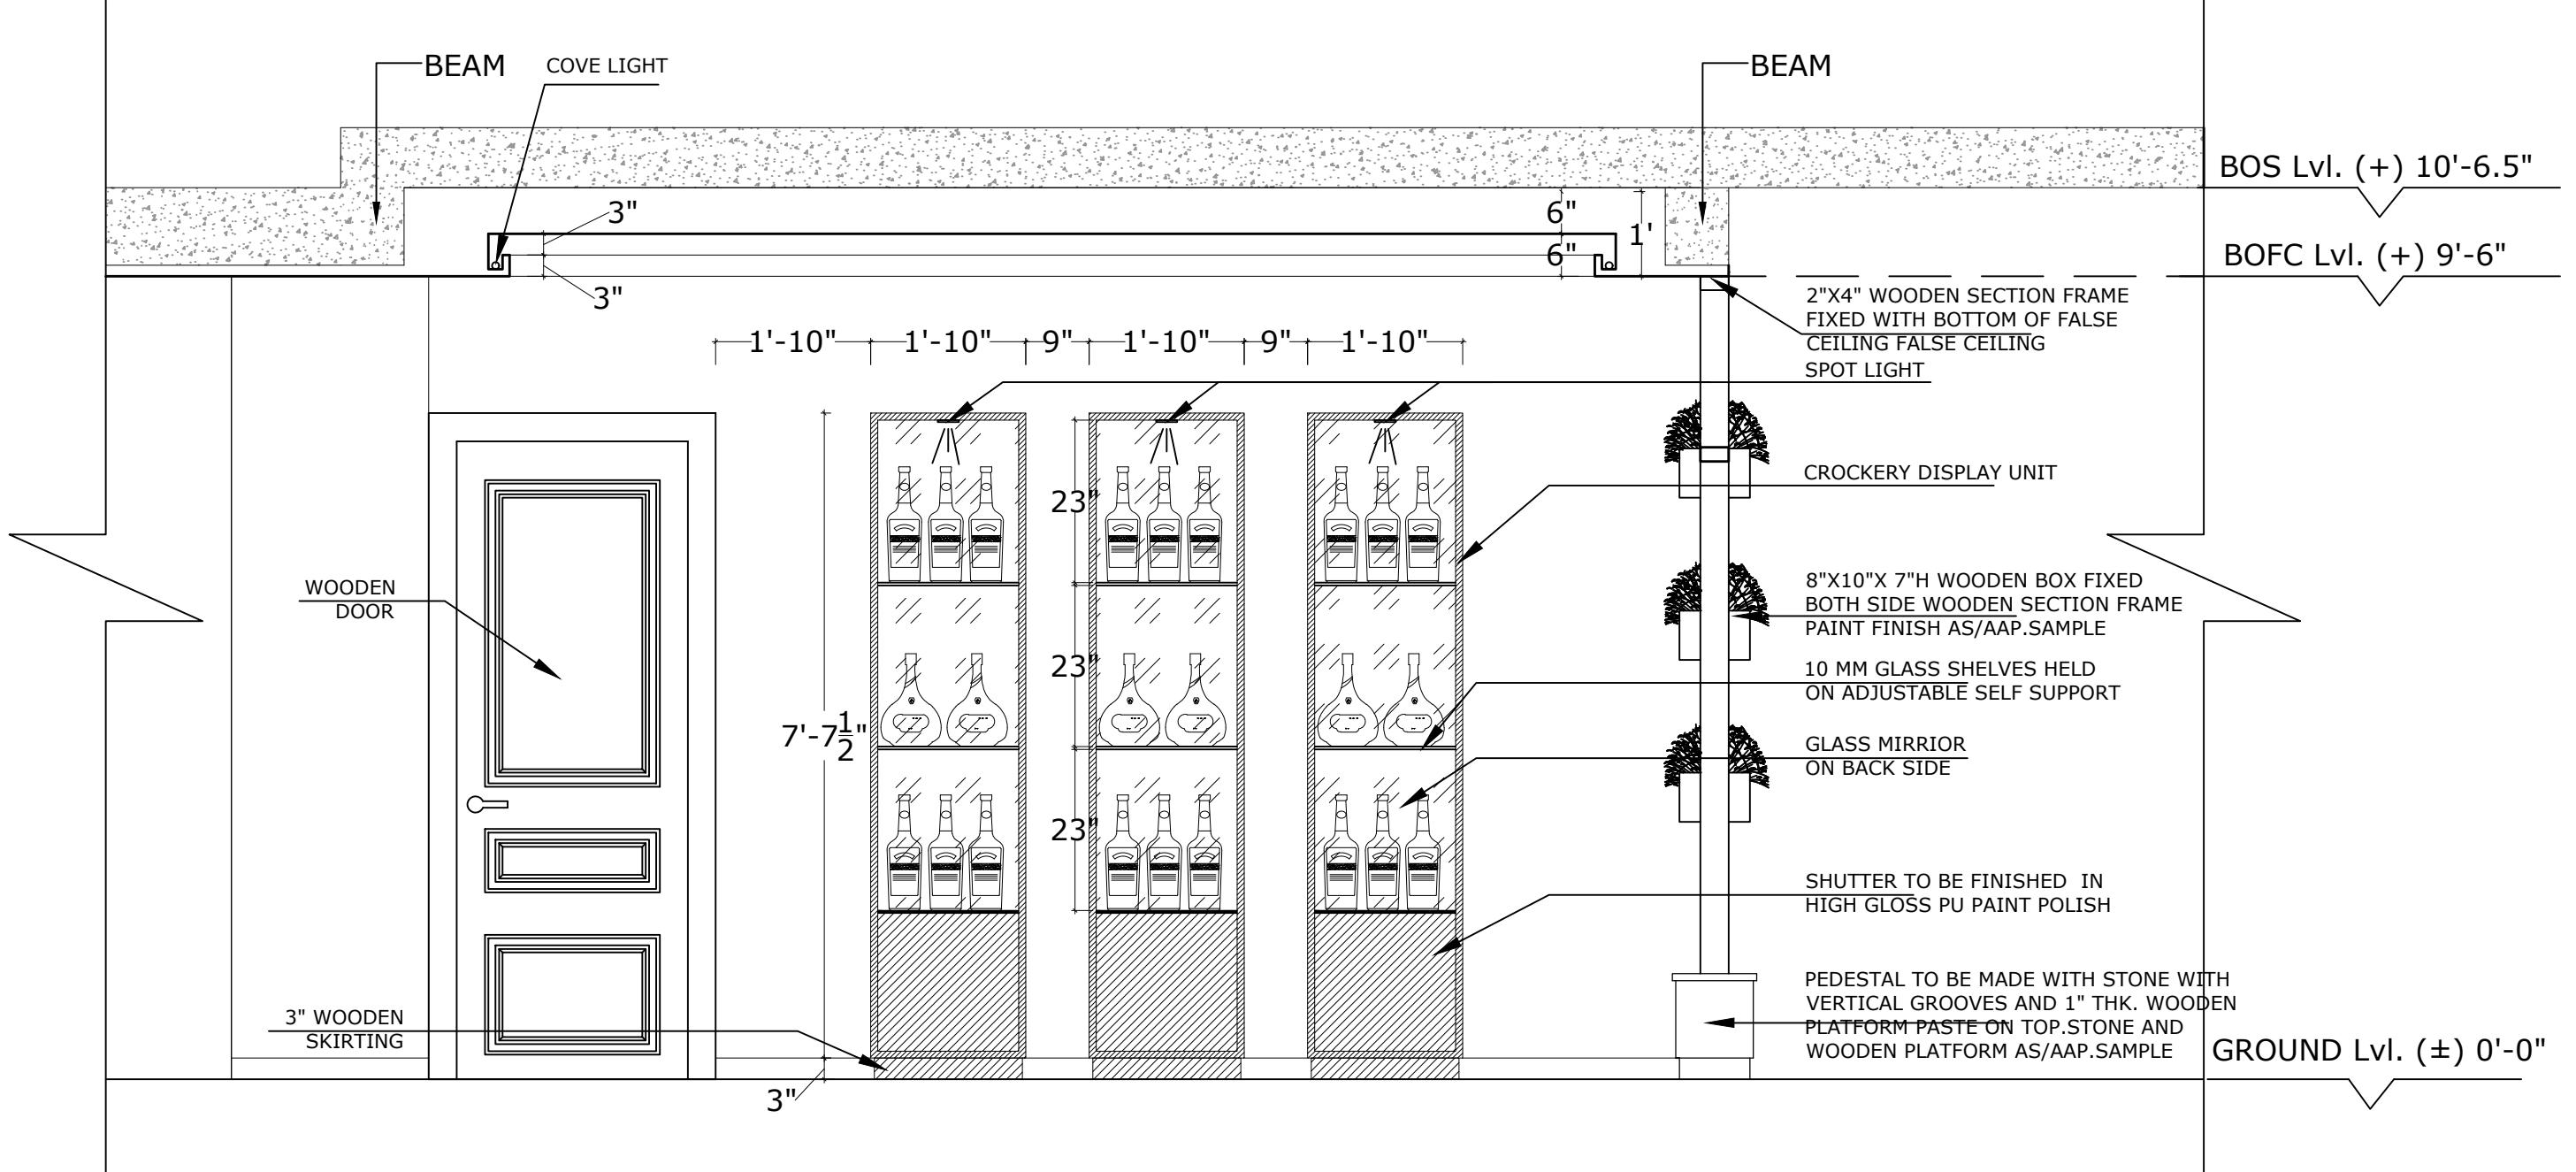

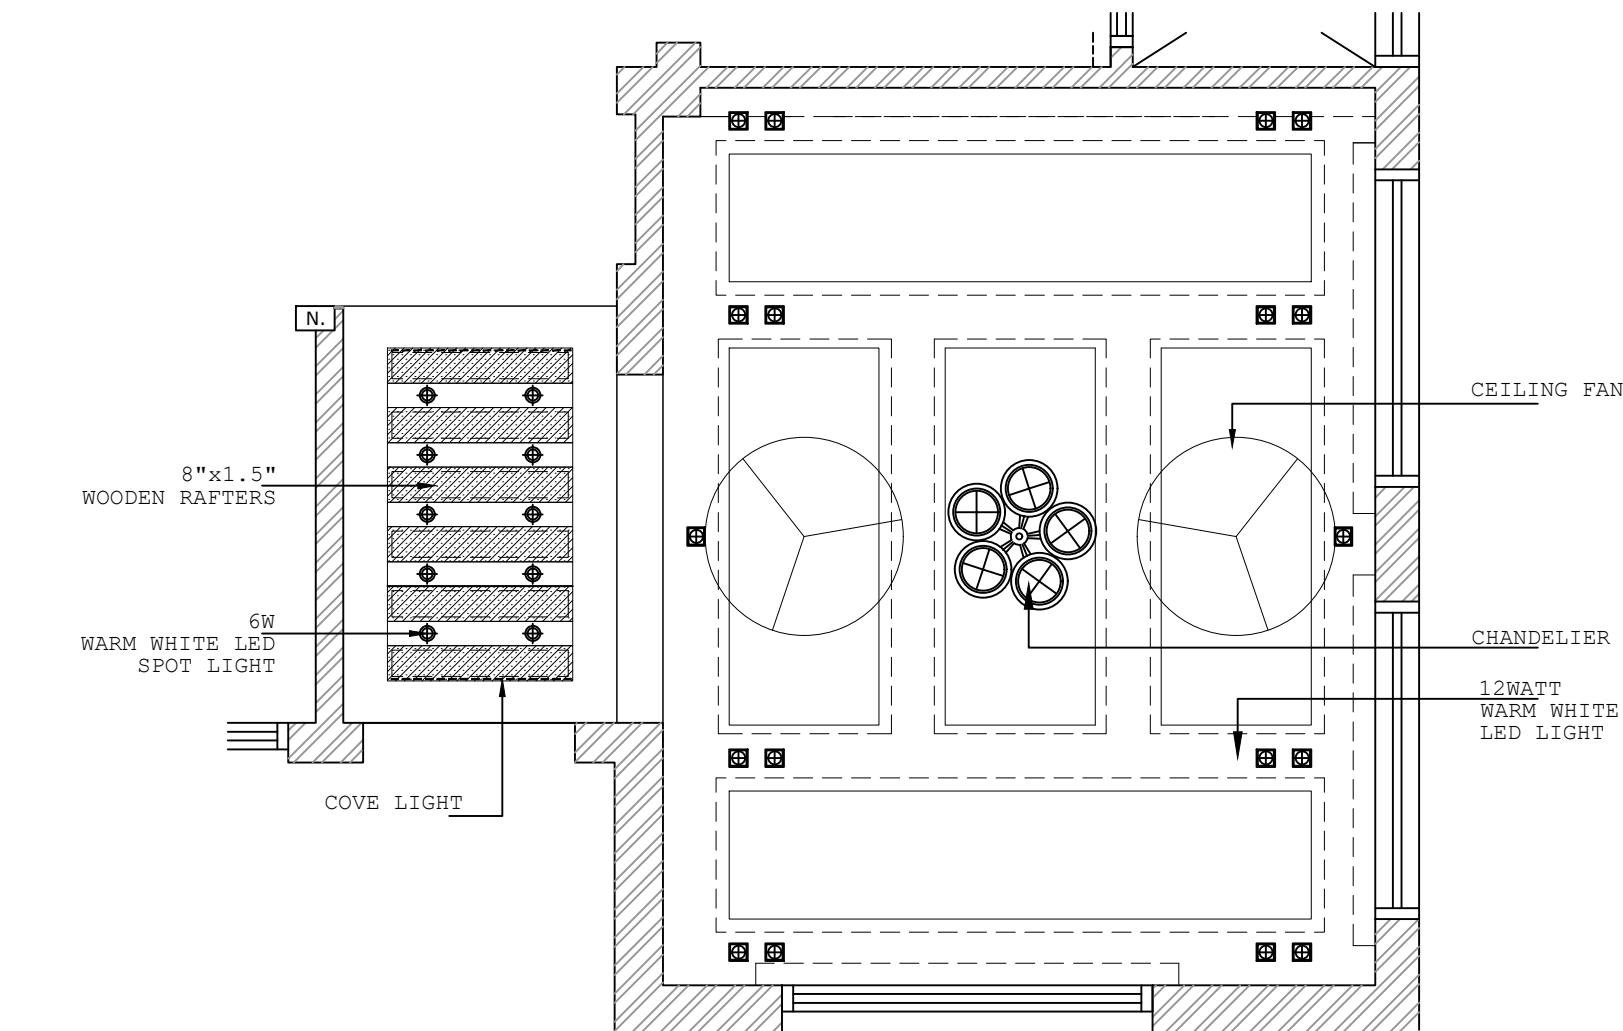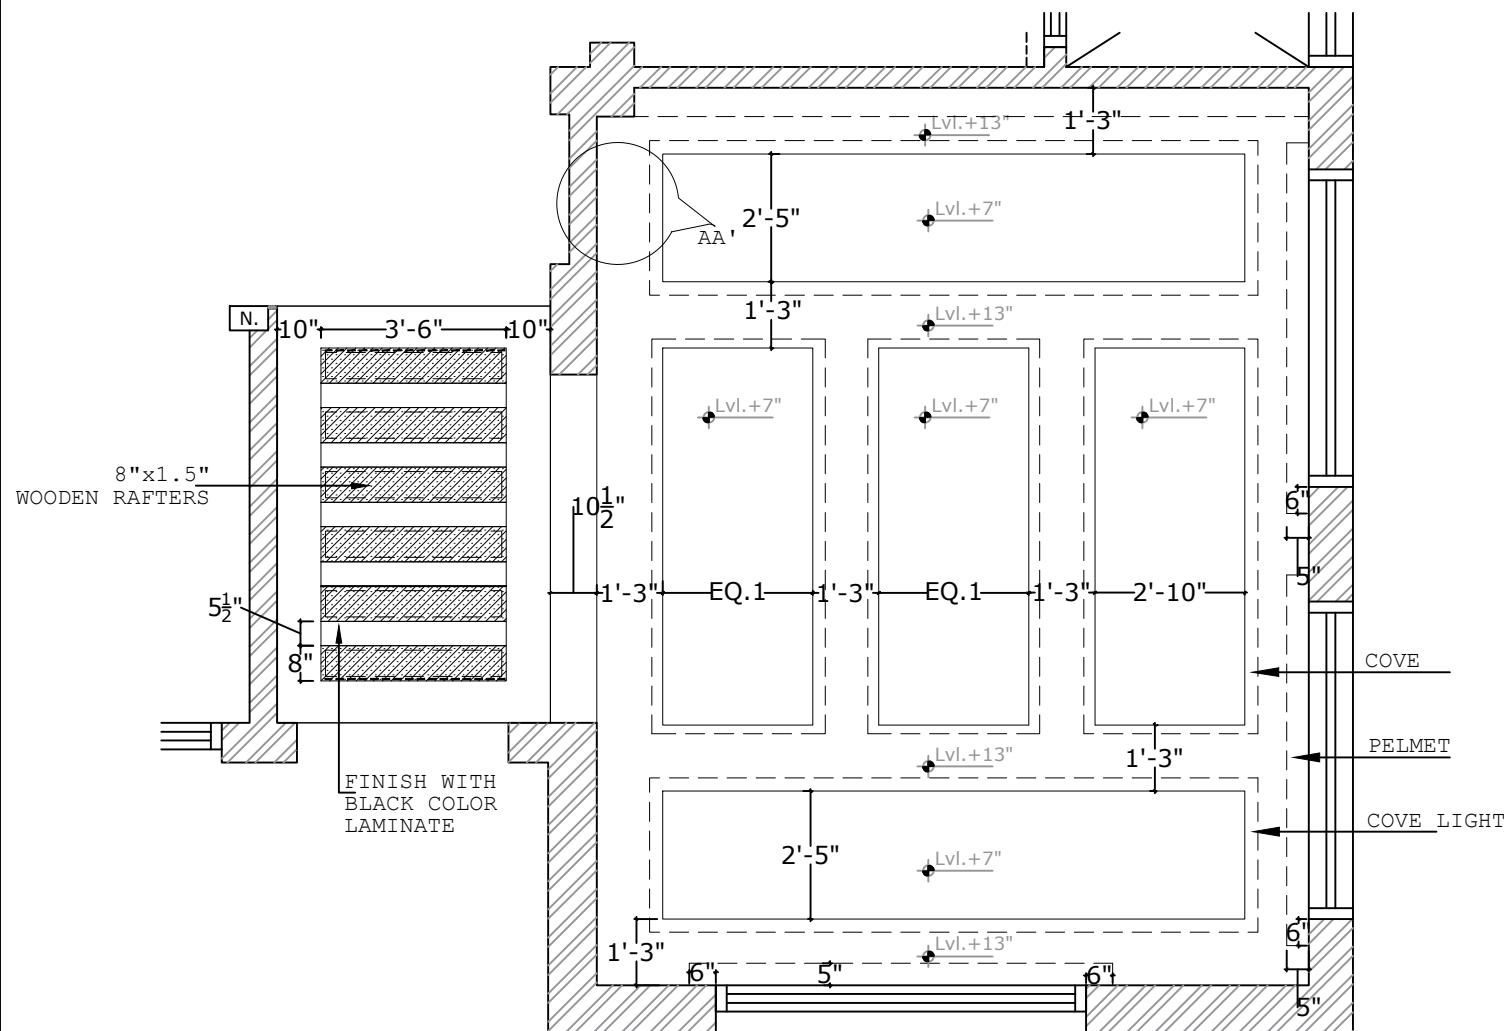


GOOD FOR CONSTRUCTION

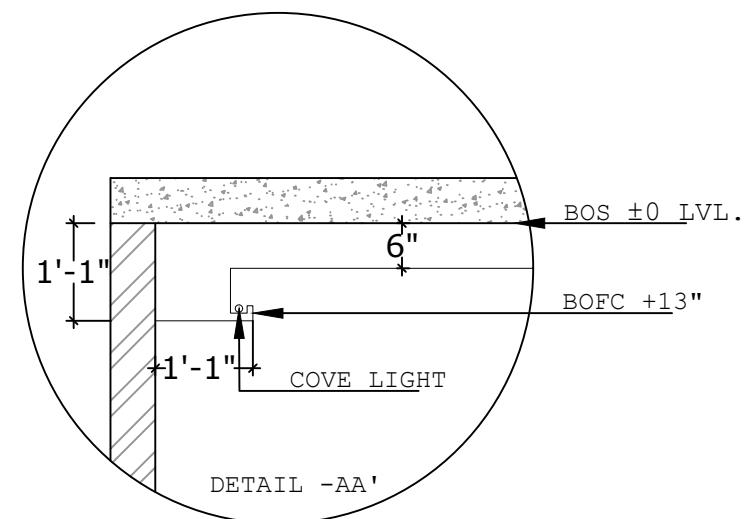




NOTE:
EOS=BOTTOM OF SLAB
BOFC= BOTTOM OF FALSE
CEILING




FALSE CEILING DONE BY
PLASTER OF PARIS

outer side 1'-1" wide patta
will be 1" down bottom of
beam in entire area as/site
required


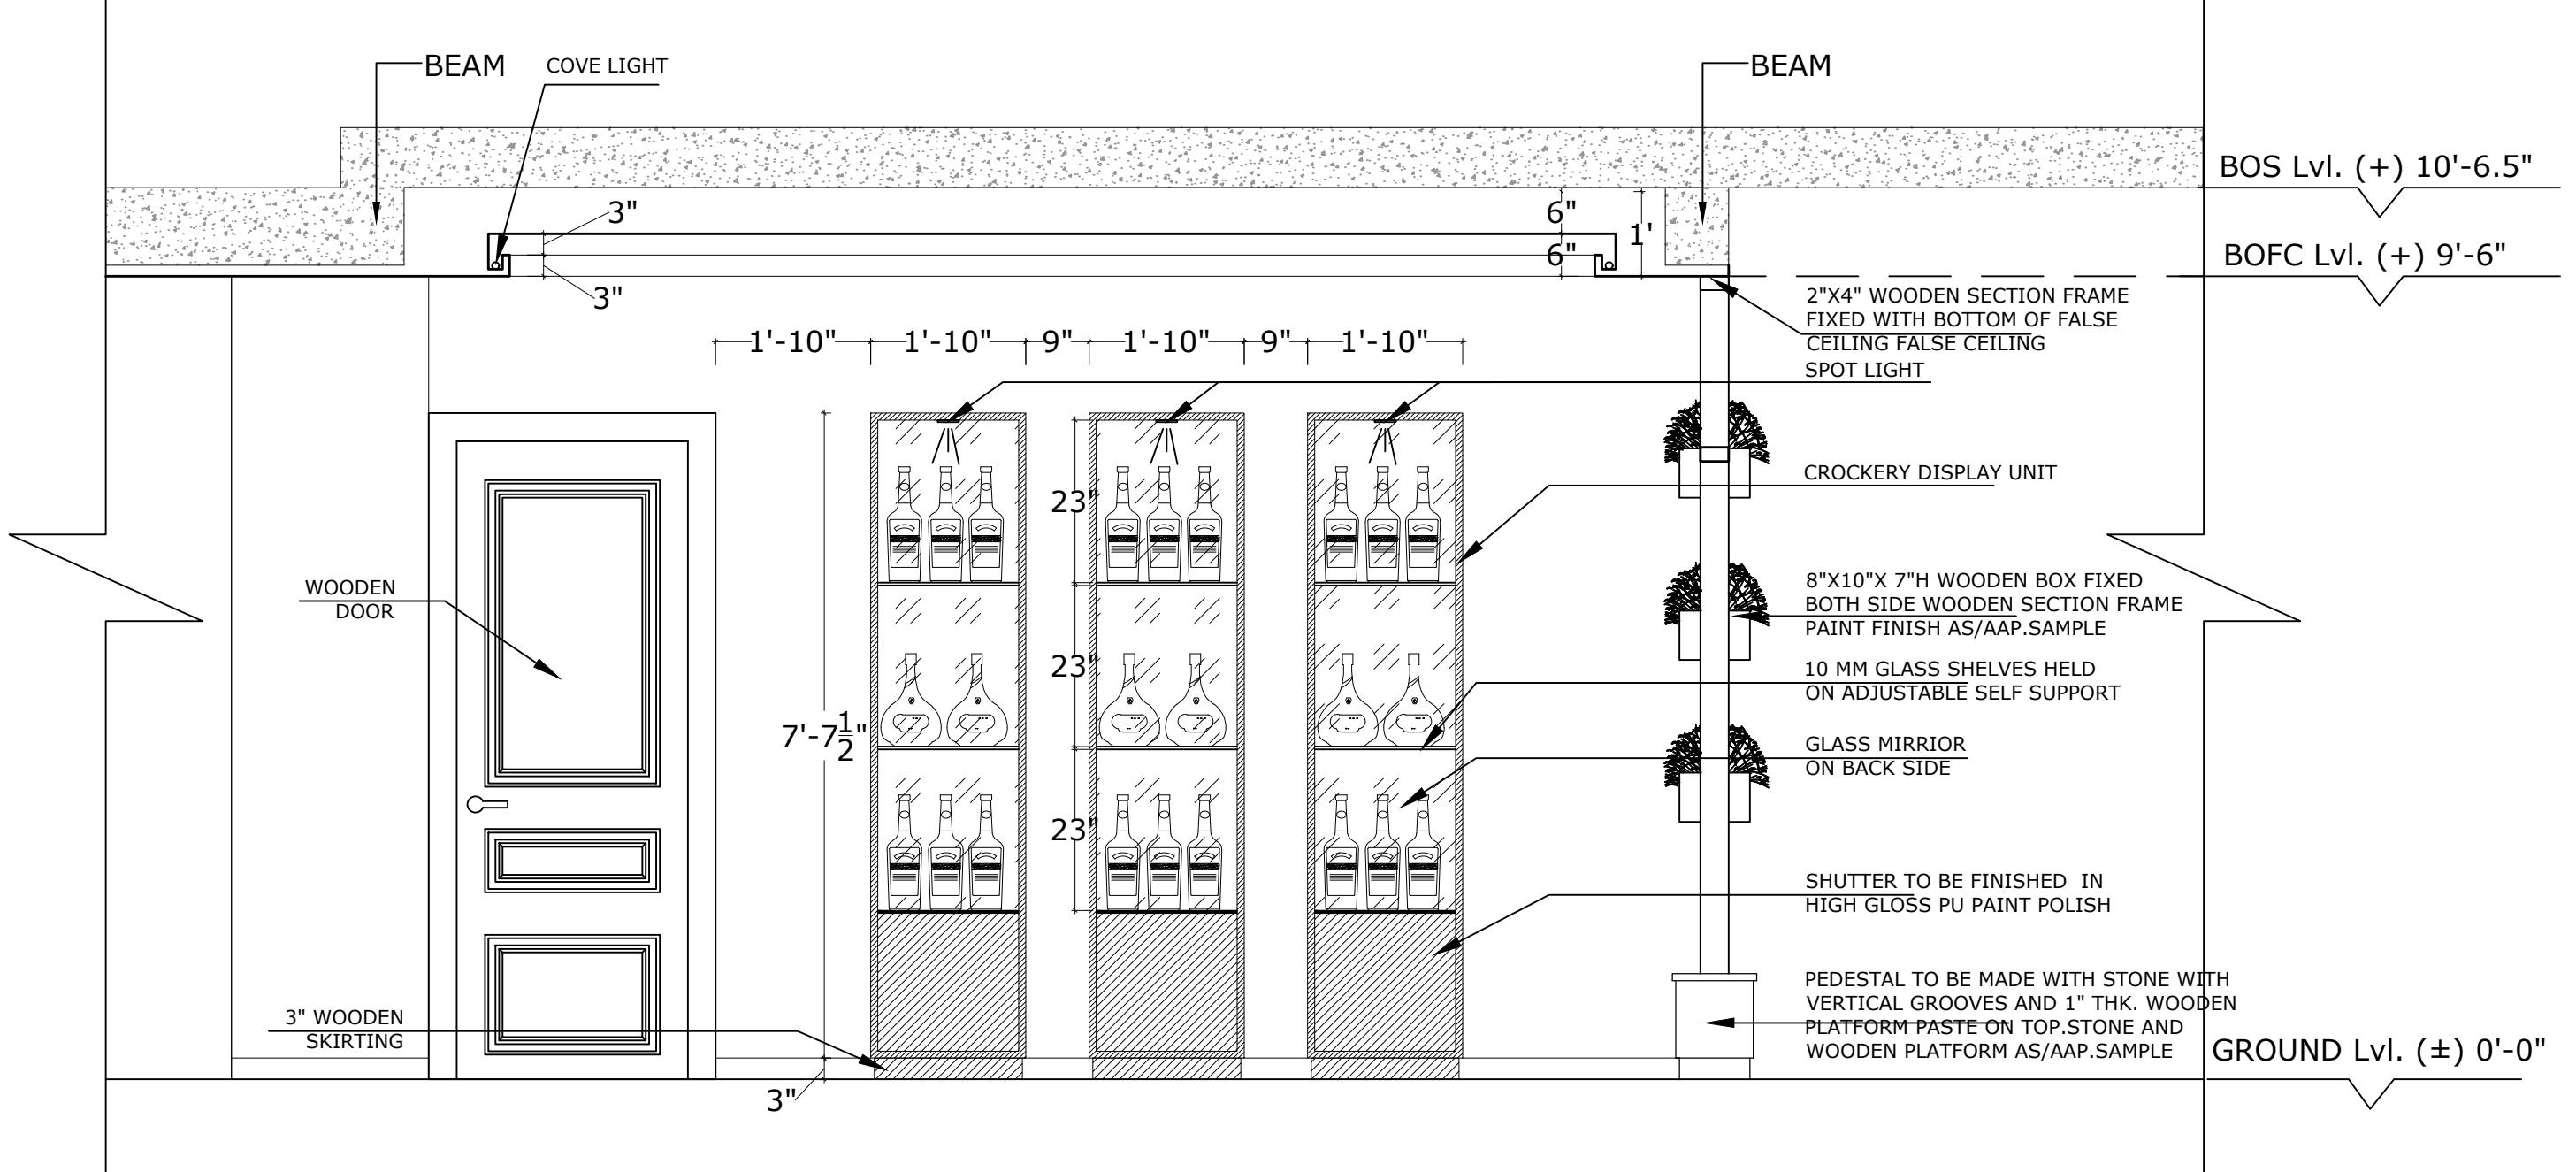


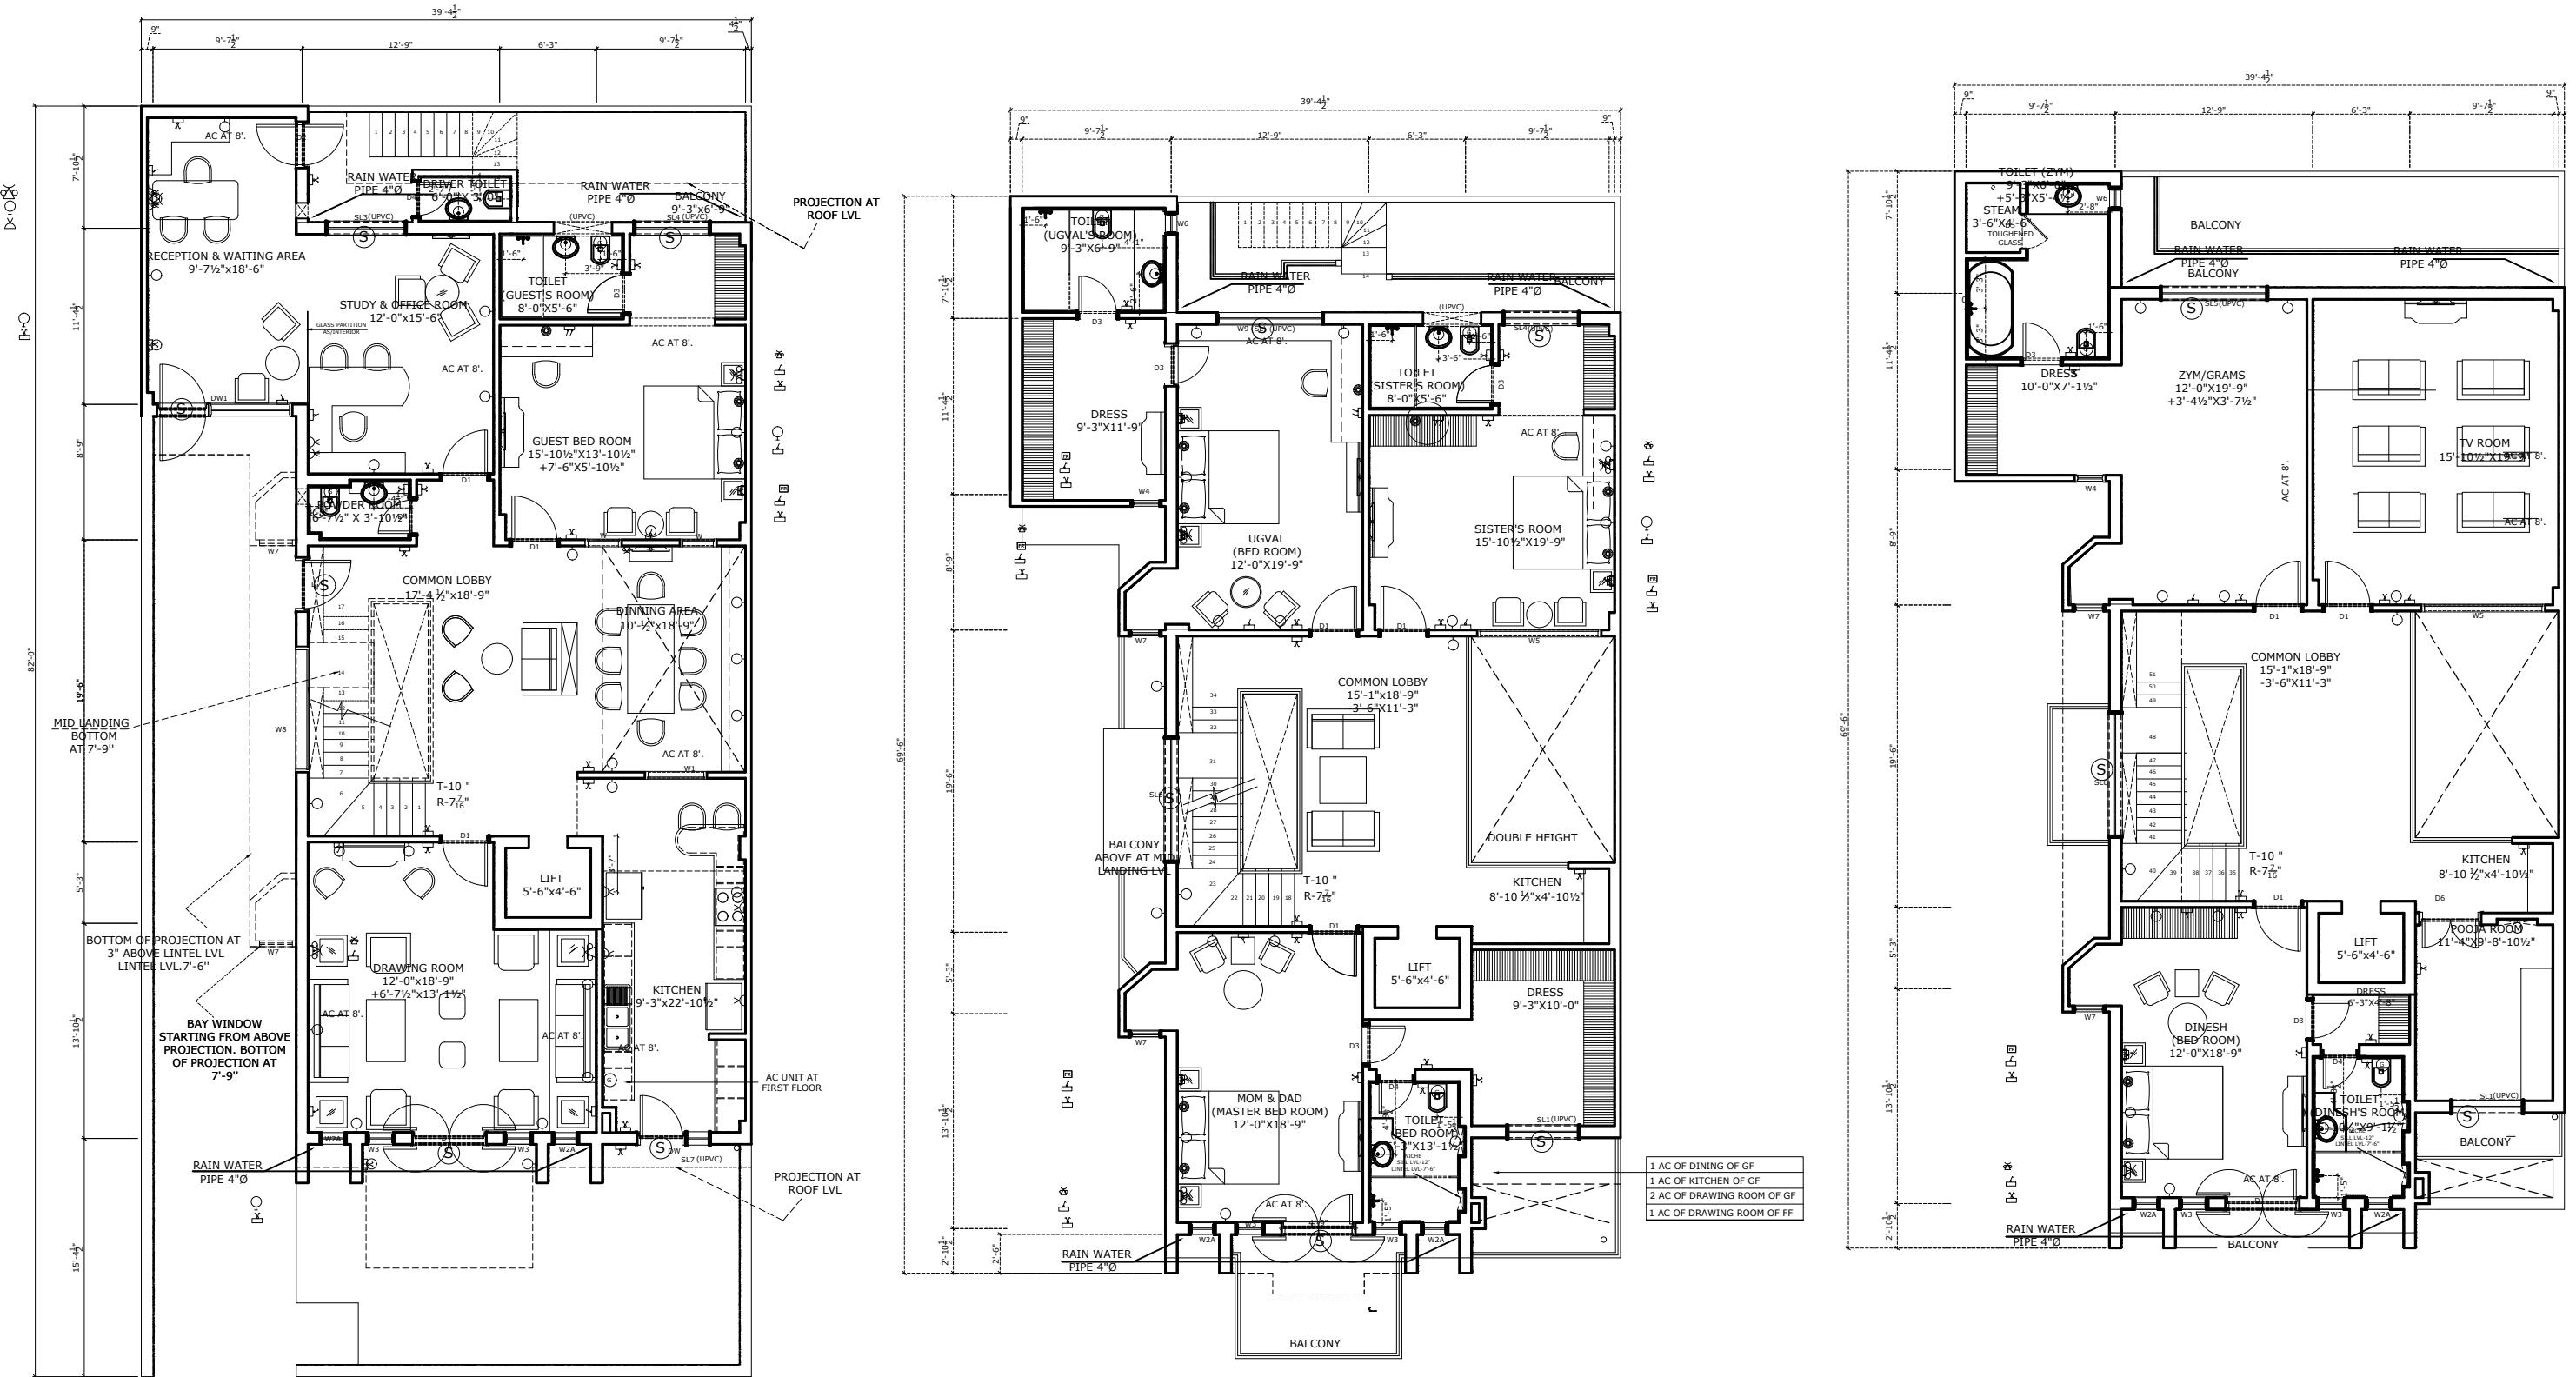



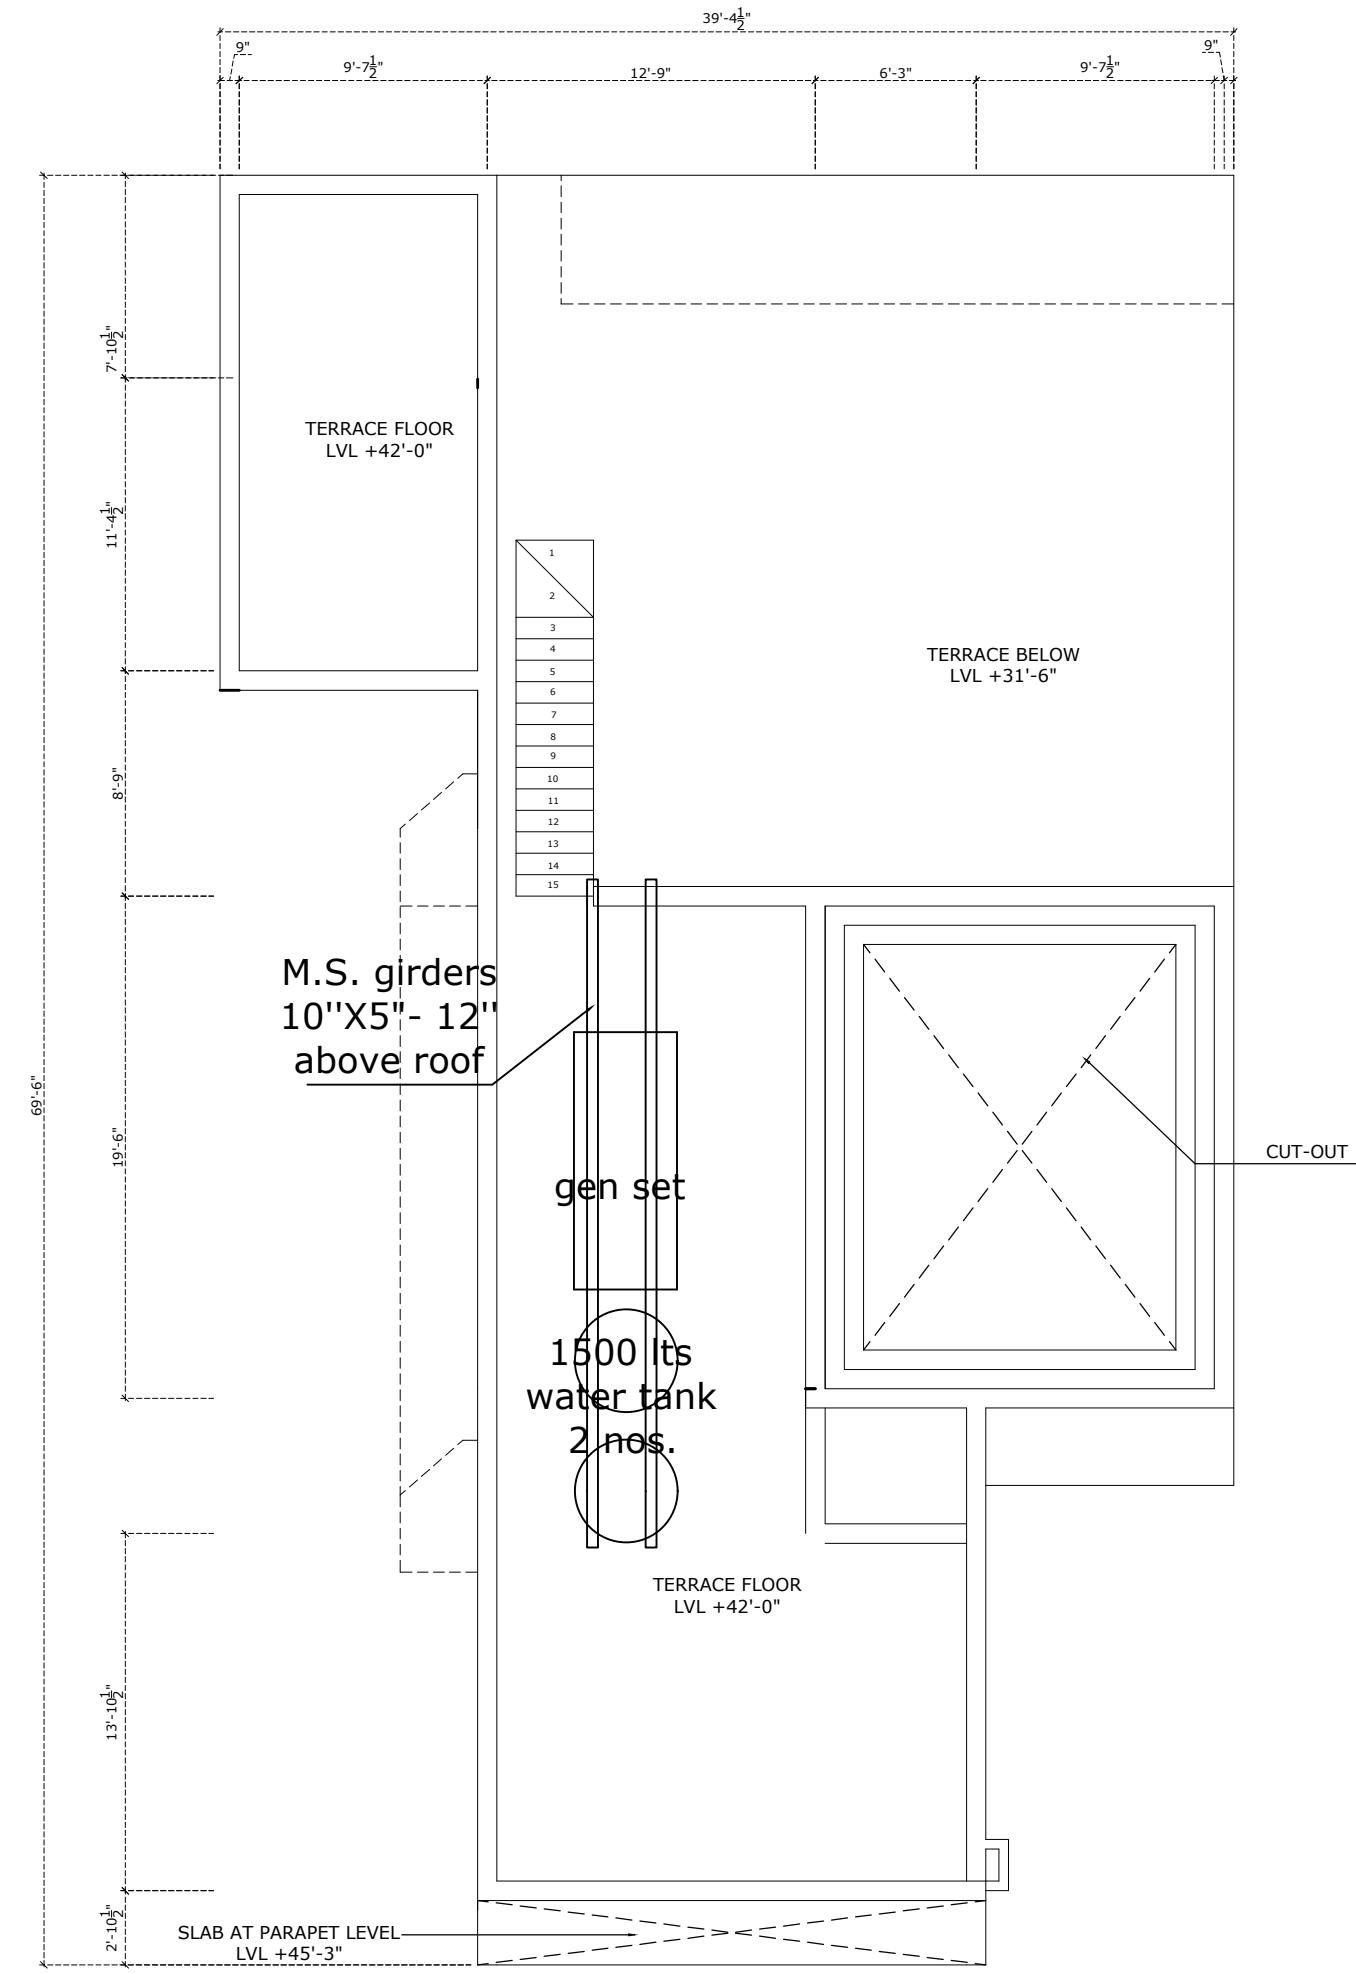
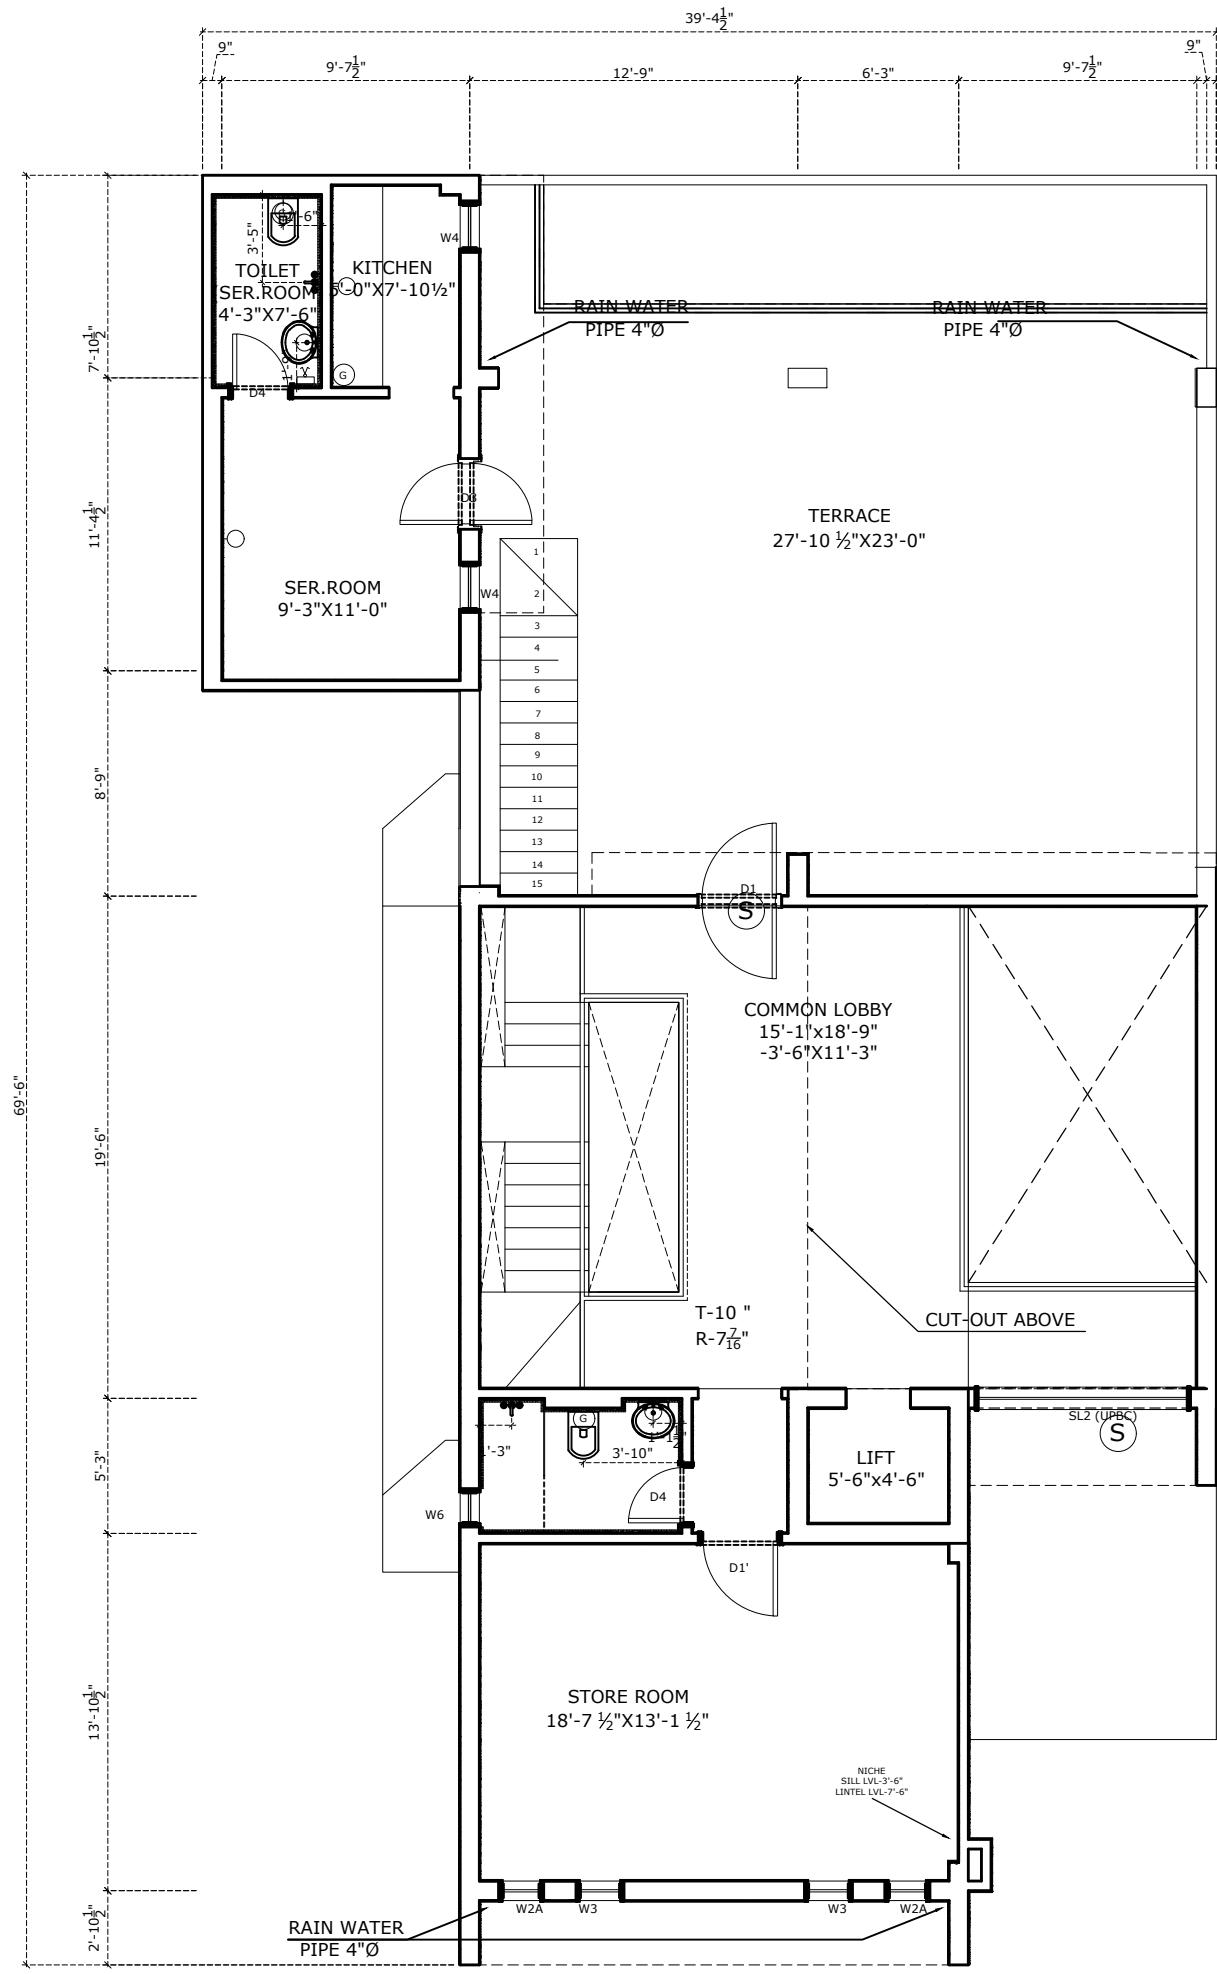


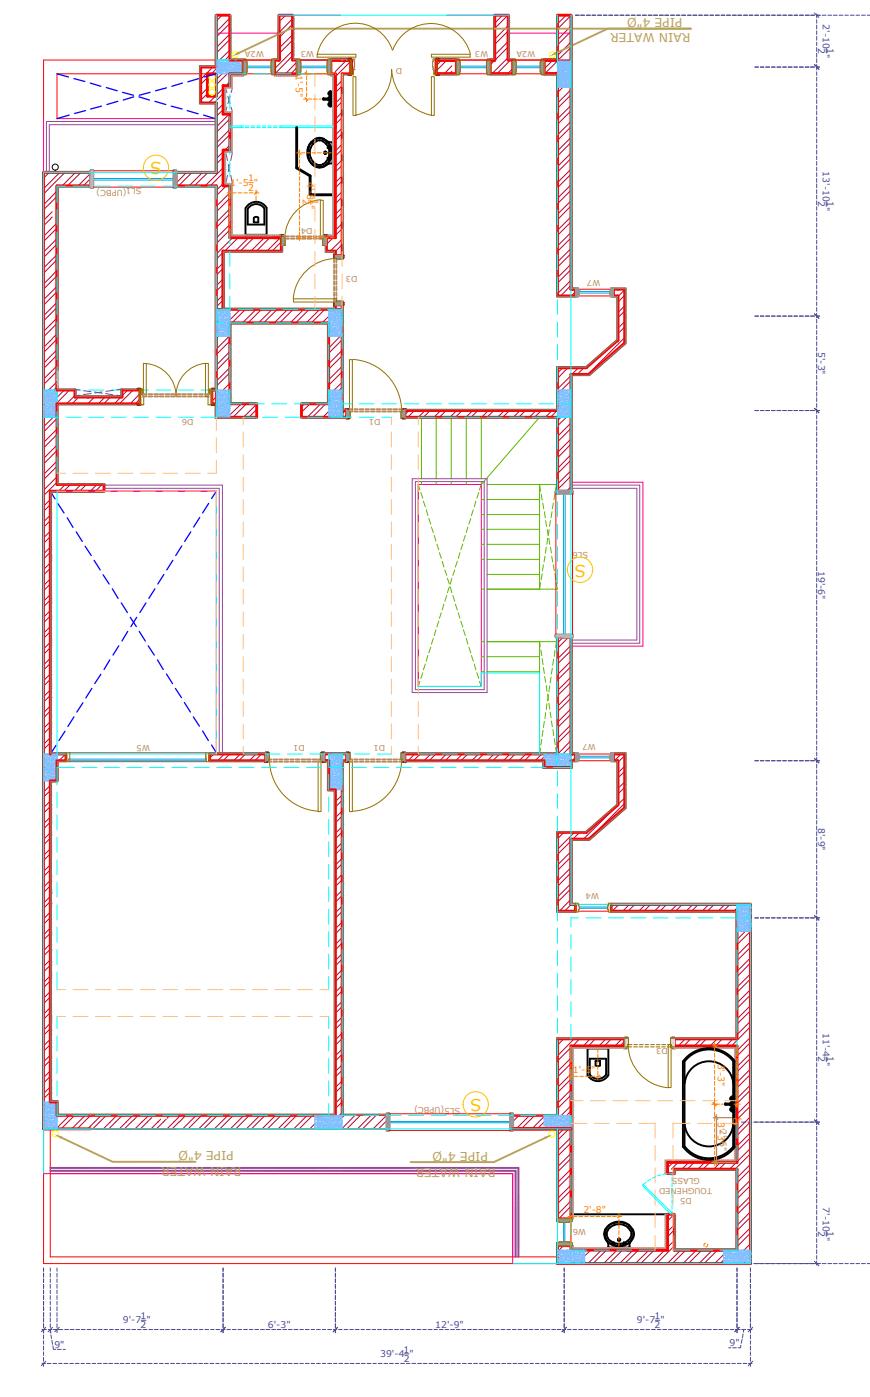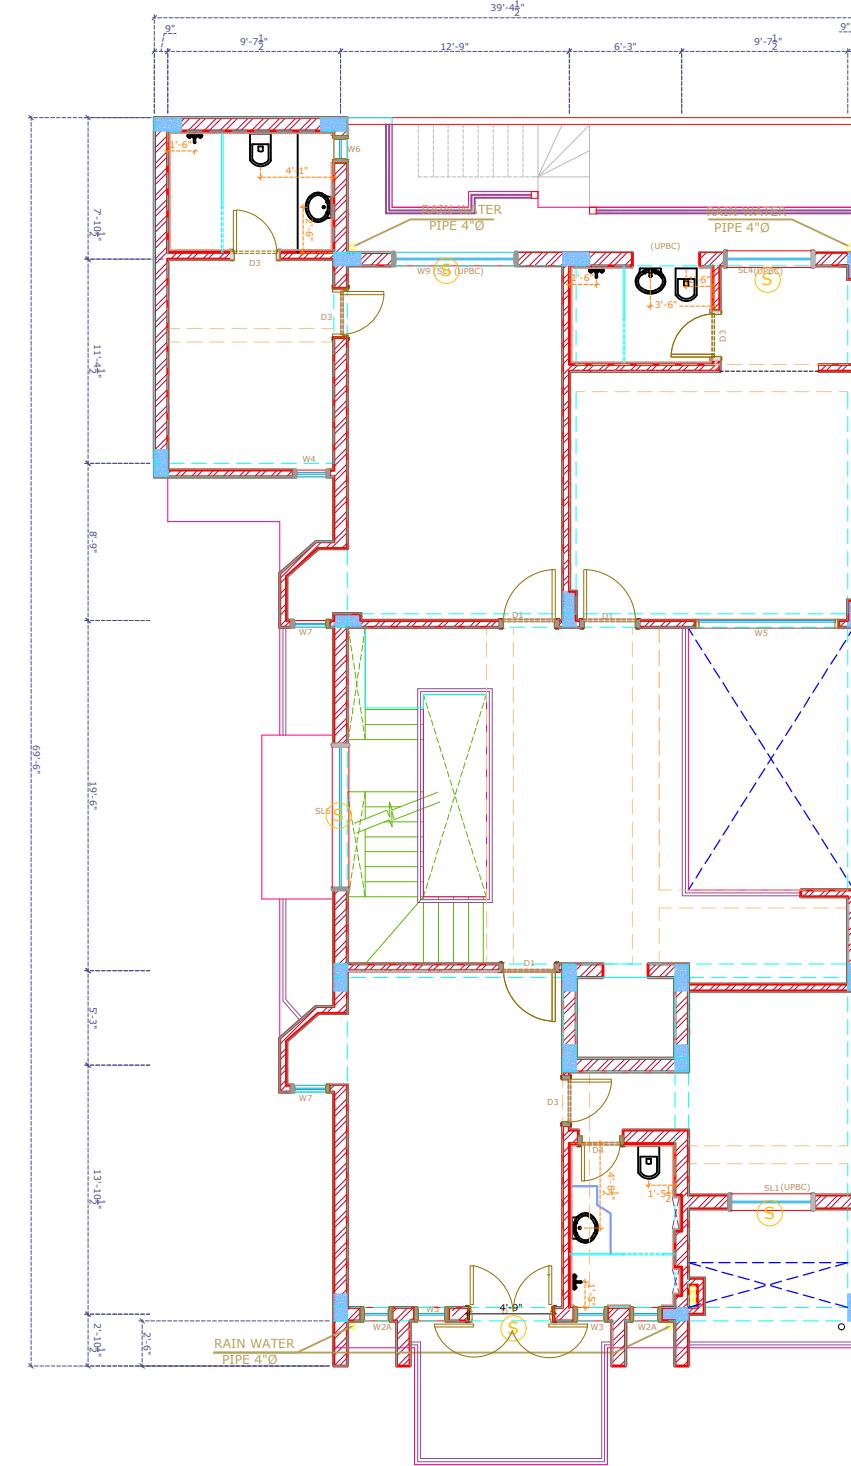
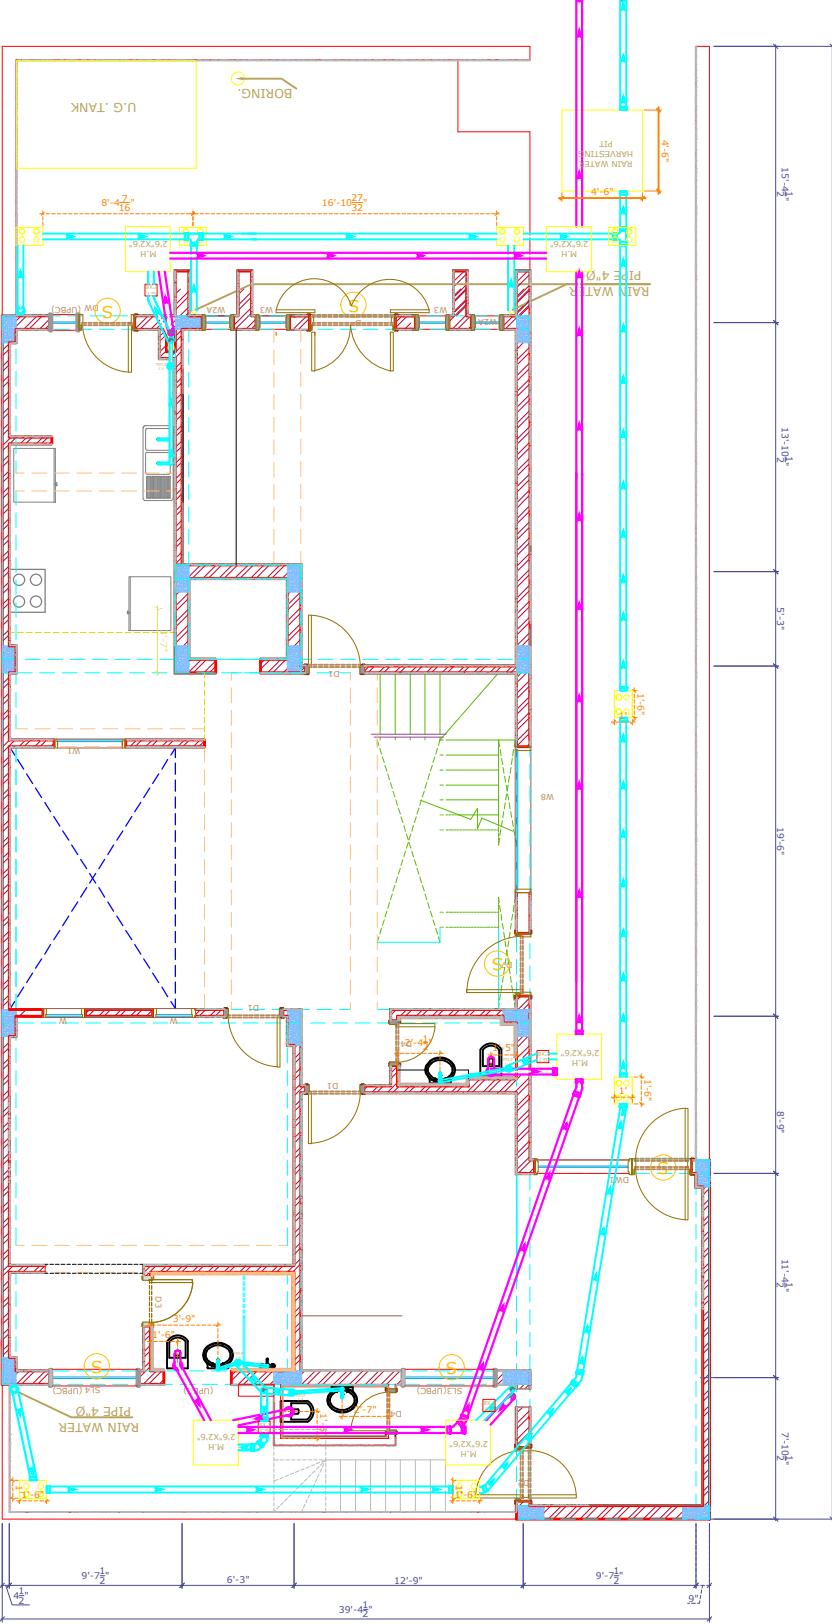


PARAPET

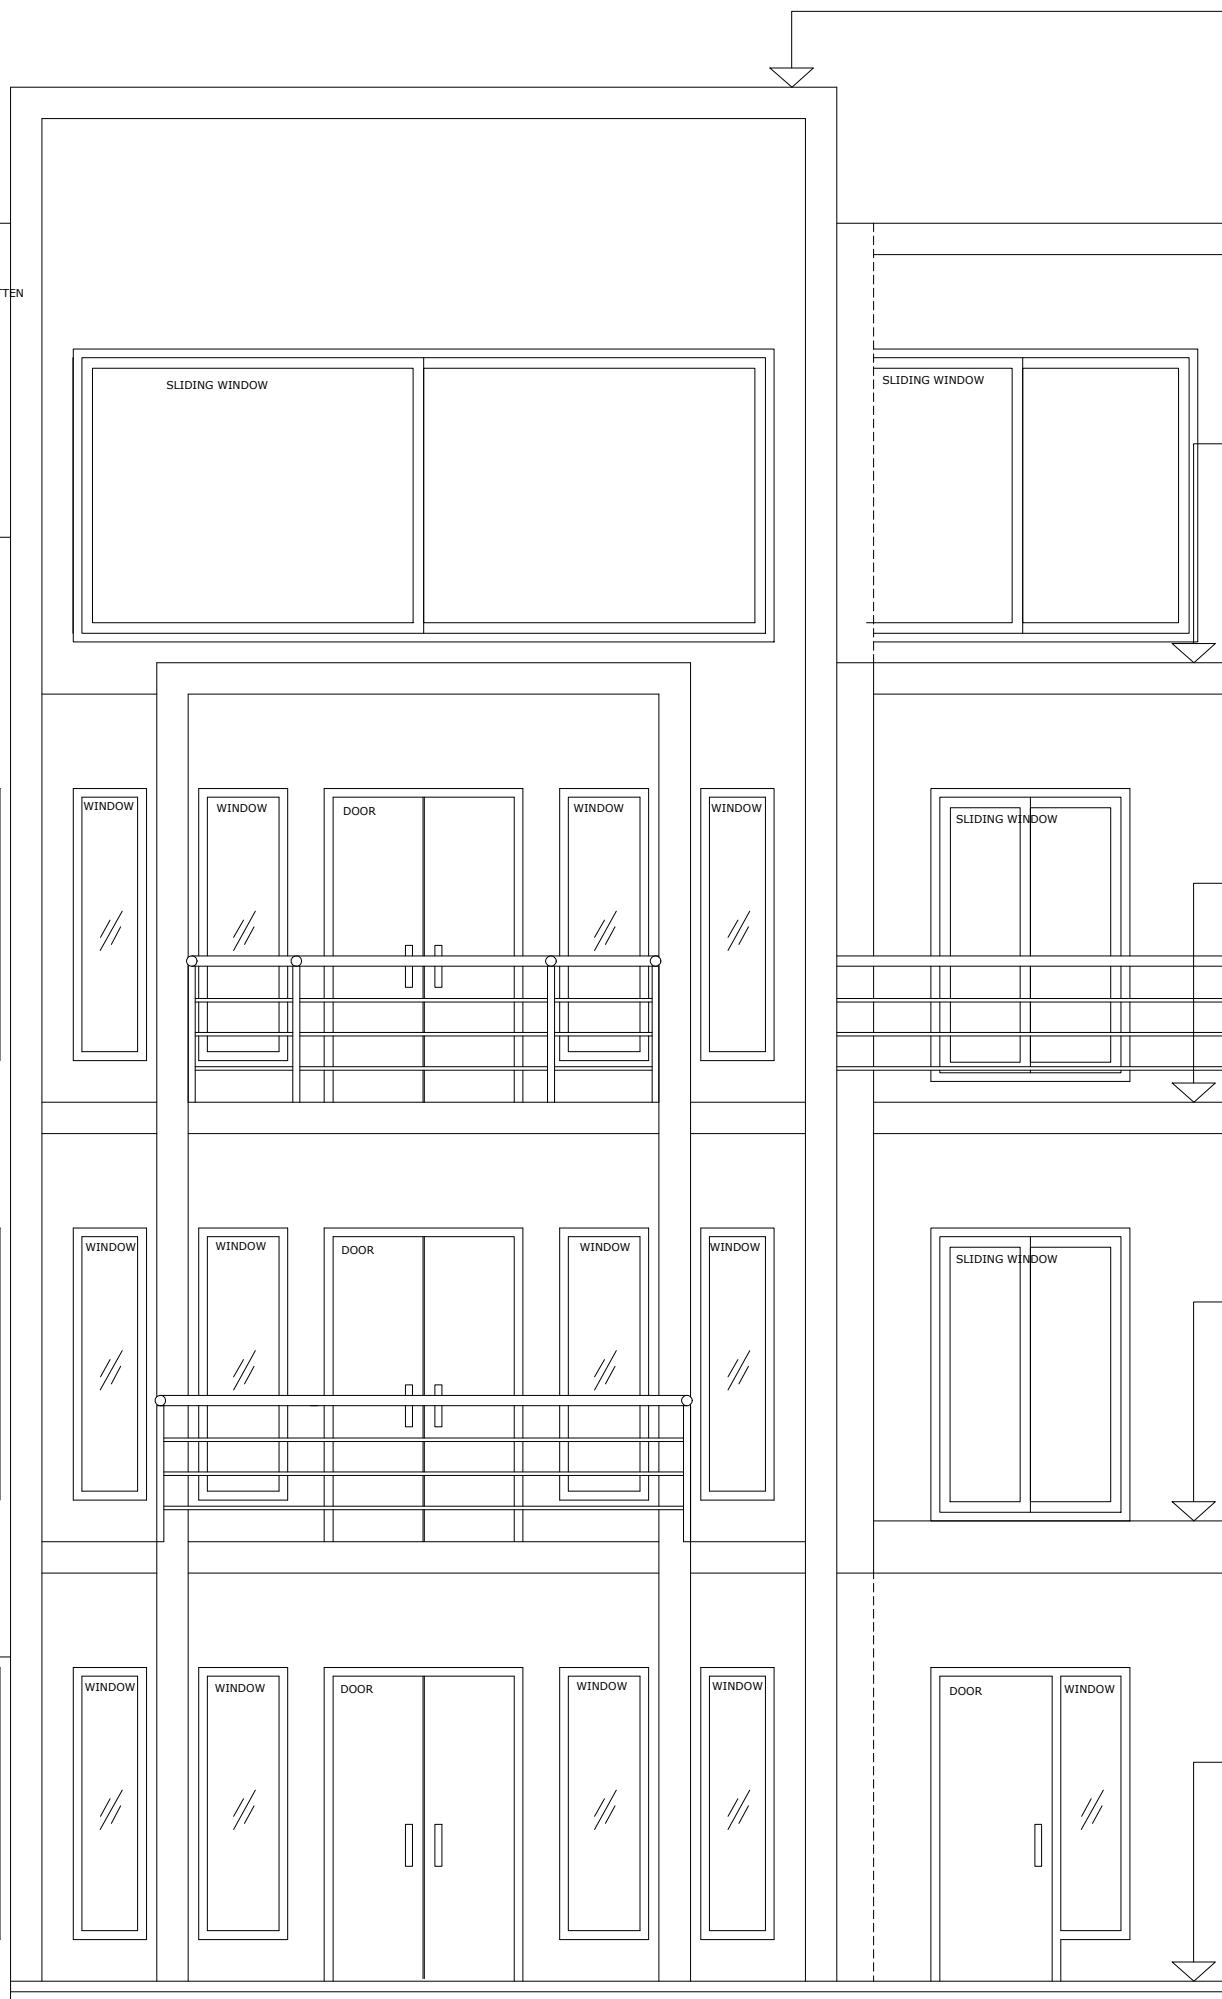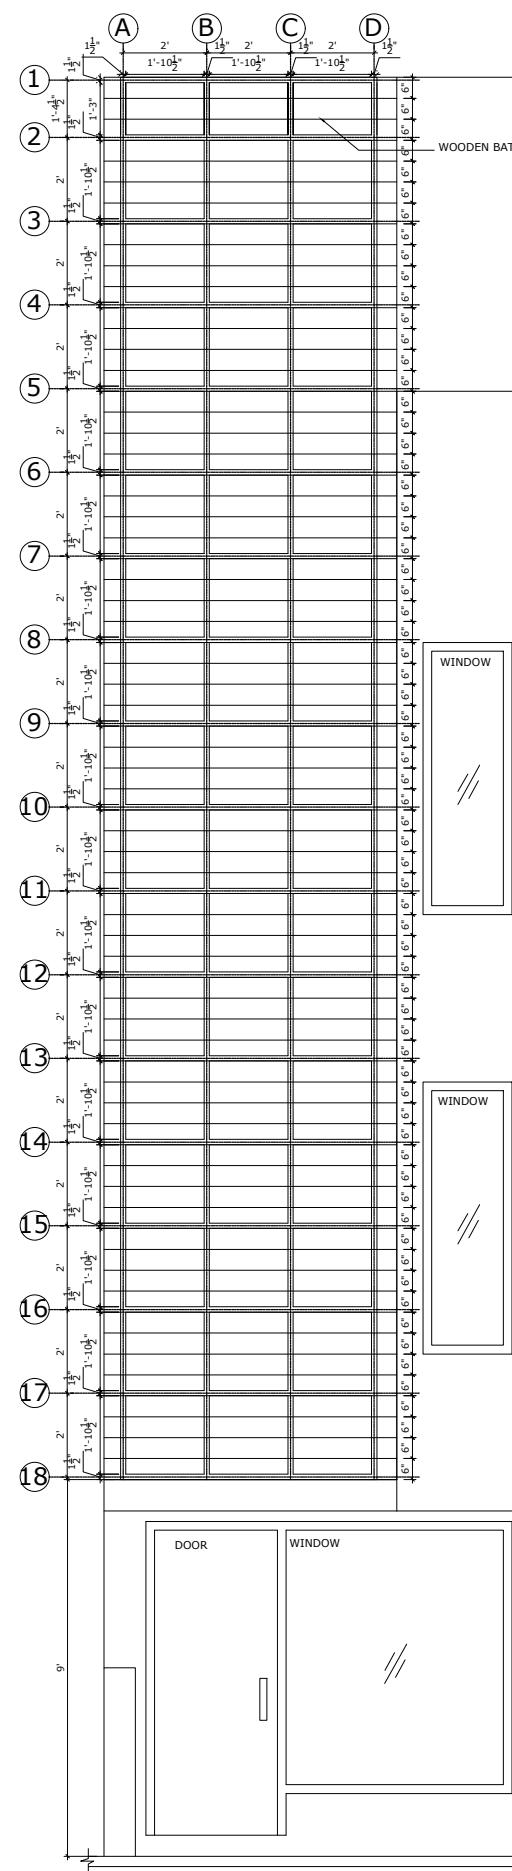

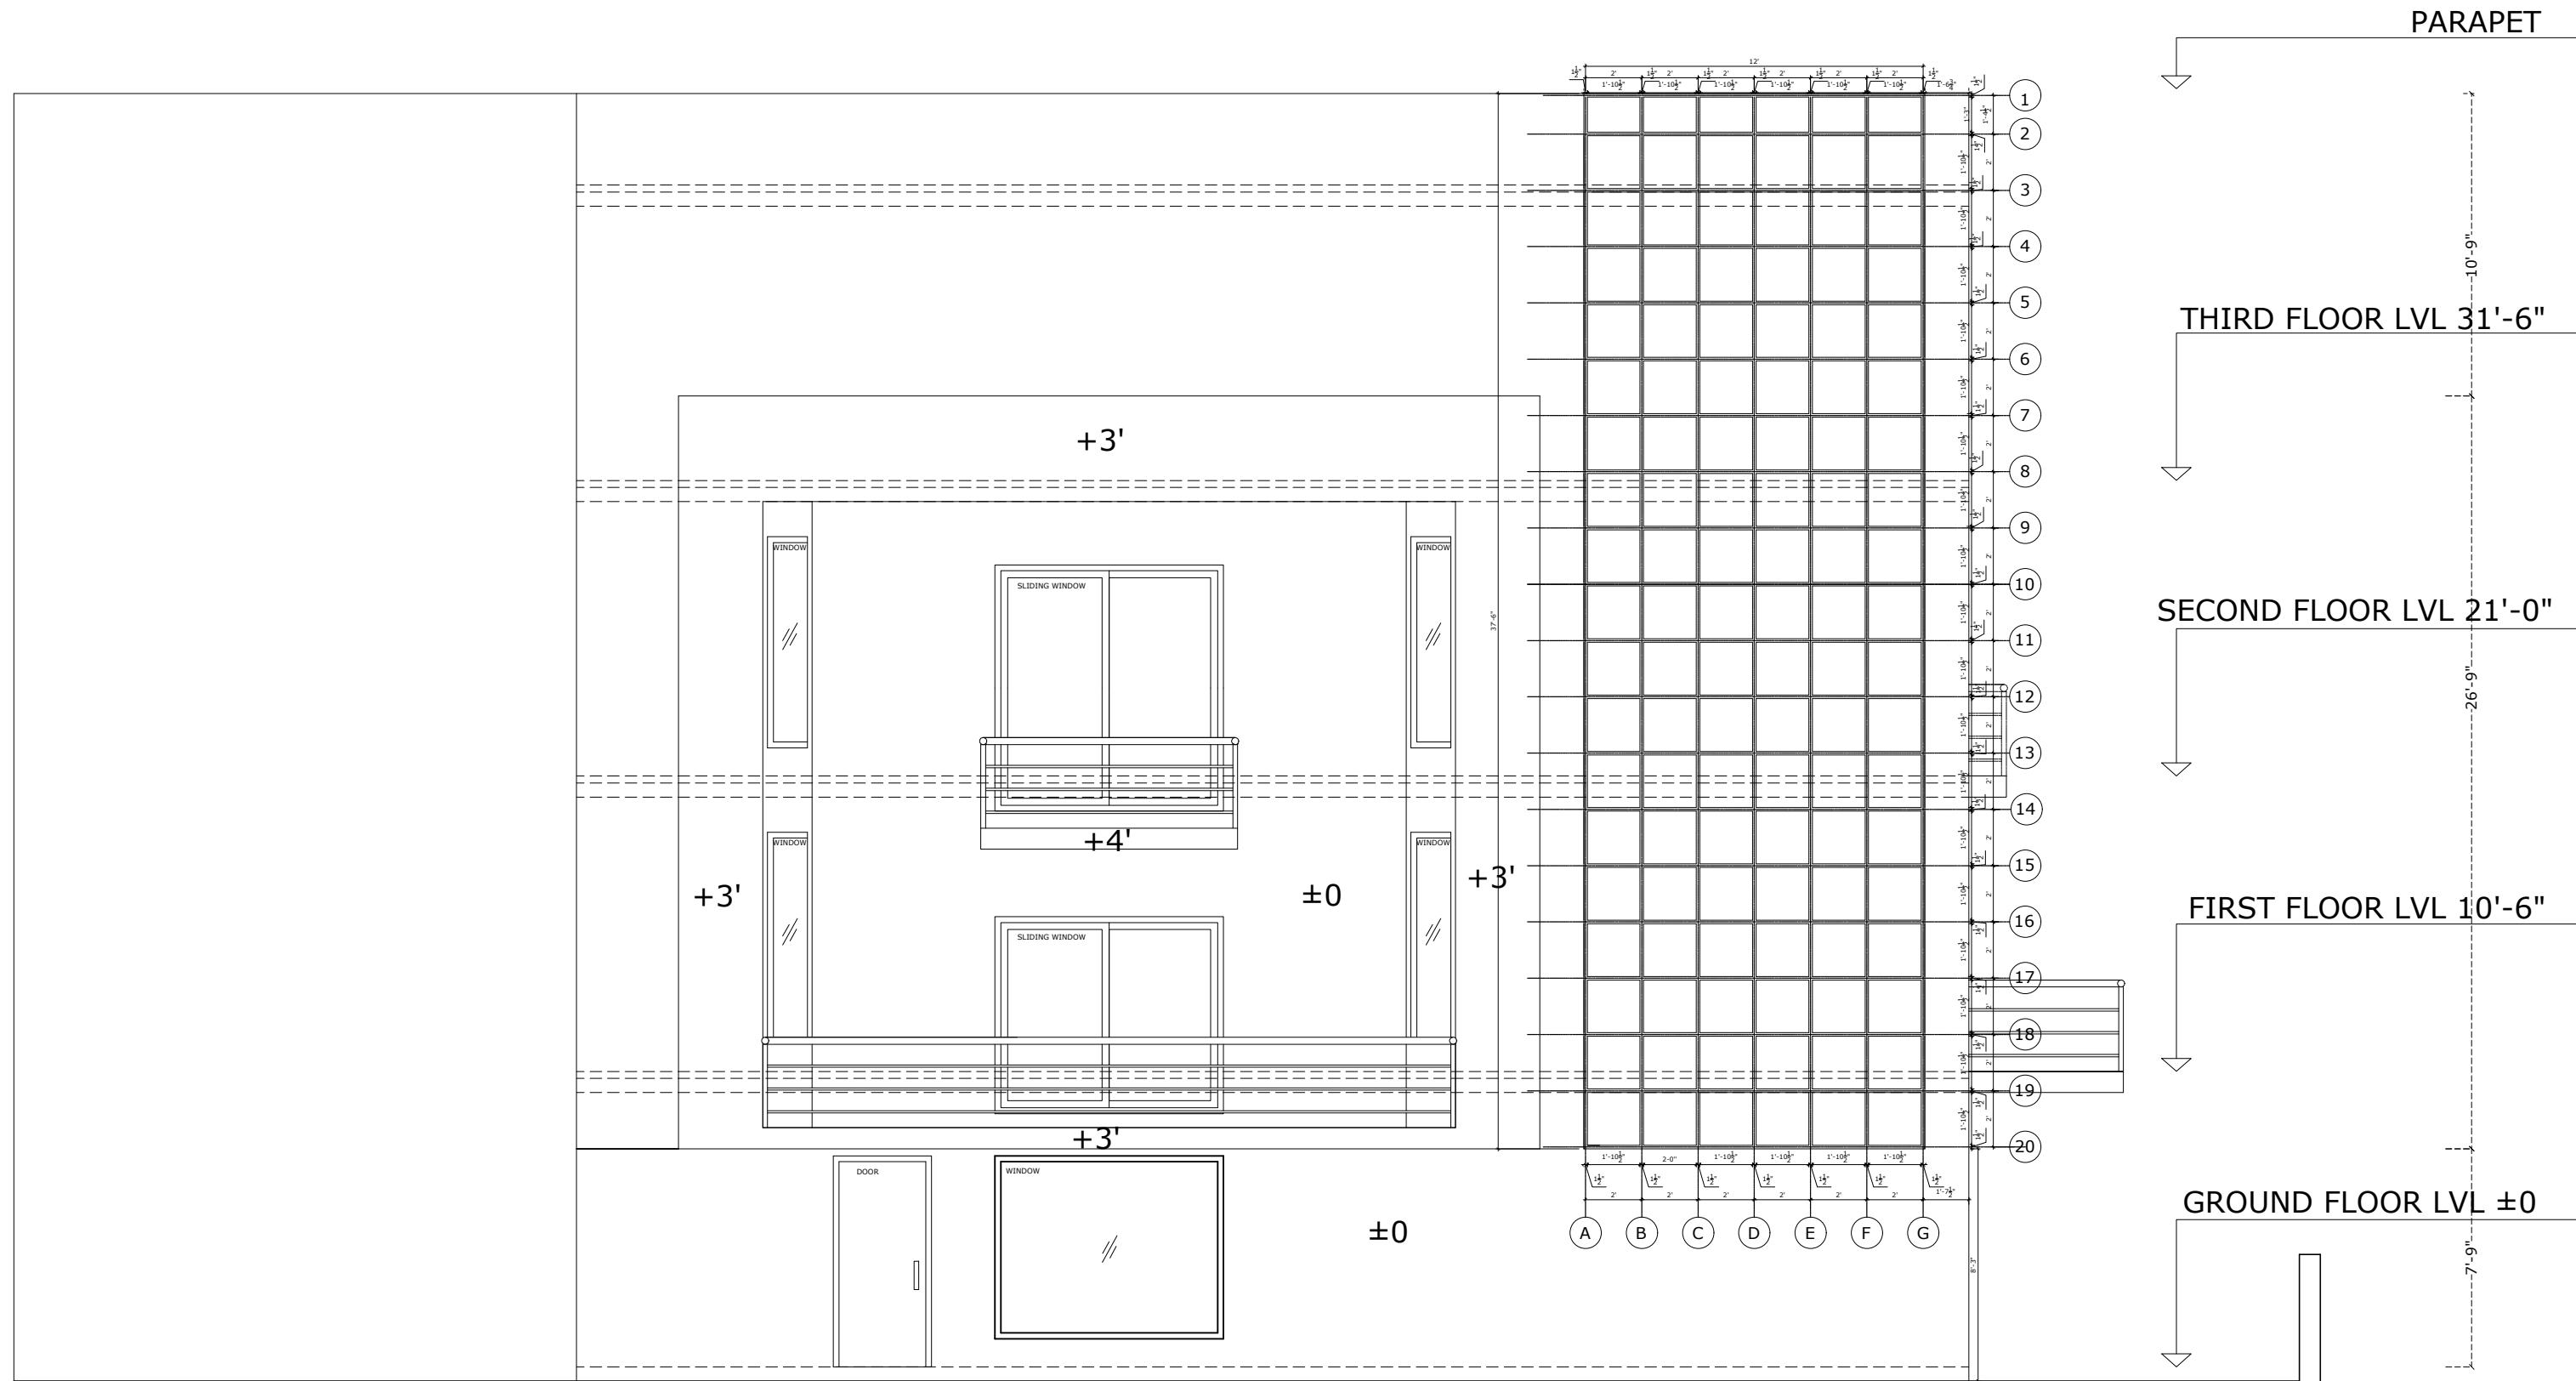

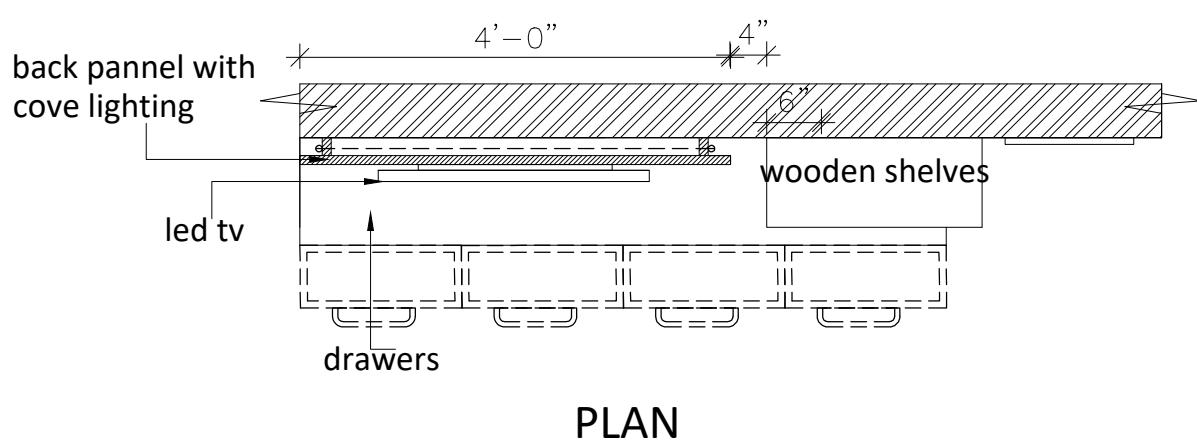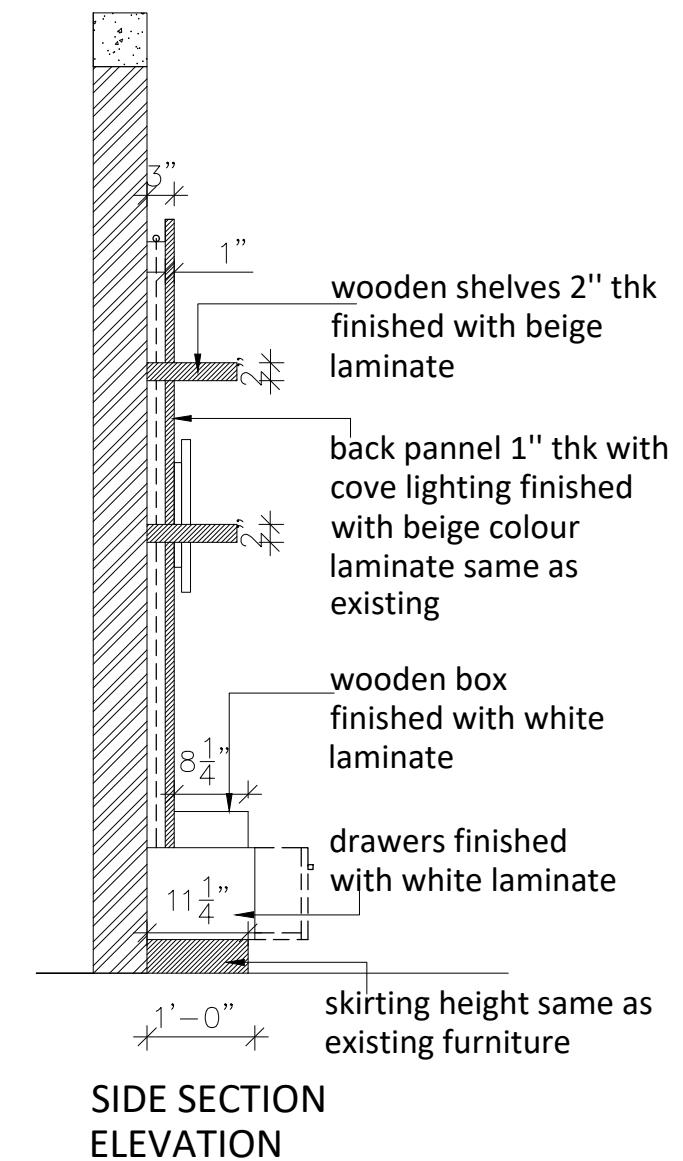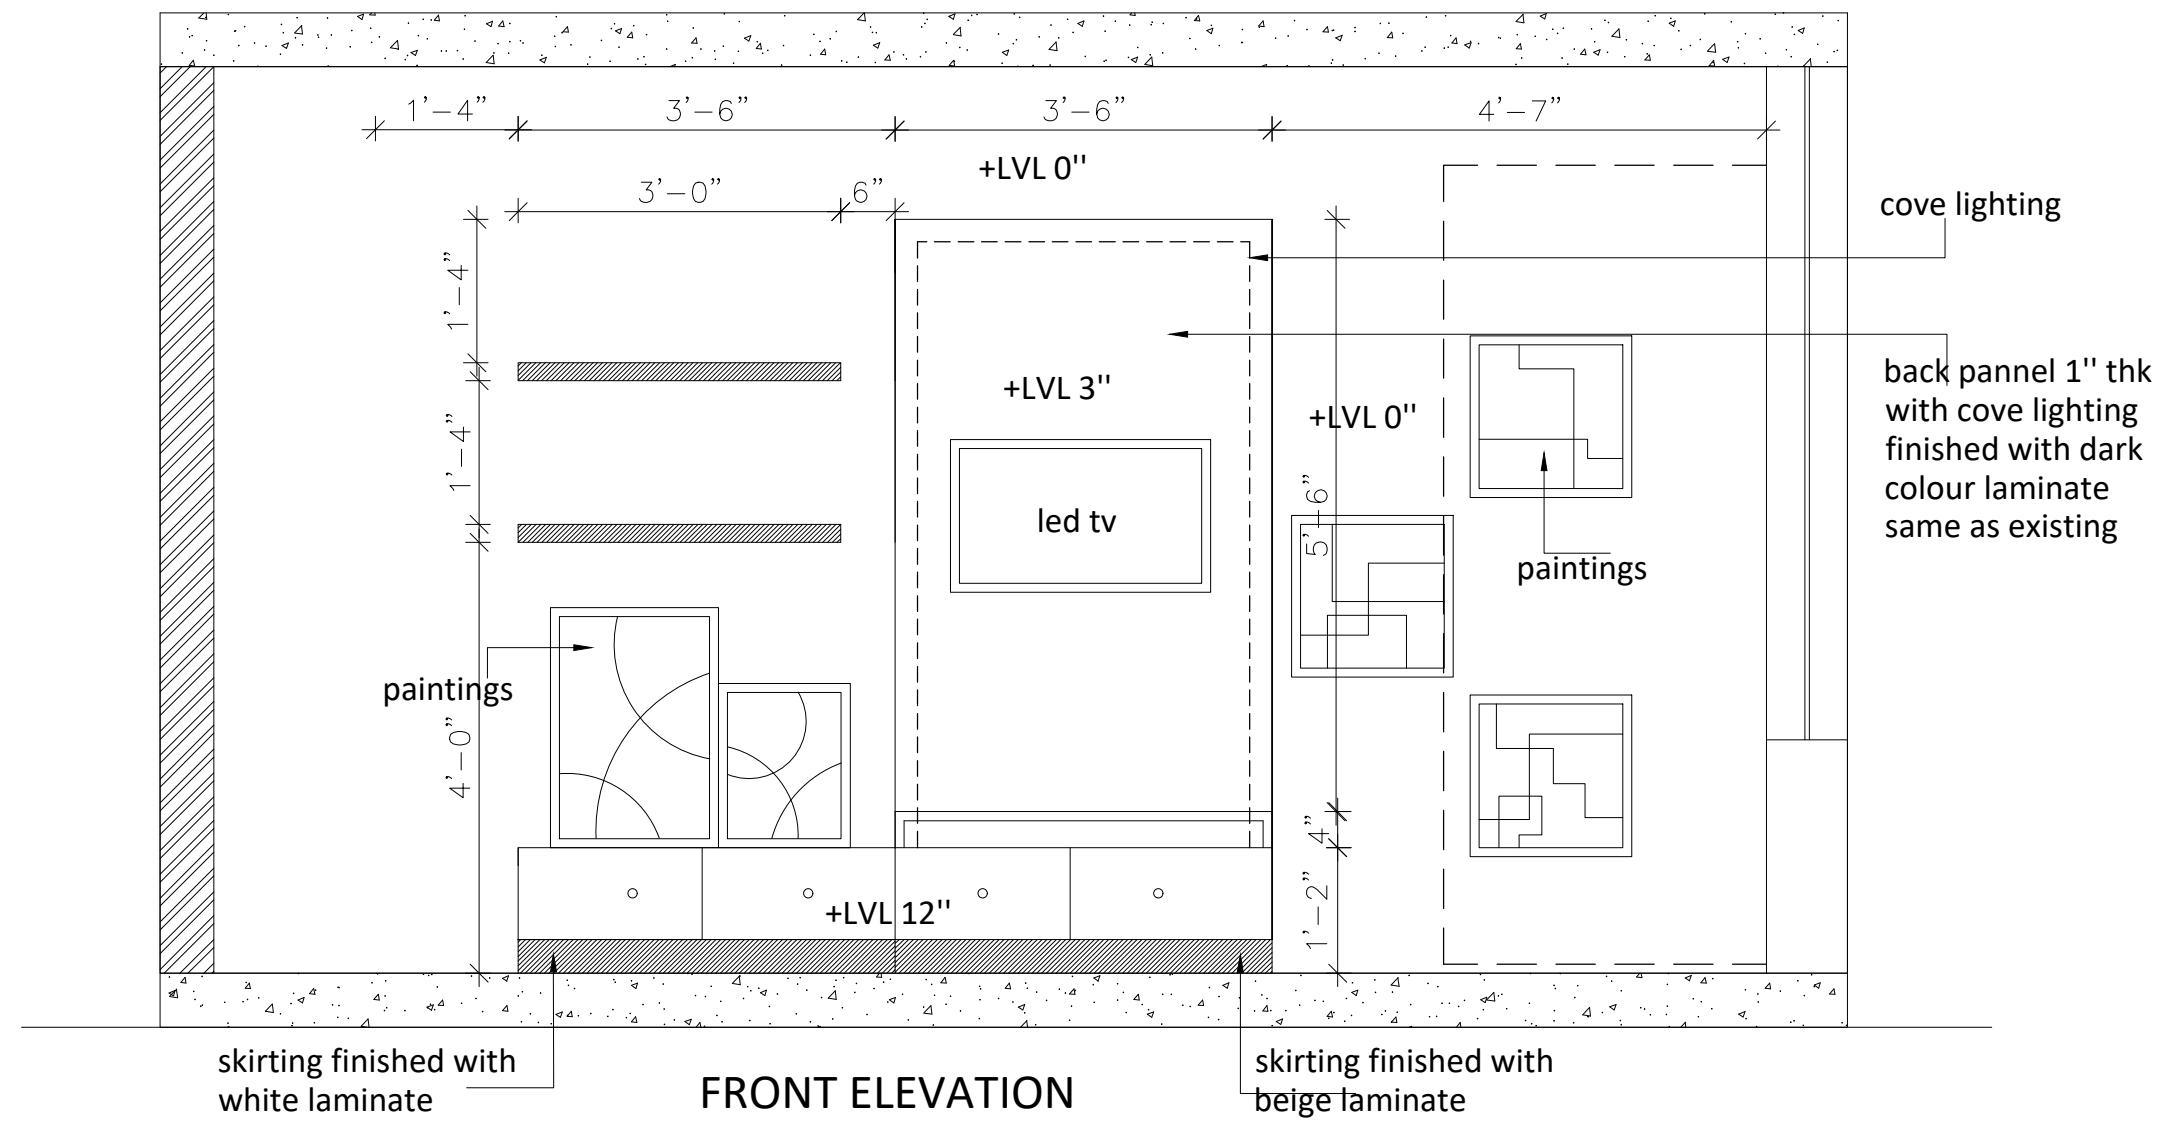

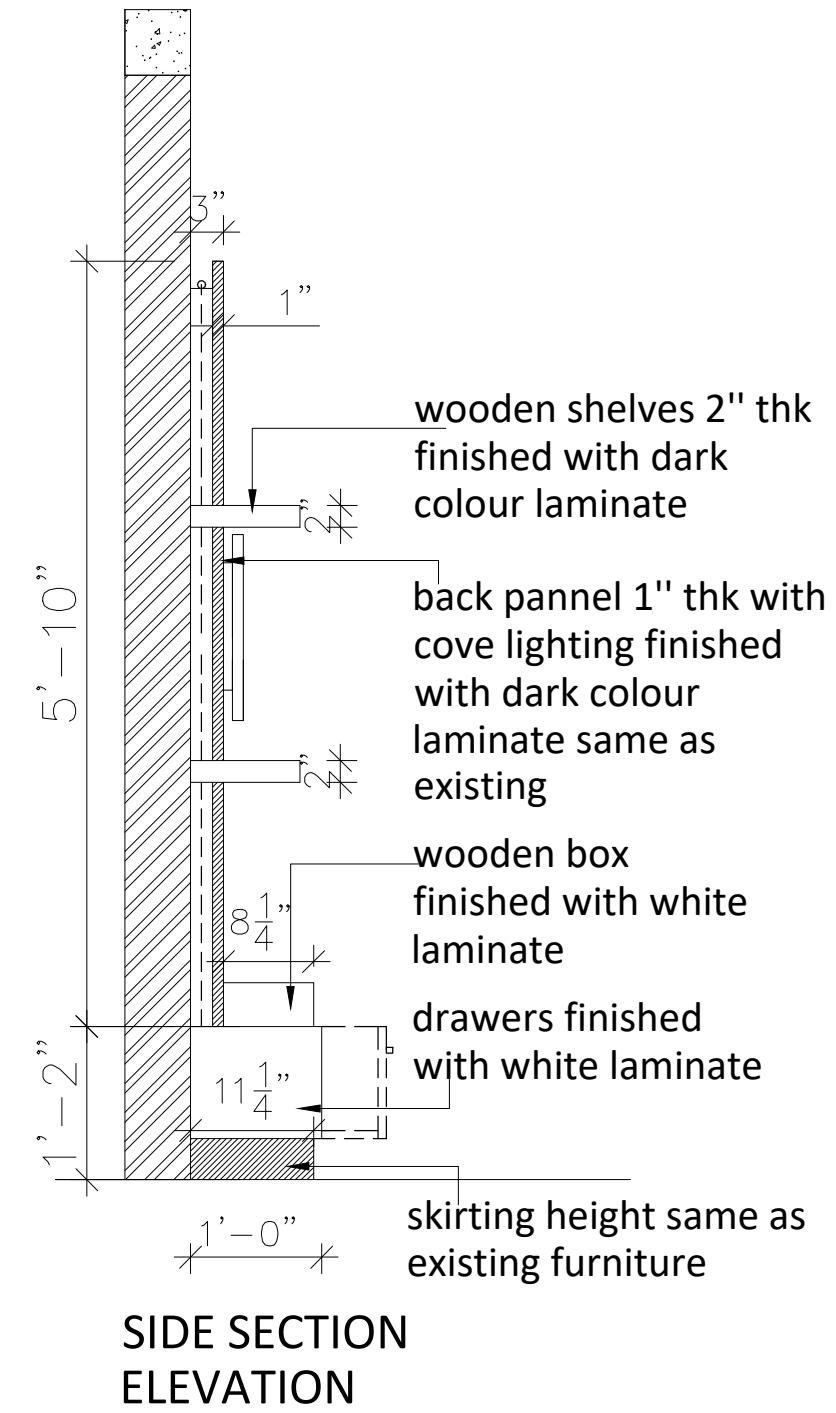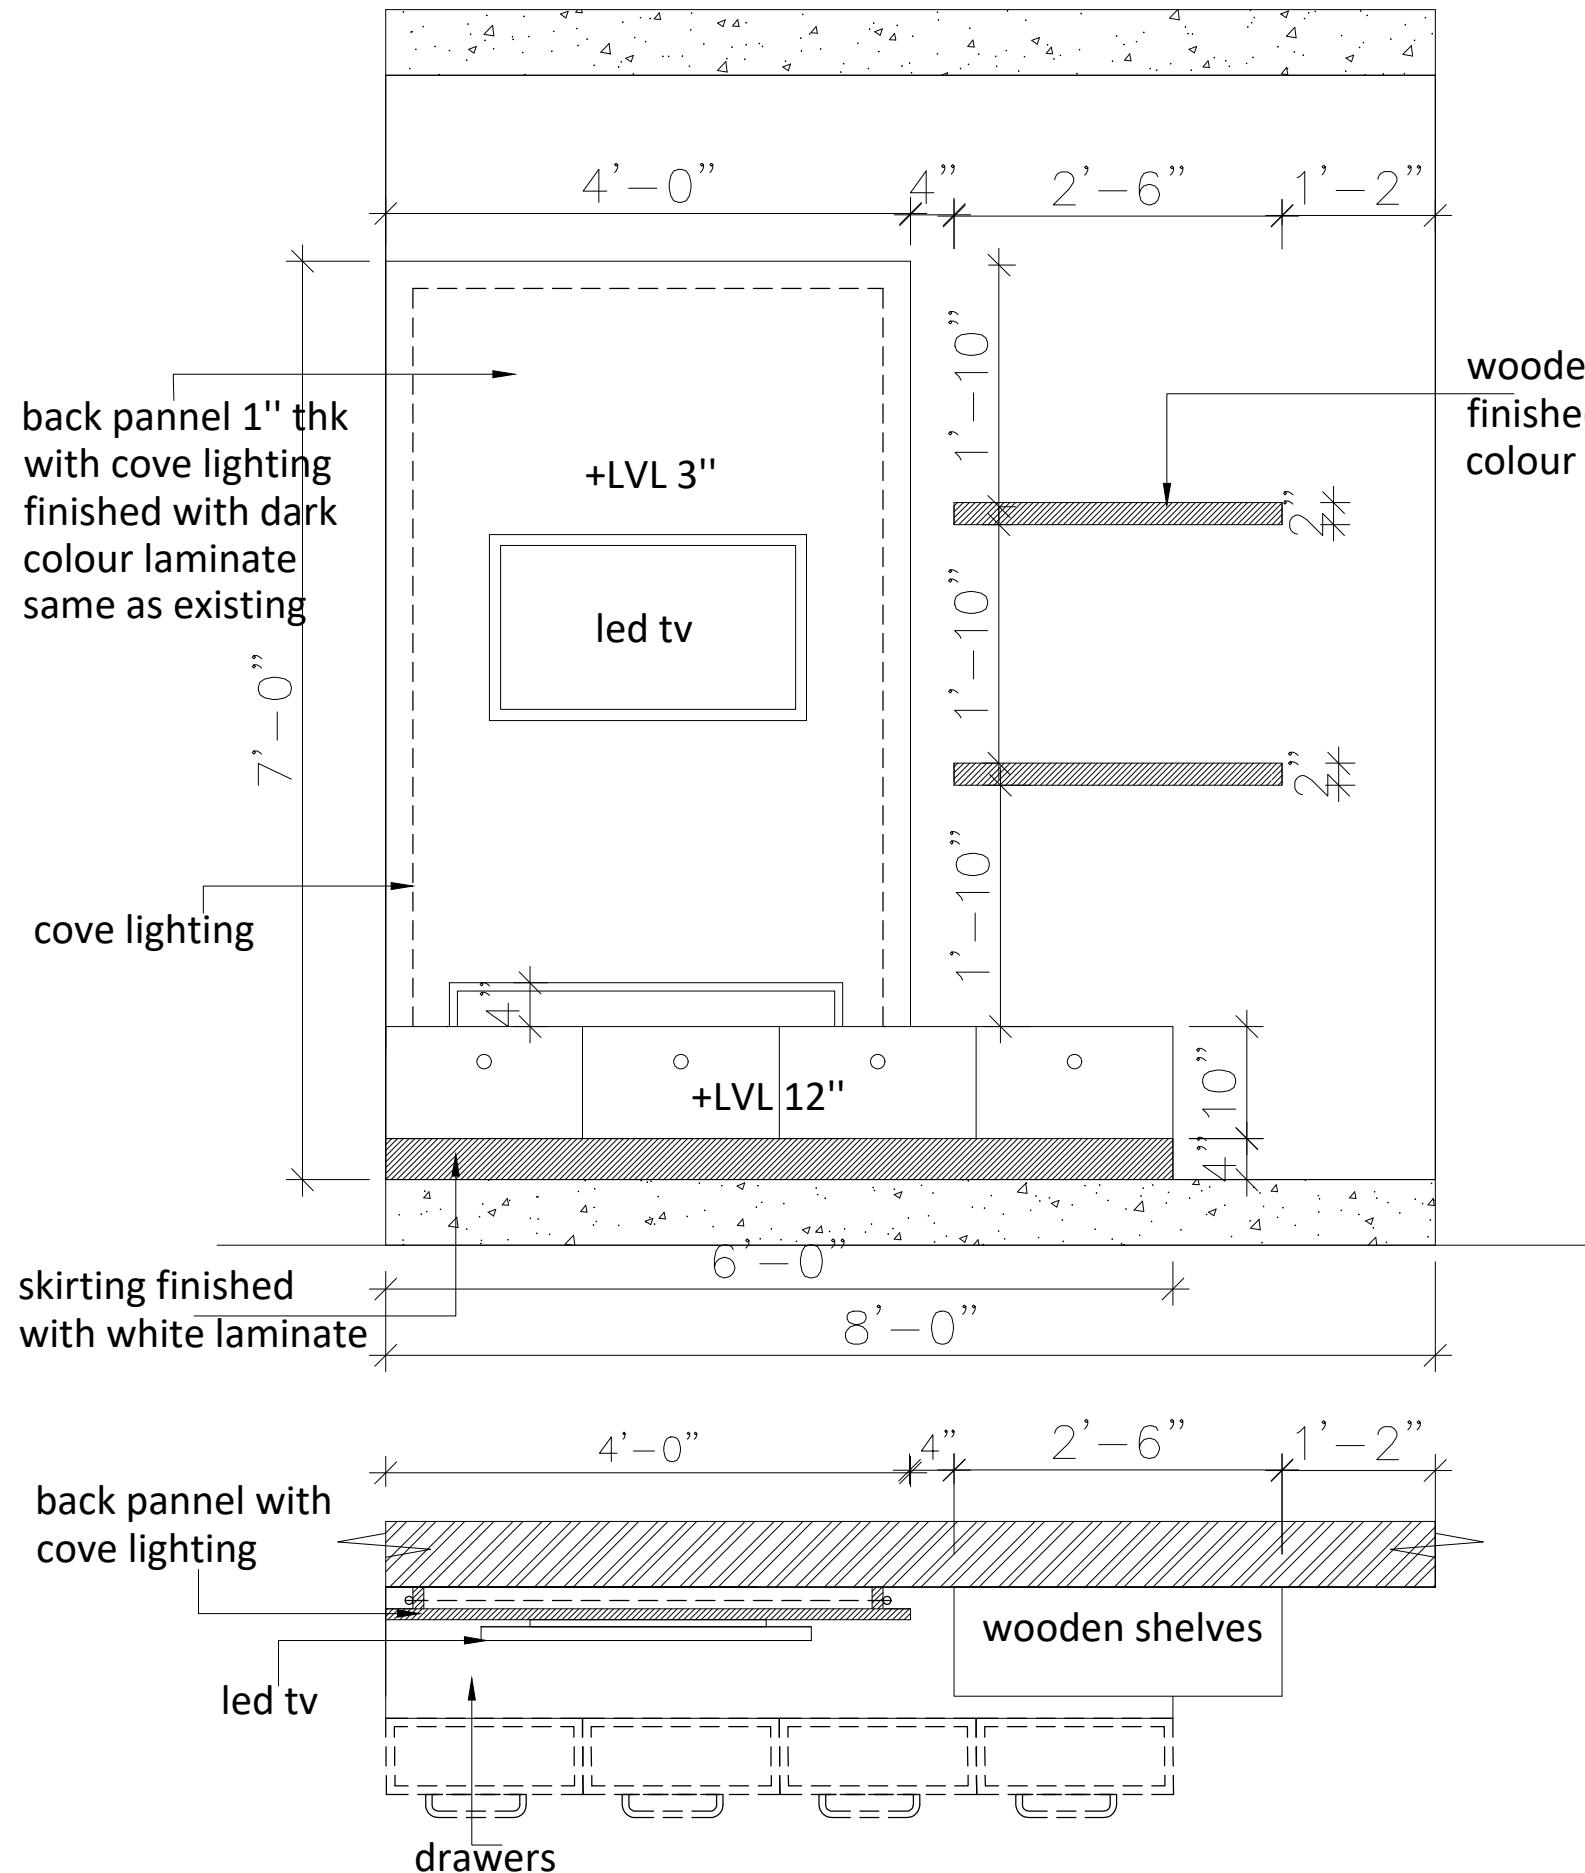

PLAN FOR LCD UNIT FOR
MASTER BEDROOM