


CONSTRUCTION DRAWINGS

INTERIOR DESIGN | ARCHITECTURE

LG Business Innovation Center


Across India— Retail Projects

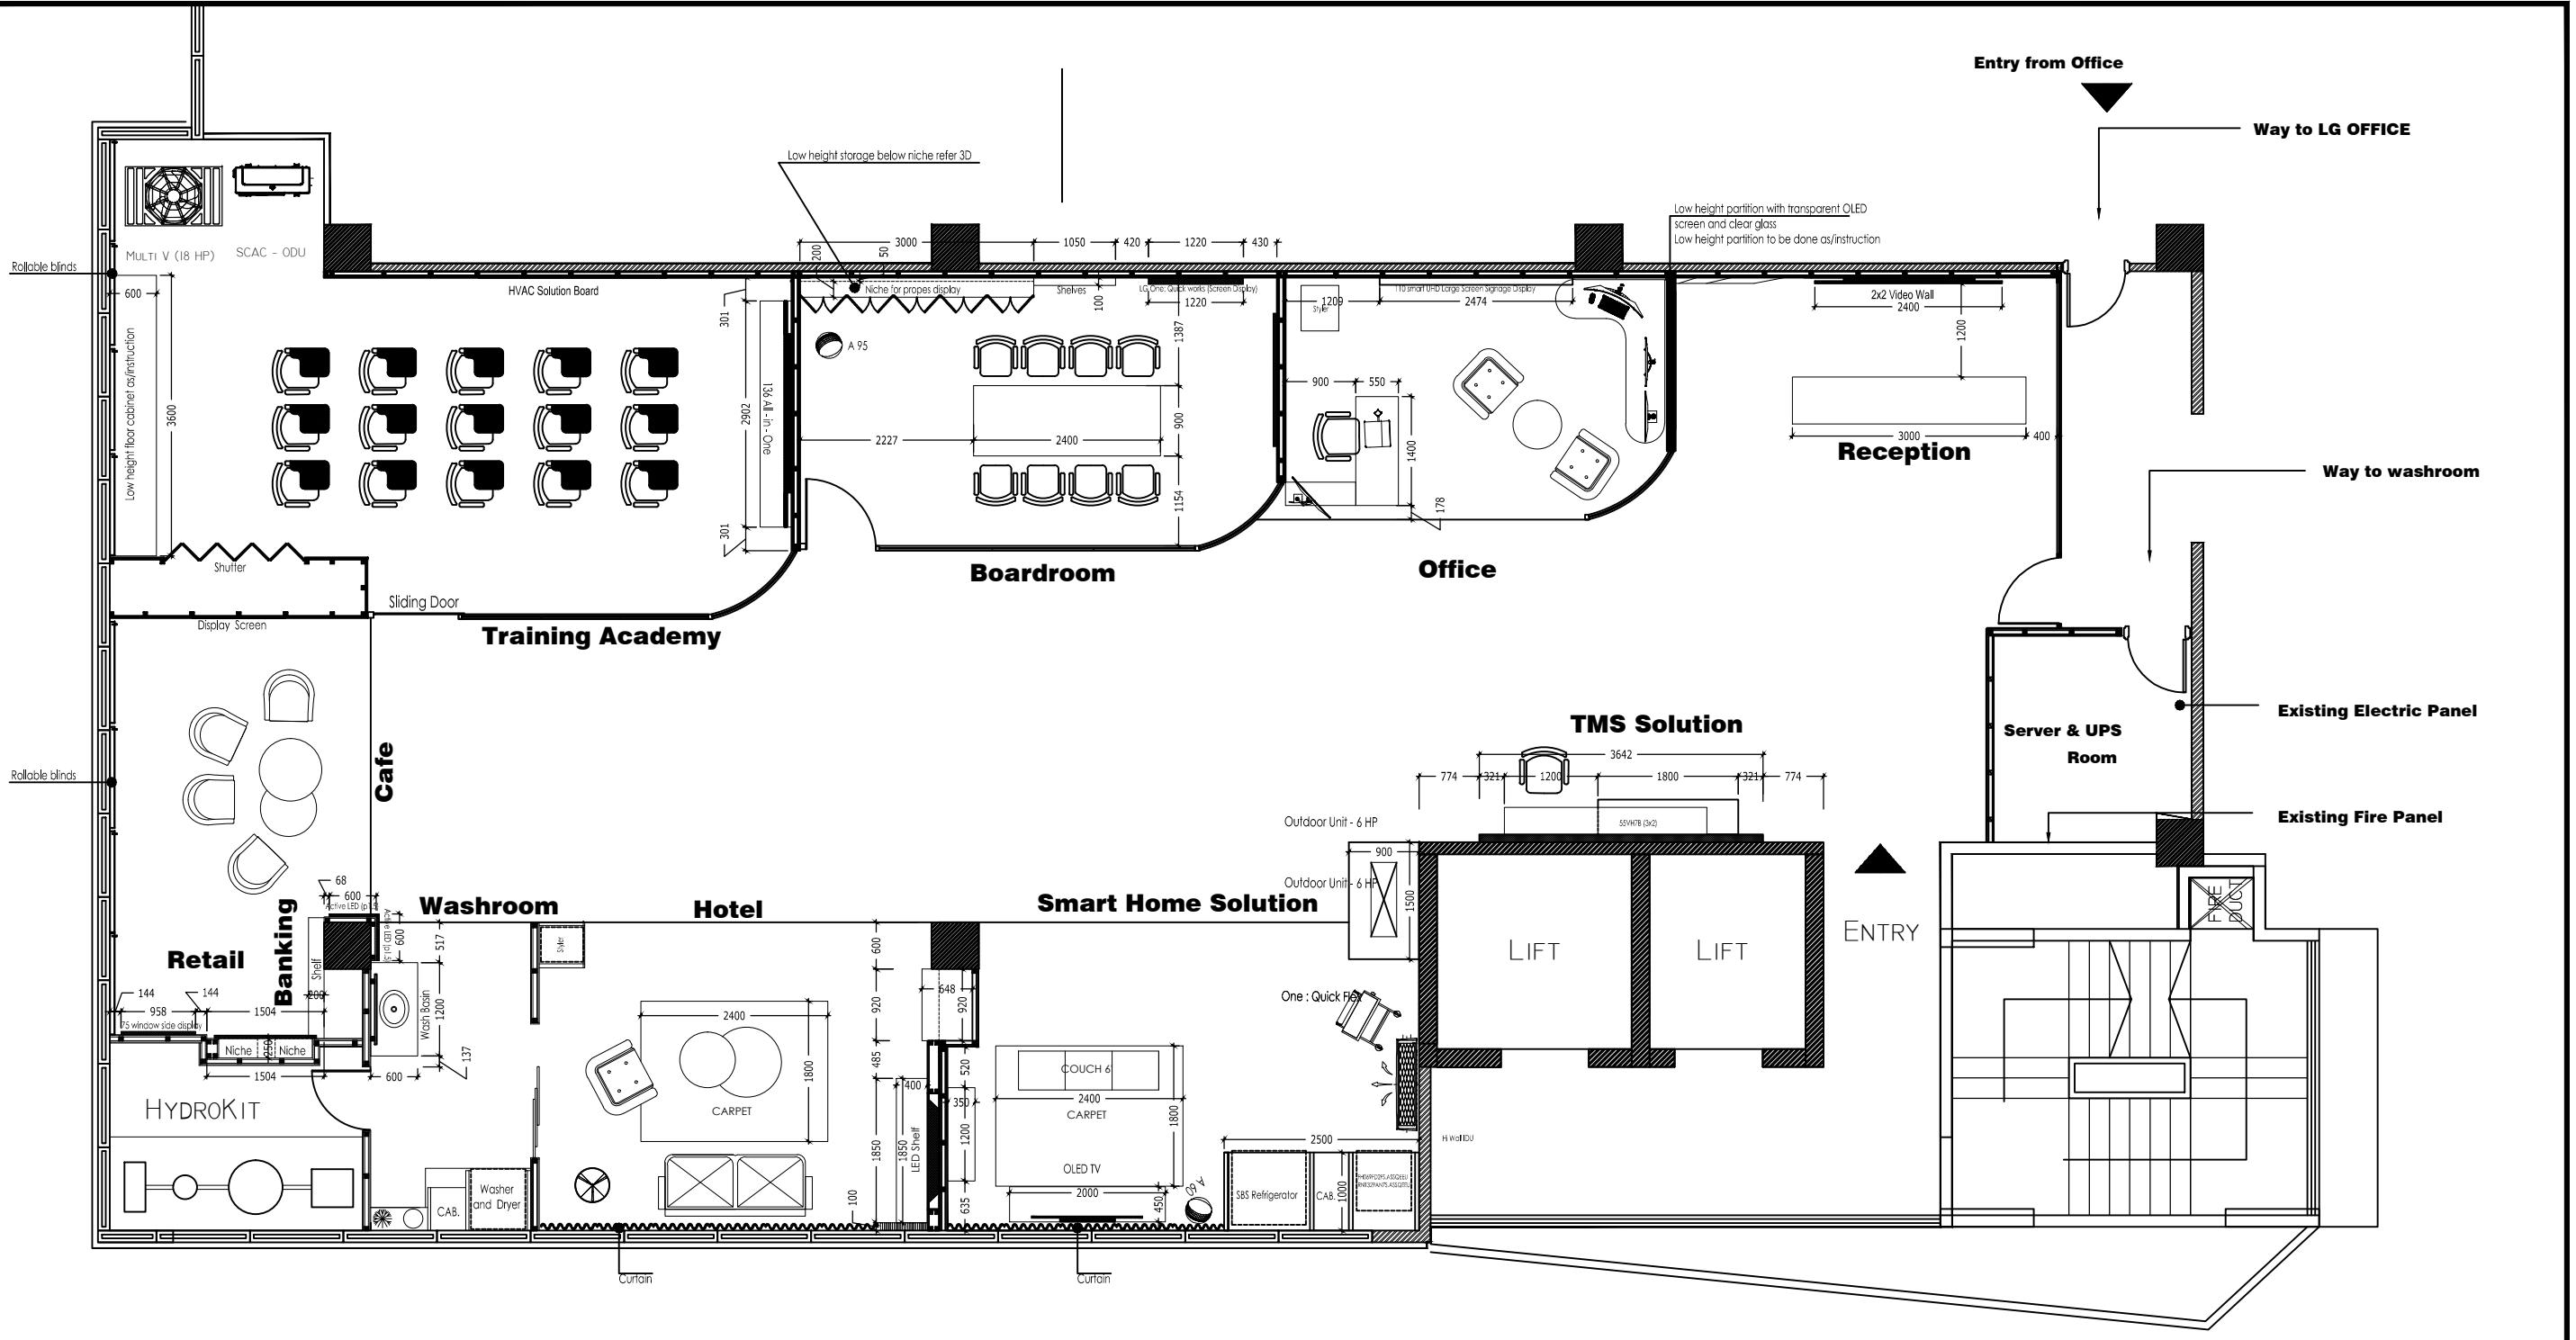


RAW FLOOR TO CEILING HEIGHT = 3170 MM
RAW FLOOR TO PILLAR BEAM BOTTOM = 3000 MM

TOTAL AREA - 2970 SQFT
SHOWROOM AREA - 2570 SQFT
TRAINING Room - 400 SQFT

STORE NAME:- LG INVATION GALLERY MUMBAI		GIIR Communications India Pvt. Ltd. KP Towers, Tower D, 12th Floor, Plot No. C-001B, Sector-16B, Noida, Uttar Pradesh-201301. 
		Drawing Title:- FLOOR LAYOUT PLAN
		Date:- 28.10.2022
		Sheet No:-
		Drawn By:-
		Scale:-

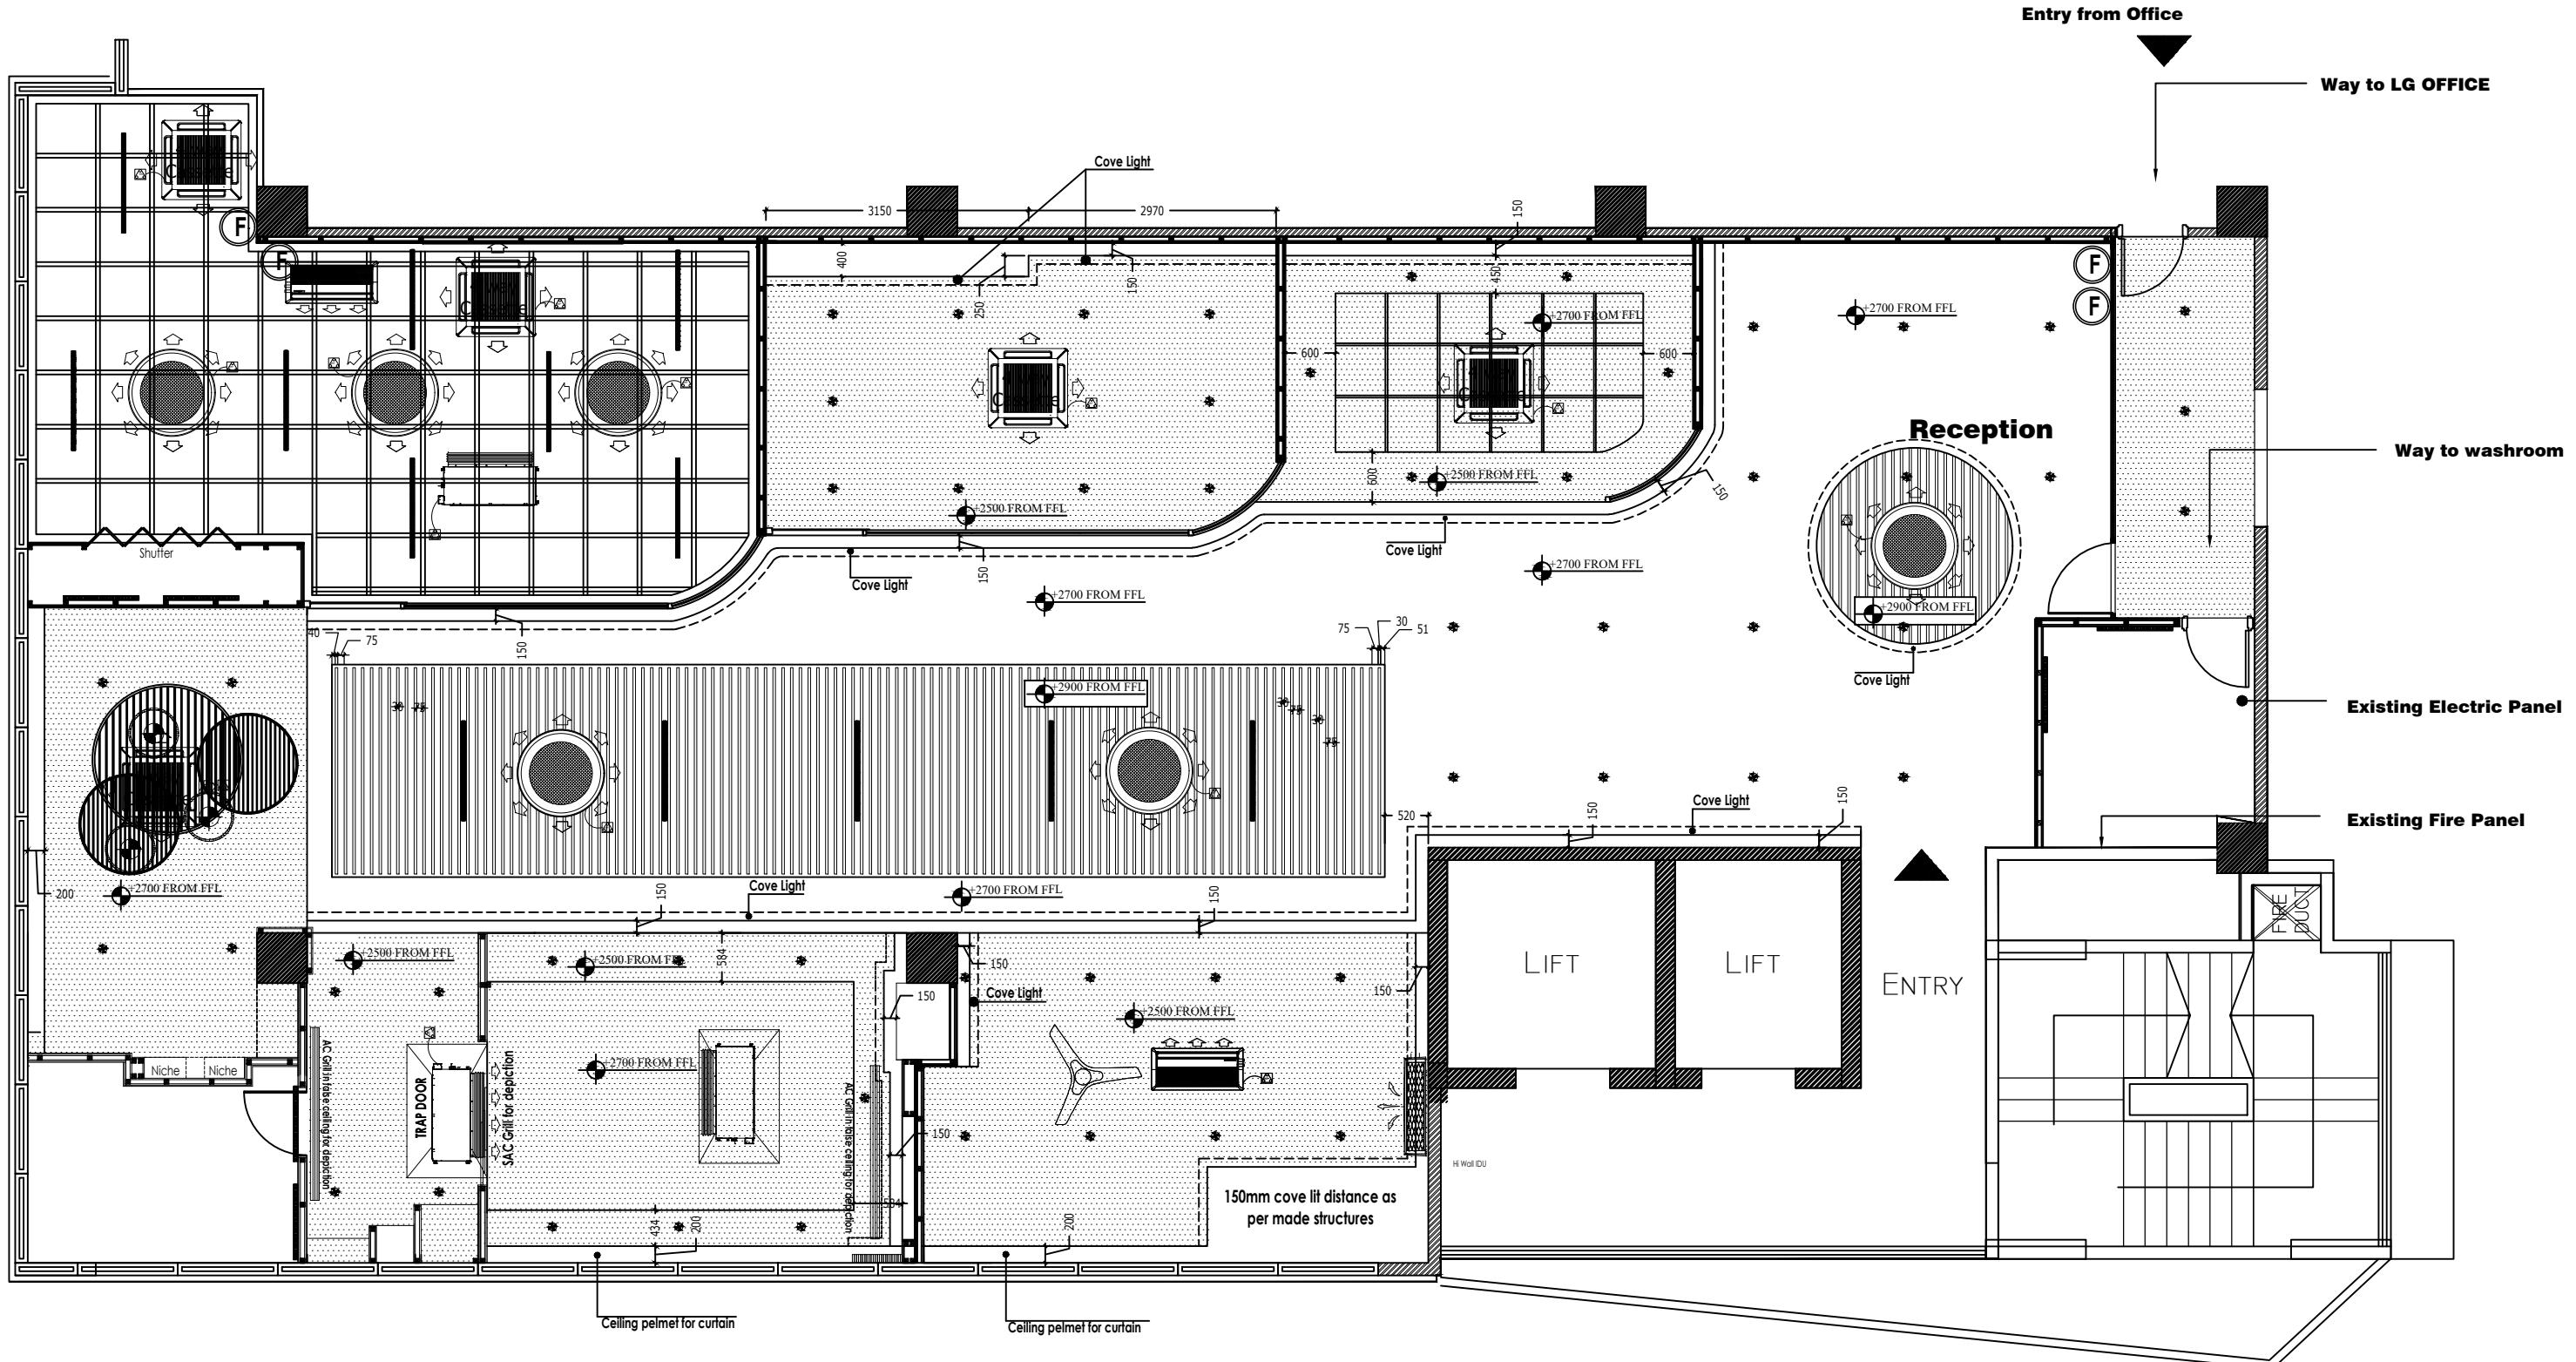


CEILING PLAN

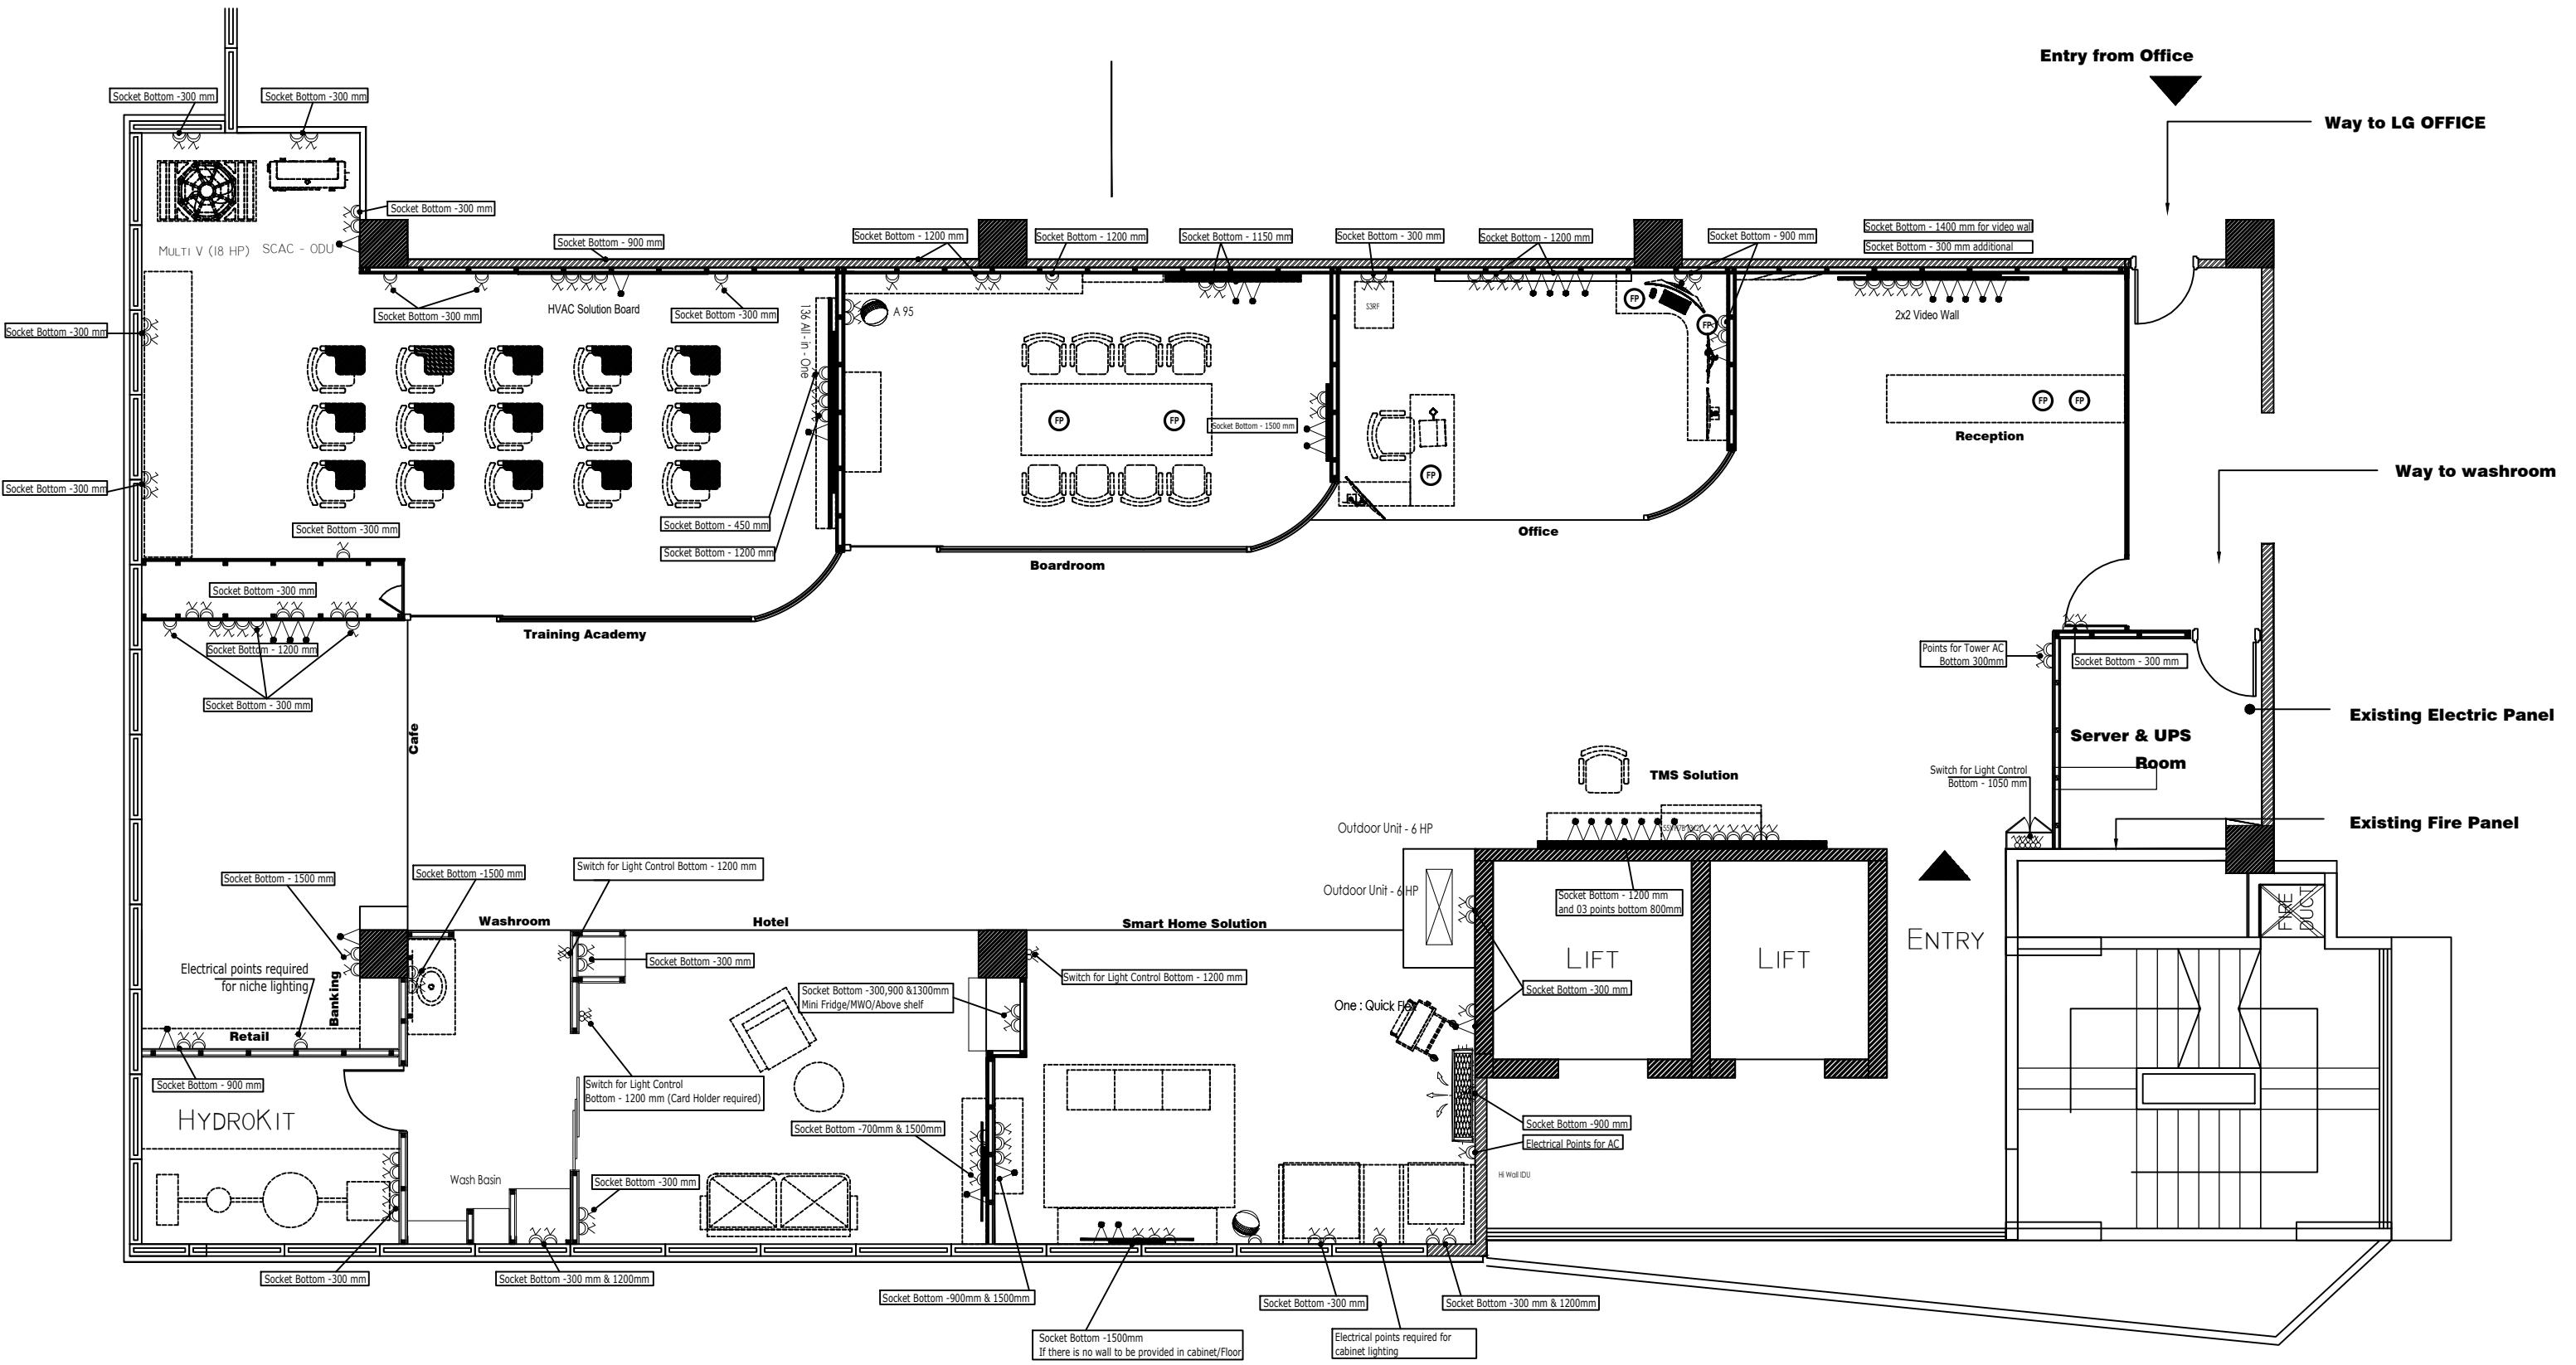


LEGEND	Qty.	Brand/Model No.
	122	Philips / Wipro / Havells
	34	Philips / Wipro / Havells
	07	Philips / Wipro / Havells

ELECTRICAL LAYOUT PLAN

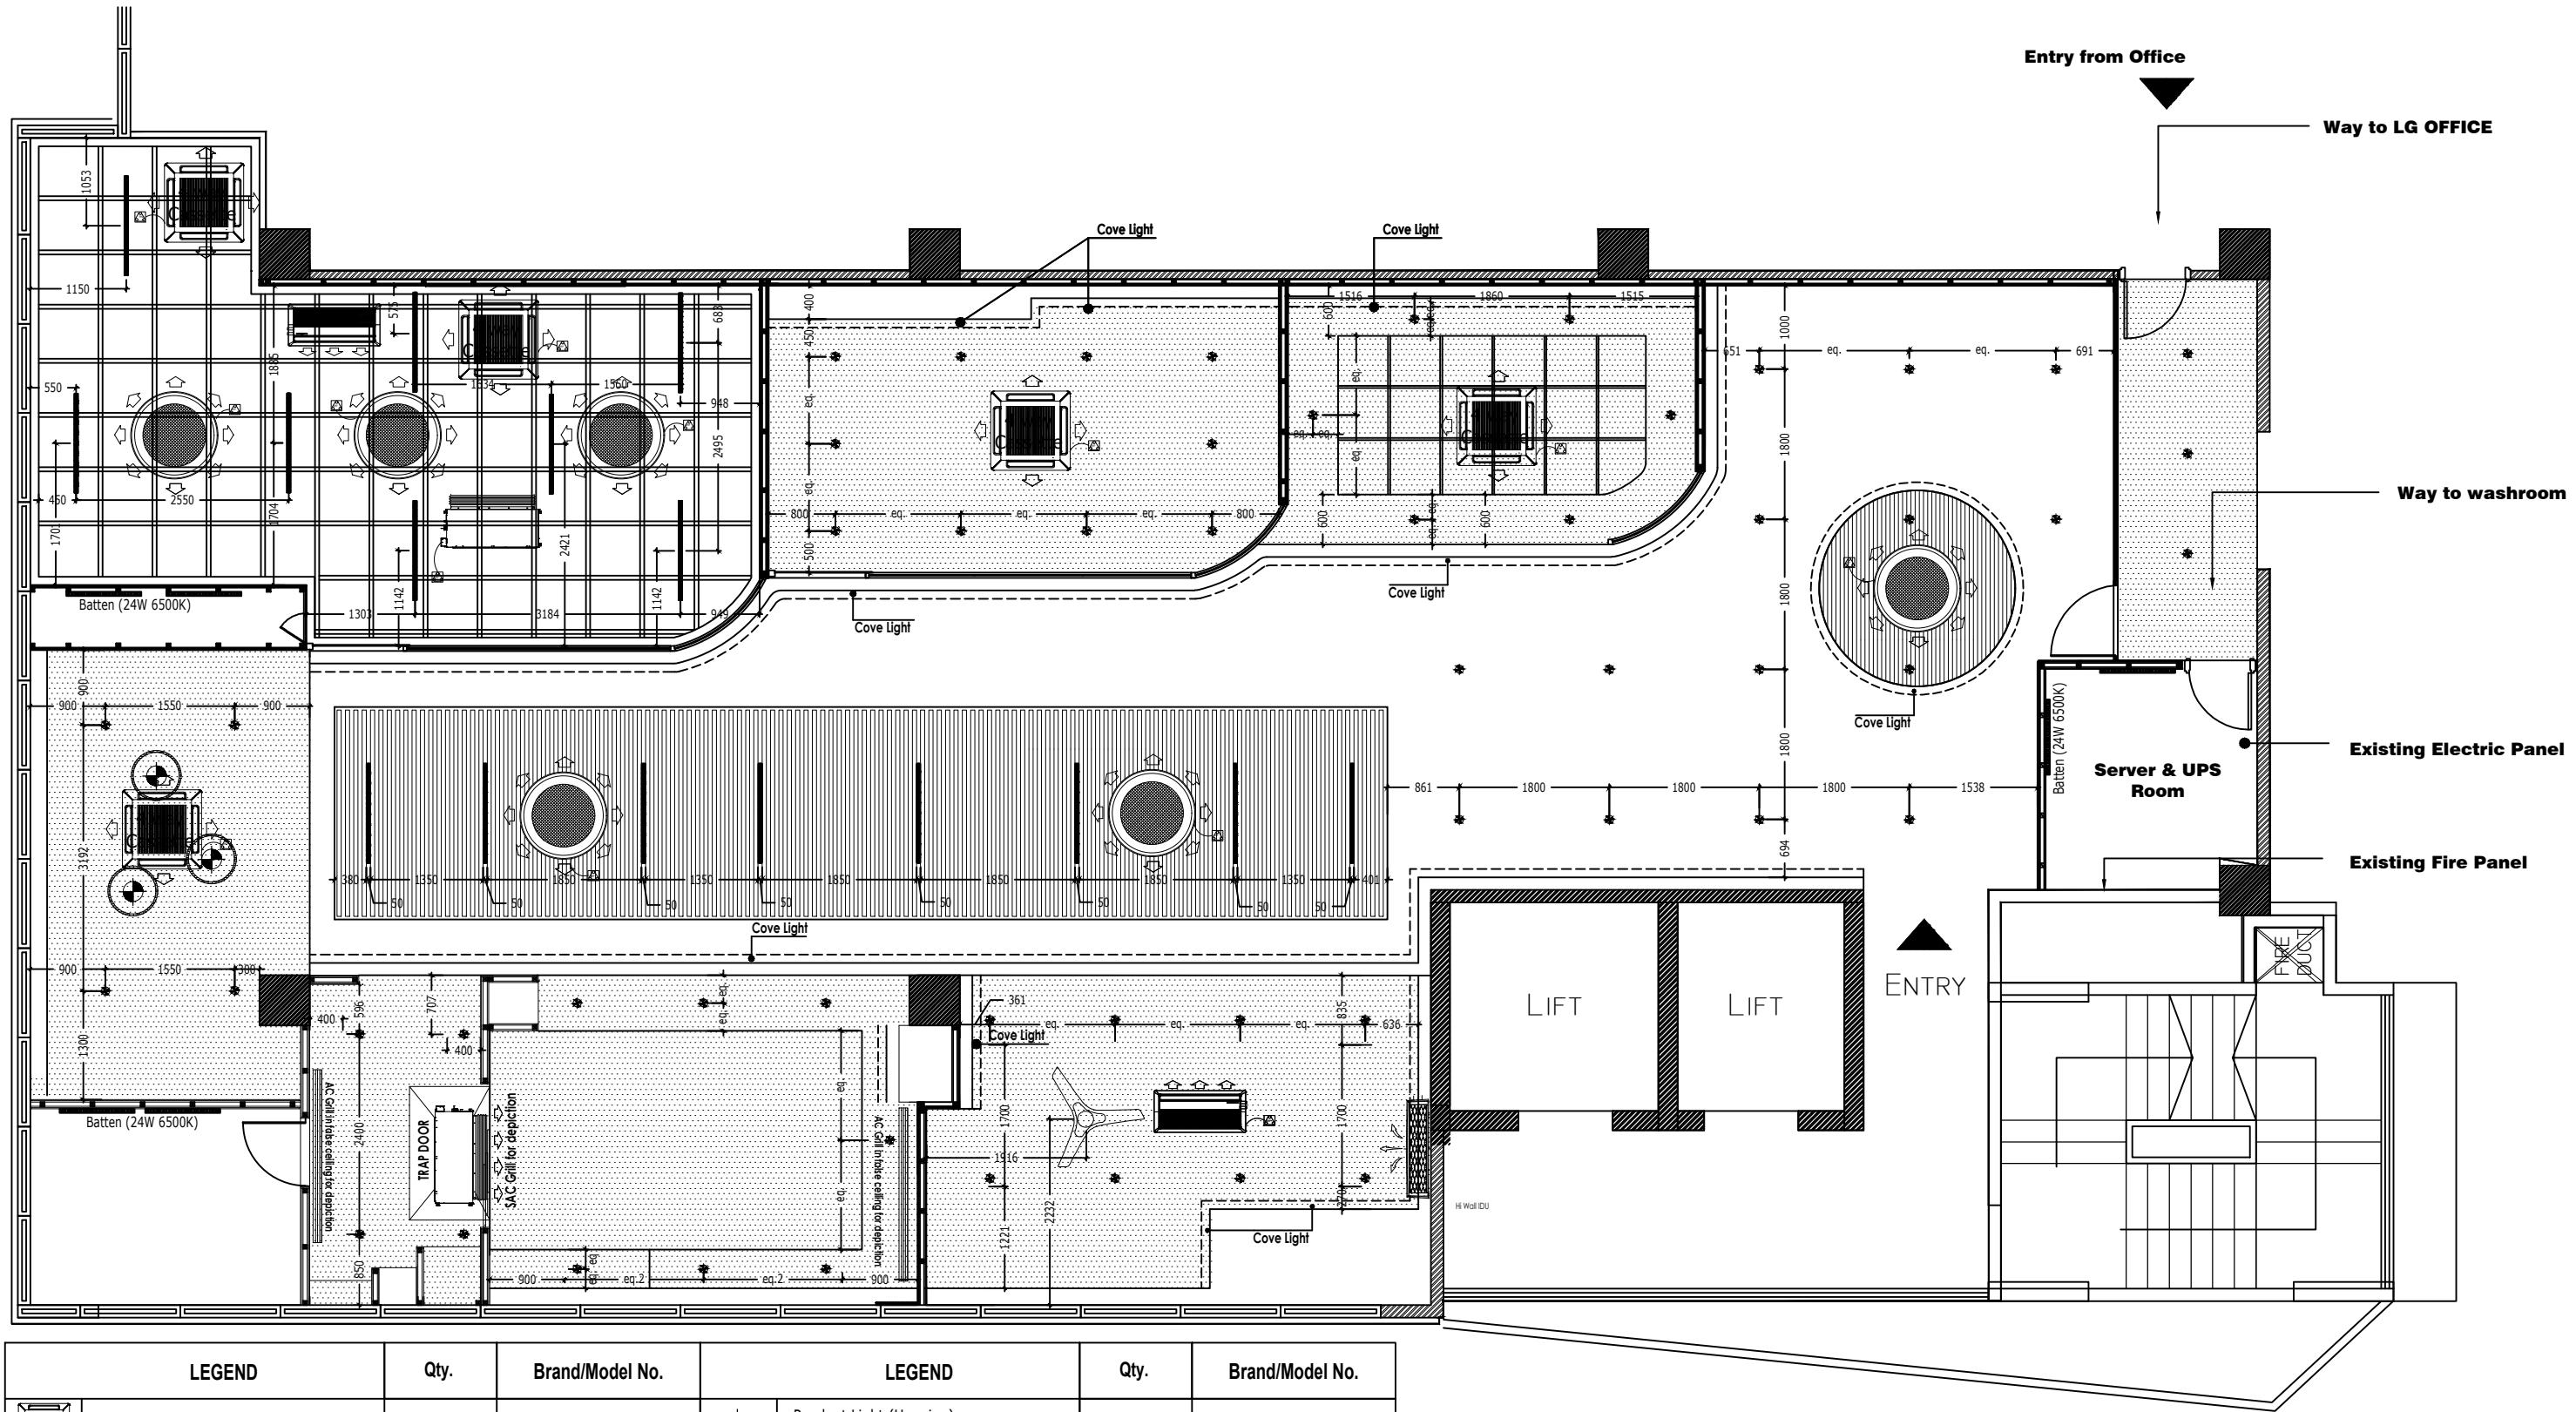








LEGEND		Qty.	Brand/Model No.	LEGEND		Qty.	Brand/Model No.
	4 Way Cassette	05	JRNU36GTNA4		Pendant Light (Hanging)	03	Philips / Wipro / Havells
	Round Cassette	06	ARNU36GTYA4		Linear LED Light (28W 6500K)	16	Philips / Wipro / Havells
	1 Way Cassette	01	ARNU24GTTB4		Batten (24W 6500K)	06	Philips / Wipro / Havells
	PLUG AND SOCKET	13			Live Ceiling Fan	01	
	Down Light (9/12W 4000K)	56	Philips / Wipro / Havells				

CEILING LIGHTING PLAN



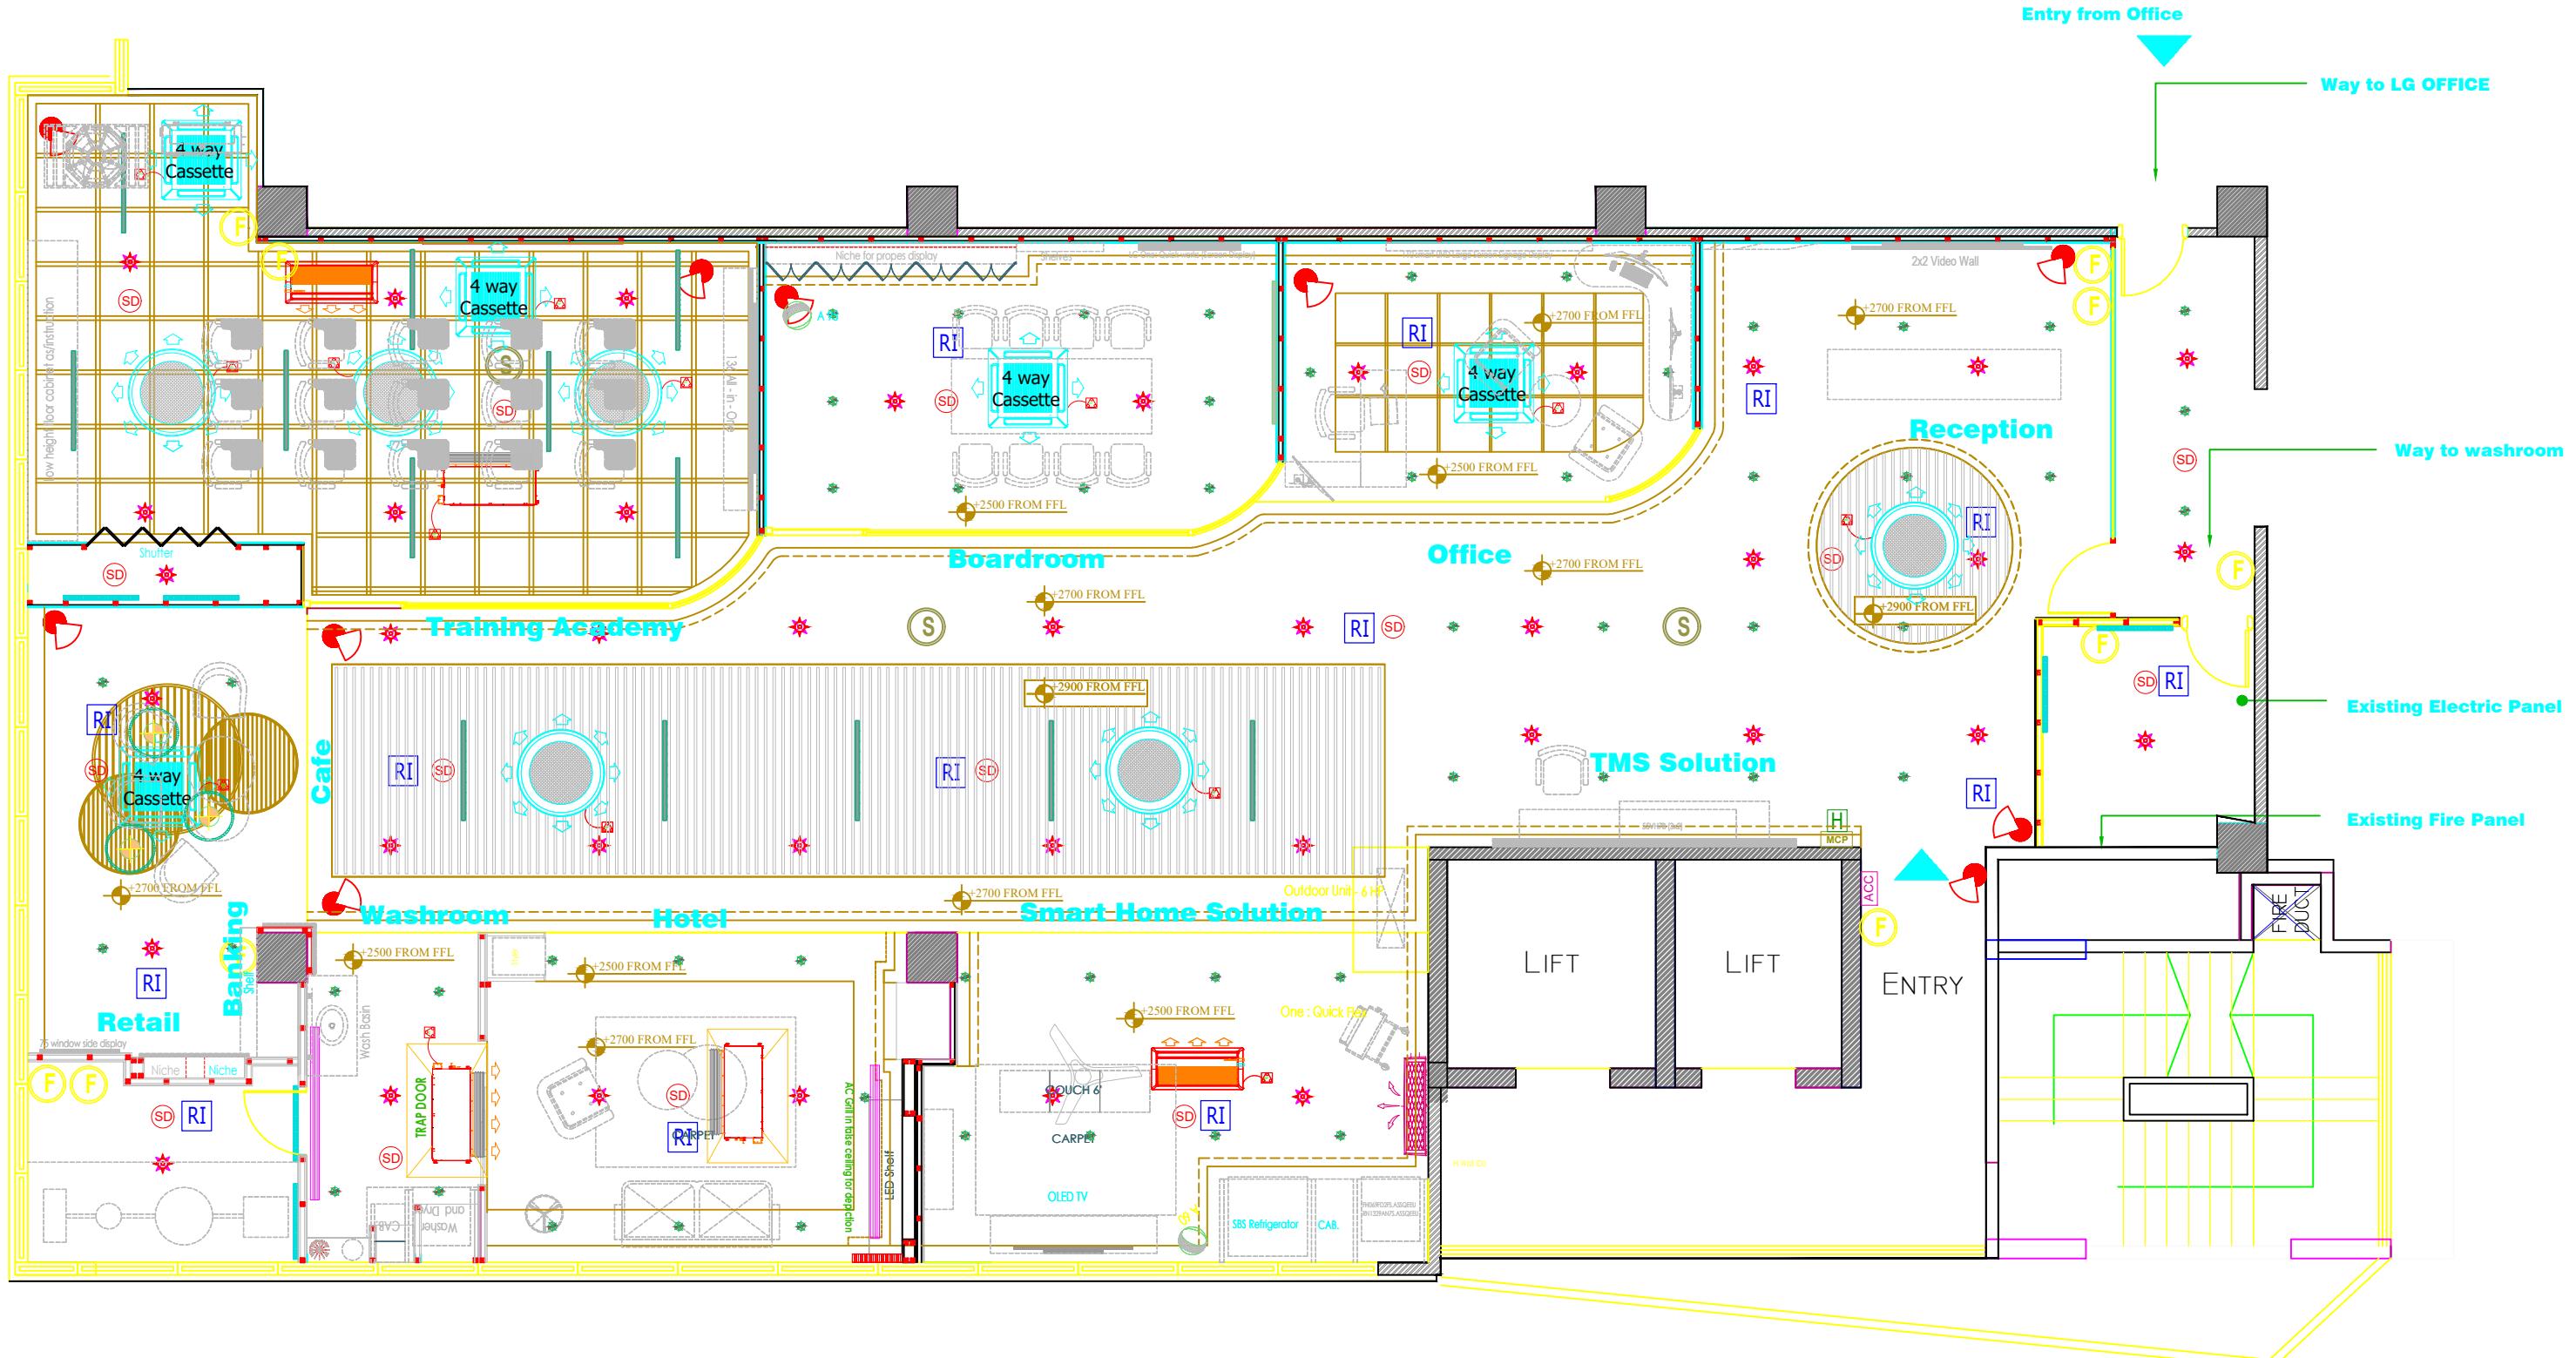


REFLECTED CEILING PLAN

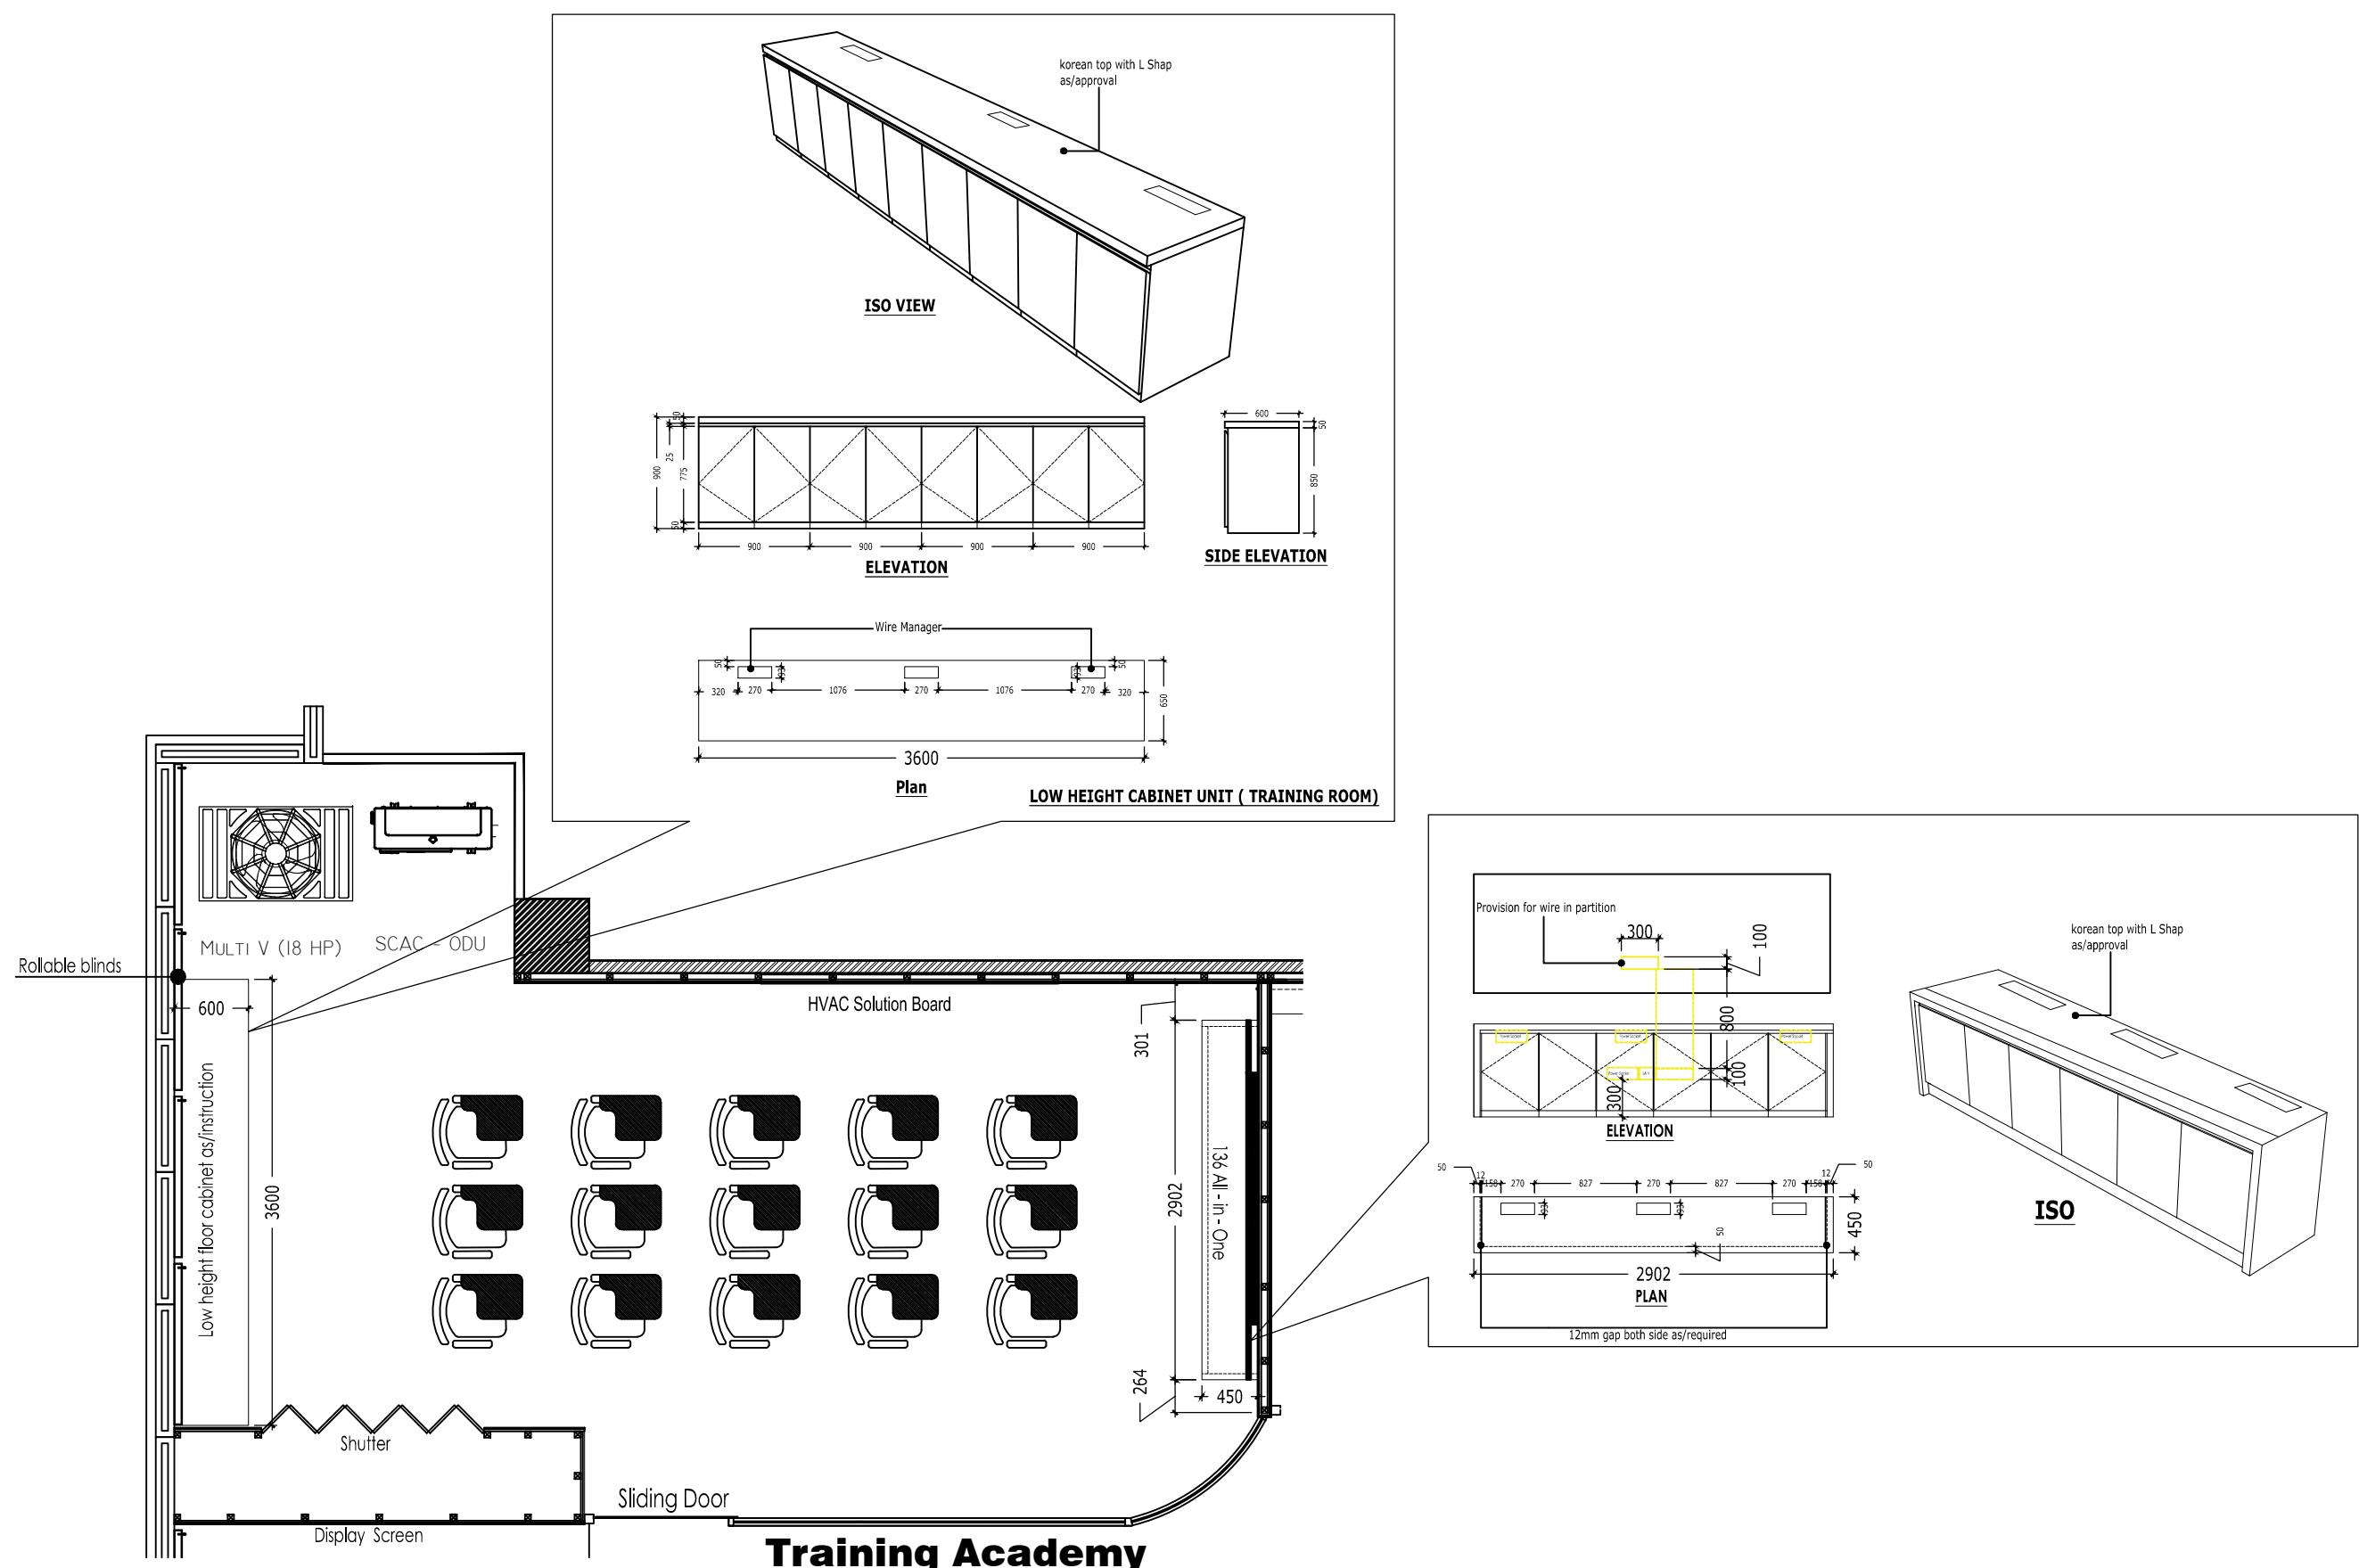


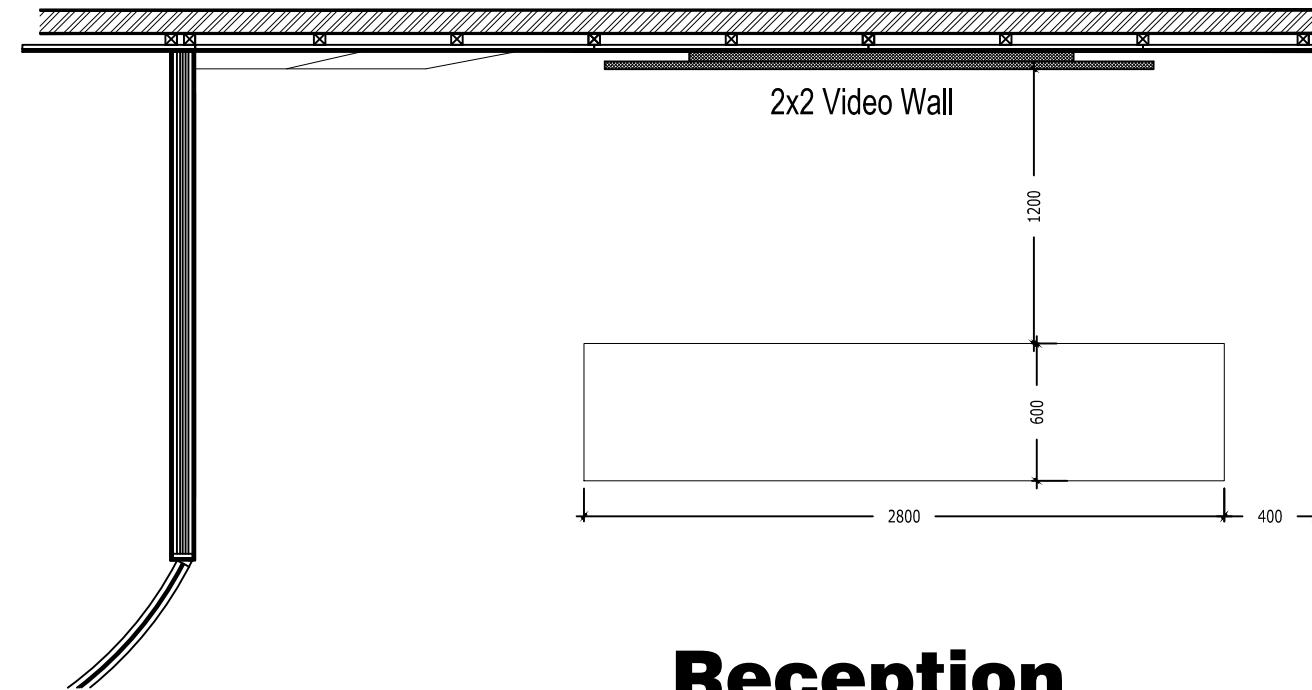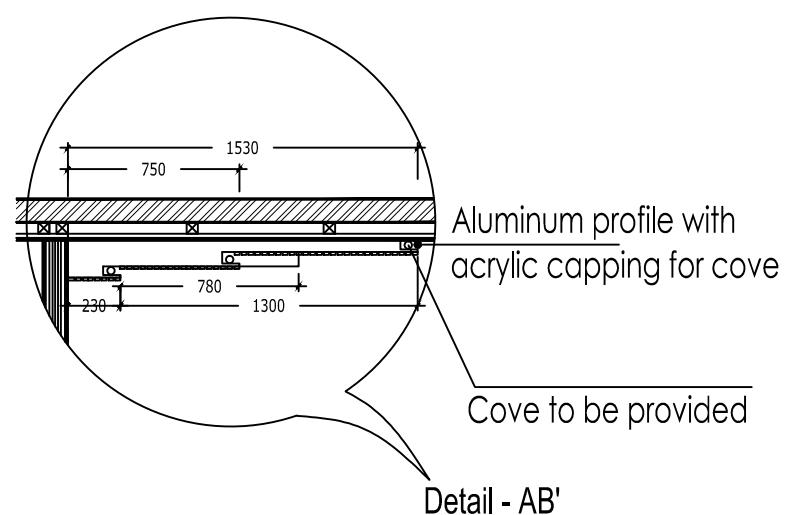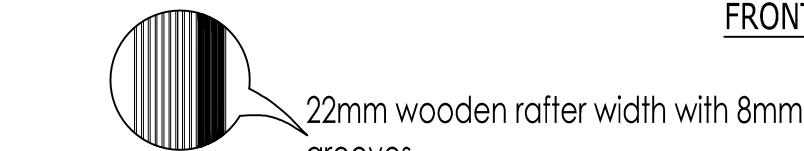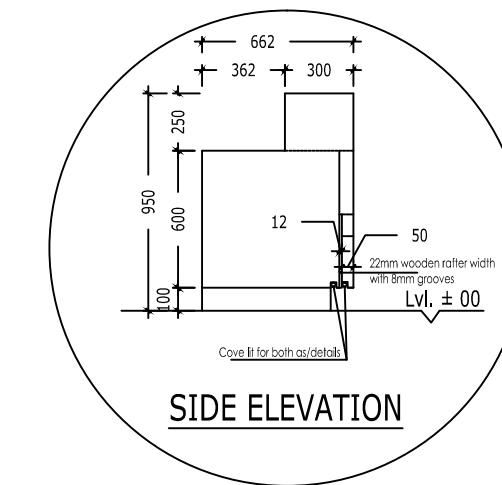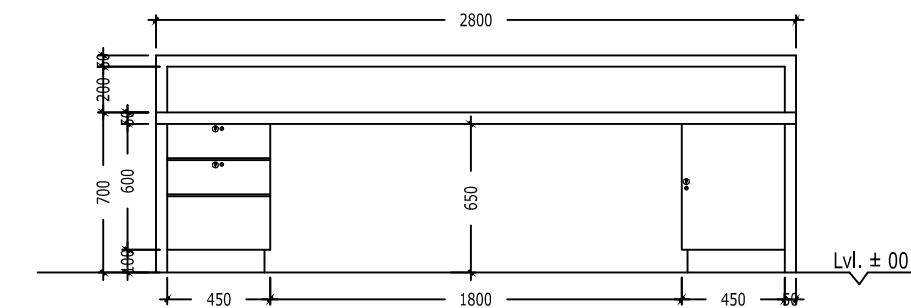
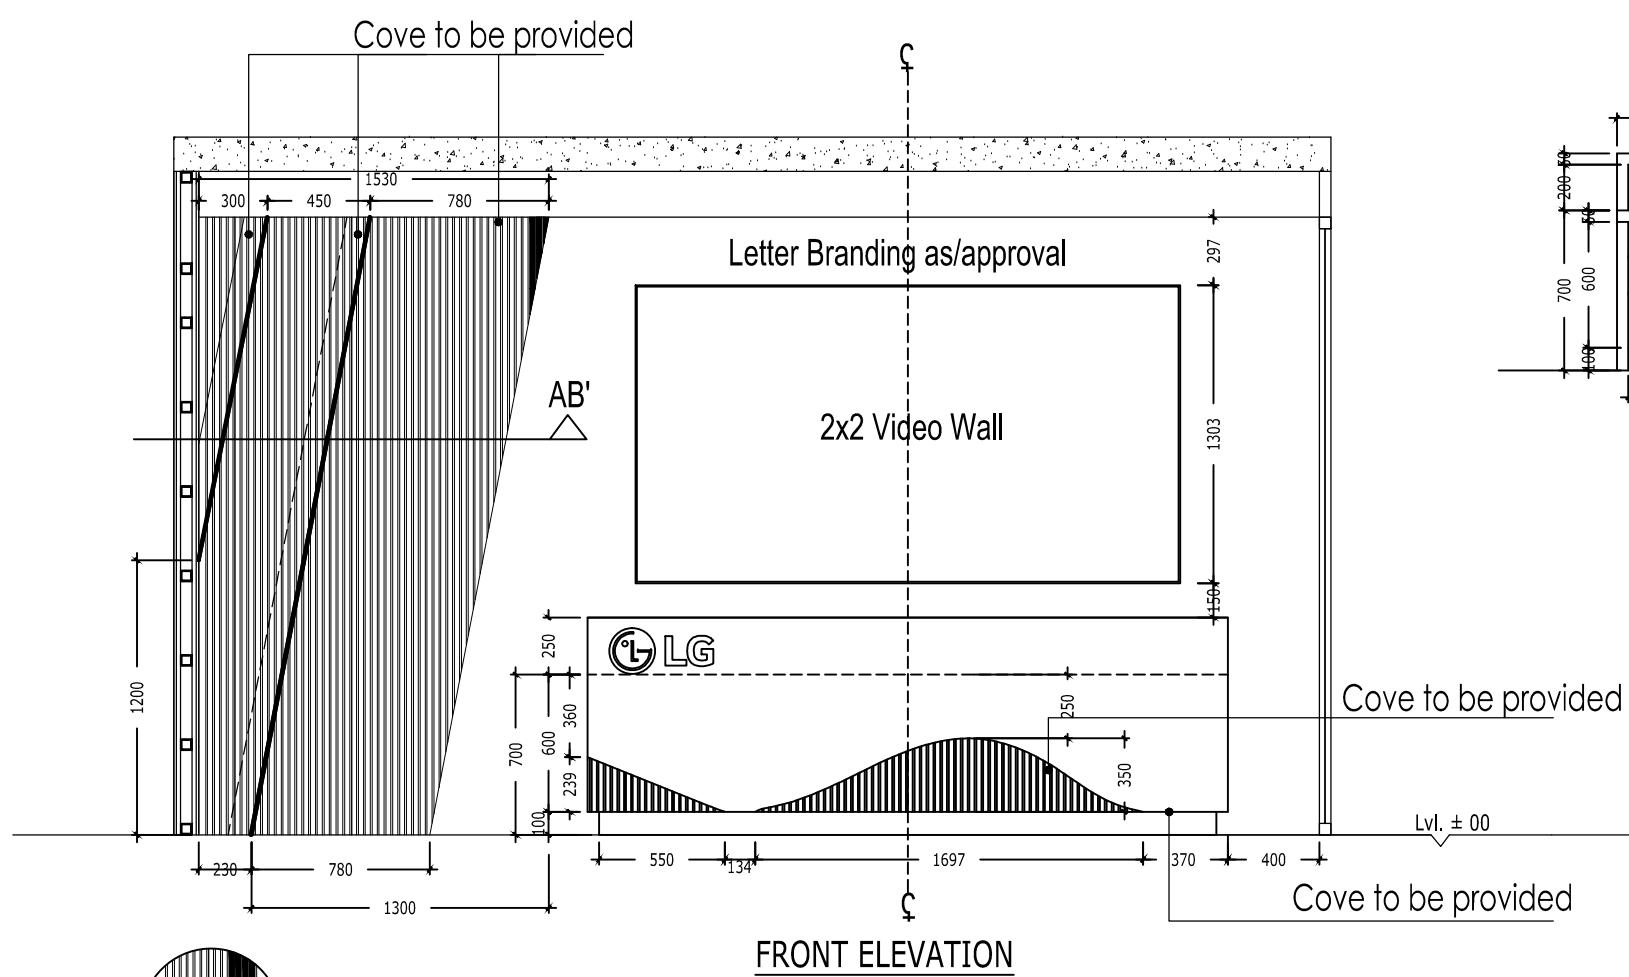



Reception

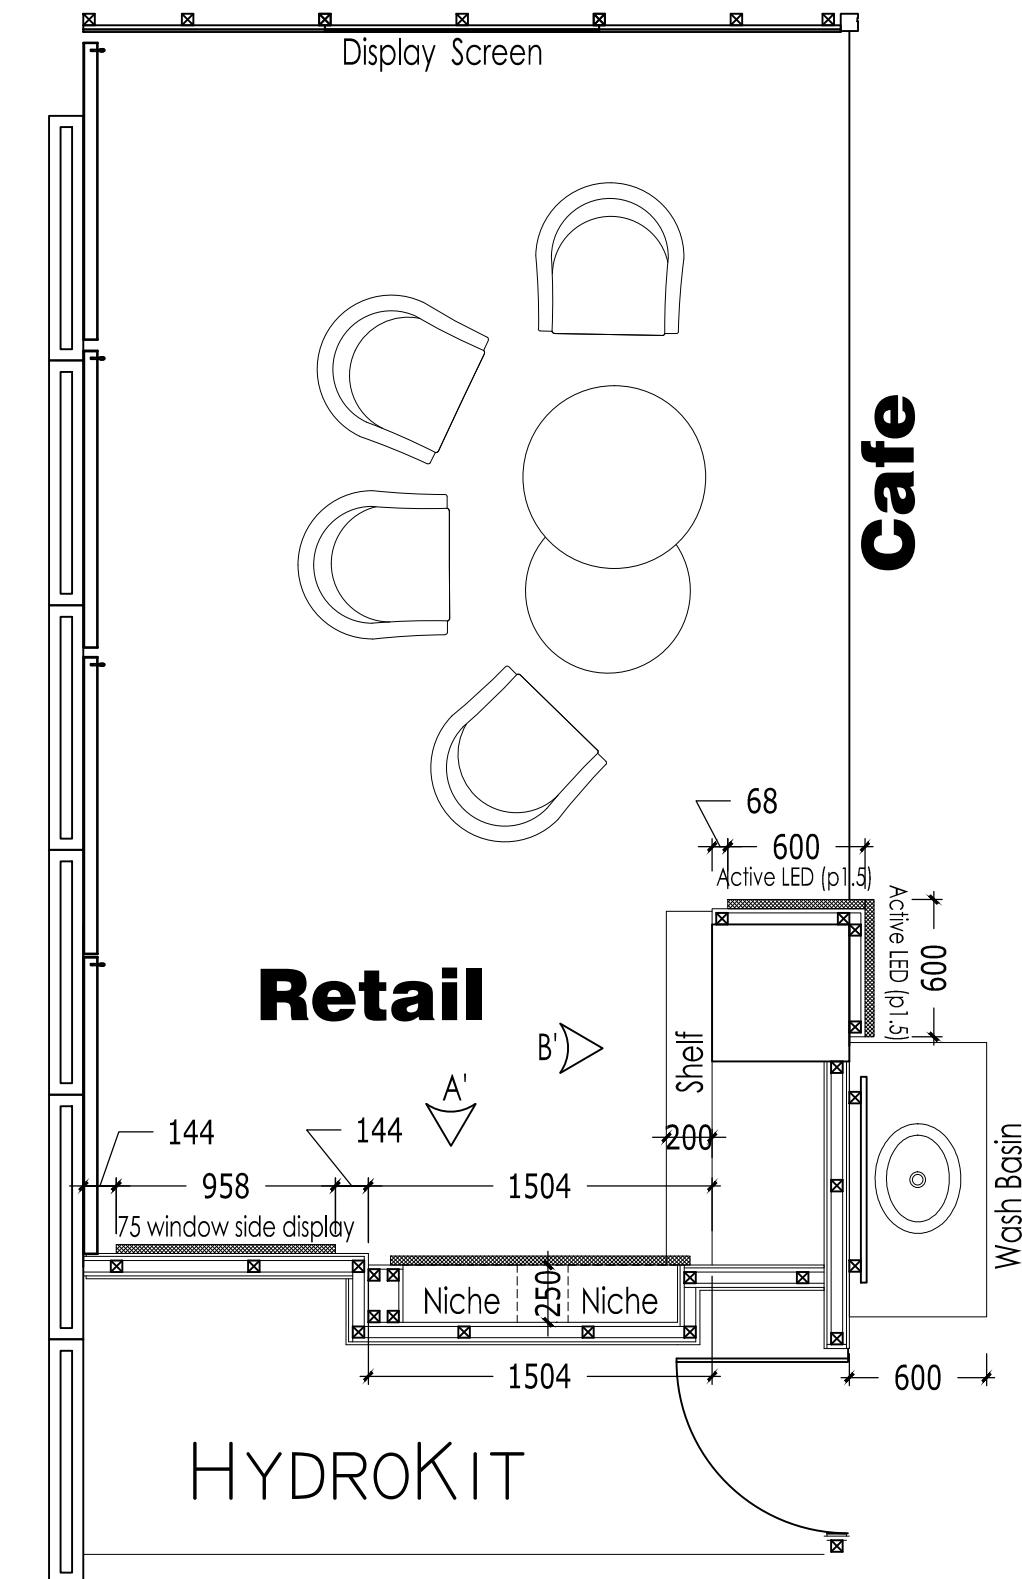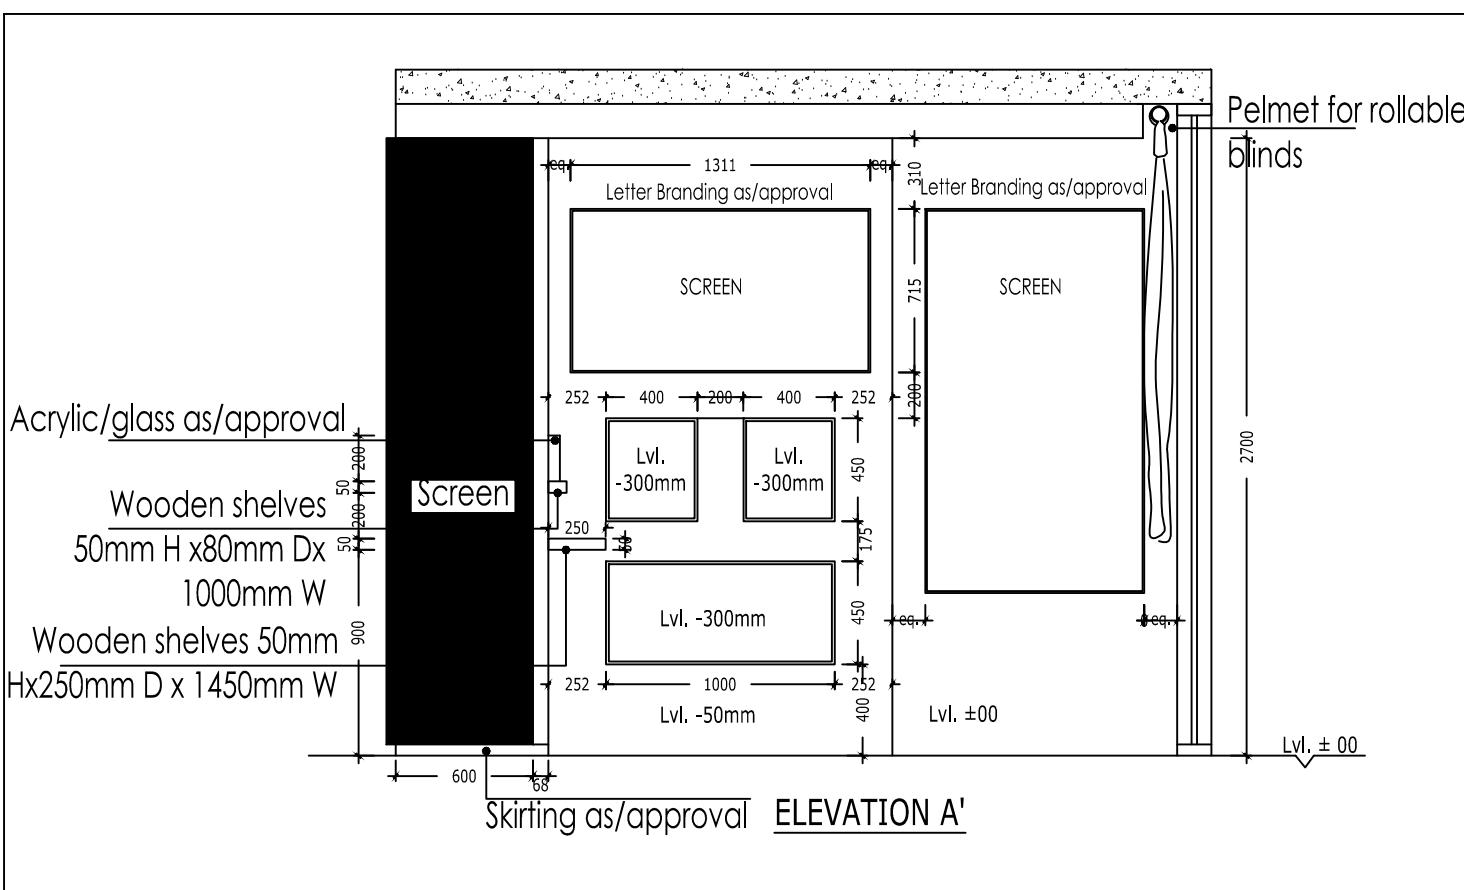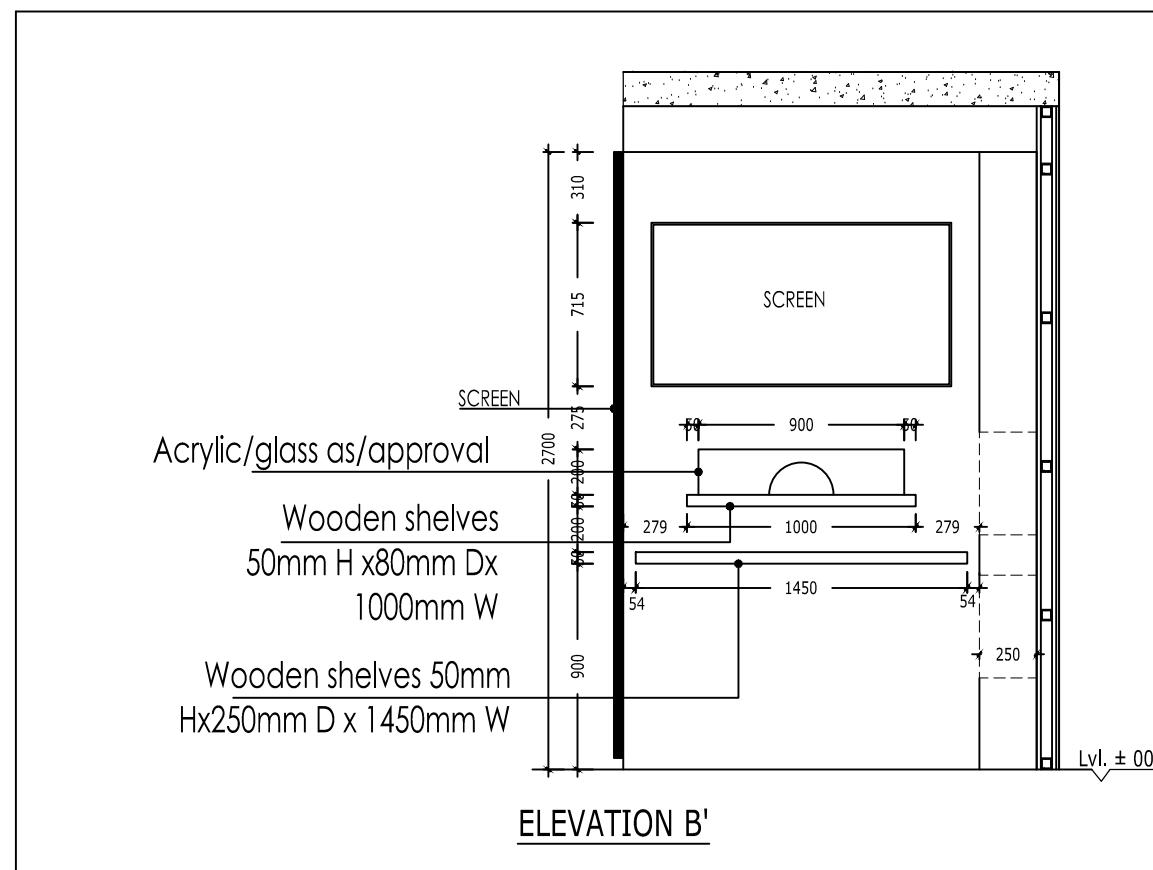


Smart Home Solution

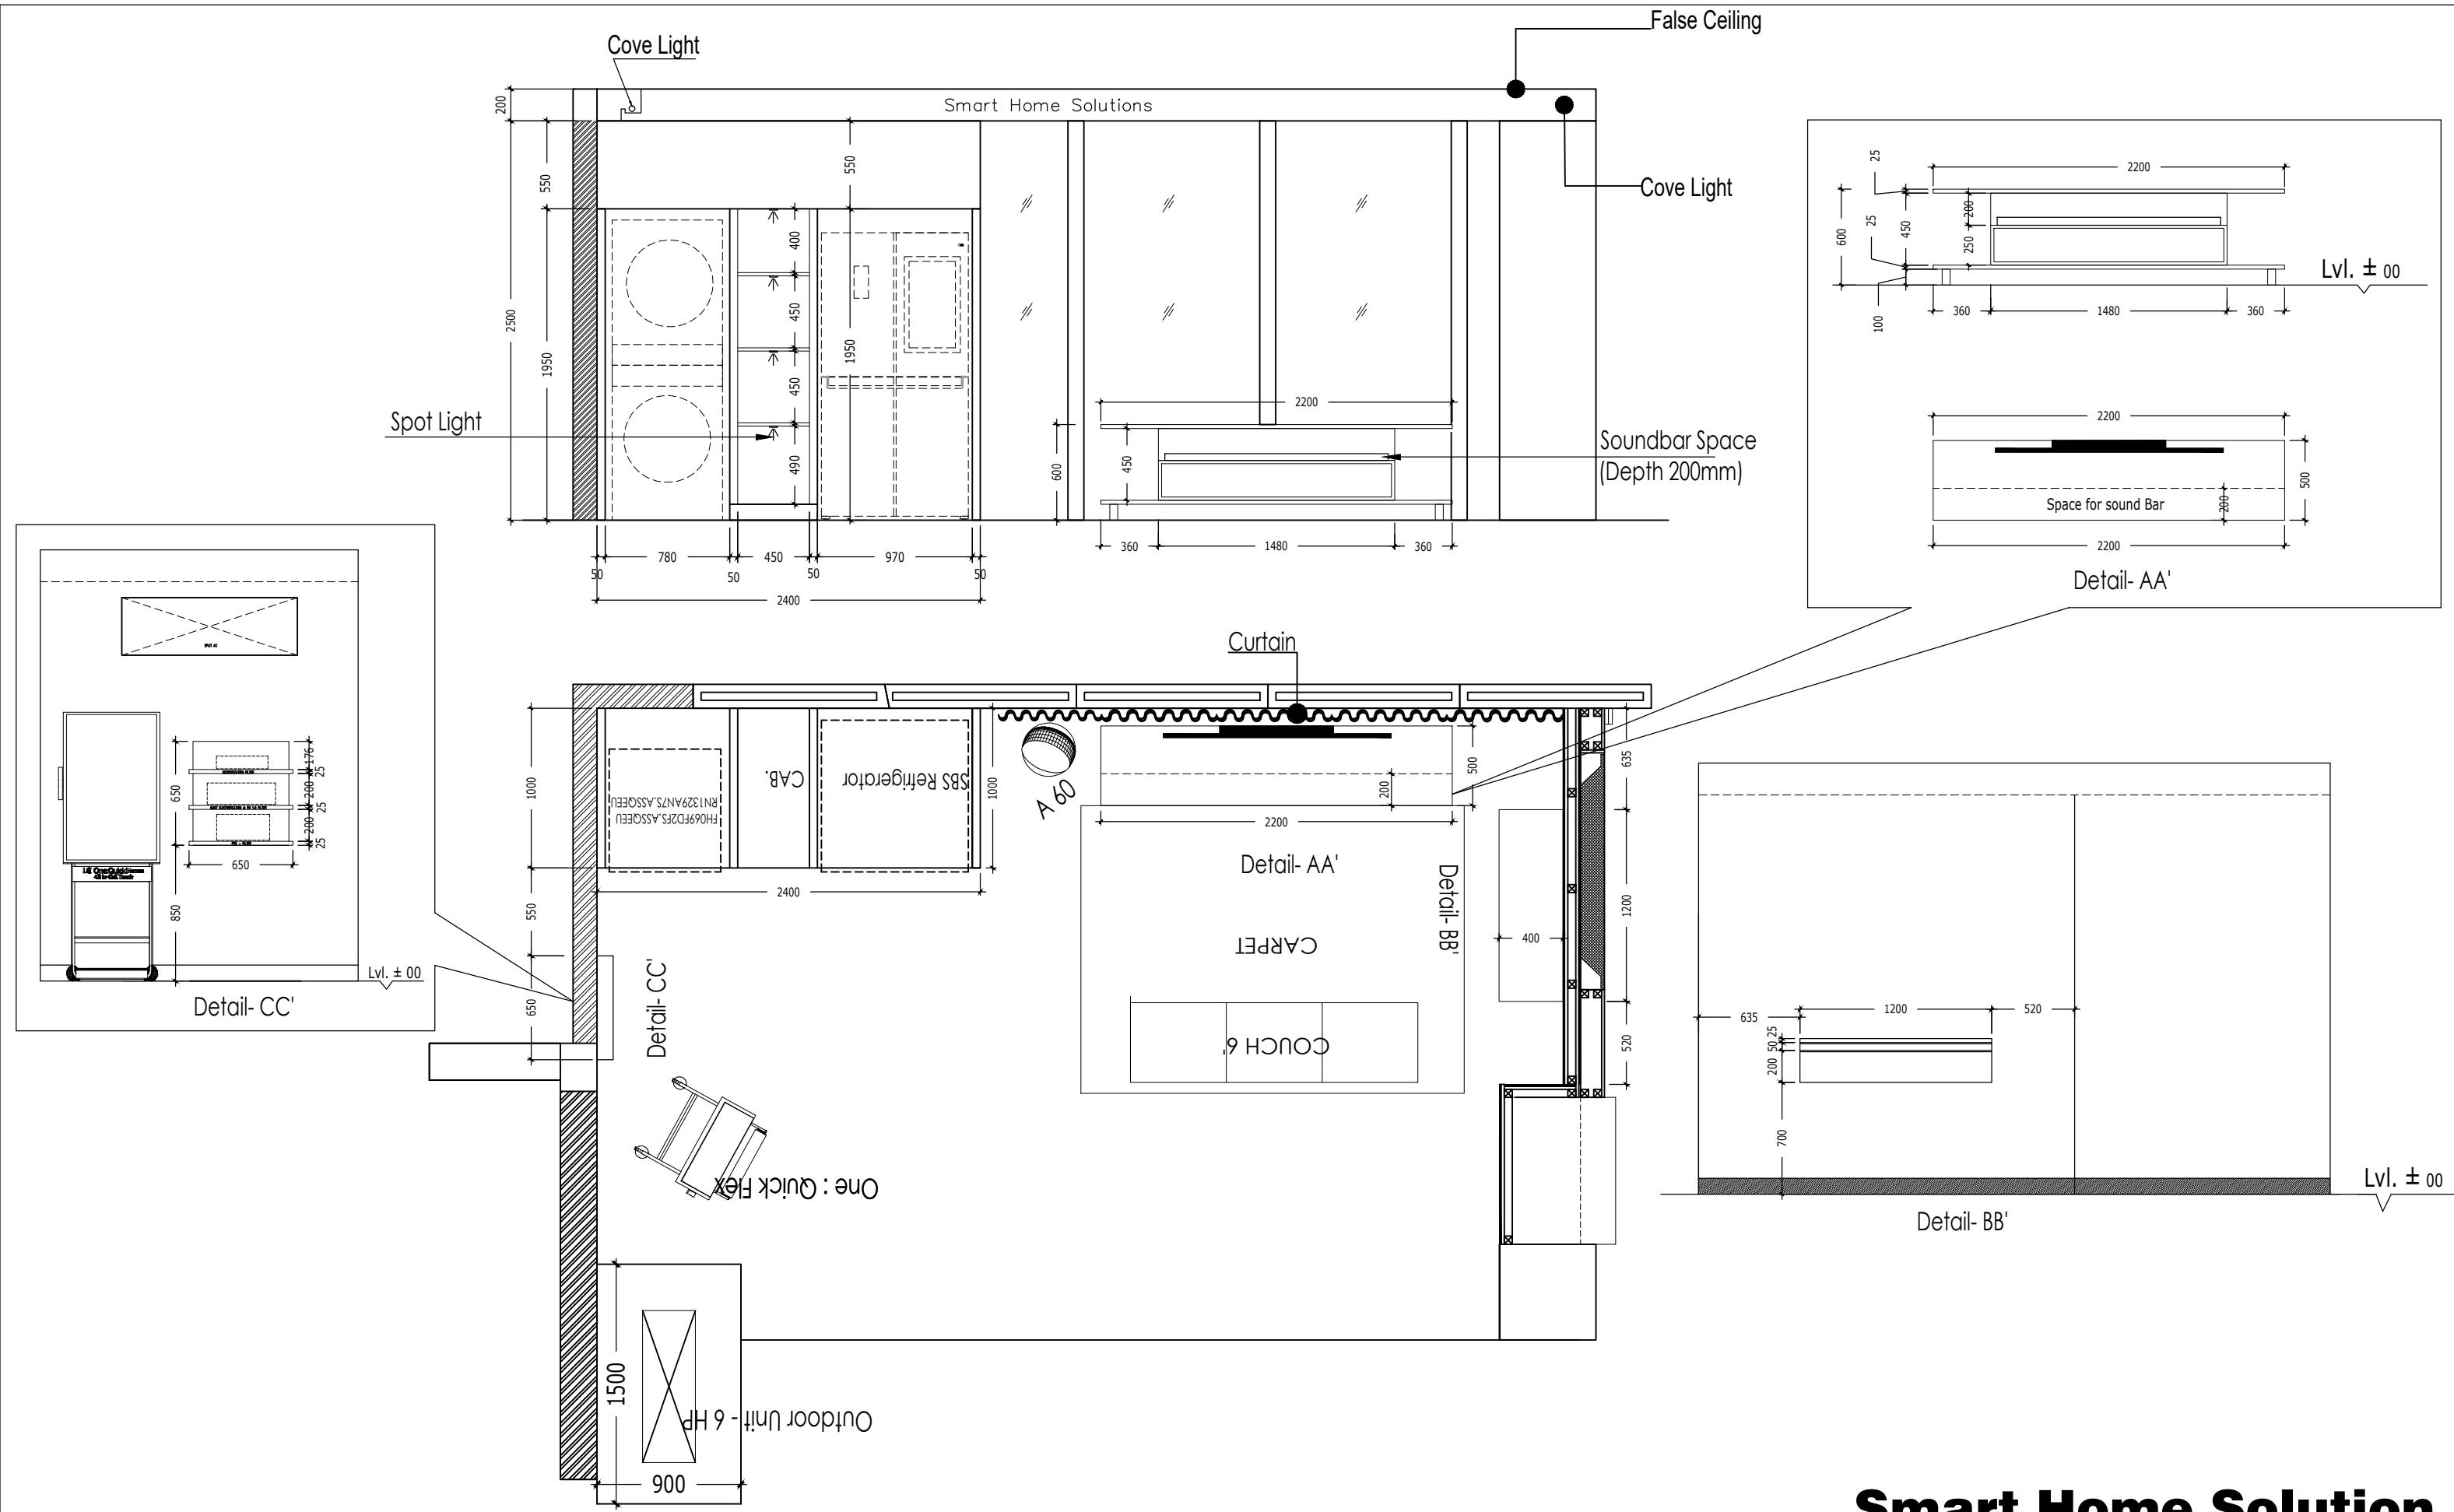

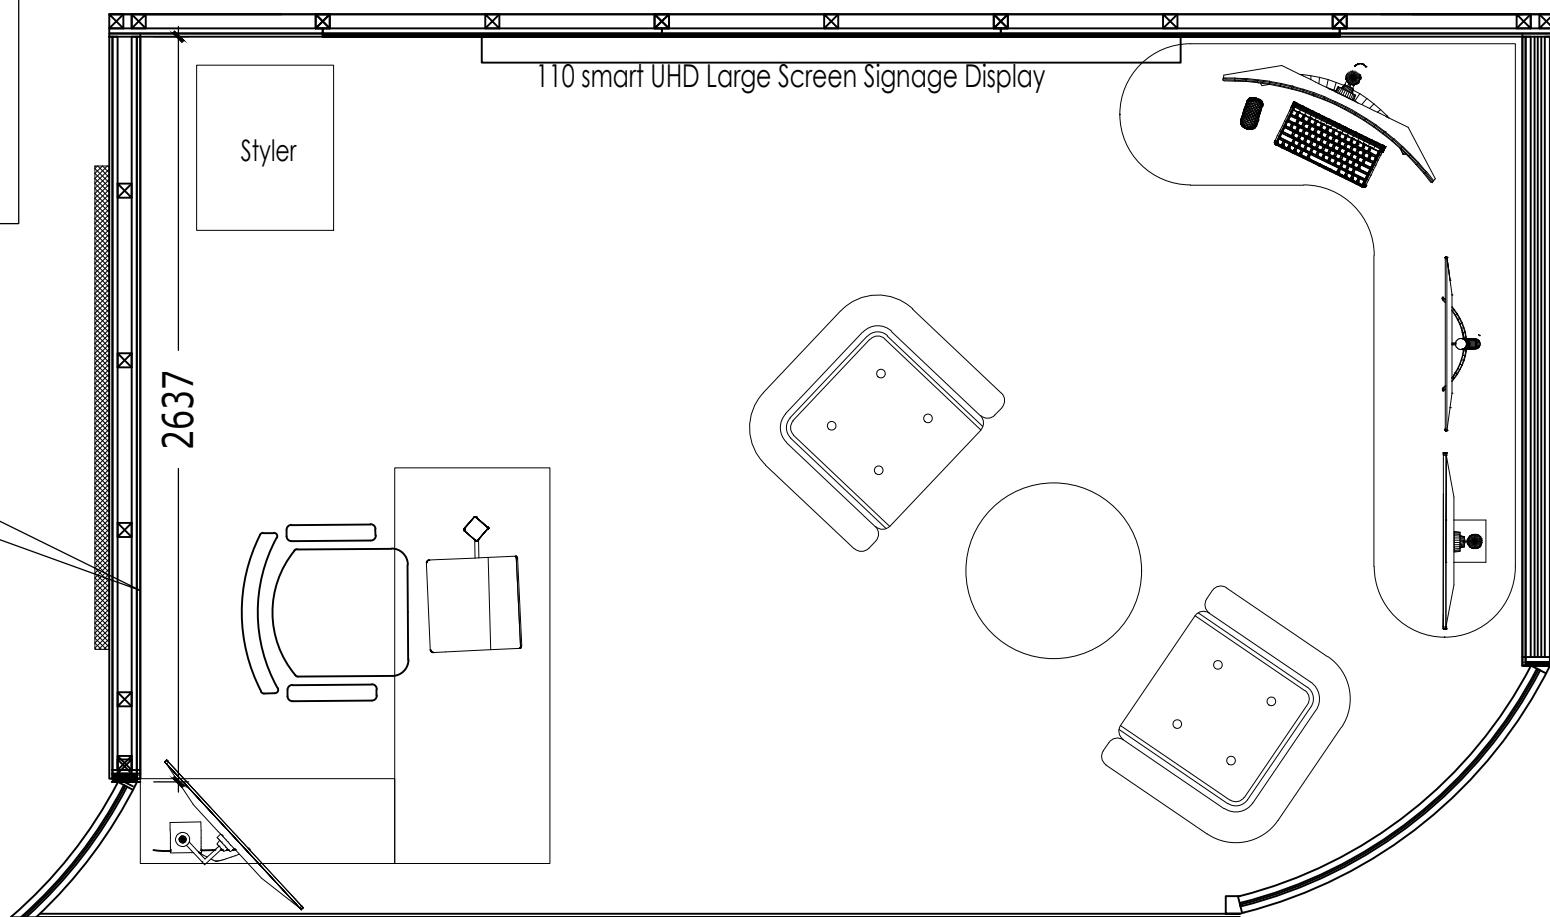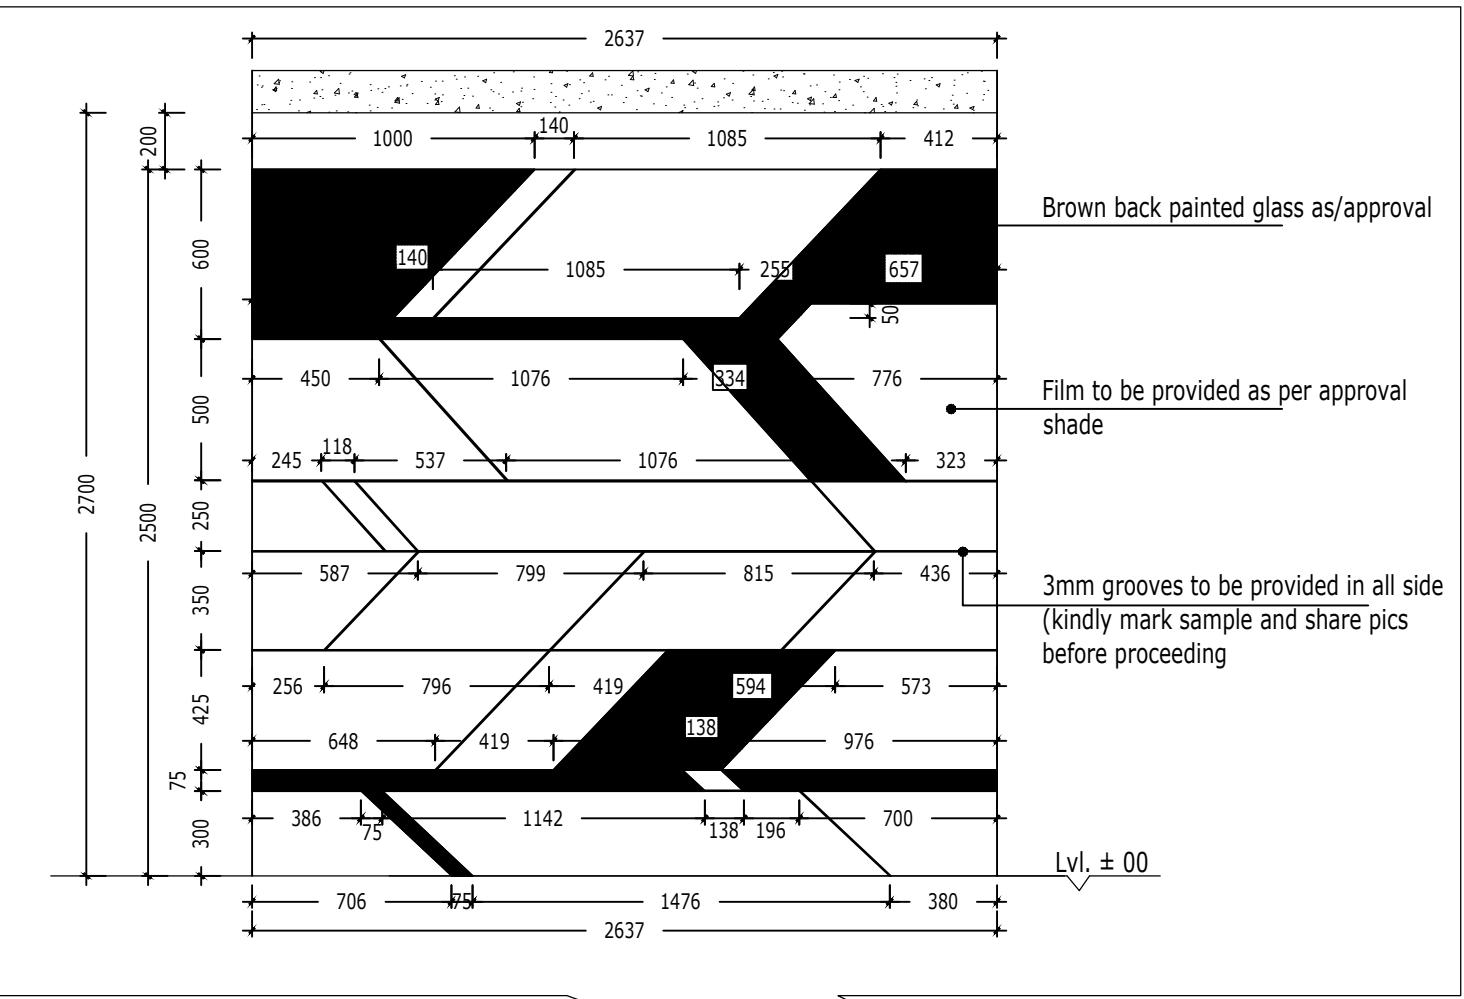

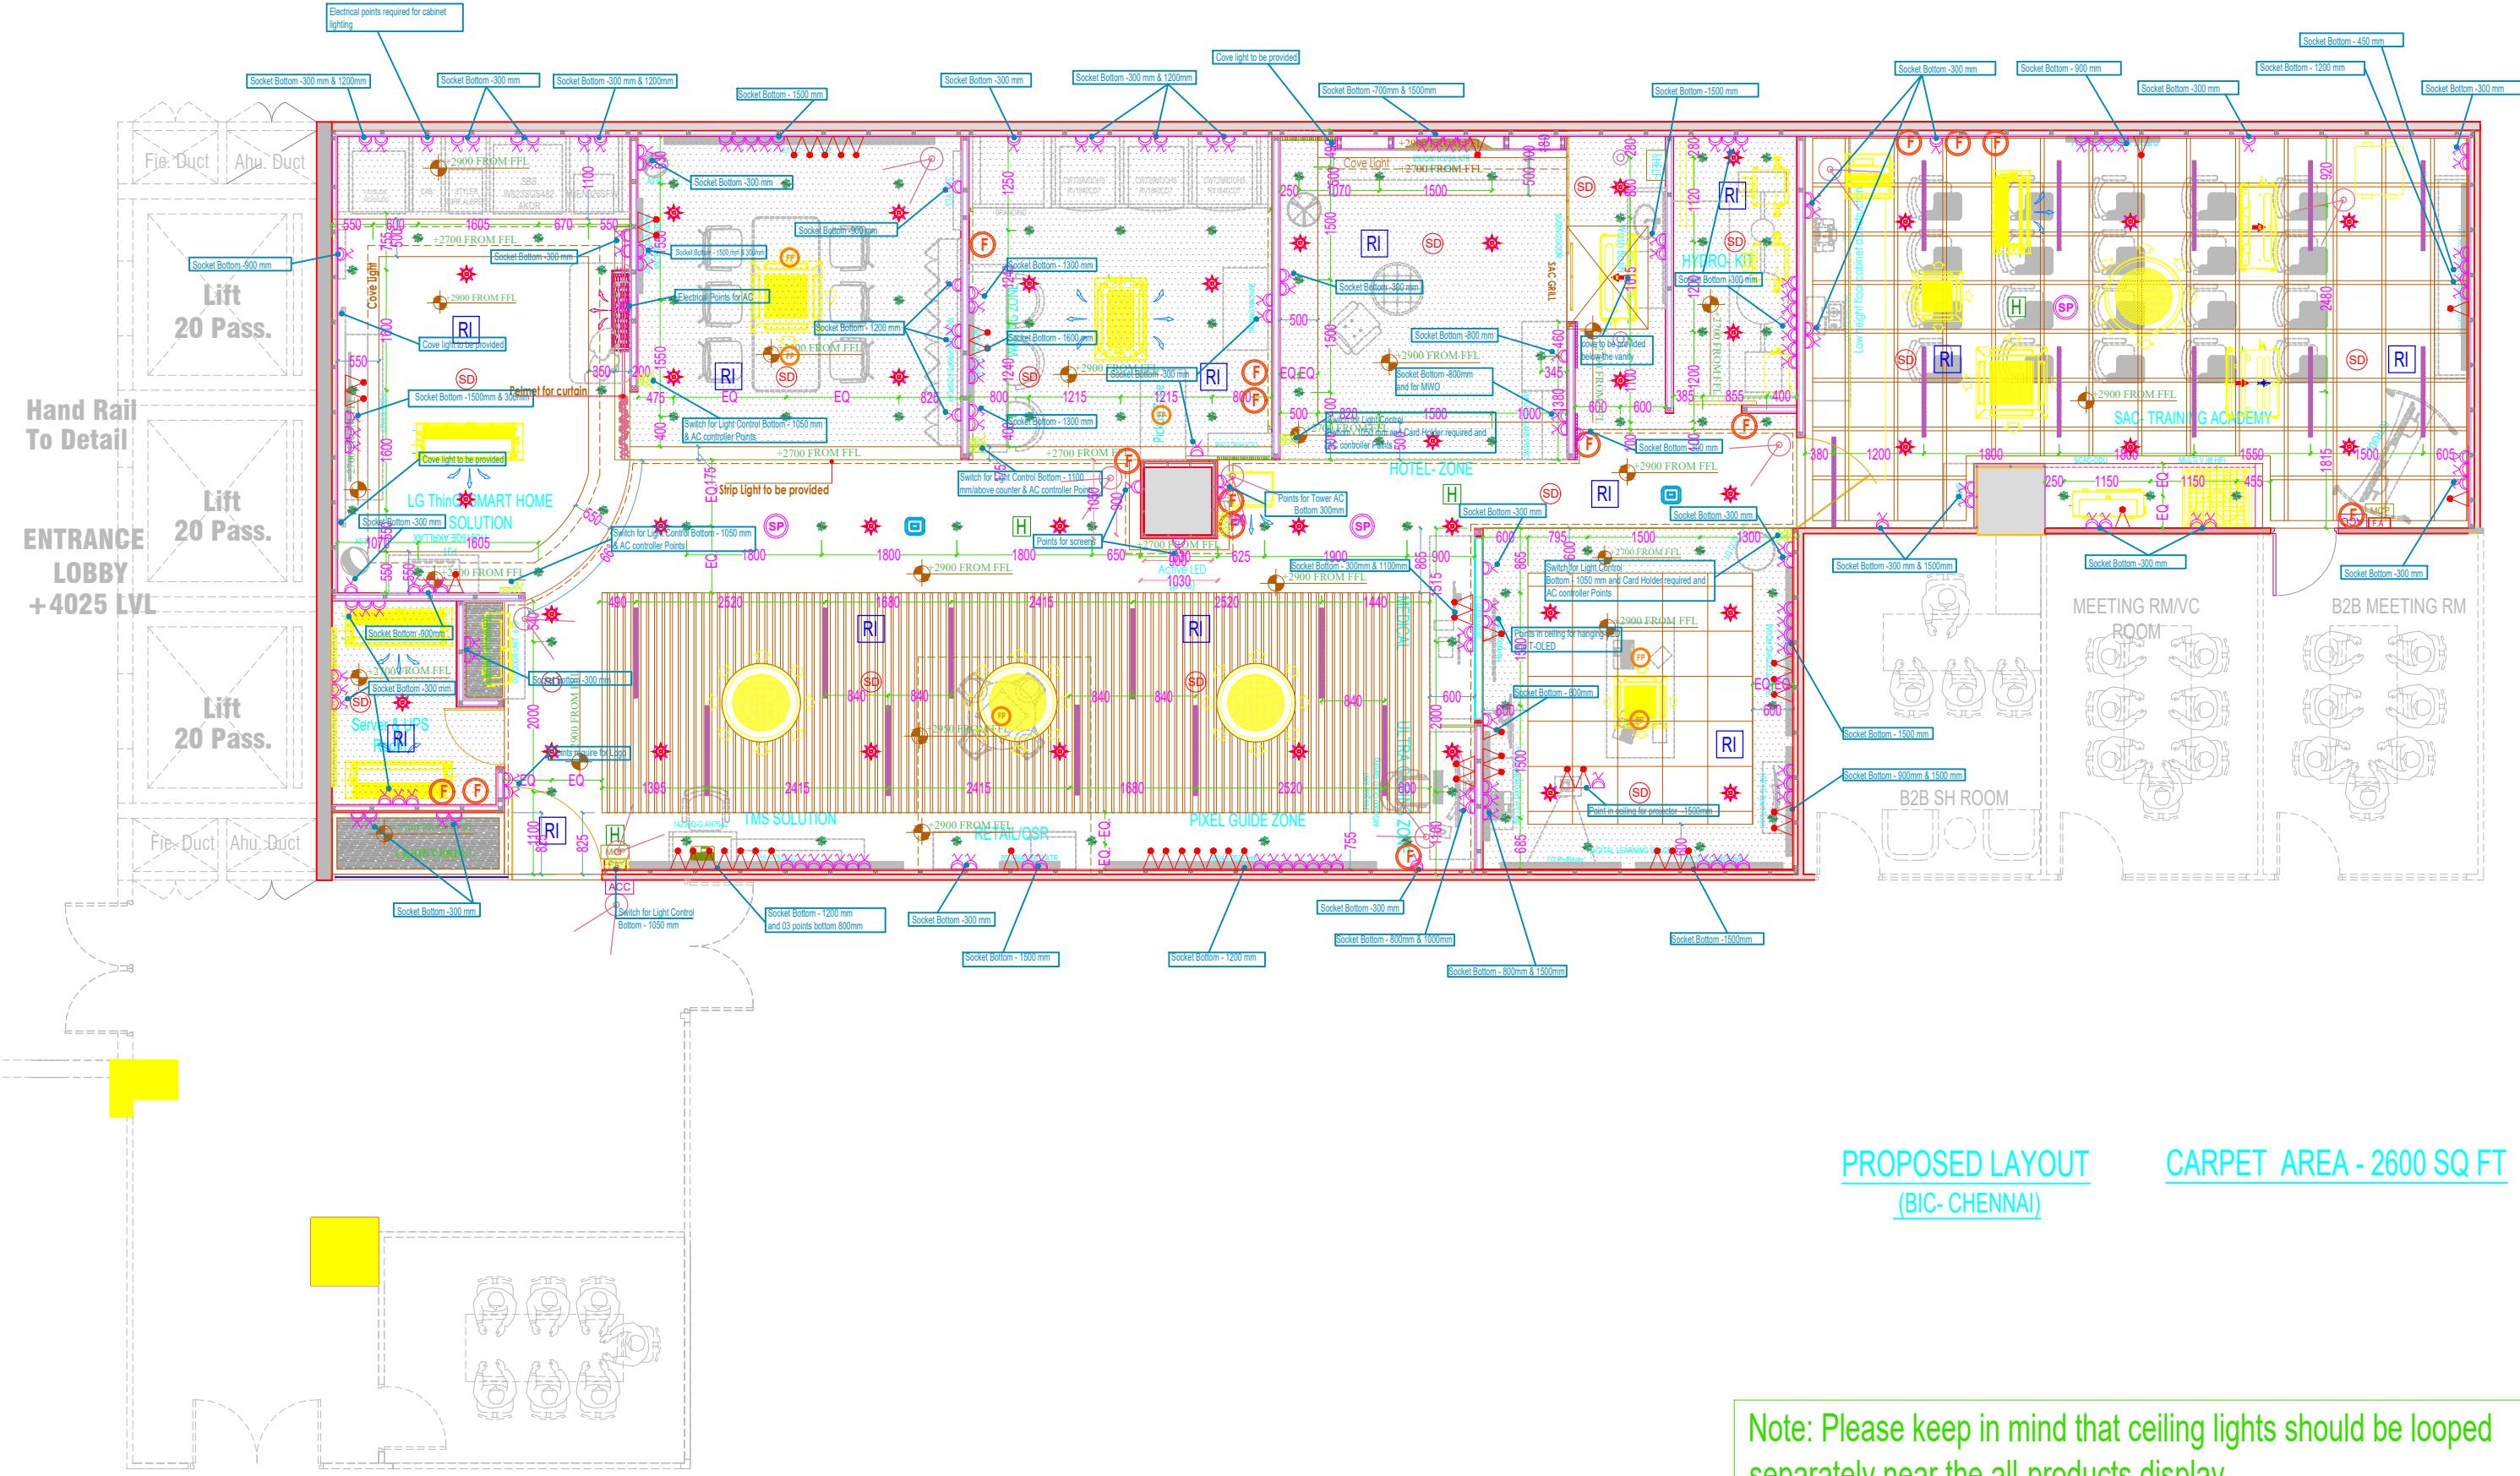

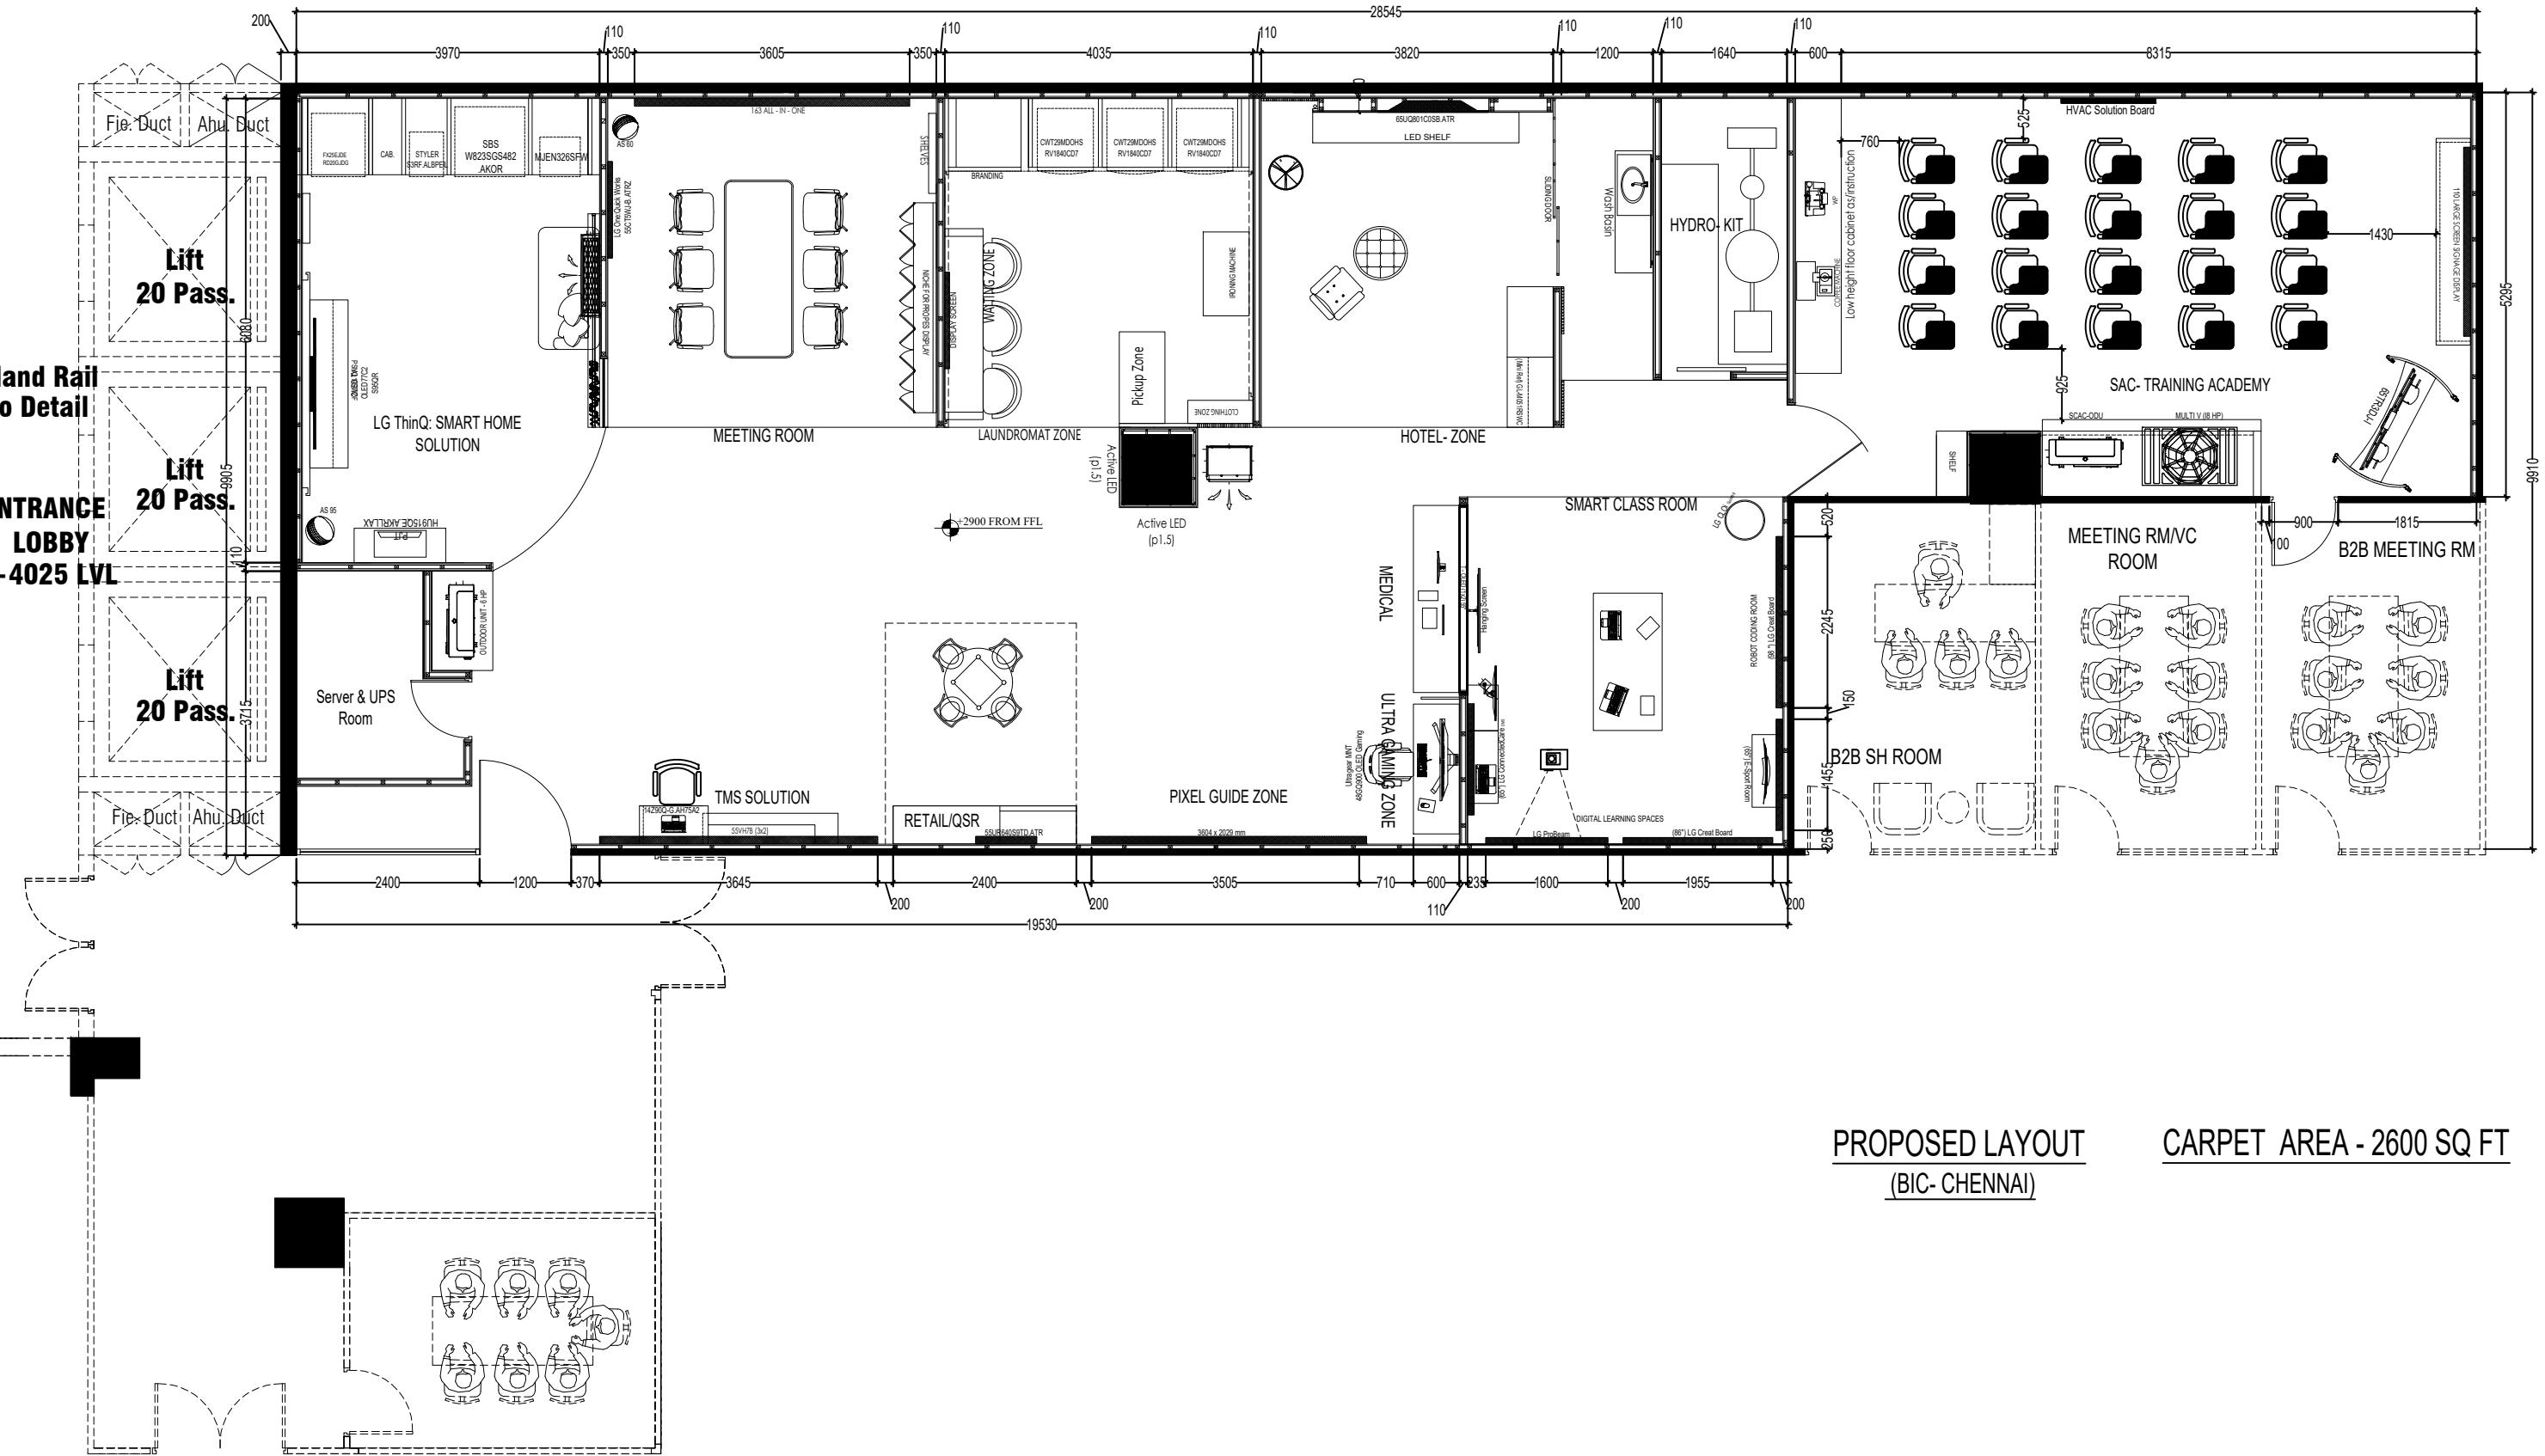

PROPOSED LAYOUT (BIC- CHENNAI)

CARPET AREA - 2600 SQ FT



LIGHTING LEGEND			
SYMBOL	TYPE	LOCATION	QTY.
	Linear LED Light (28W 6500K)	Philips / Wipro / Havells	21
	Batten (24W 6500K)	Philips / Wipro / Havells	02
	Down Light (9 12W 4000K)	Philips / Wipro / Havells	75
	Strip light with aluminum profile	As/Approval	122 RFT.
	Cove Strip light	As/Approval	62 RFT.
	Panel Lights	As/Approval	2300mmx825mm 1300mmx525mm
	Access control	As/Approval	02
	Camera	As/Approval	10
	Wifi Router	As/Approval	02
	Speaker	As/Approval	03
	Hanging Lights for Washroom	As/Approval	02


LEGEND		
SYMBOL	TYPE	QTY.
	Smoke detector below false ceiling	14
	Heat detector Below false ceiling	00
	Response indicator	13
	Hooter	04
	Manual call point	02
	Fire alarm panel	02
	Gypsum Ceiling Fire Sprinkler	39
	Fire extinguisher on the wall	15

CLIENT: LG ELECTRONICS INDIA PVT. LTD.
PROJECT NAME: LG BIC, CHENNAI
DRAWING TITLE: REFLECTED CEILING PLAN

<u>DATE</u>	<u>SCALE</u>
10-08-2023	N.T.S.
<u>REVISION</u>	<u>PAPER SIZE</u>
R0	A 3


NOTE :
ALL DIMENSION TO BE CHECKED ON SITE.
DO NOT SCALE FROM THIS DRAWING.



HS Ad
GIIR Communications India Pvt. Ltd.
KP Towers, Tower D, 12th Floor, Plot
No. C-001B, Sector-16B,
Noida, Uttar Pradesh-201301.

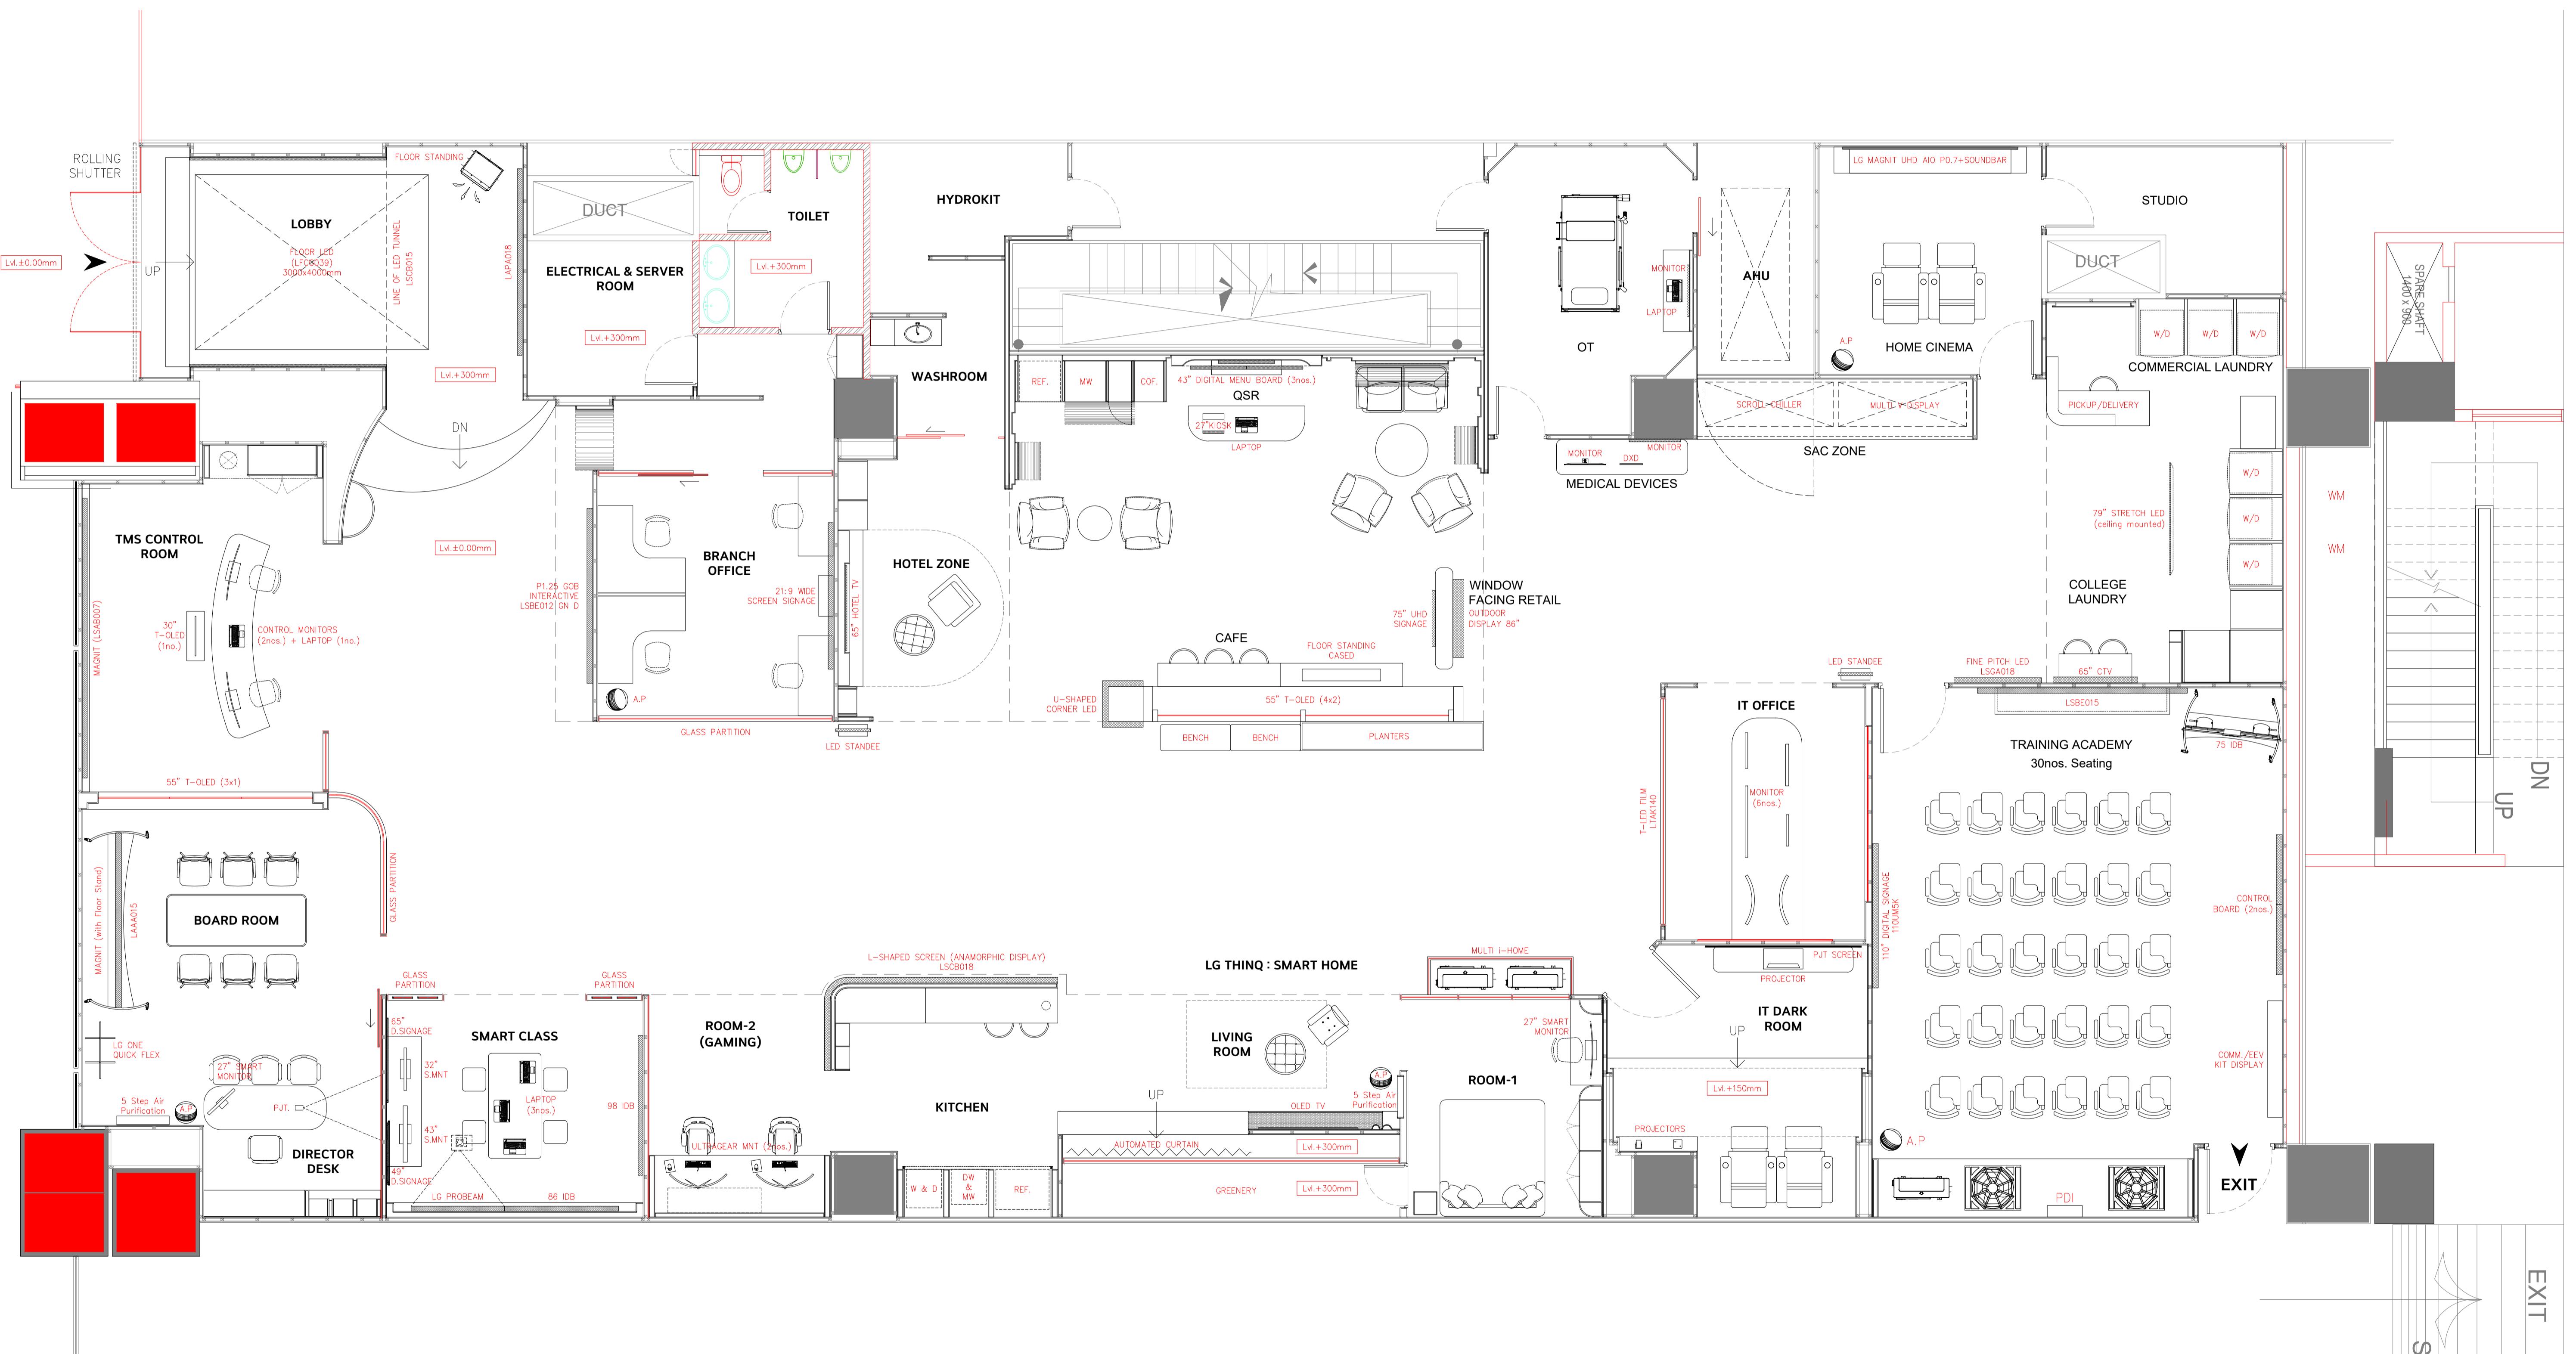


SleepWell

Across India – Retail Projects

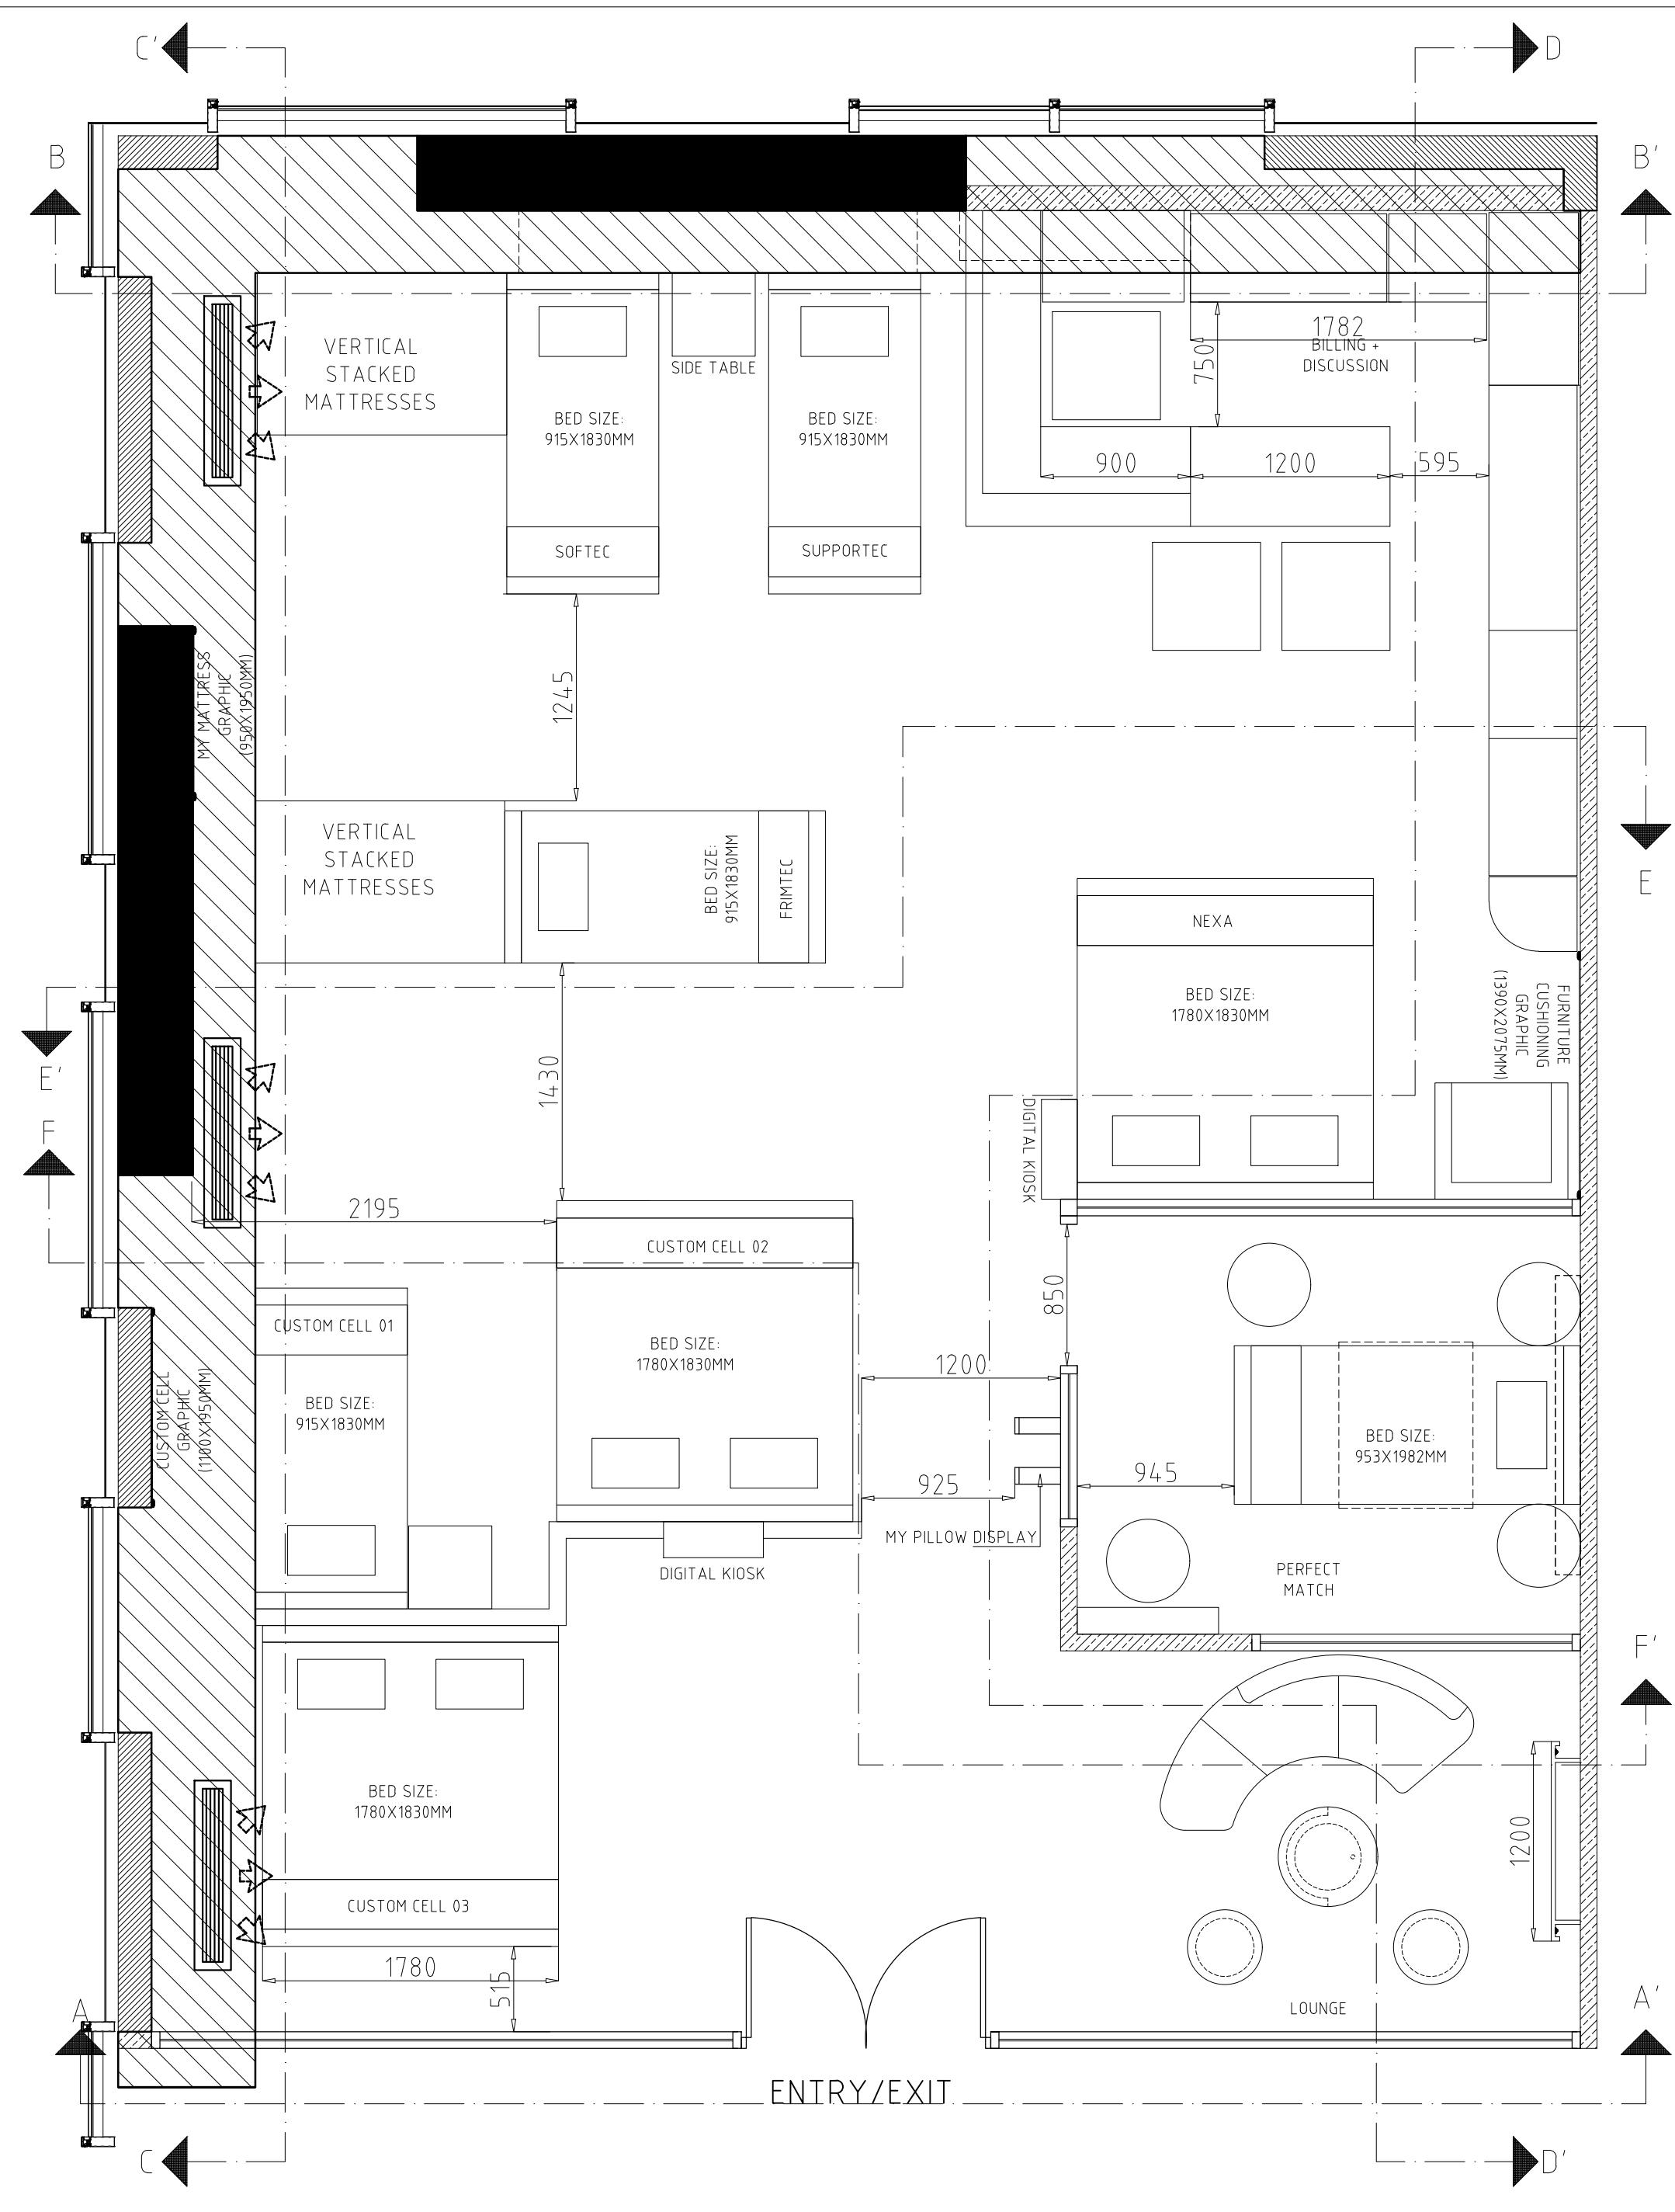

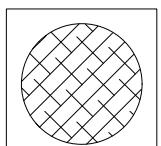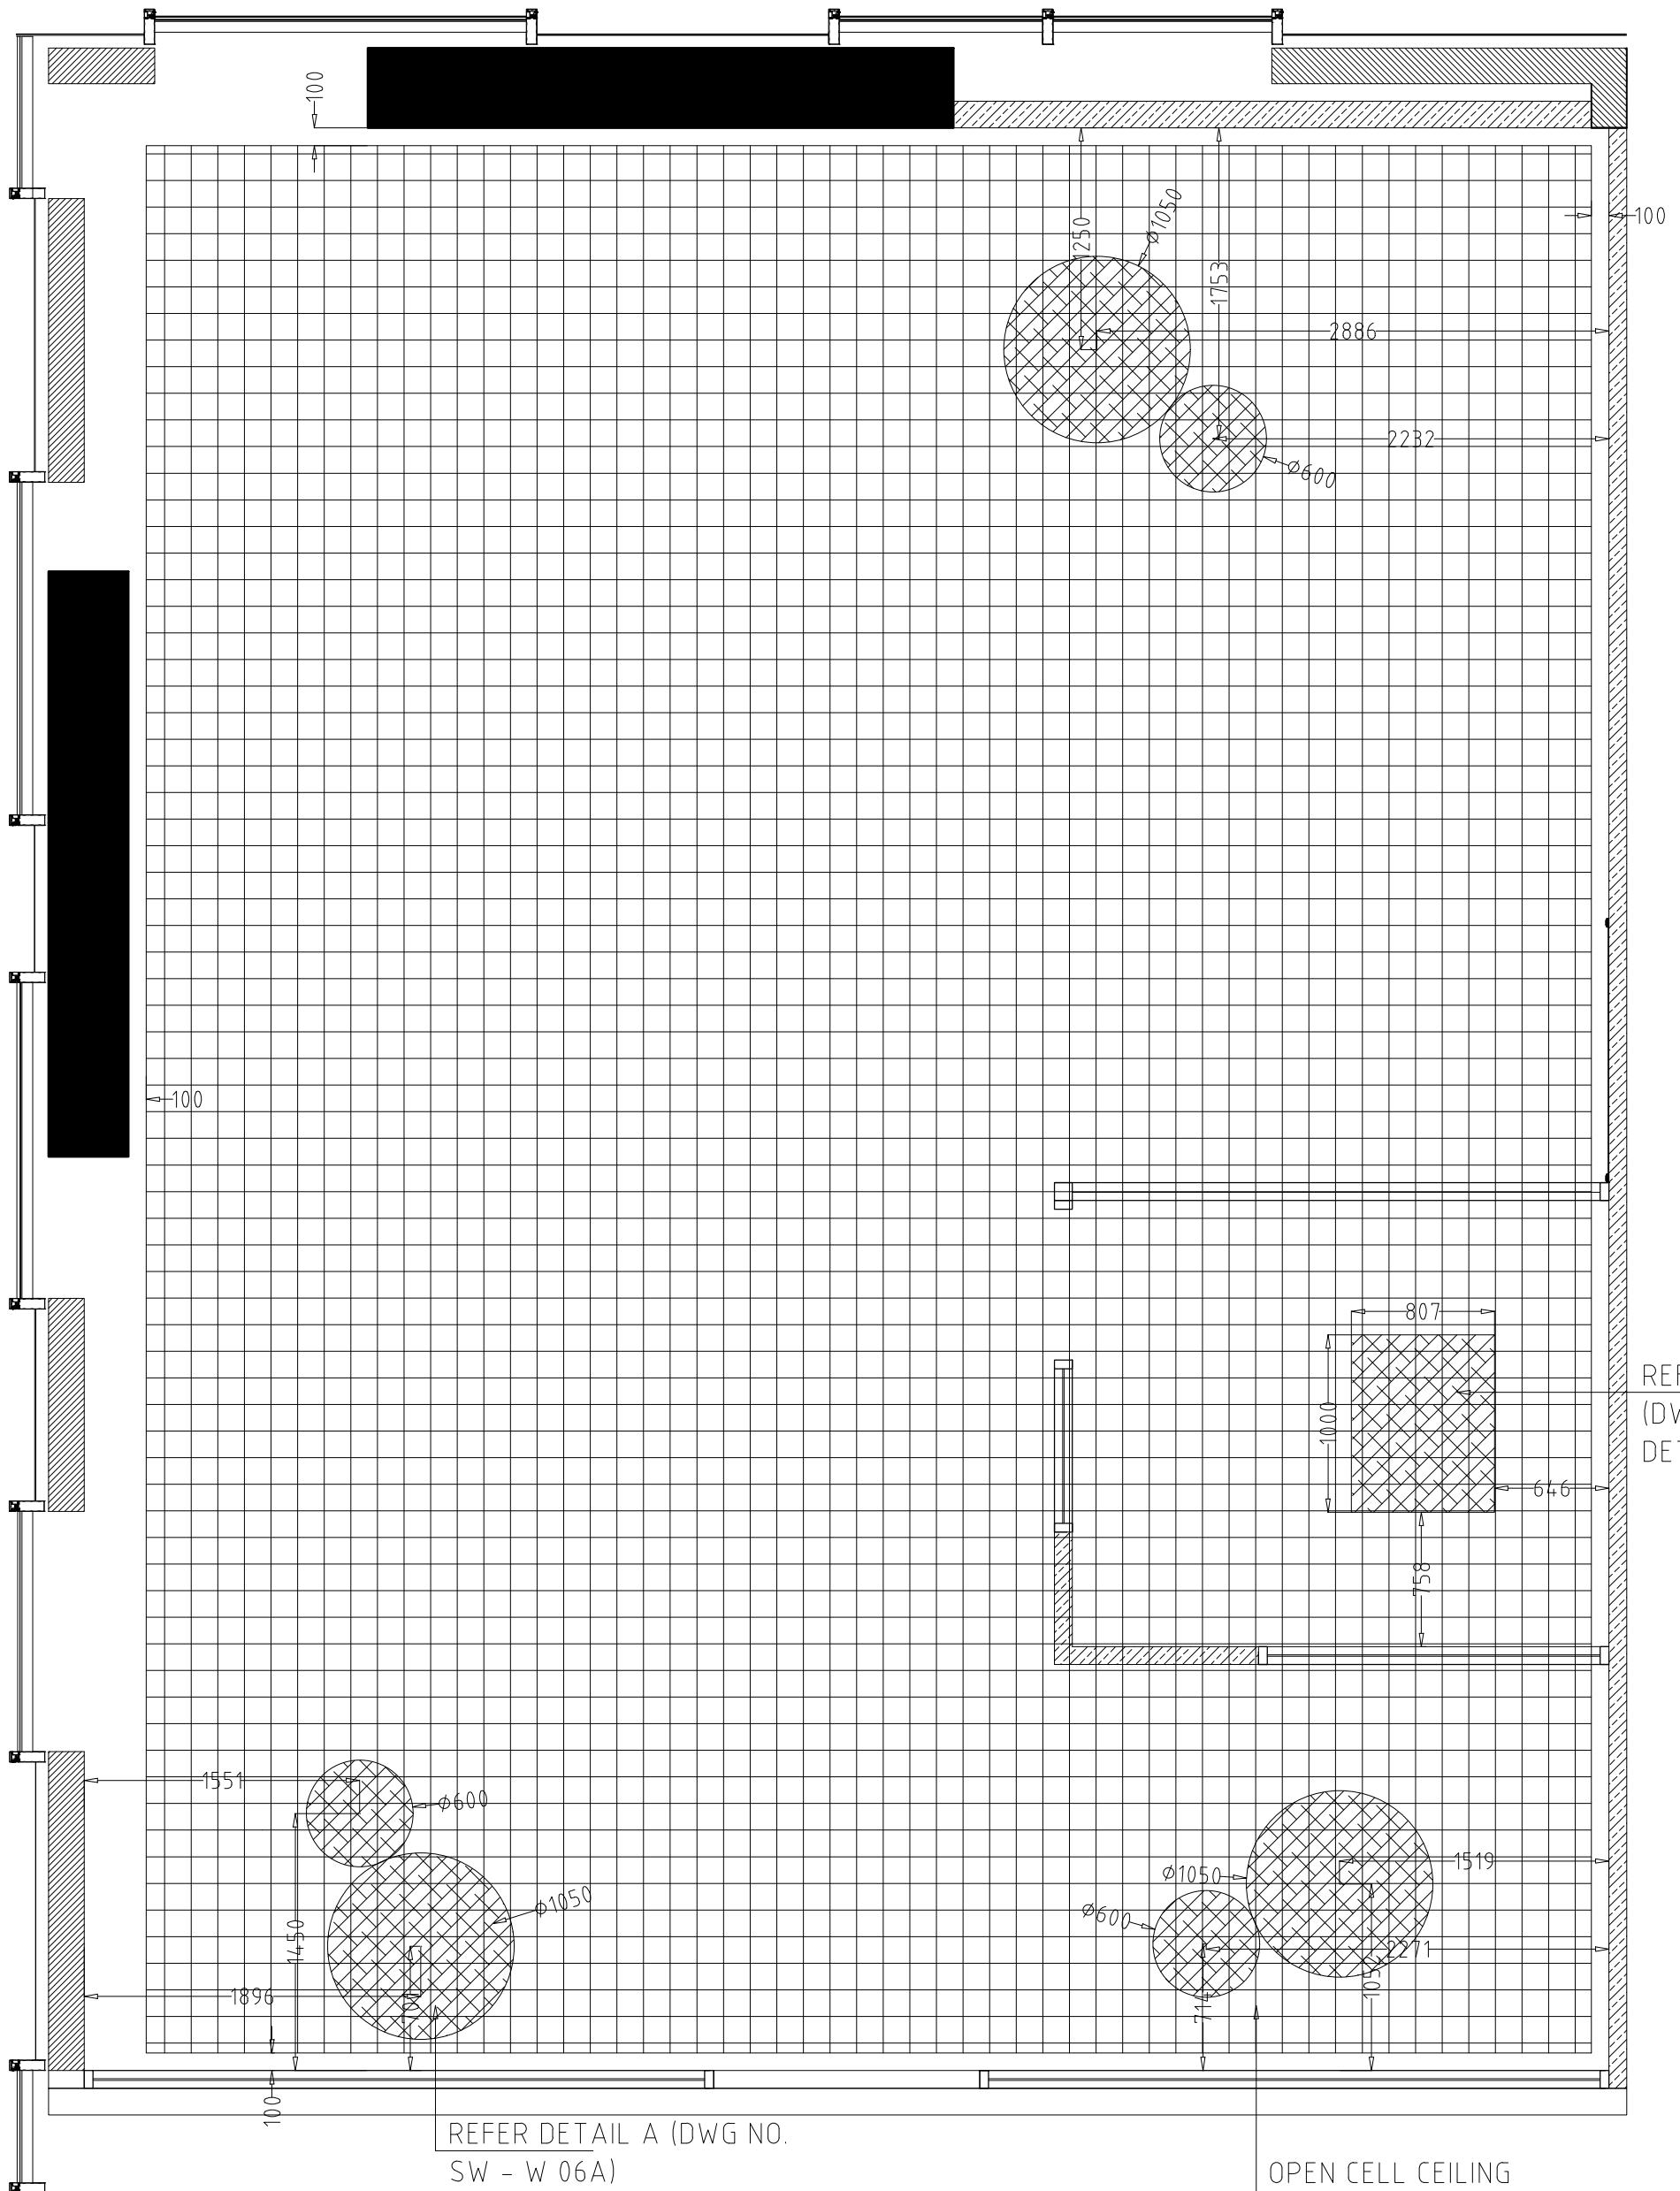


PAINT FINISH: ACRYLIC EMULSION PAINT: STEEL
GREY 0643, COLOR SPECTRA, ASIAN PAINTS

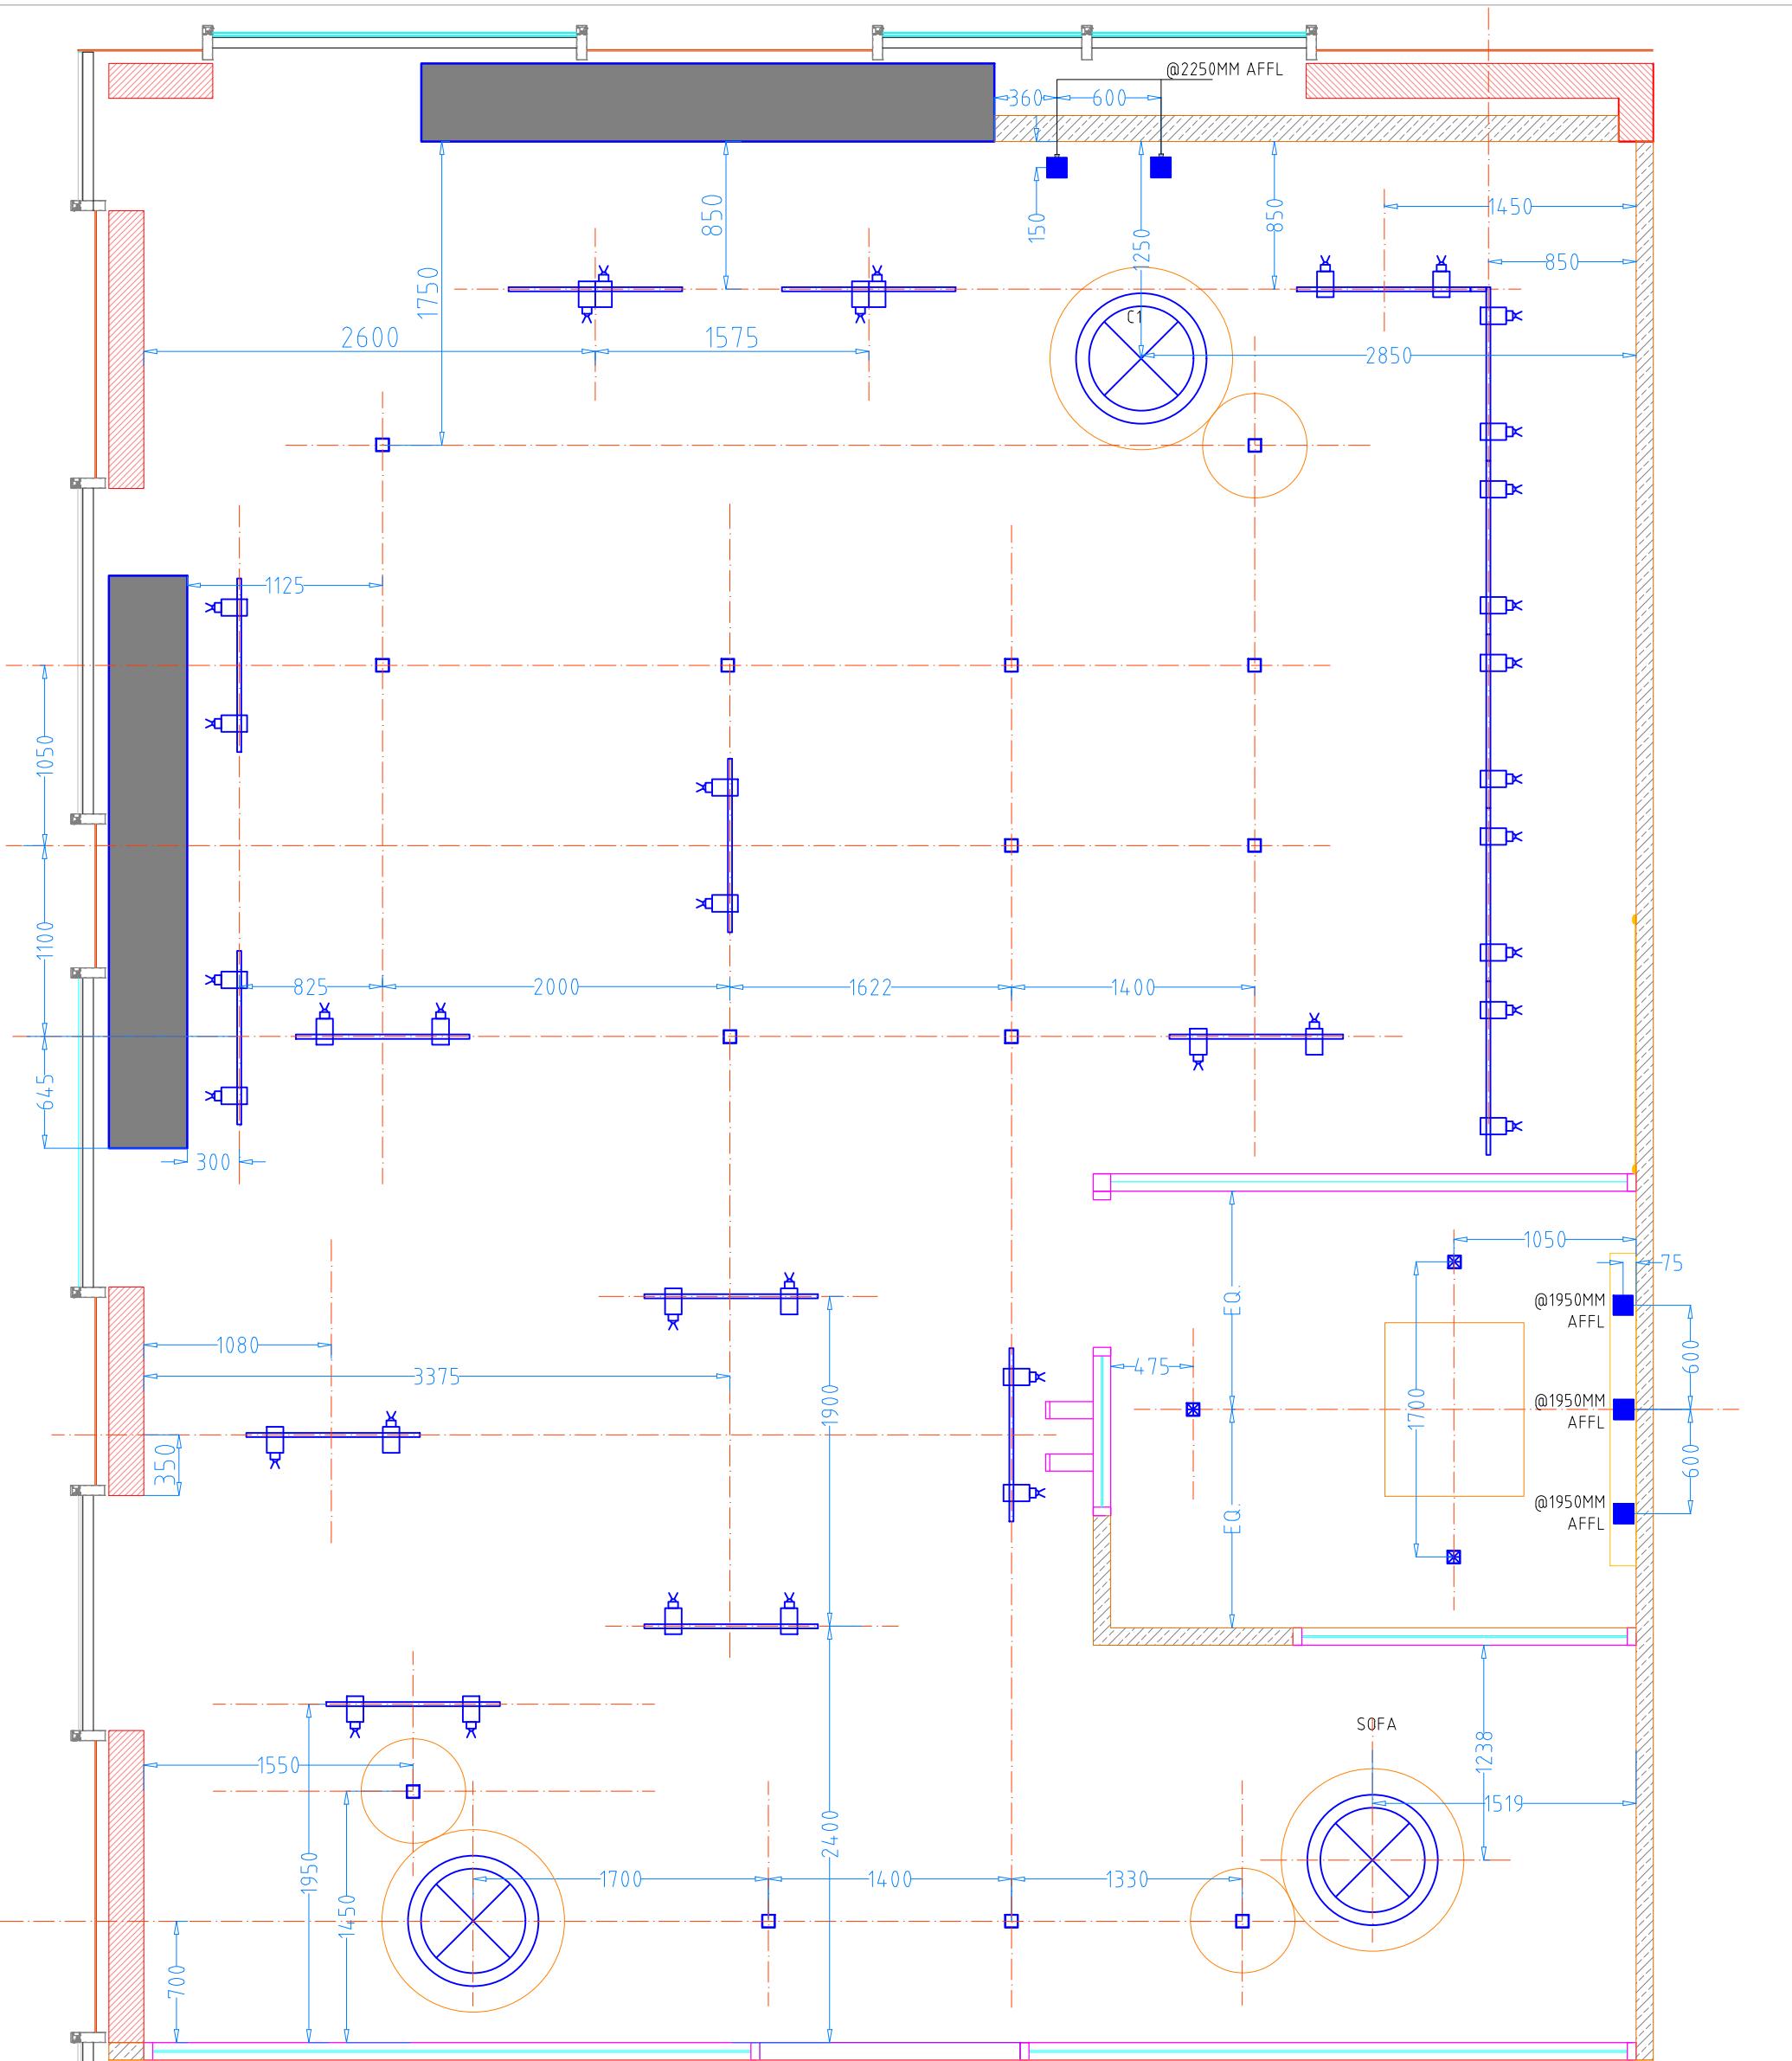


ENTRY/EXIT

LEGEND:		
SYMBOL	DESCRIPTION	QTY.
(circle with X)	HANGING LIGHT AS/SAMPLE	03
—(track system symbol)	1X20W 4000K, ANKUR TOSH GU10 TRACK SPOT BK FITTING (BLACK) ANKUR MAKE	36
□	QR LED SWIVEL LIGHT	18
■	1W SHELF LIGHT	05
☒	20W QR LED LIGHT WITH DIMMABLE BALLAST	03

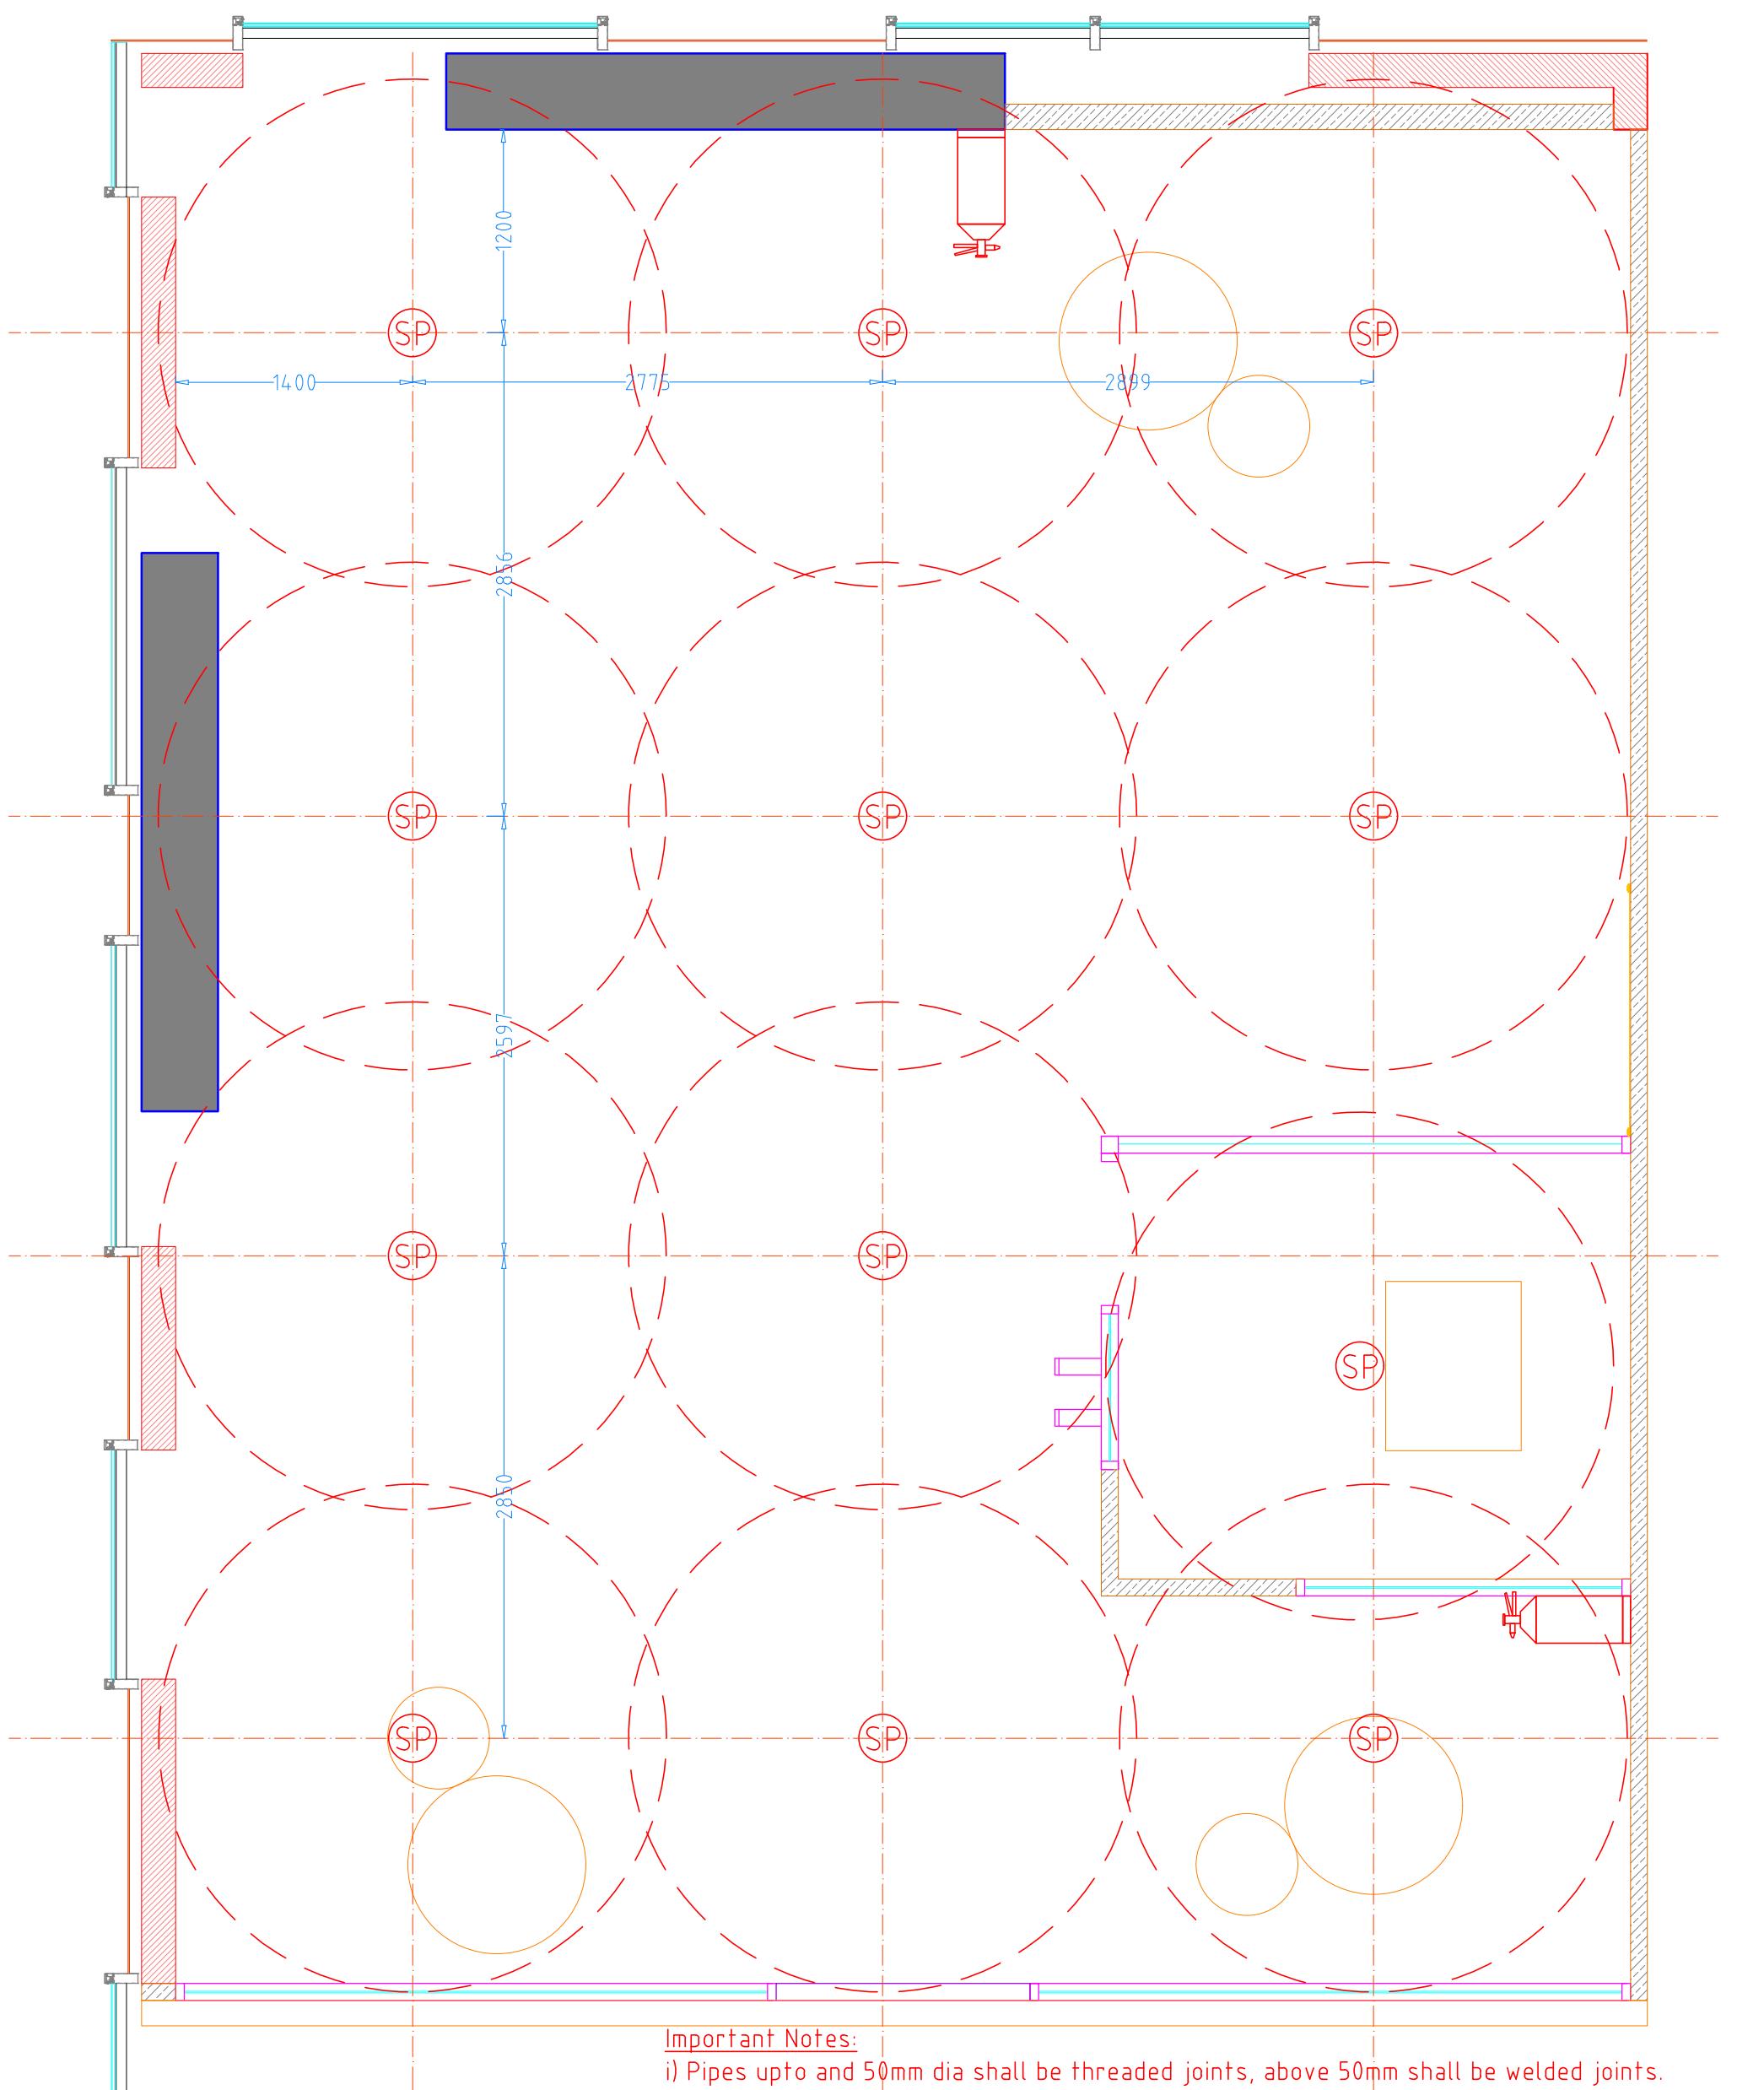


LEGEND:-

SYMBOL	DESCRIPTION
	68°C NEW PENDENT TYPE SPRINKLERS (TYCO MAKE)
	HAND HELD CO2 TYPE FIRE EXTINGUISHER 4 Kg CAPACITY, CEASEFIRE MAKE, CENTER MOUNTED @ 1050mm AFFL



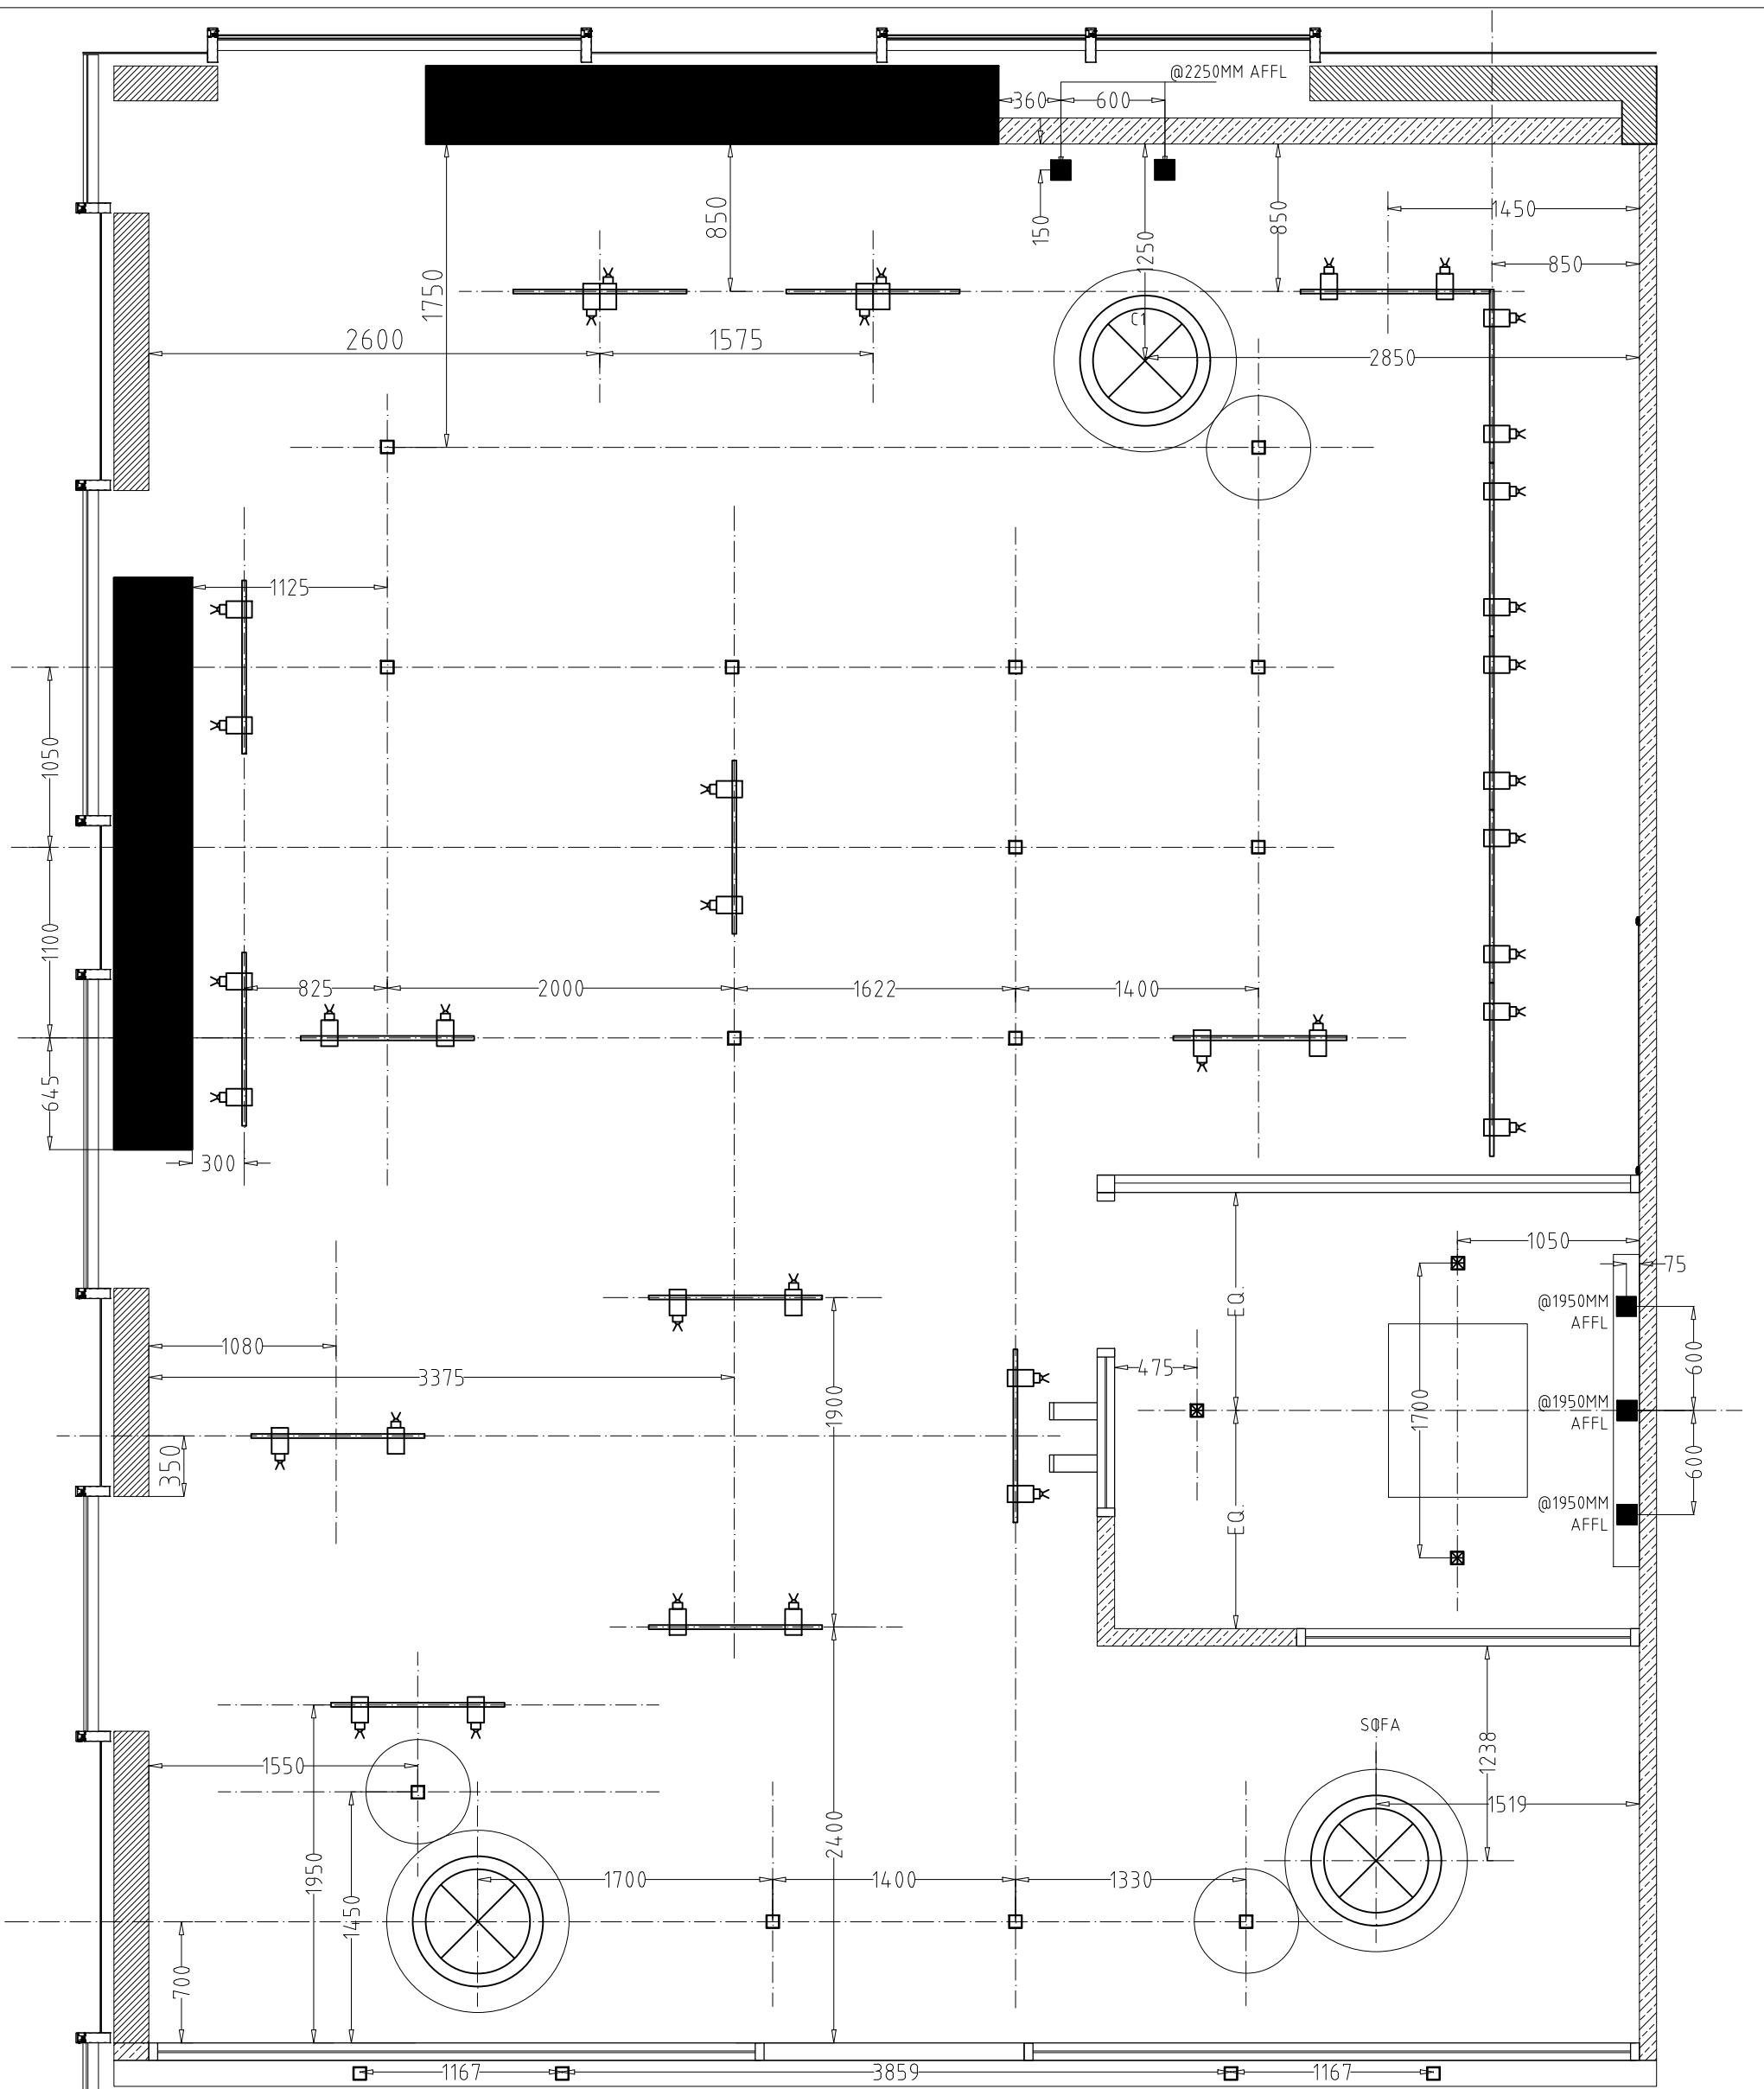


3039



<u>LEGEND:</u>		
SYMBOL	DESCRIPTION	Q.T.Y.
	HANGING LIGHT AS/SAMPLE	03
	1X20W 4000K, ANKUR TOSH GU10 TRACK SPOT BK FITTING (BLACK) ANKUR MAKE	36
	QR LED SWIVEL LIGHT	18
	1W SHELF LIGHT	05
	20W QR LED LIGHT WITH DIMMABLE BALLAST	03

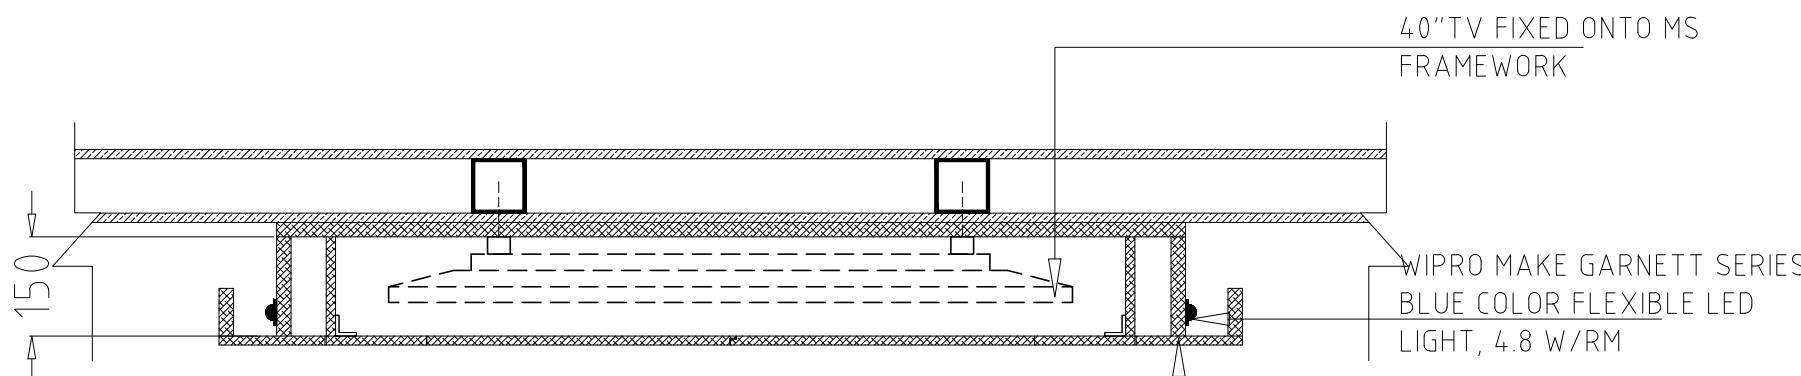

SECTIONAL PLAN

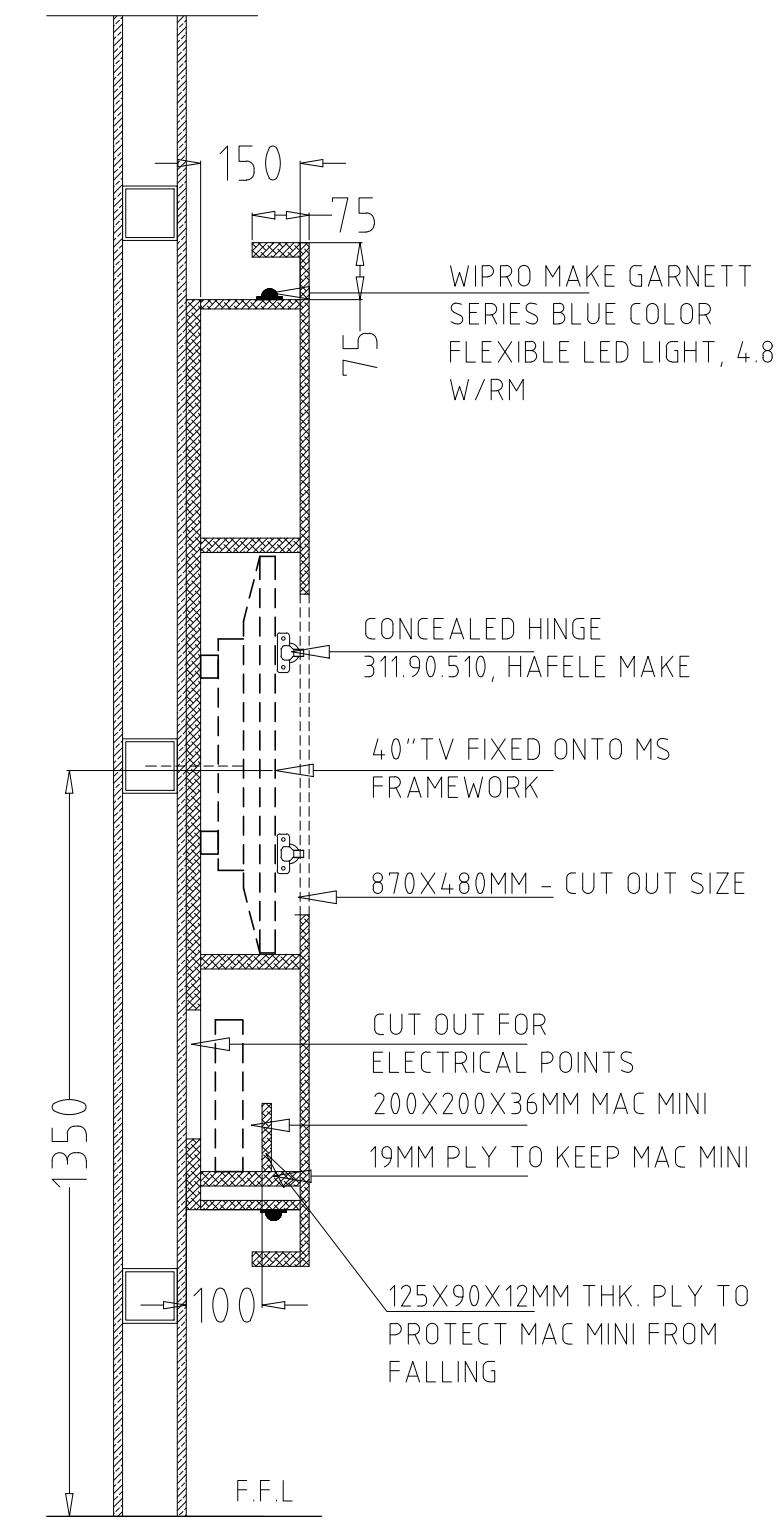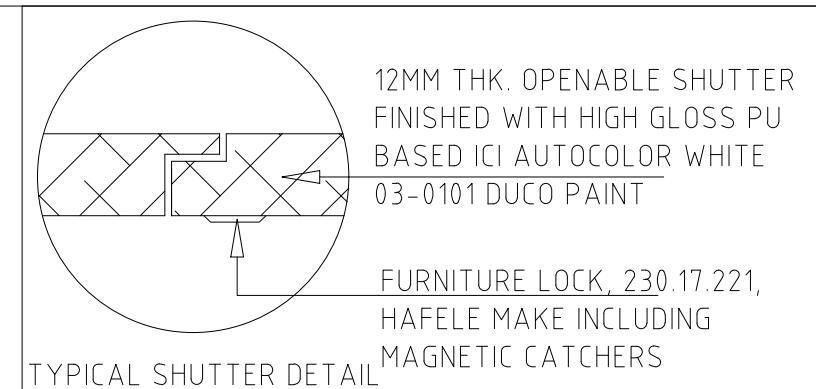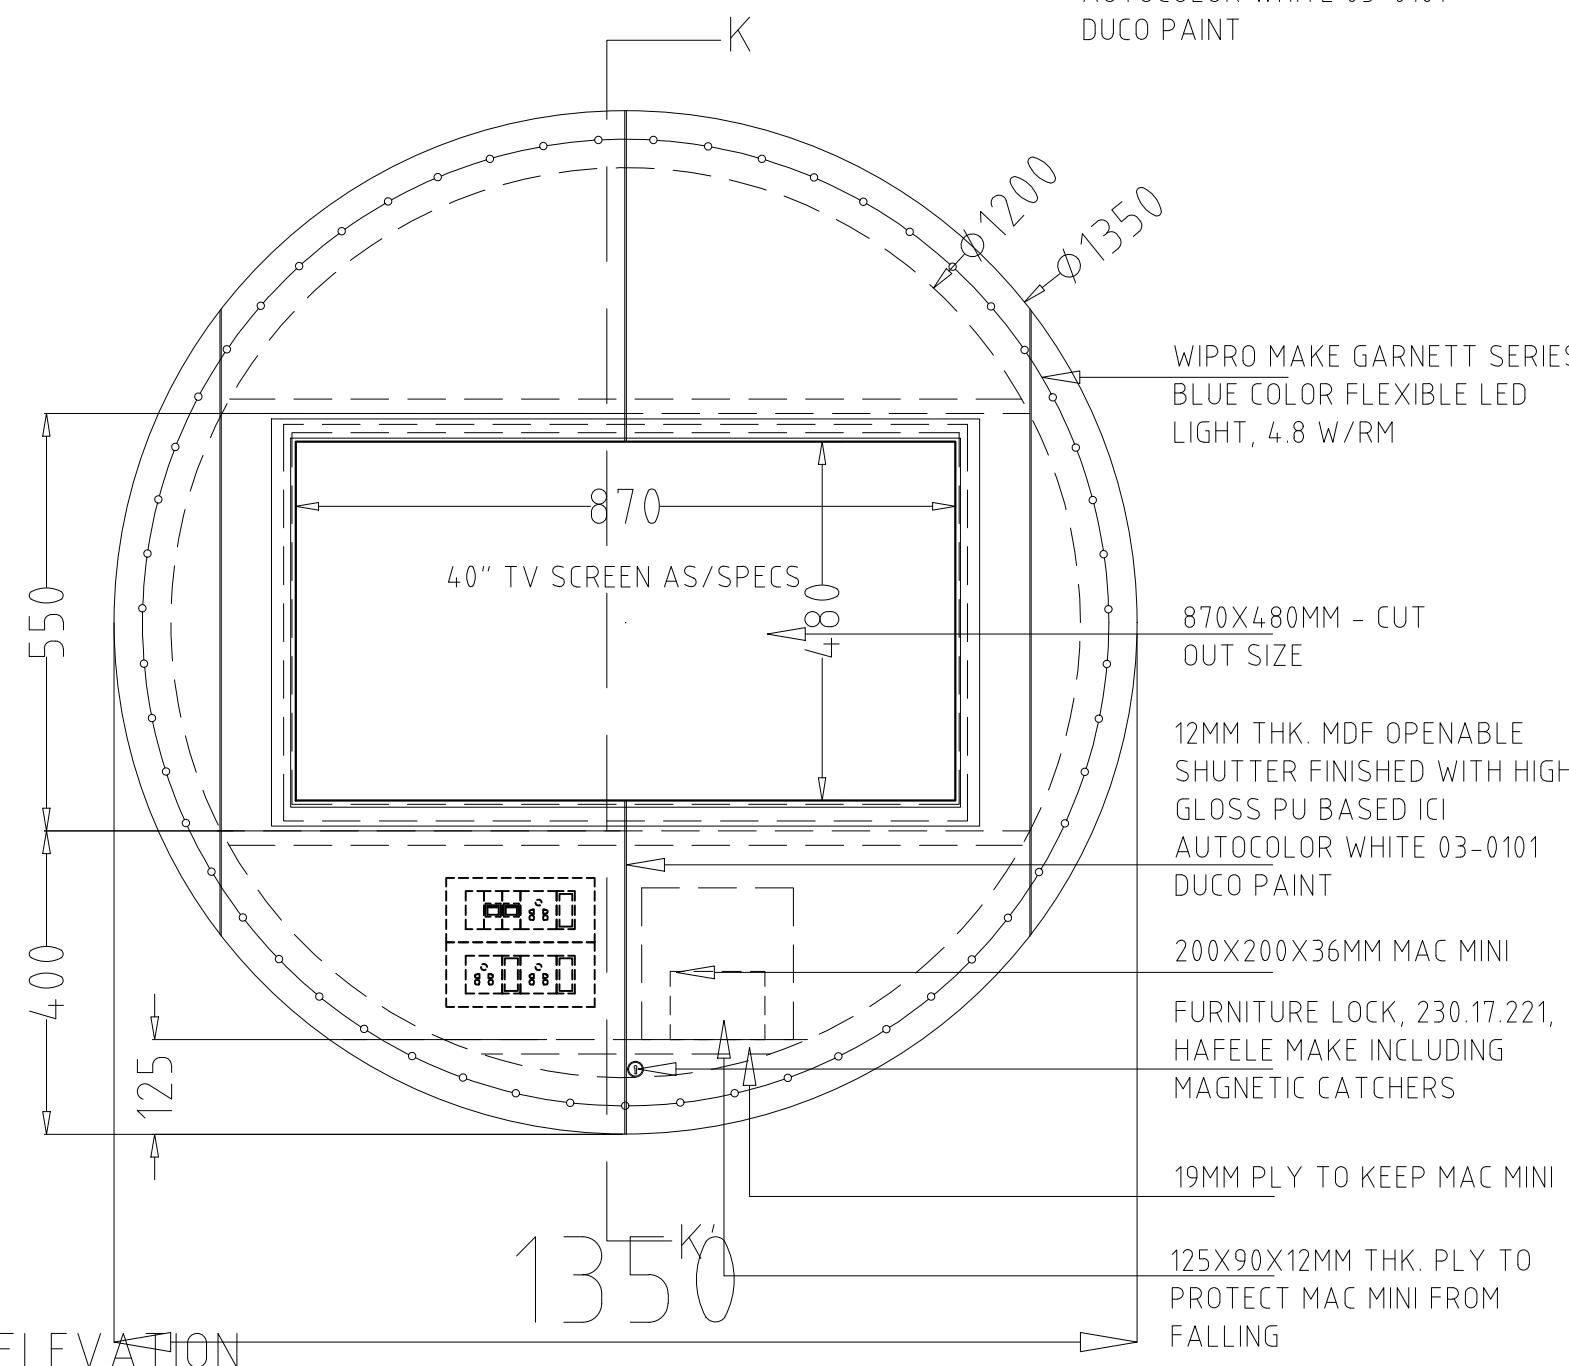

SECTION K-K'

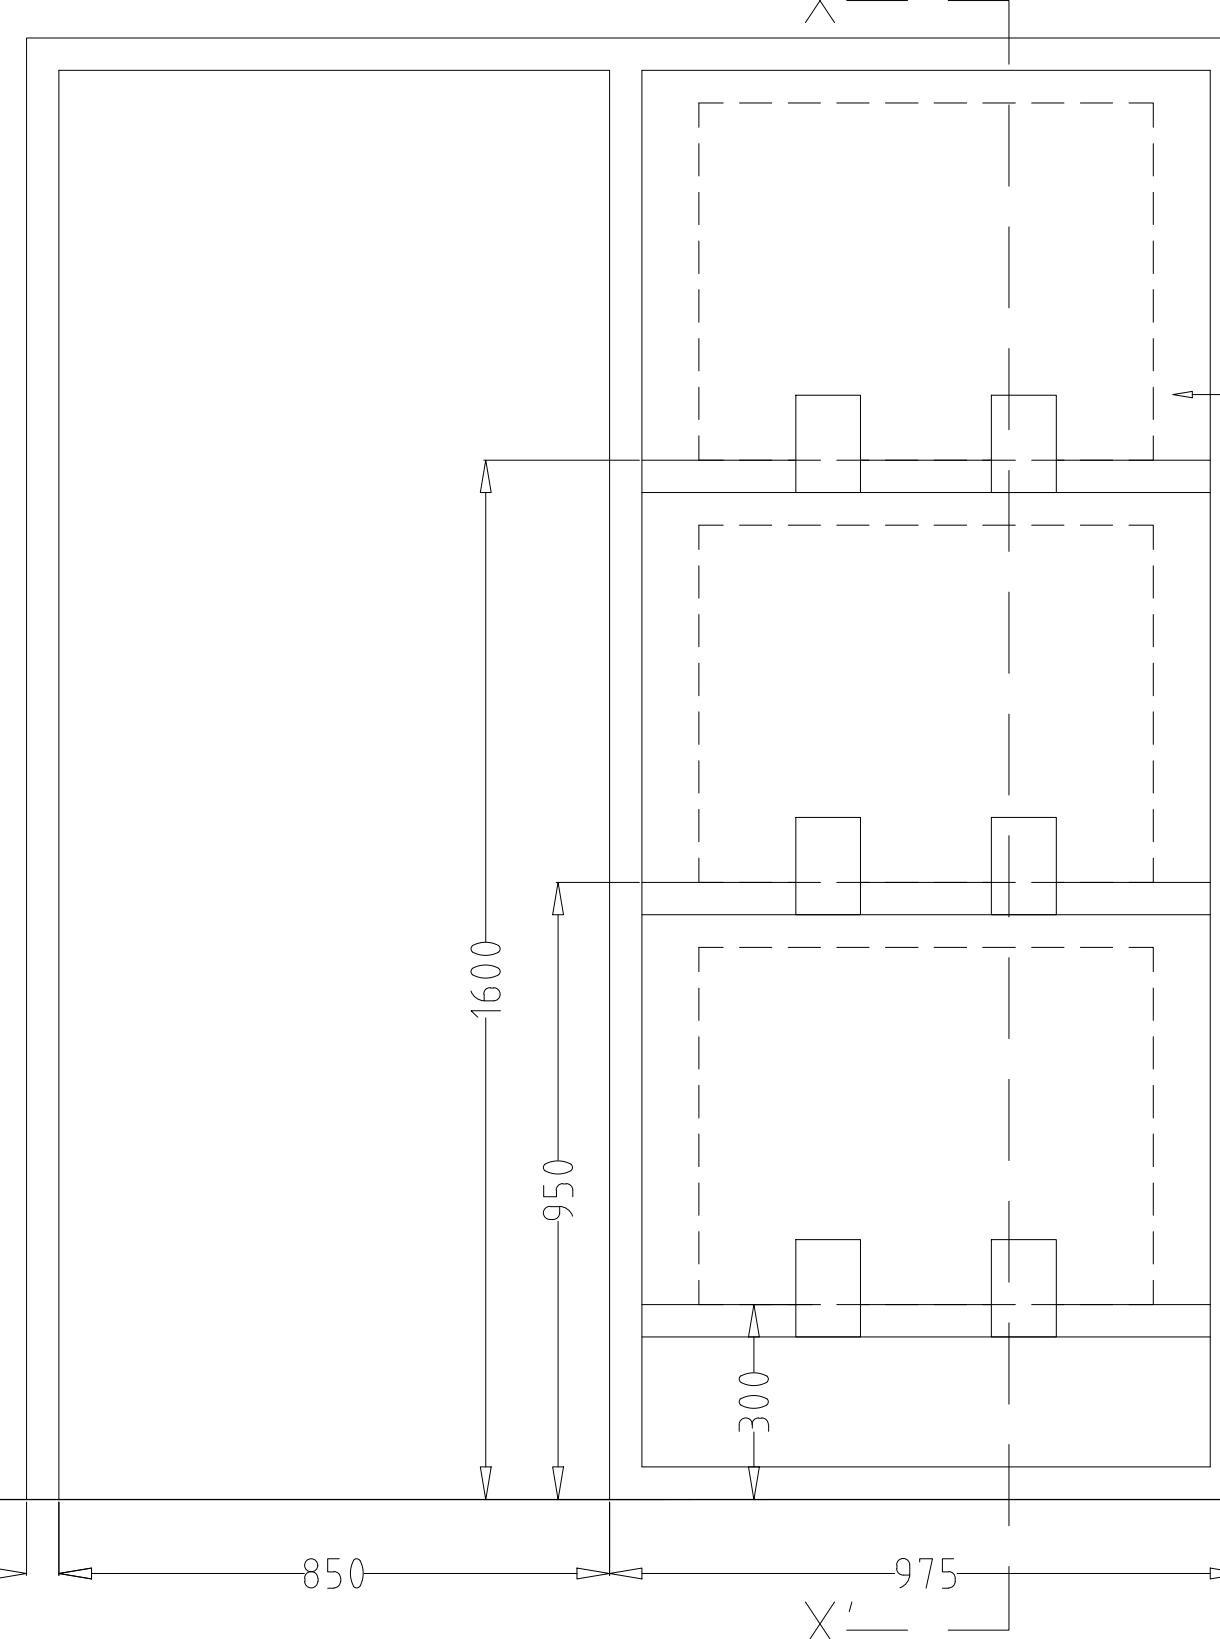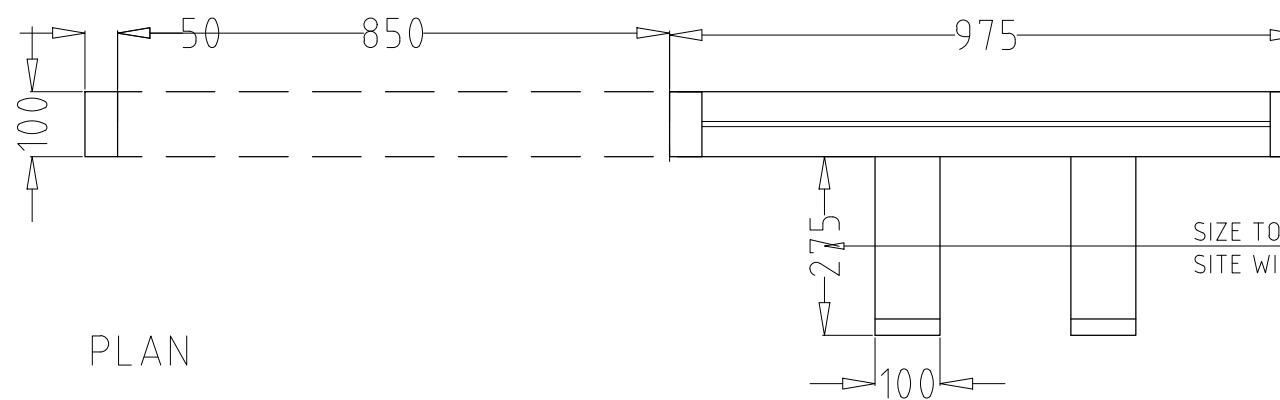

50X100MM WOODEN SECTION
FINISHED IN HIGH GLOSS PU BASED ICI
AUTOCOLOR SANDAL PASTE 03 -
9414 DUCO PAINT

10MM TOUGHENED GLASS

50X100MM WOODEN SECTION
FINISHED IN HIGH GLOSS PU BASED ICI
AUTOCOLOR SANDAL PASTE 03 -
9414 DUCO PAINT

10MM TOUGHENED GLASS

50X100MM WOODEN SECTION
FINISHED IN HIGH GLOSS PU BASED ICI
AUTOCOLOR SANDAL PASTE 03 -
9414 DUCO PAINT

25X150MM WOODEN SECTION
FINISHED IN HIGH GLOSS PU BASED ICI
AUTOCOLOR SANDAL PASTE 03 -
9414 DUCO PAINT

1600

950

300


275


150

100


SIZE TO BE CONFIRMED AT SITE WITH ACTUAL PRODUCT



SECTION X-X'

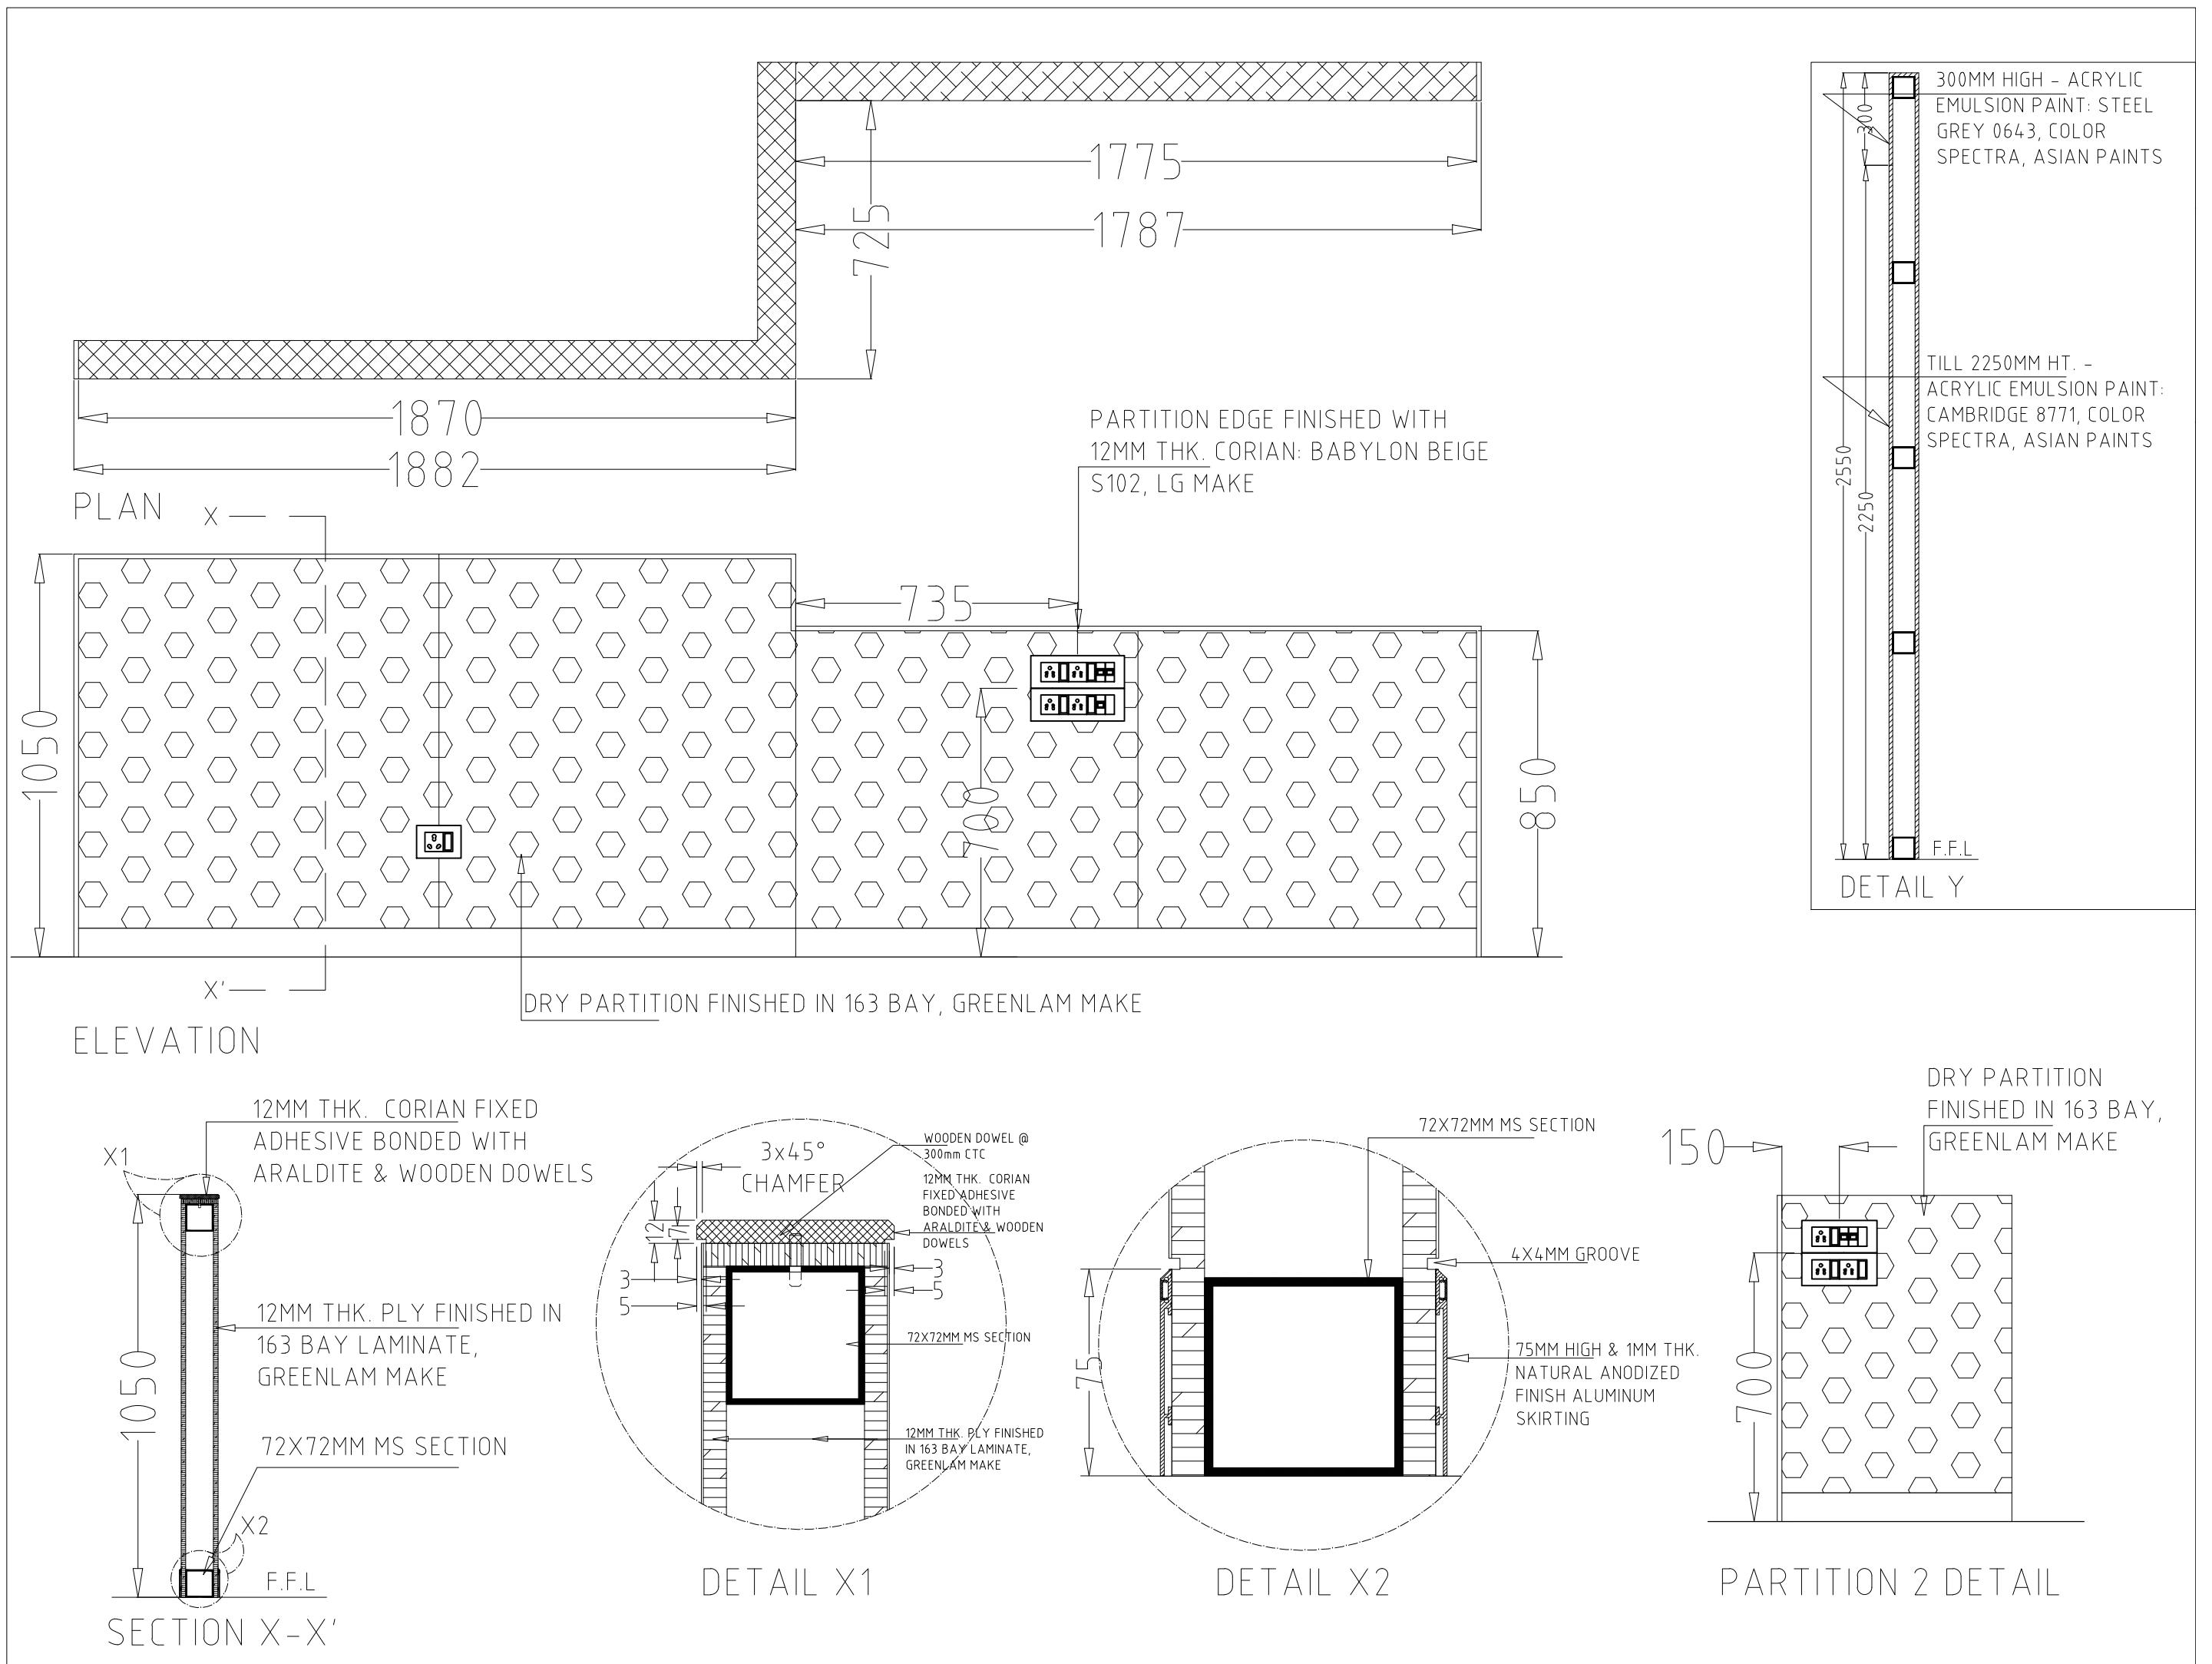



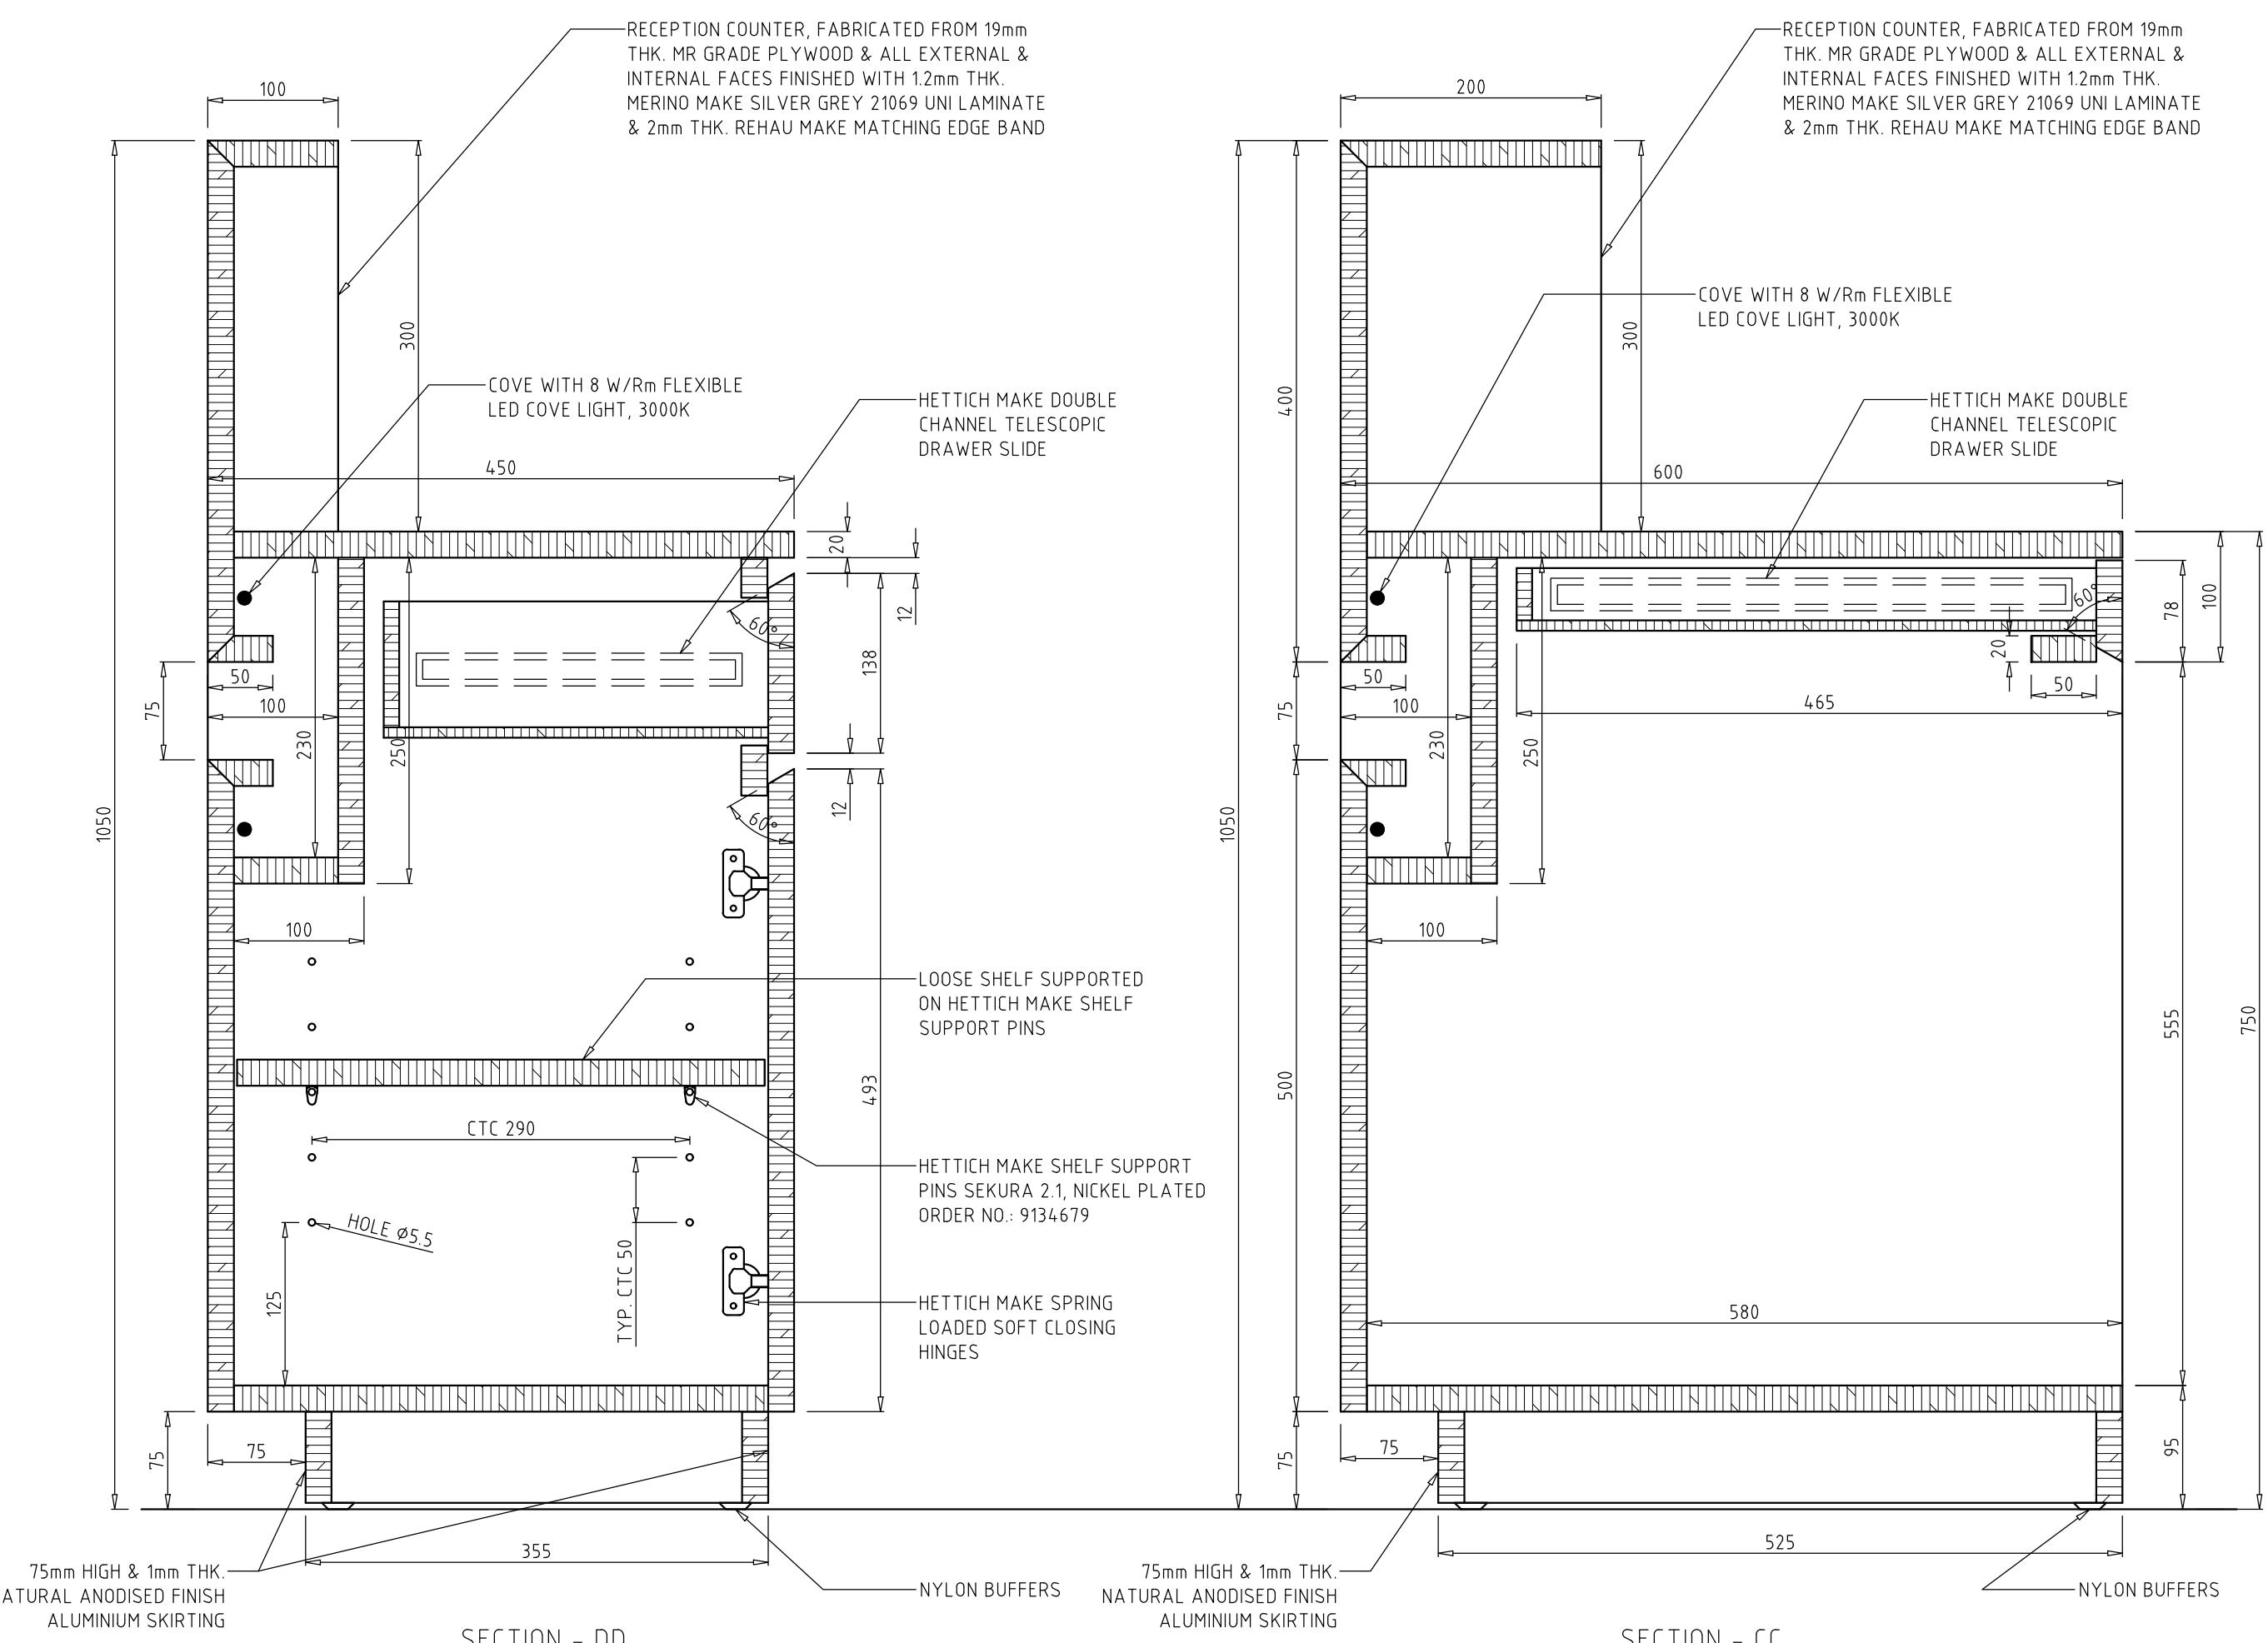


SECTION - DD

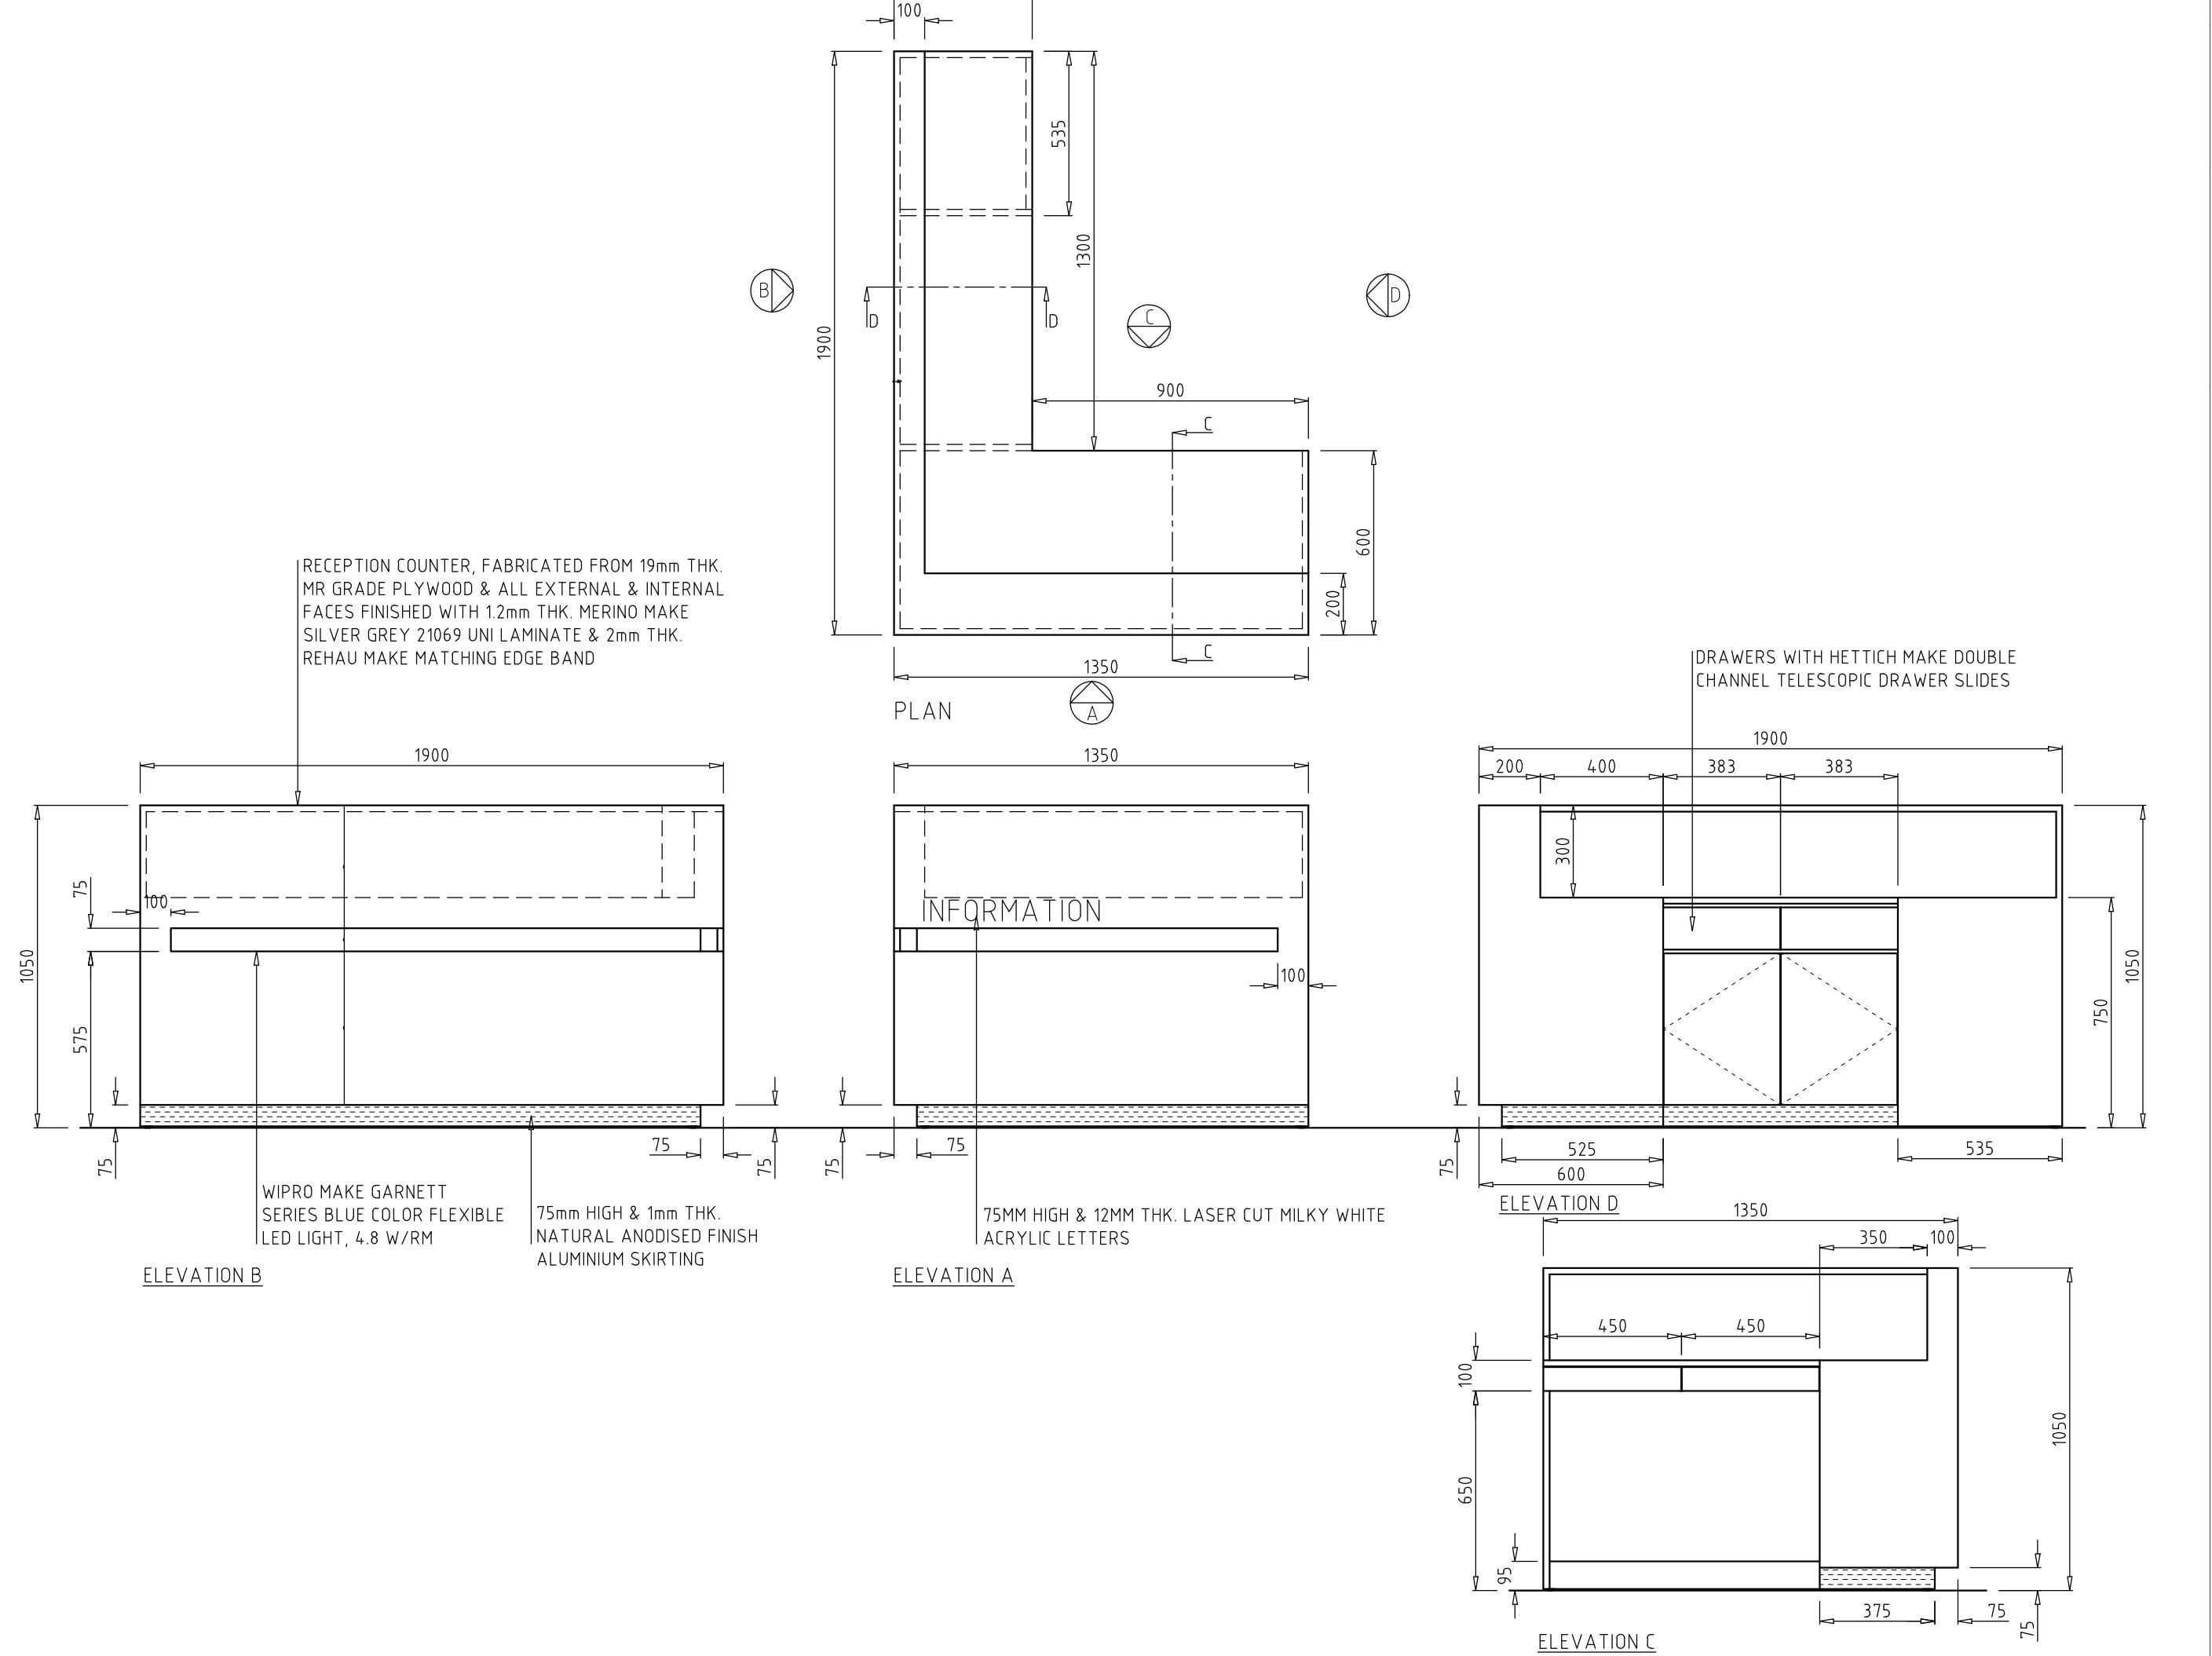


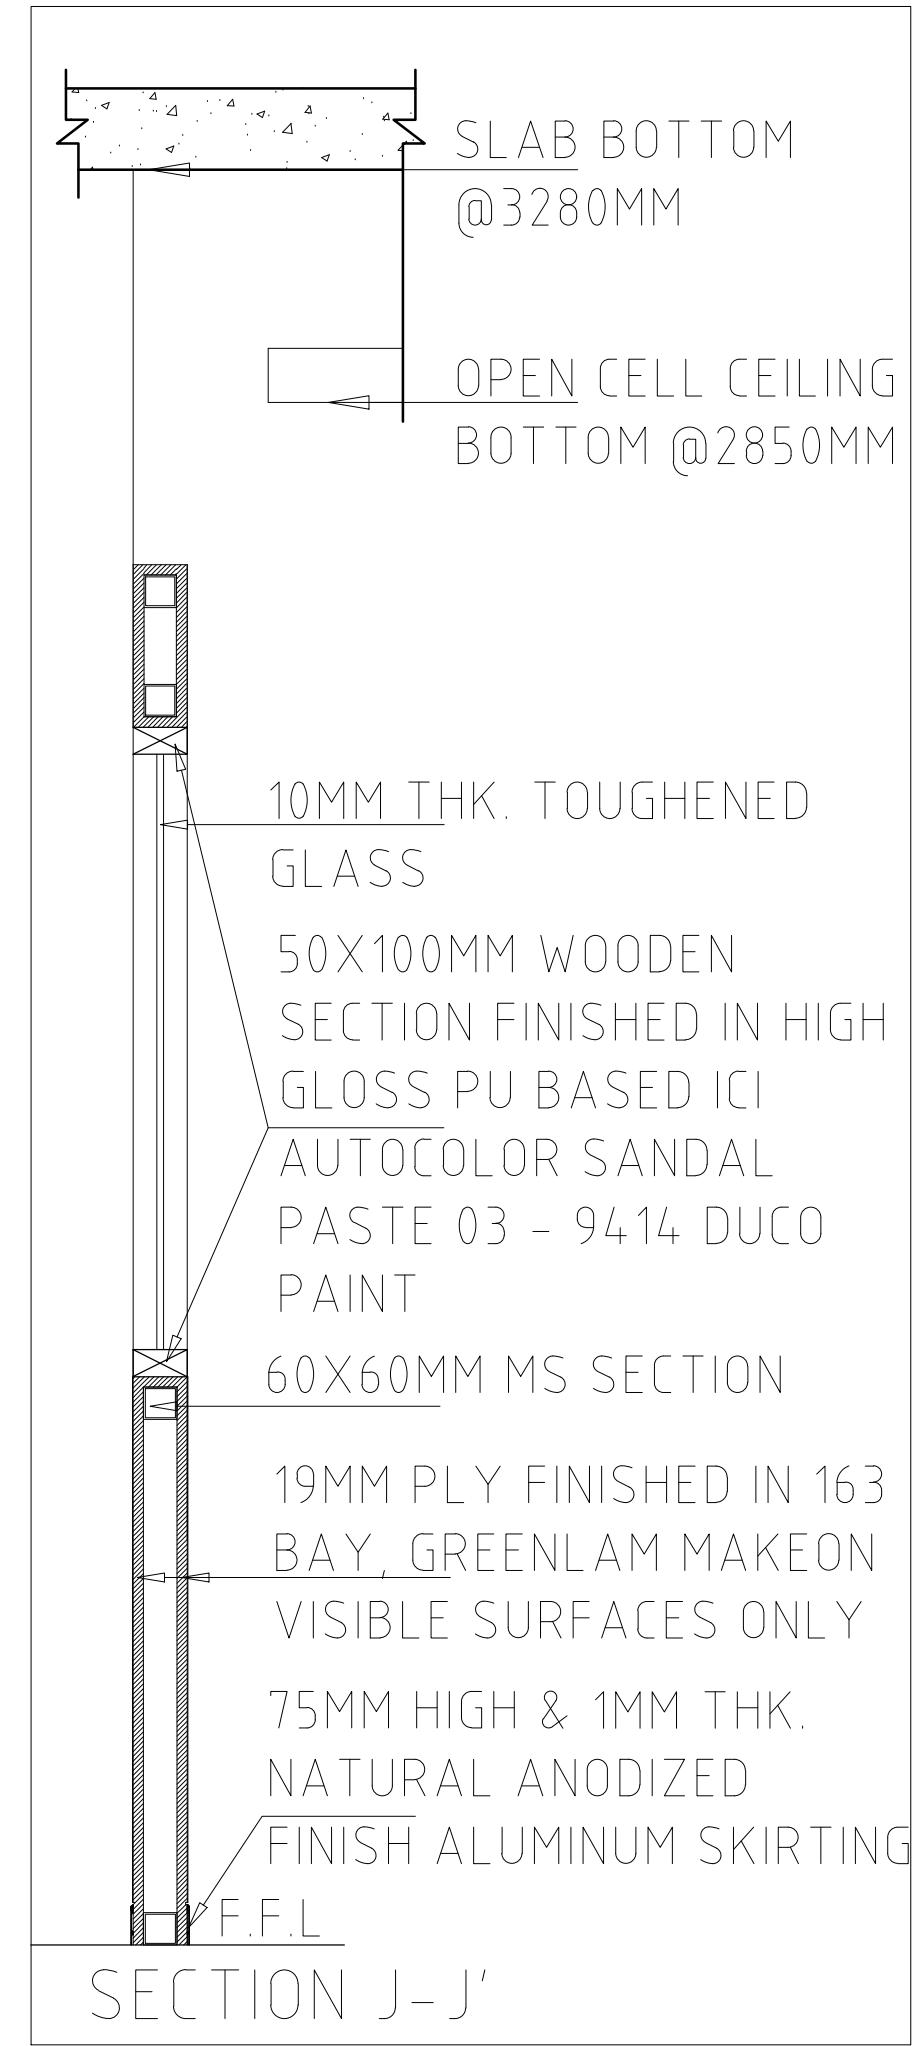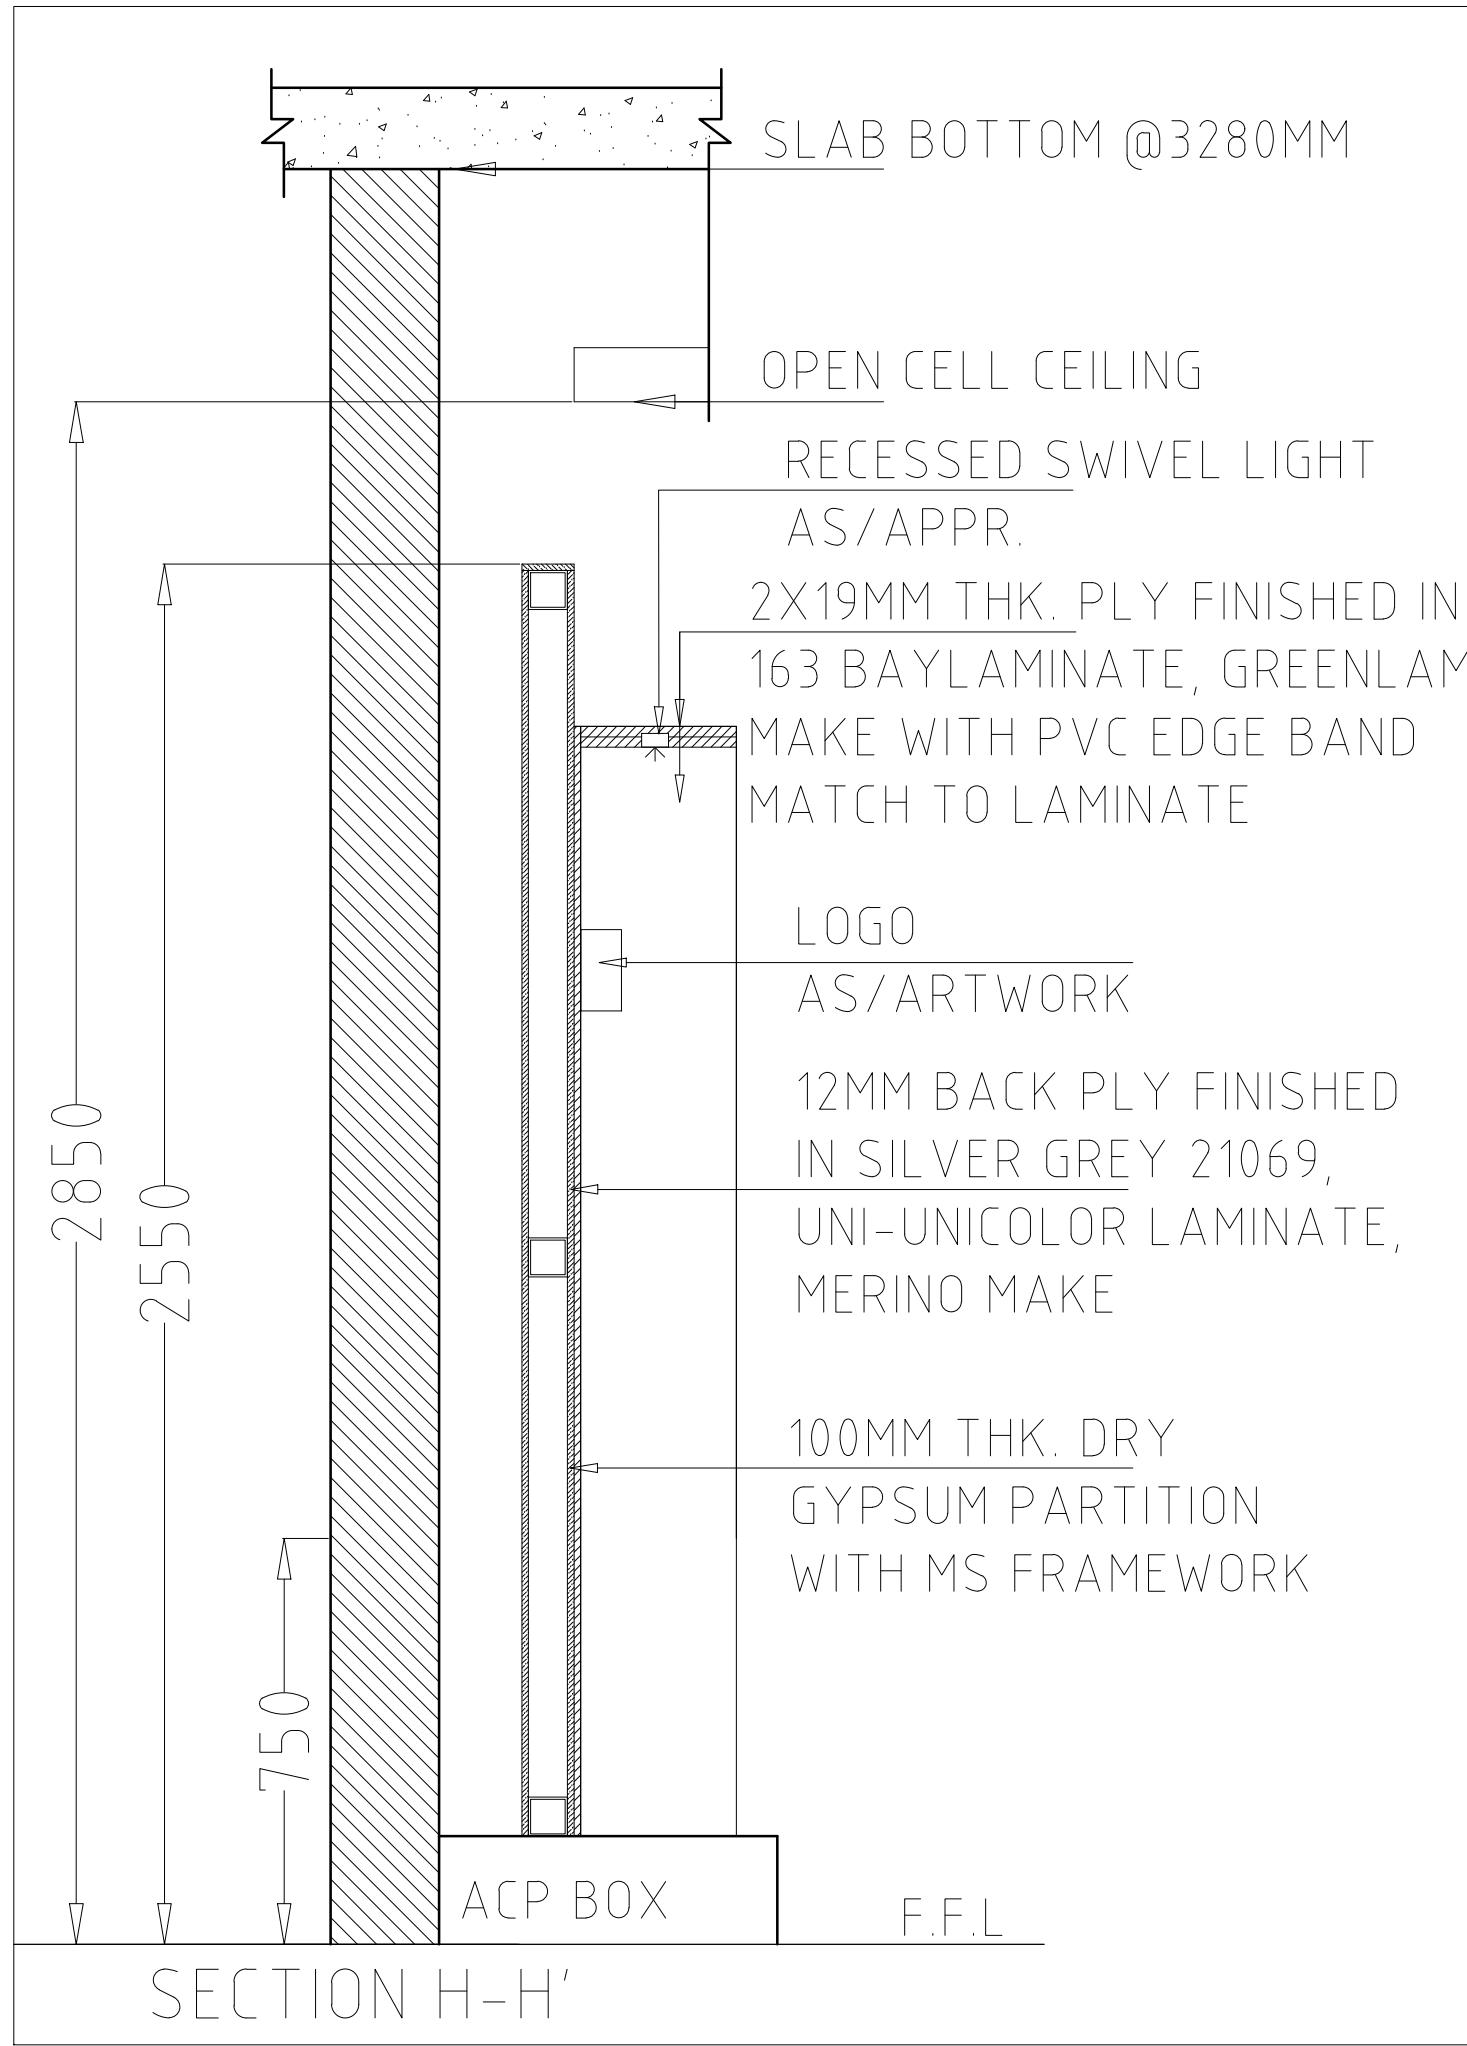

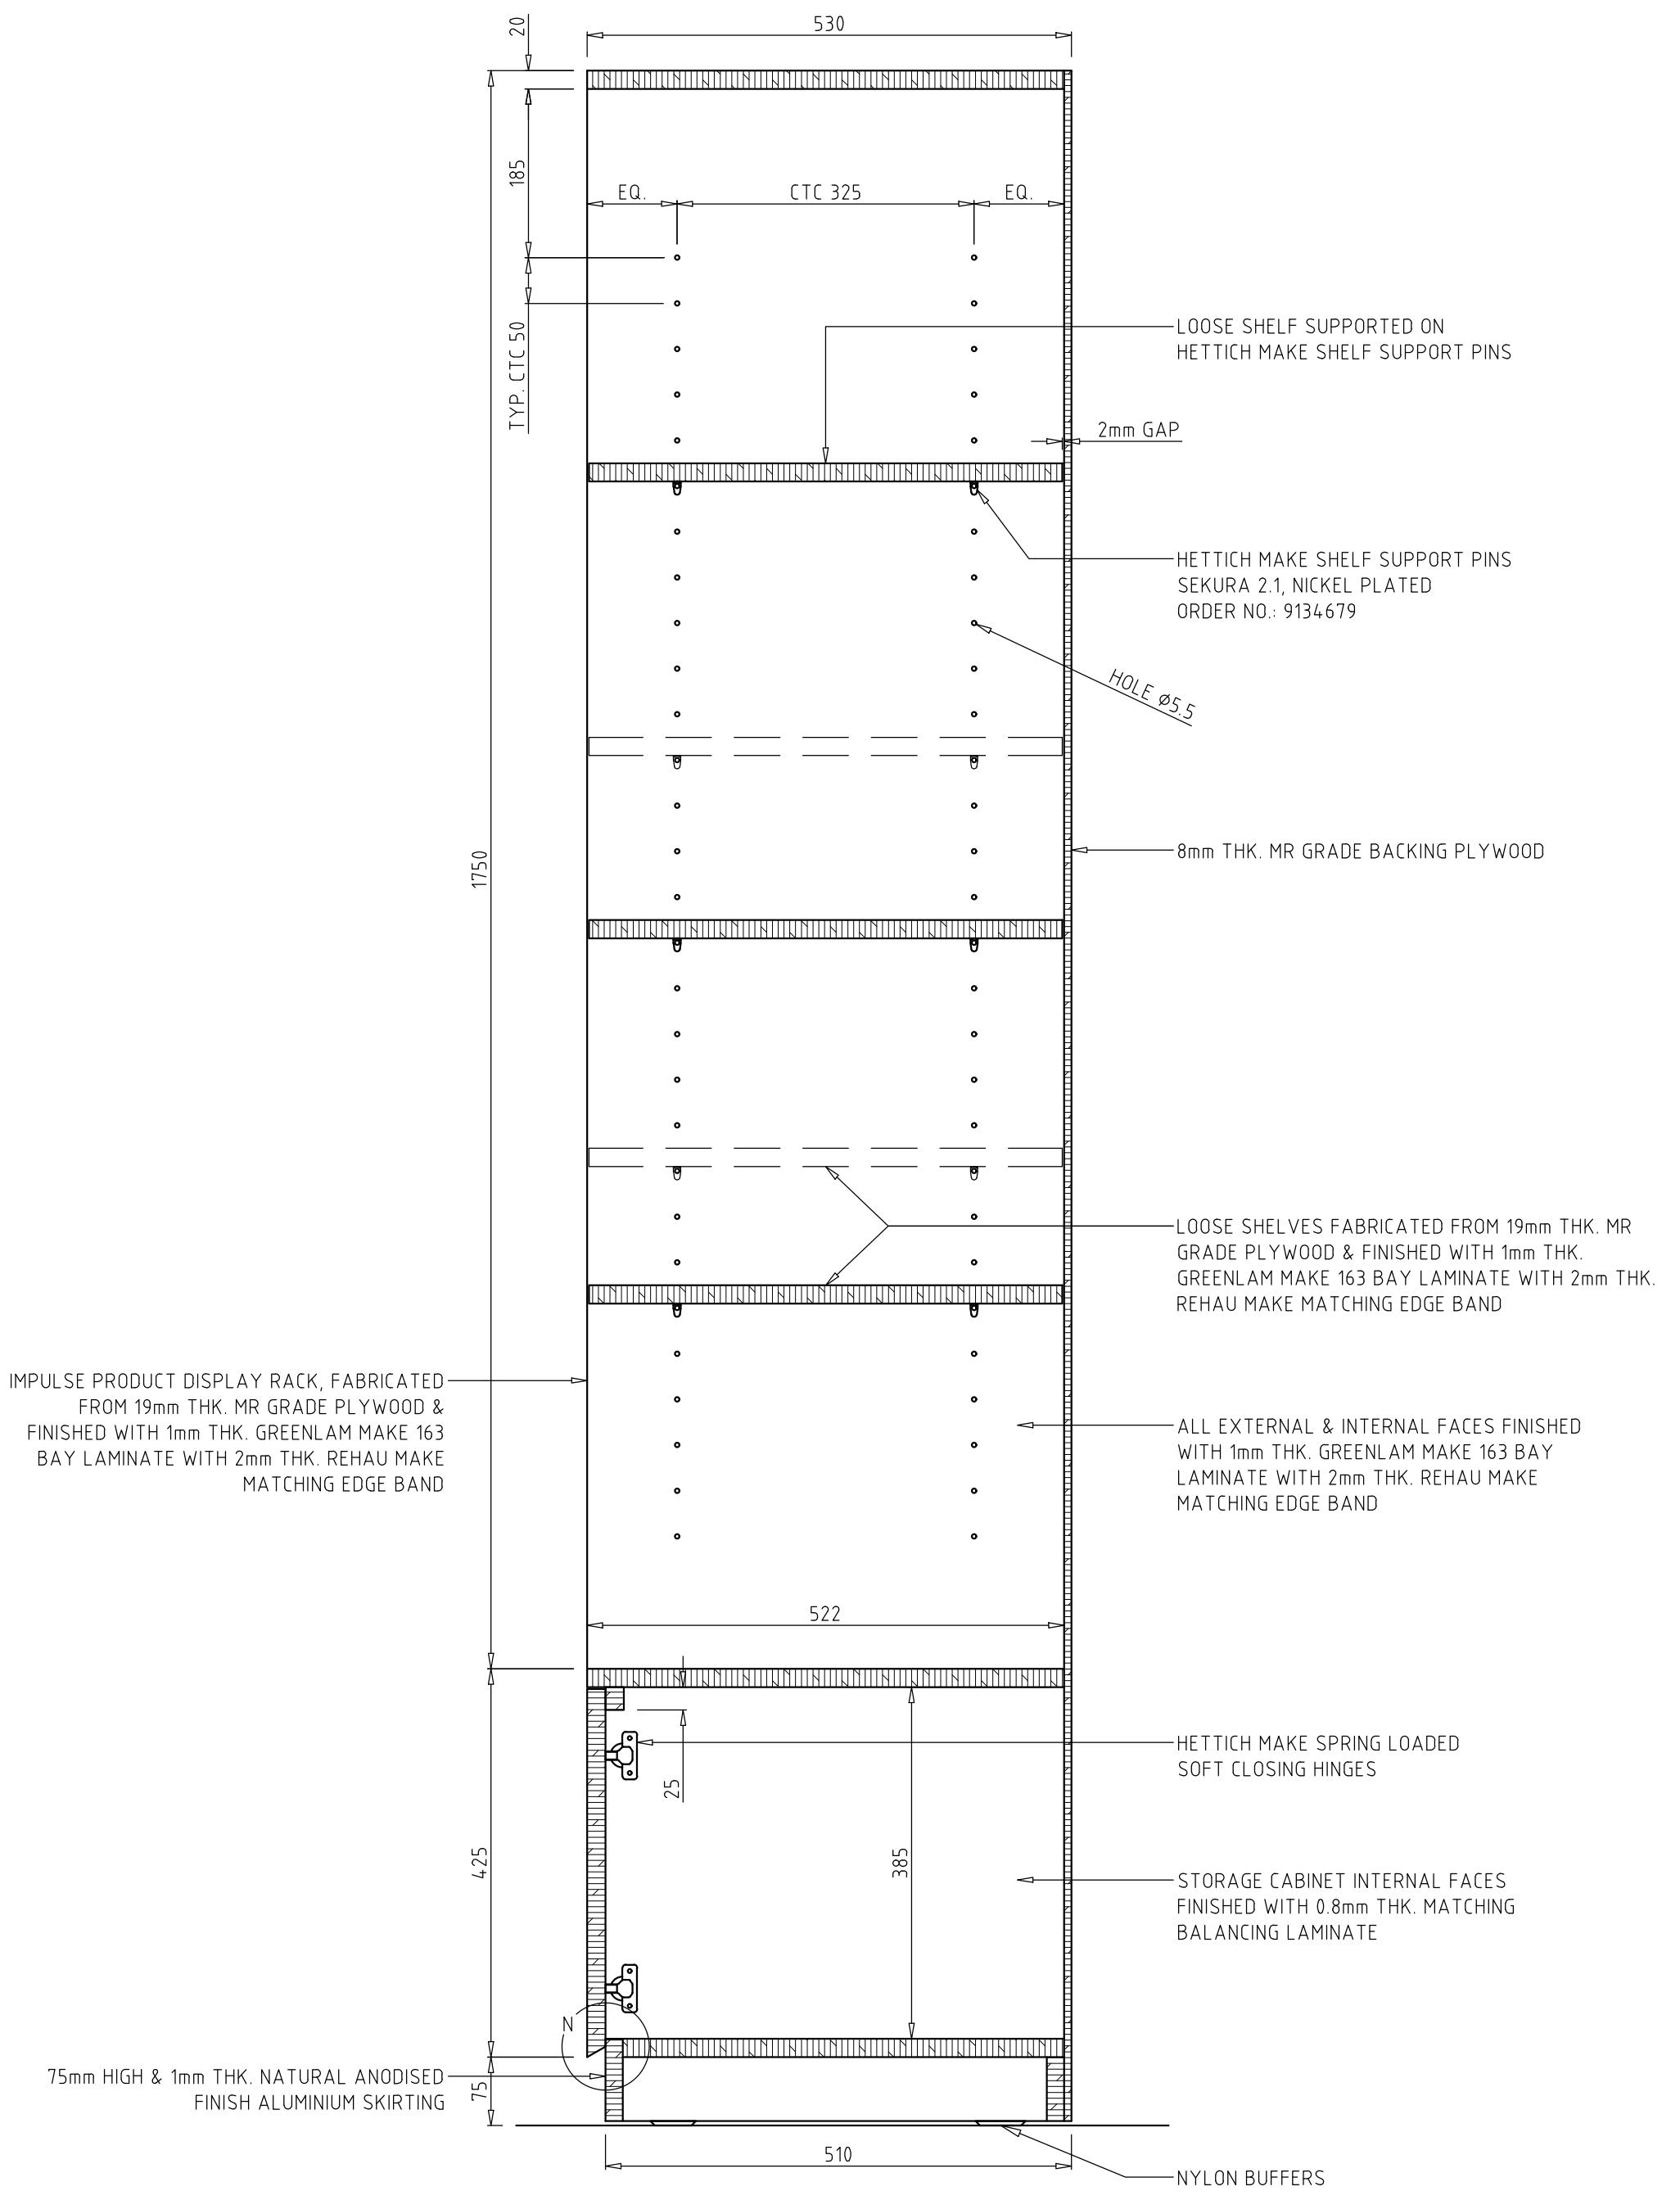

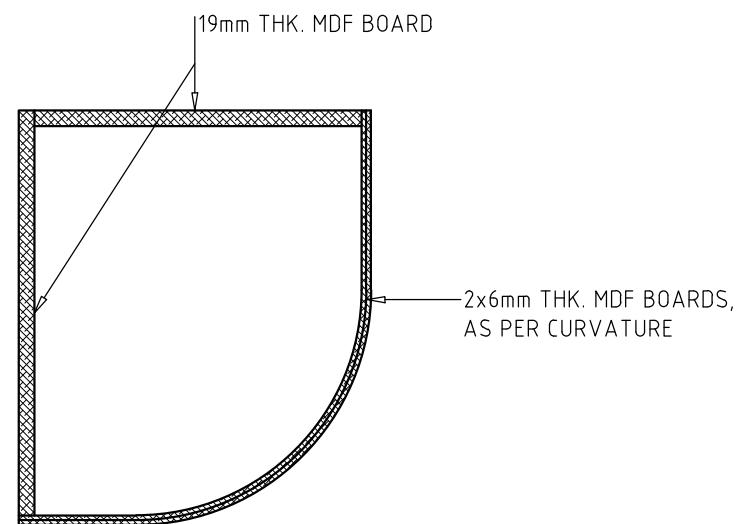
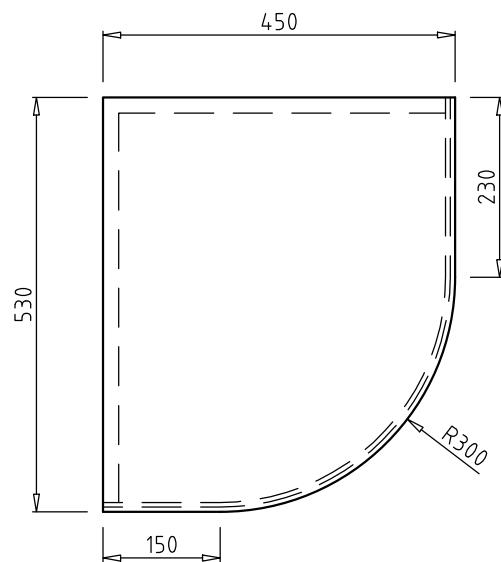


ALL INTERNAL FACES OF DISPLAY
SHELVES TO BE FINISHED WITH 1mm THK.
GREENLAM MAKE 163 BAY LAMINATE

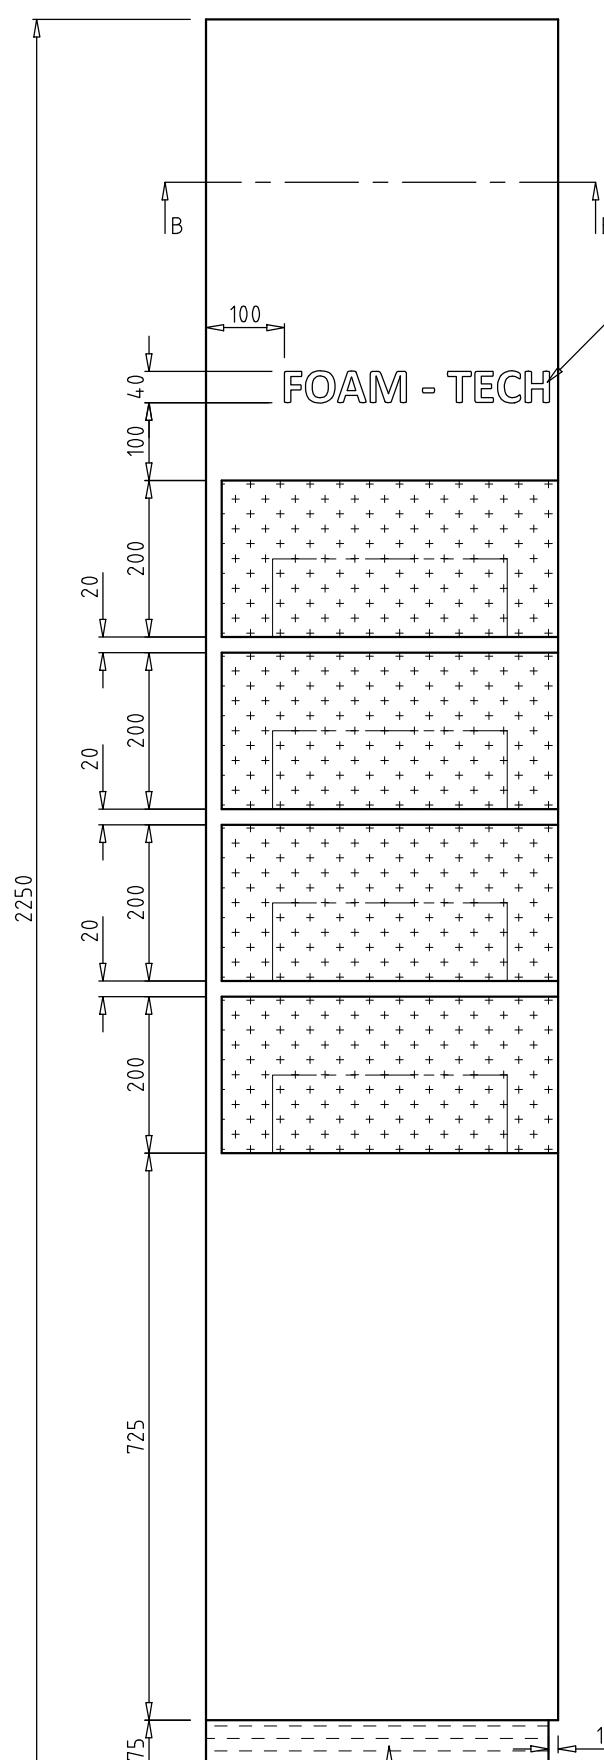

FOAM TECH DISPLAY RACK, FABRICATED FROM
19mm & 6mm THK. MDF BOARDS & FINISHED WITH
HIGH GLOSS PU BASED DUCO PAINT (COLOUR
MATCHED TO SLEEPWELL BRAND COLOUR)


3M MAKE COMPUTER CUT VINYL LETTERS
PASTED ON DUCO PAINTED SURFACE,
FONT AS PER ARTWORK

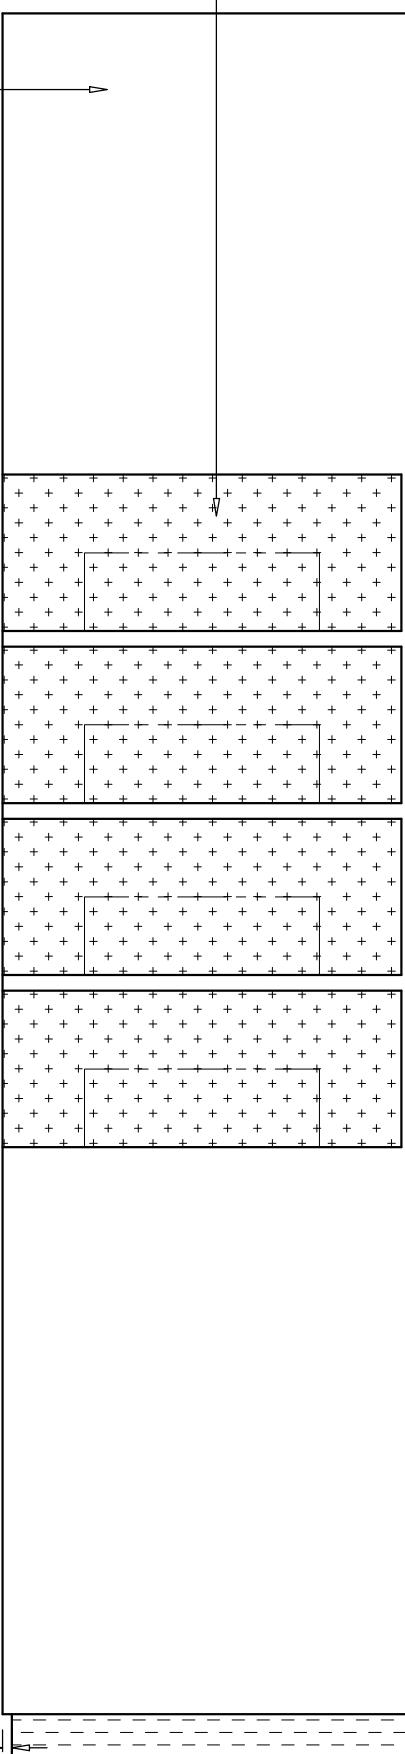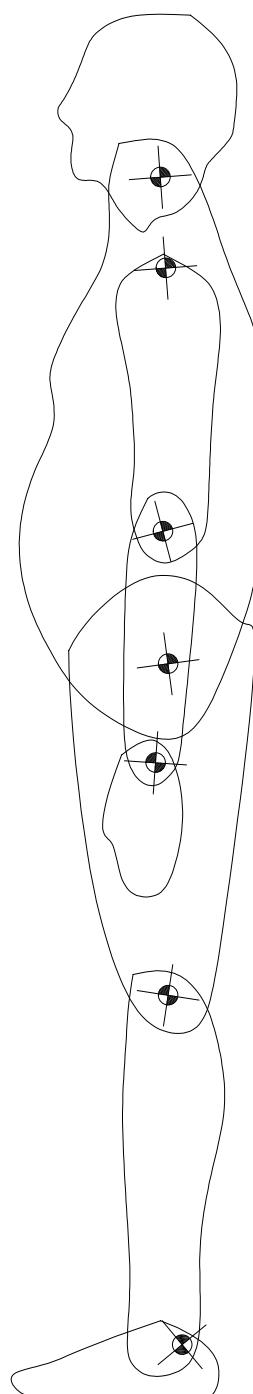


75mm HIGH & 1mm THK. NATURAL
ANODISED FINISH ALUMINIUM SKIRTING

FRONT ELEVATION

SIDE ELEVATION

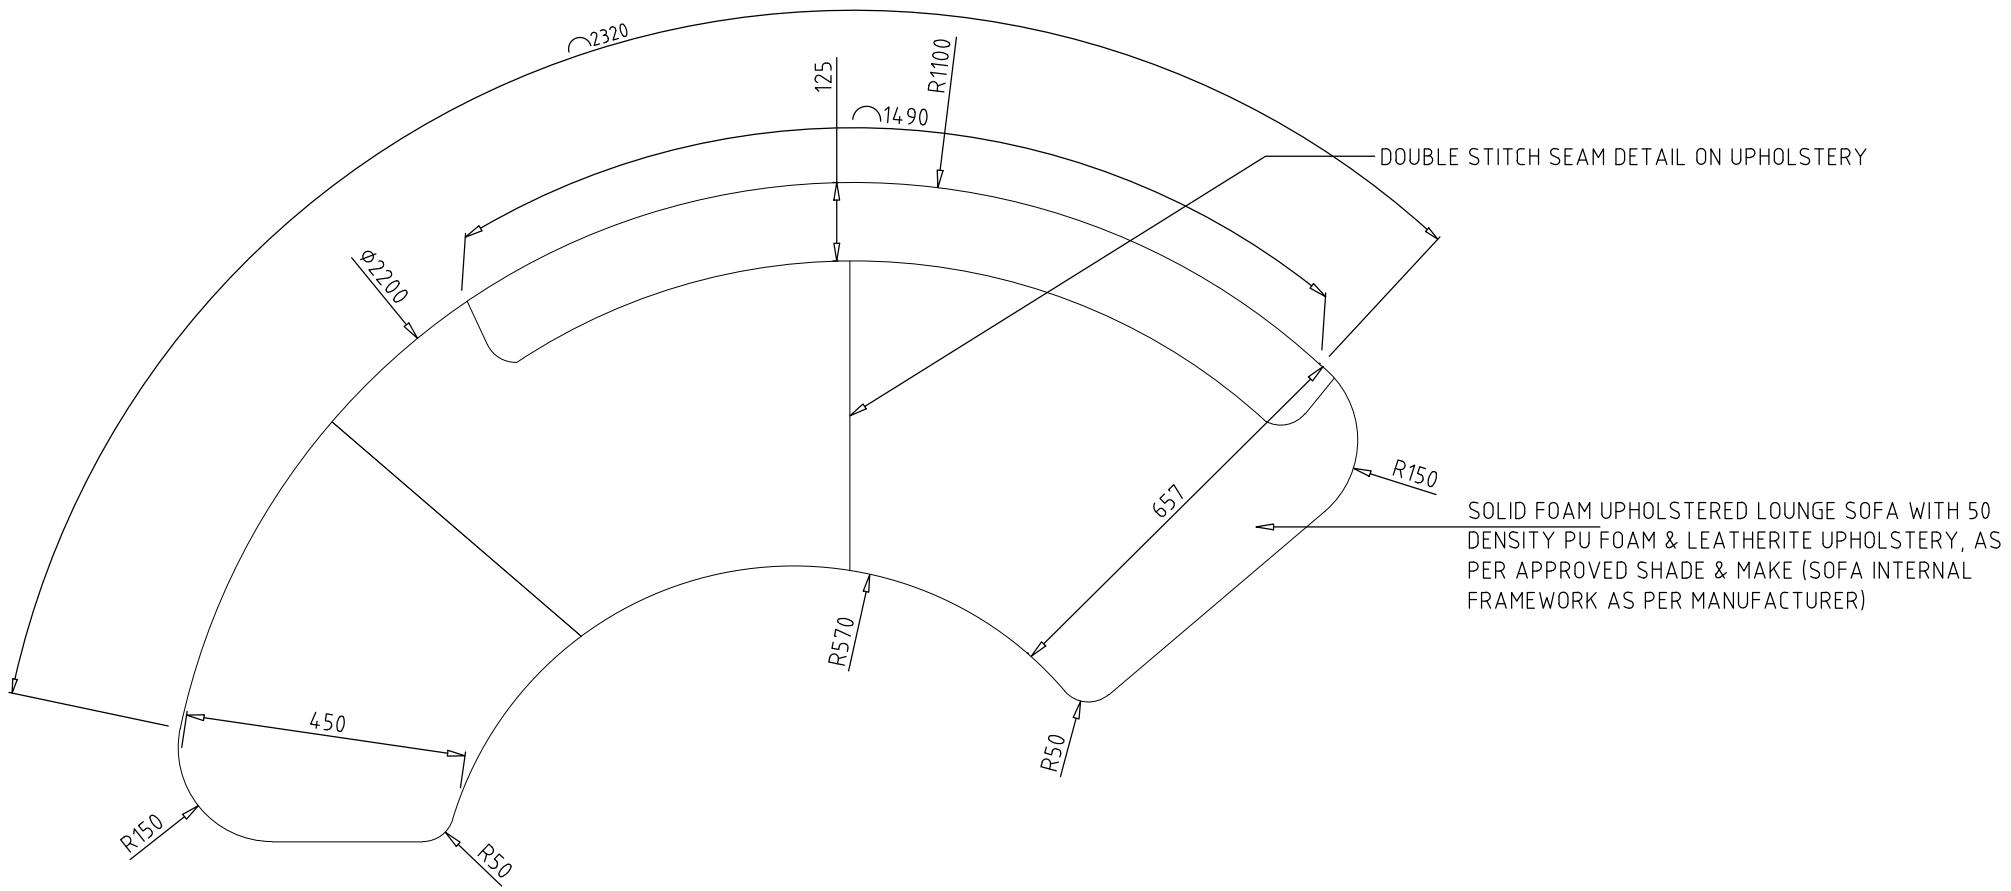


PLAN

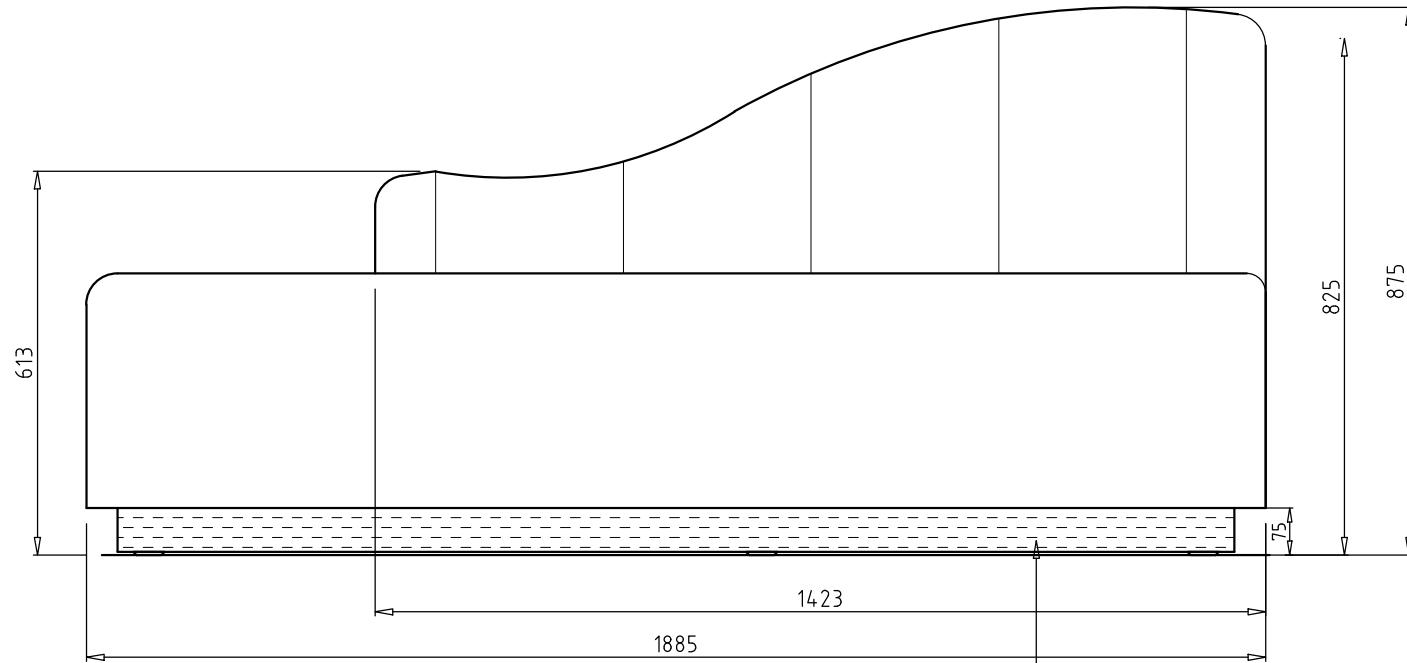


FRONT ELEVATION

75mm HIGH & 1mm THK. NATURAL
ANODISED FINISH ALUMINIUM SKIRTING

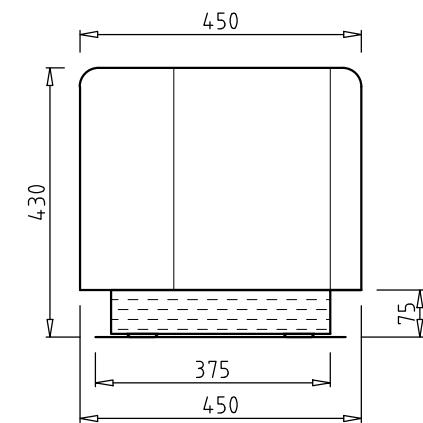



SIDE ELEVATION A

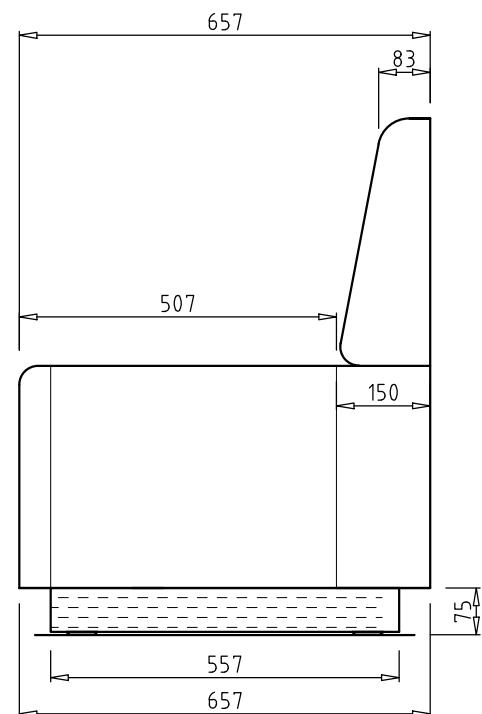



SIDE ELEVATION B

LOUNGE CENTER TABLE, FABRICATED
FROM 19mm & 6mm THK. MDF & FINISHED
WITH HIGH GLOSS PU BASED ICI
AUTOCOLOR WHITE 03-0101 DUCO PAINT

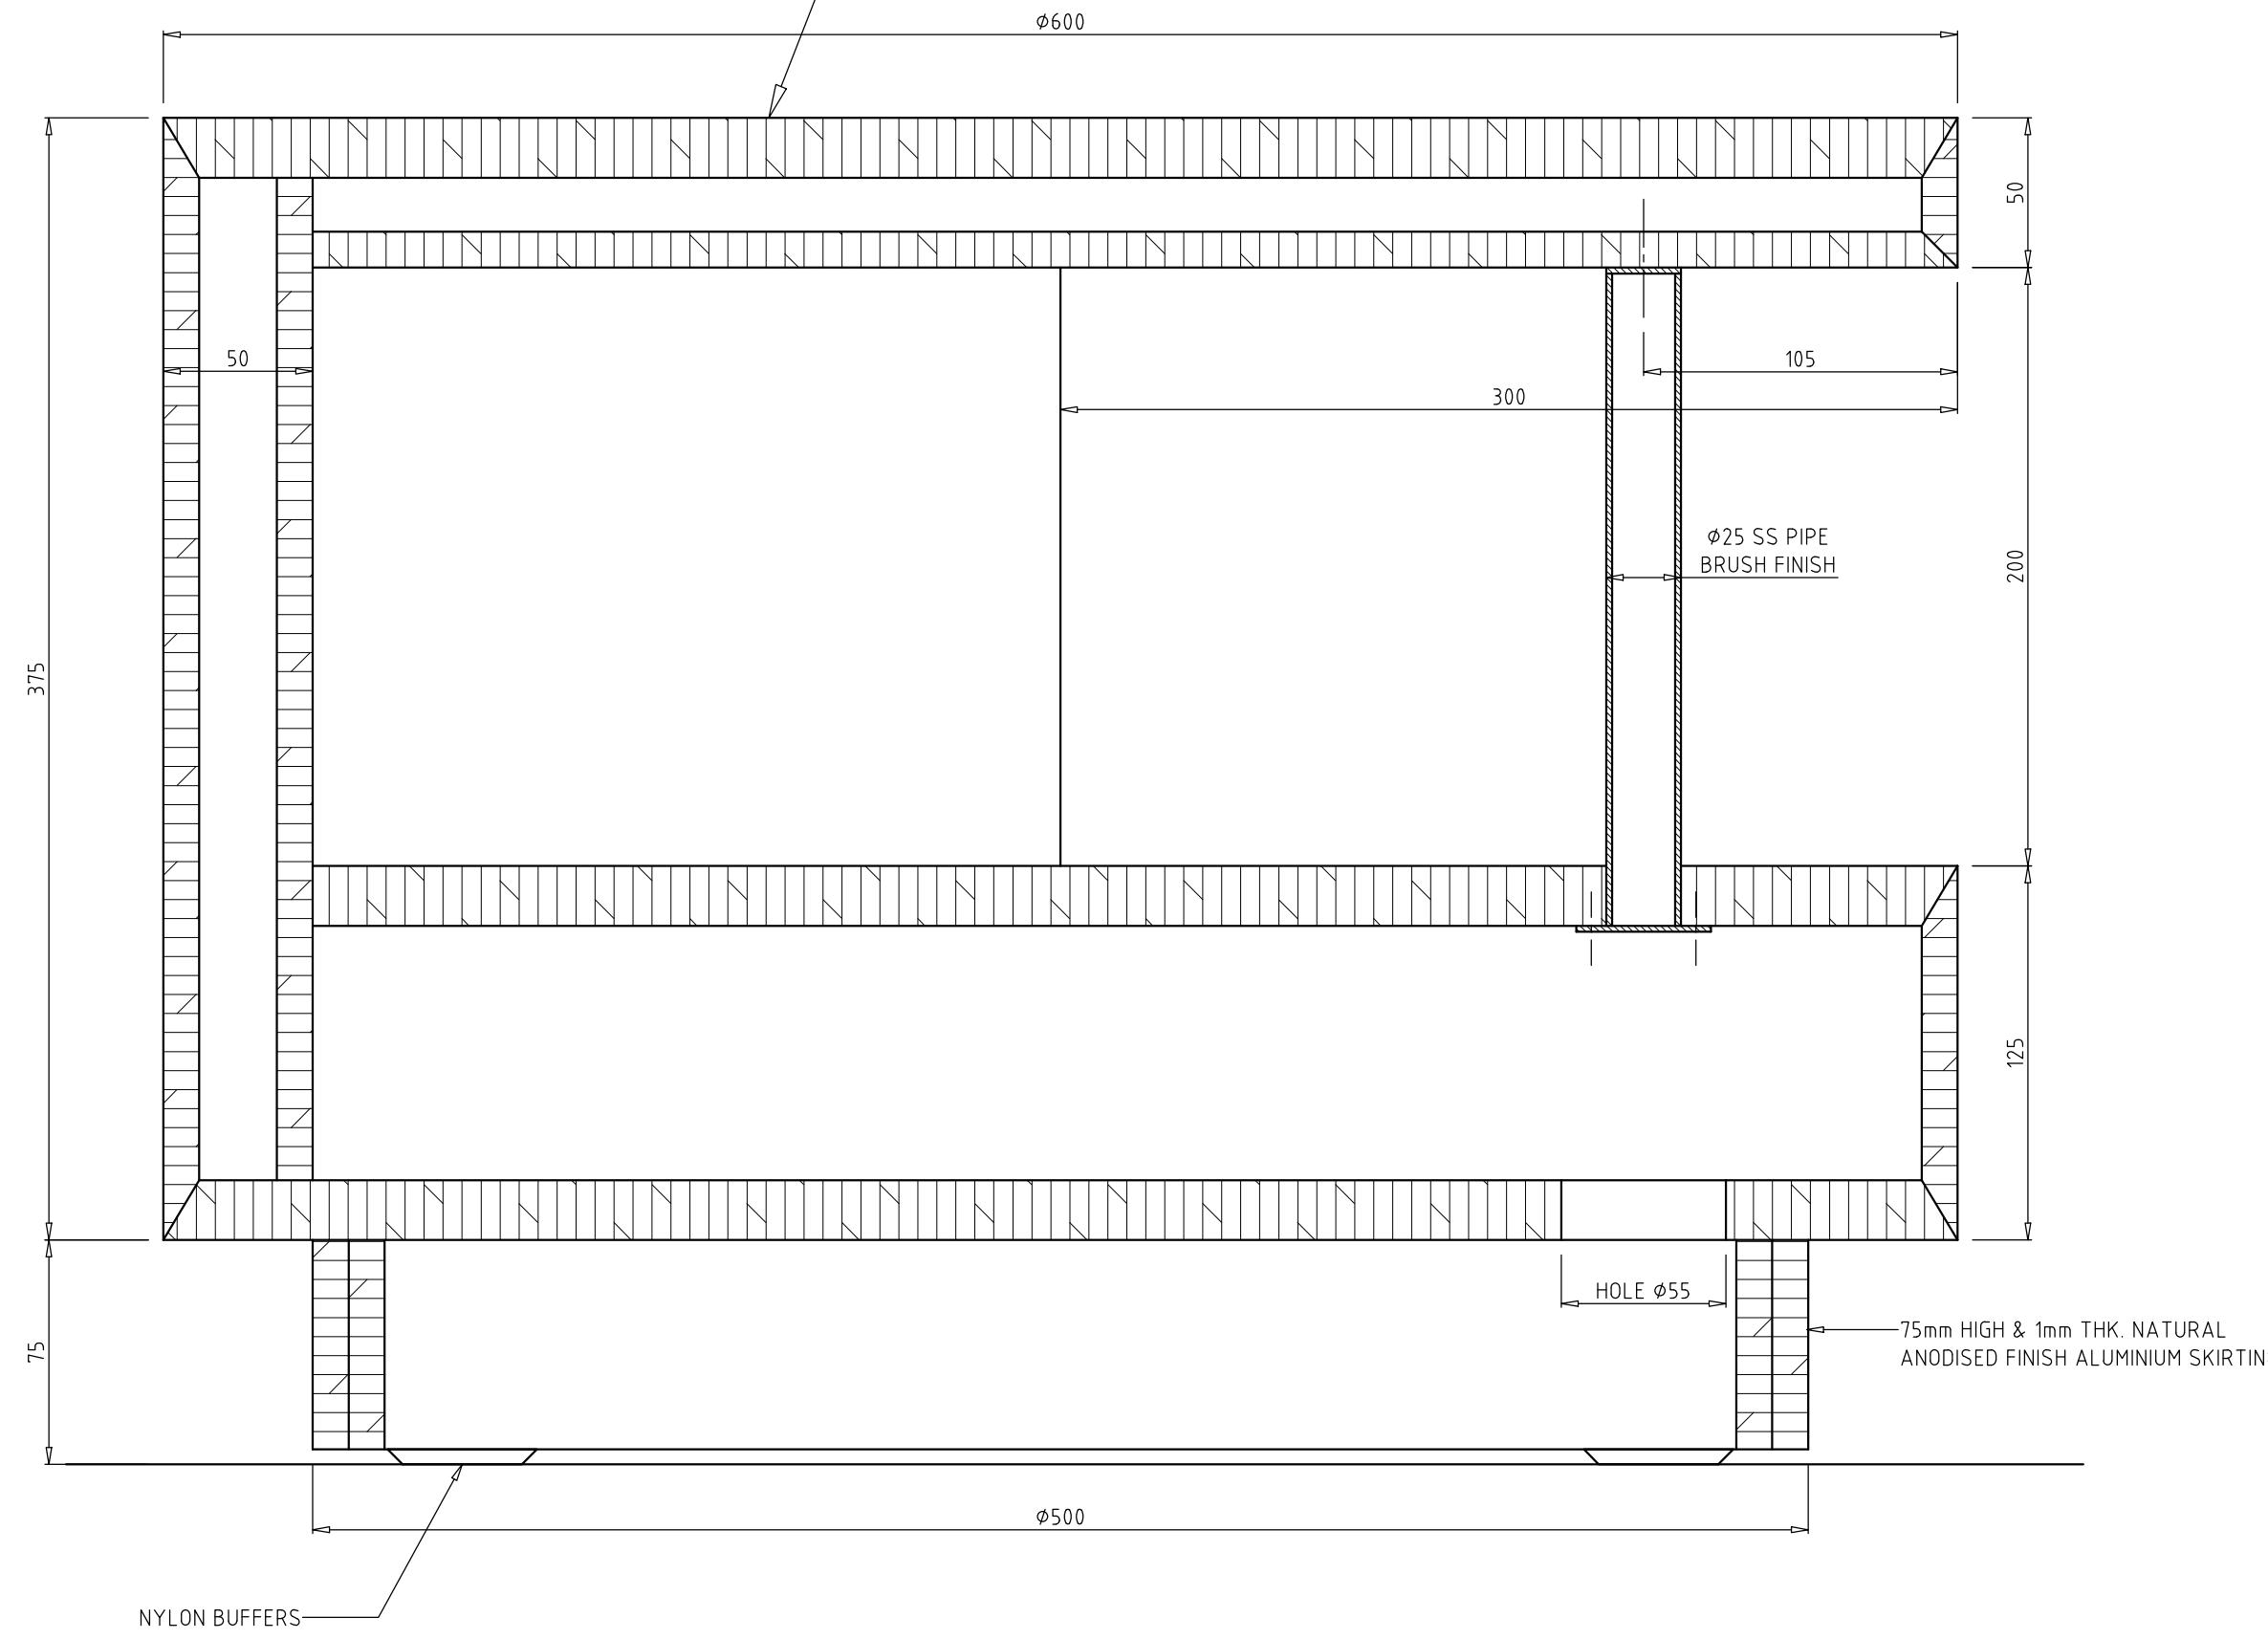

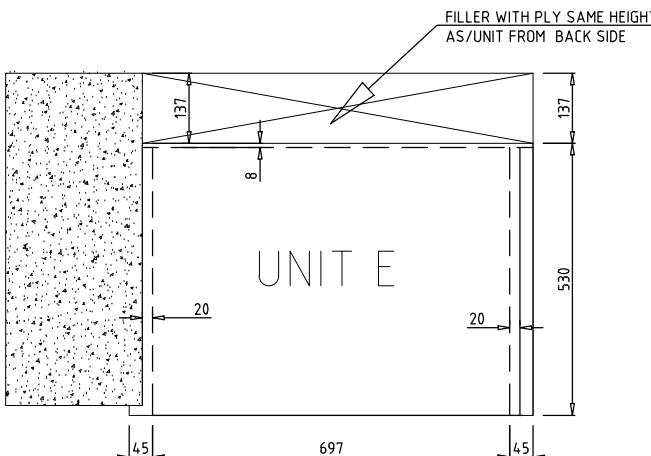




IMPULSE PRODUCT DISPLAY RACK - E,
FABRICATED FROM 19mm THK. MR GRADE
PLYWOOD & FINISHED WITH 1mm THK. GREENLAM
MAKE 163 BAY LAMINATE WITH 2mm THK. REHAU
MAKE MATCHING EDGE BAND

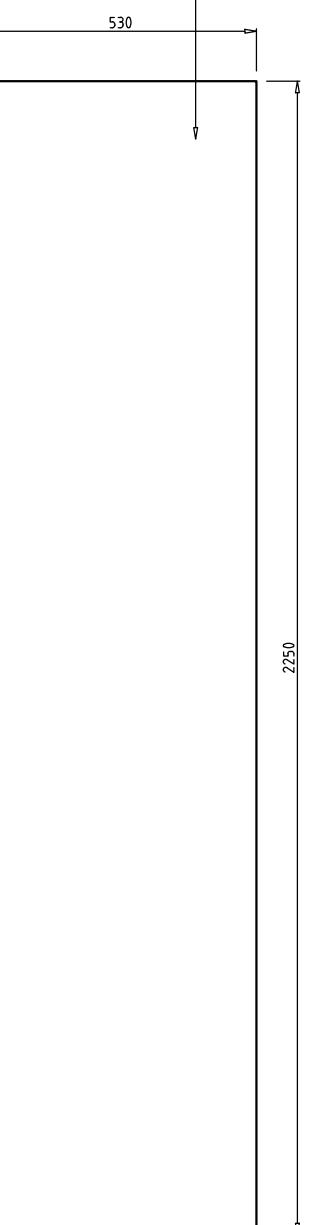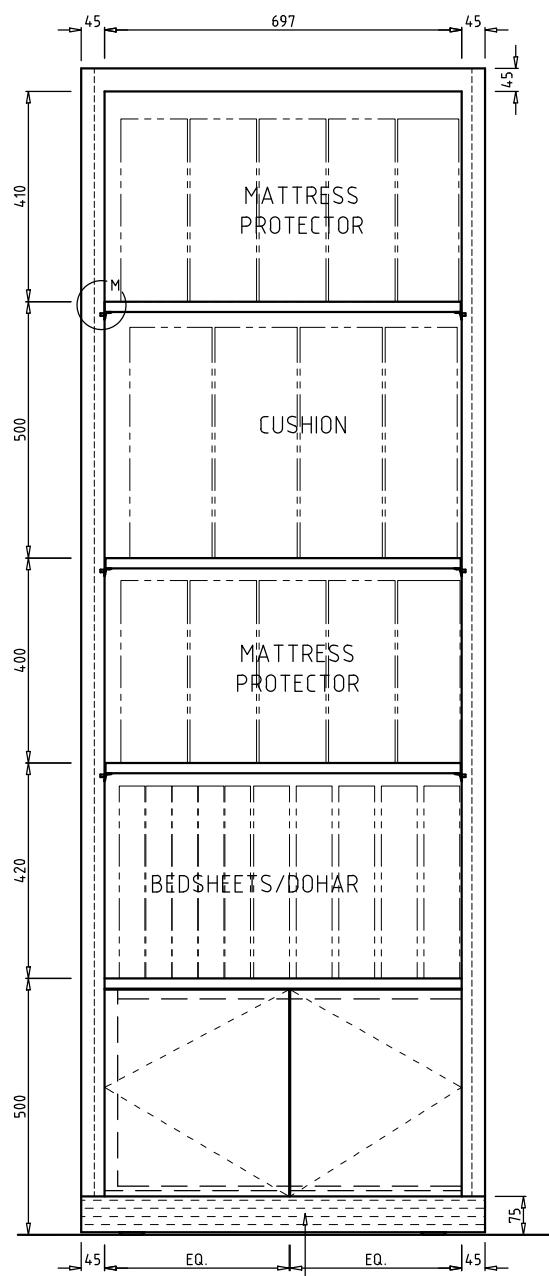


IMPULSE PRODUCT DISPLAY RACK, FABRICATED
FROM 19mm THK. MR GRADE PLYWOOD &
FINISHED WITH 1mm THK. GREENLAM MAKE 163
BAY LAMINATE WITH 2mm THK. REHAU MAKE
MATCHING EDGE BAND

75mm HIGH & 1mm THK. 163 BAY LAMINATE
GREEN LAME MAKE

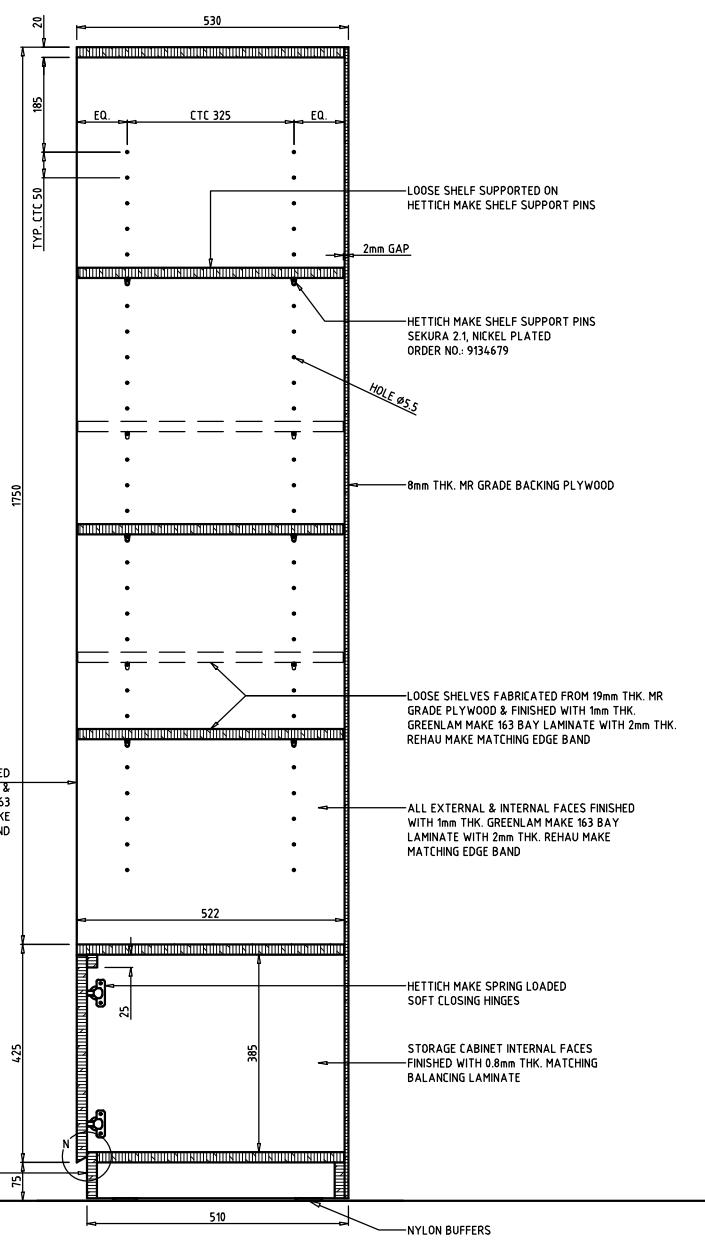


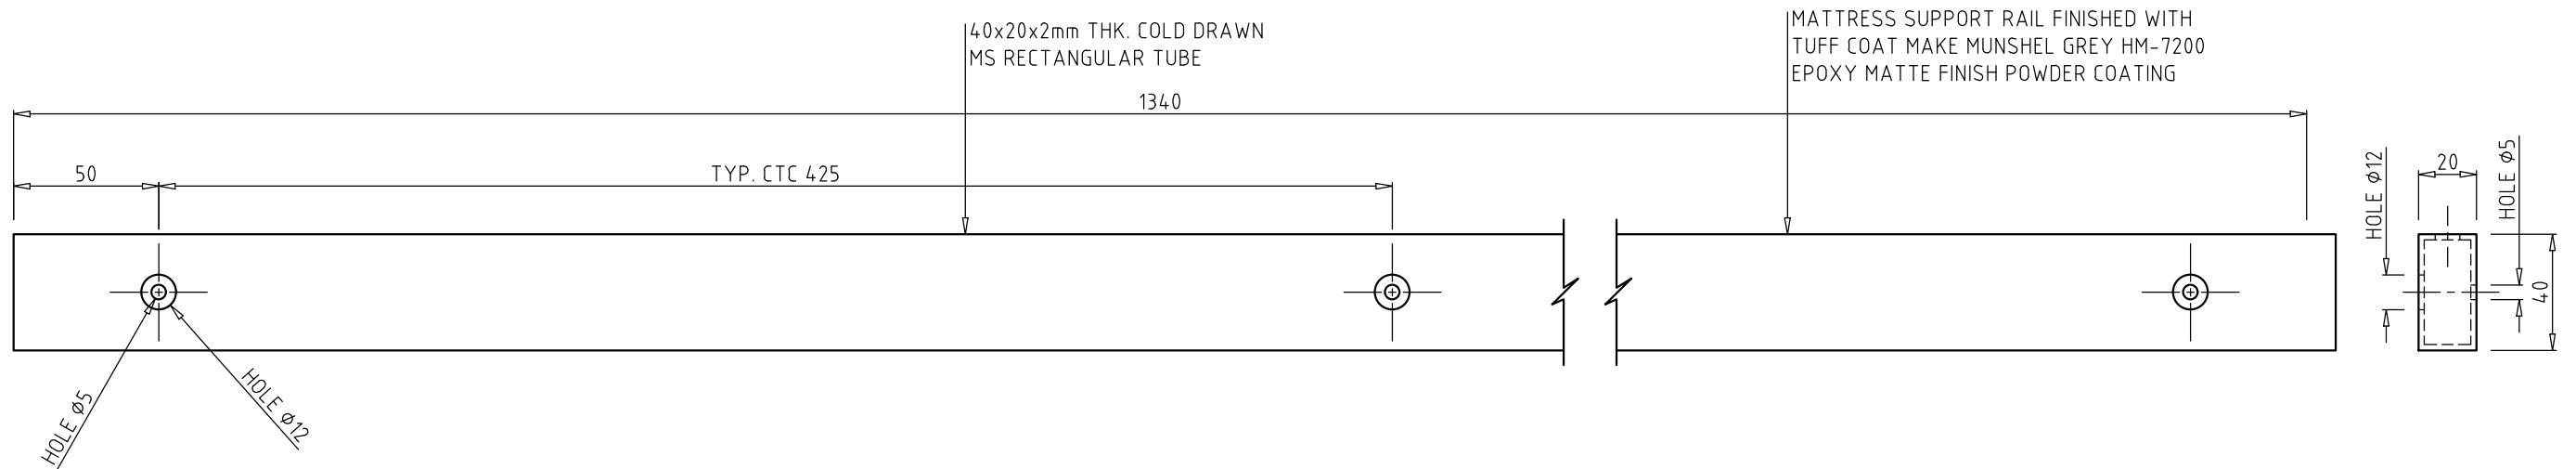
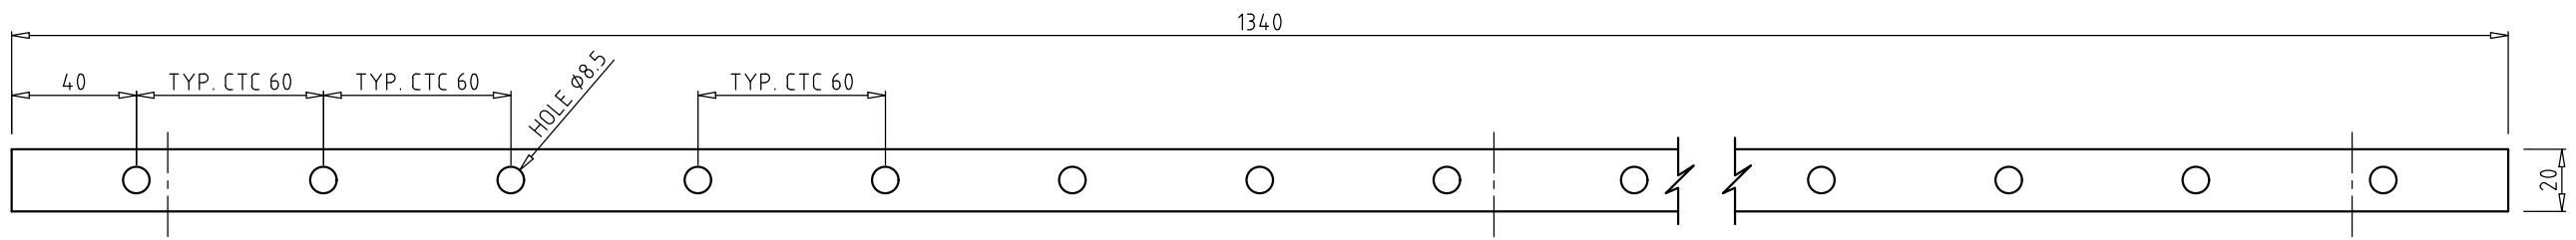


MATTRESS SUPPORT RAIL

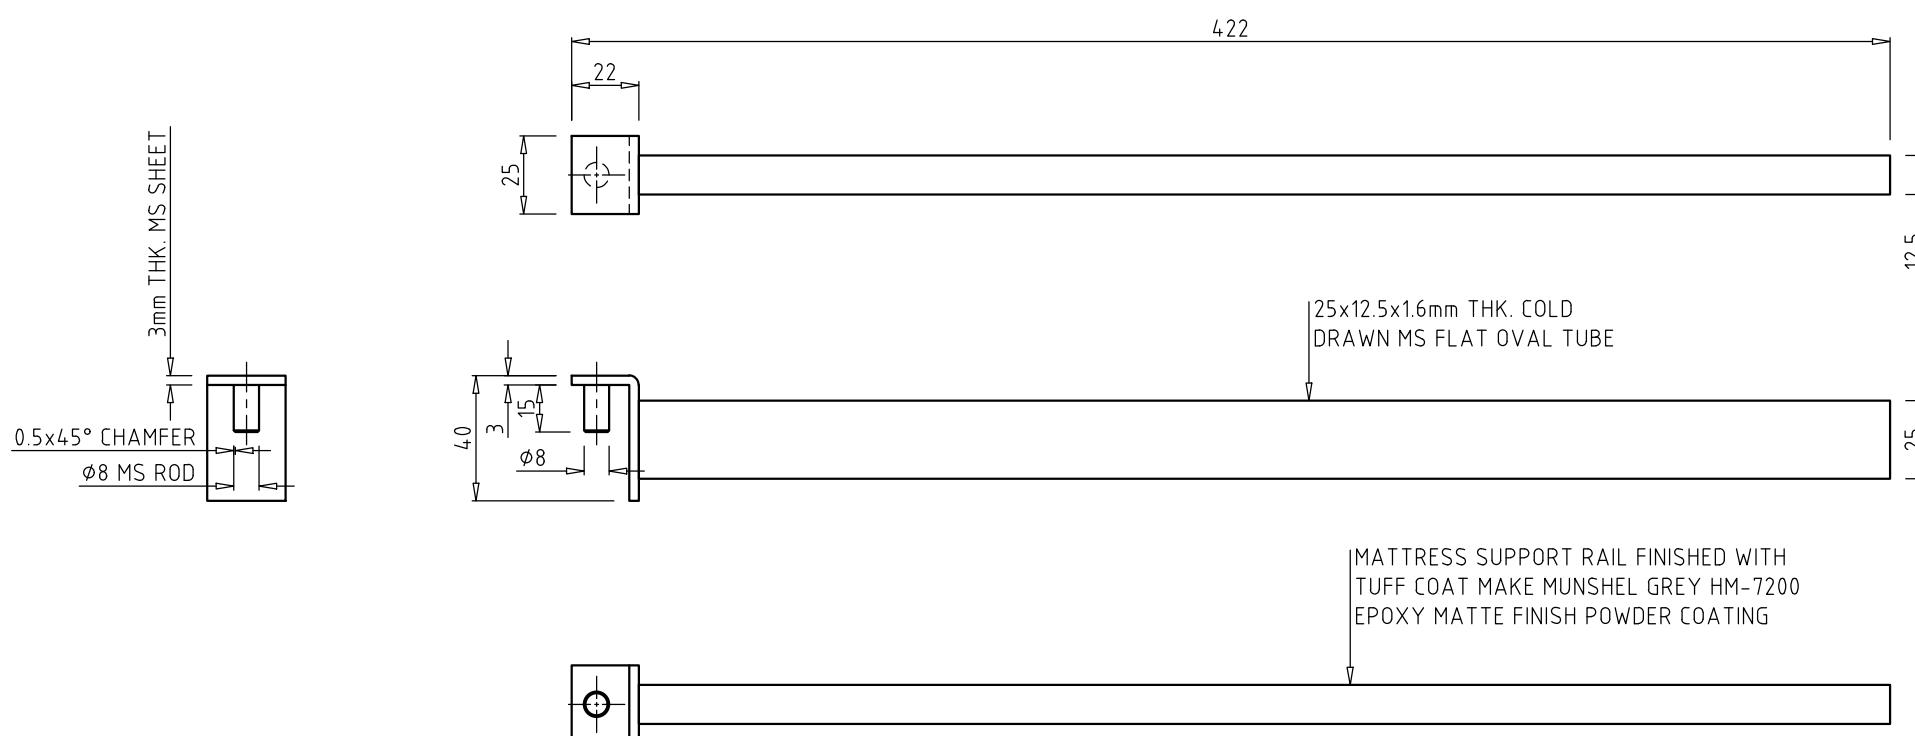


MATTRESS SUPPORT BRACKET

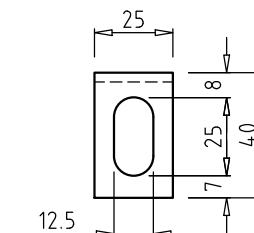

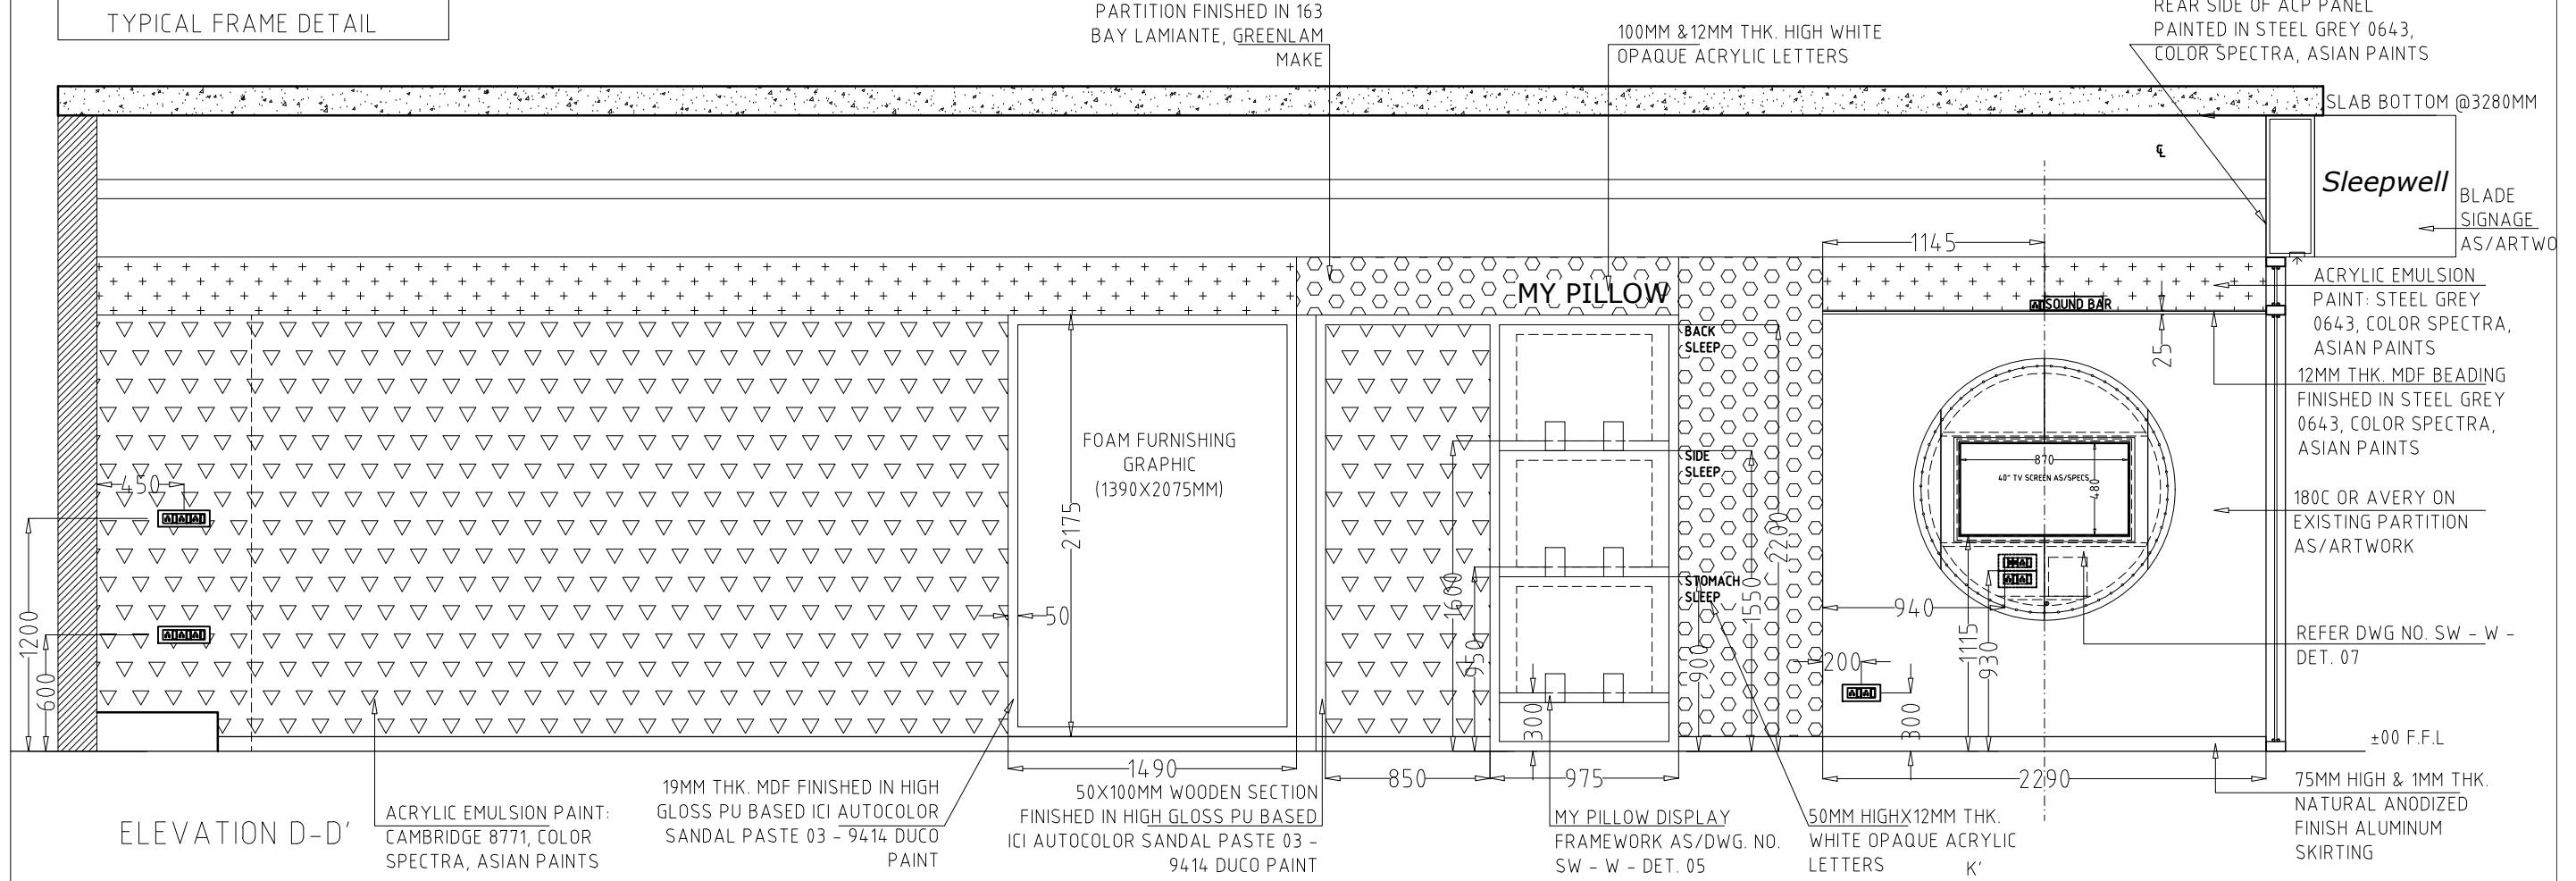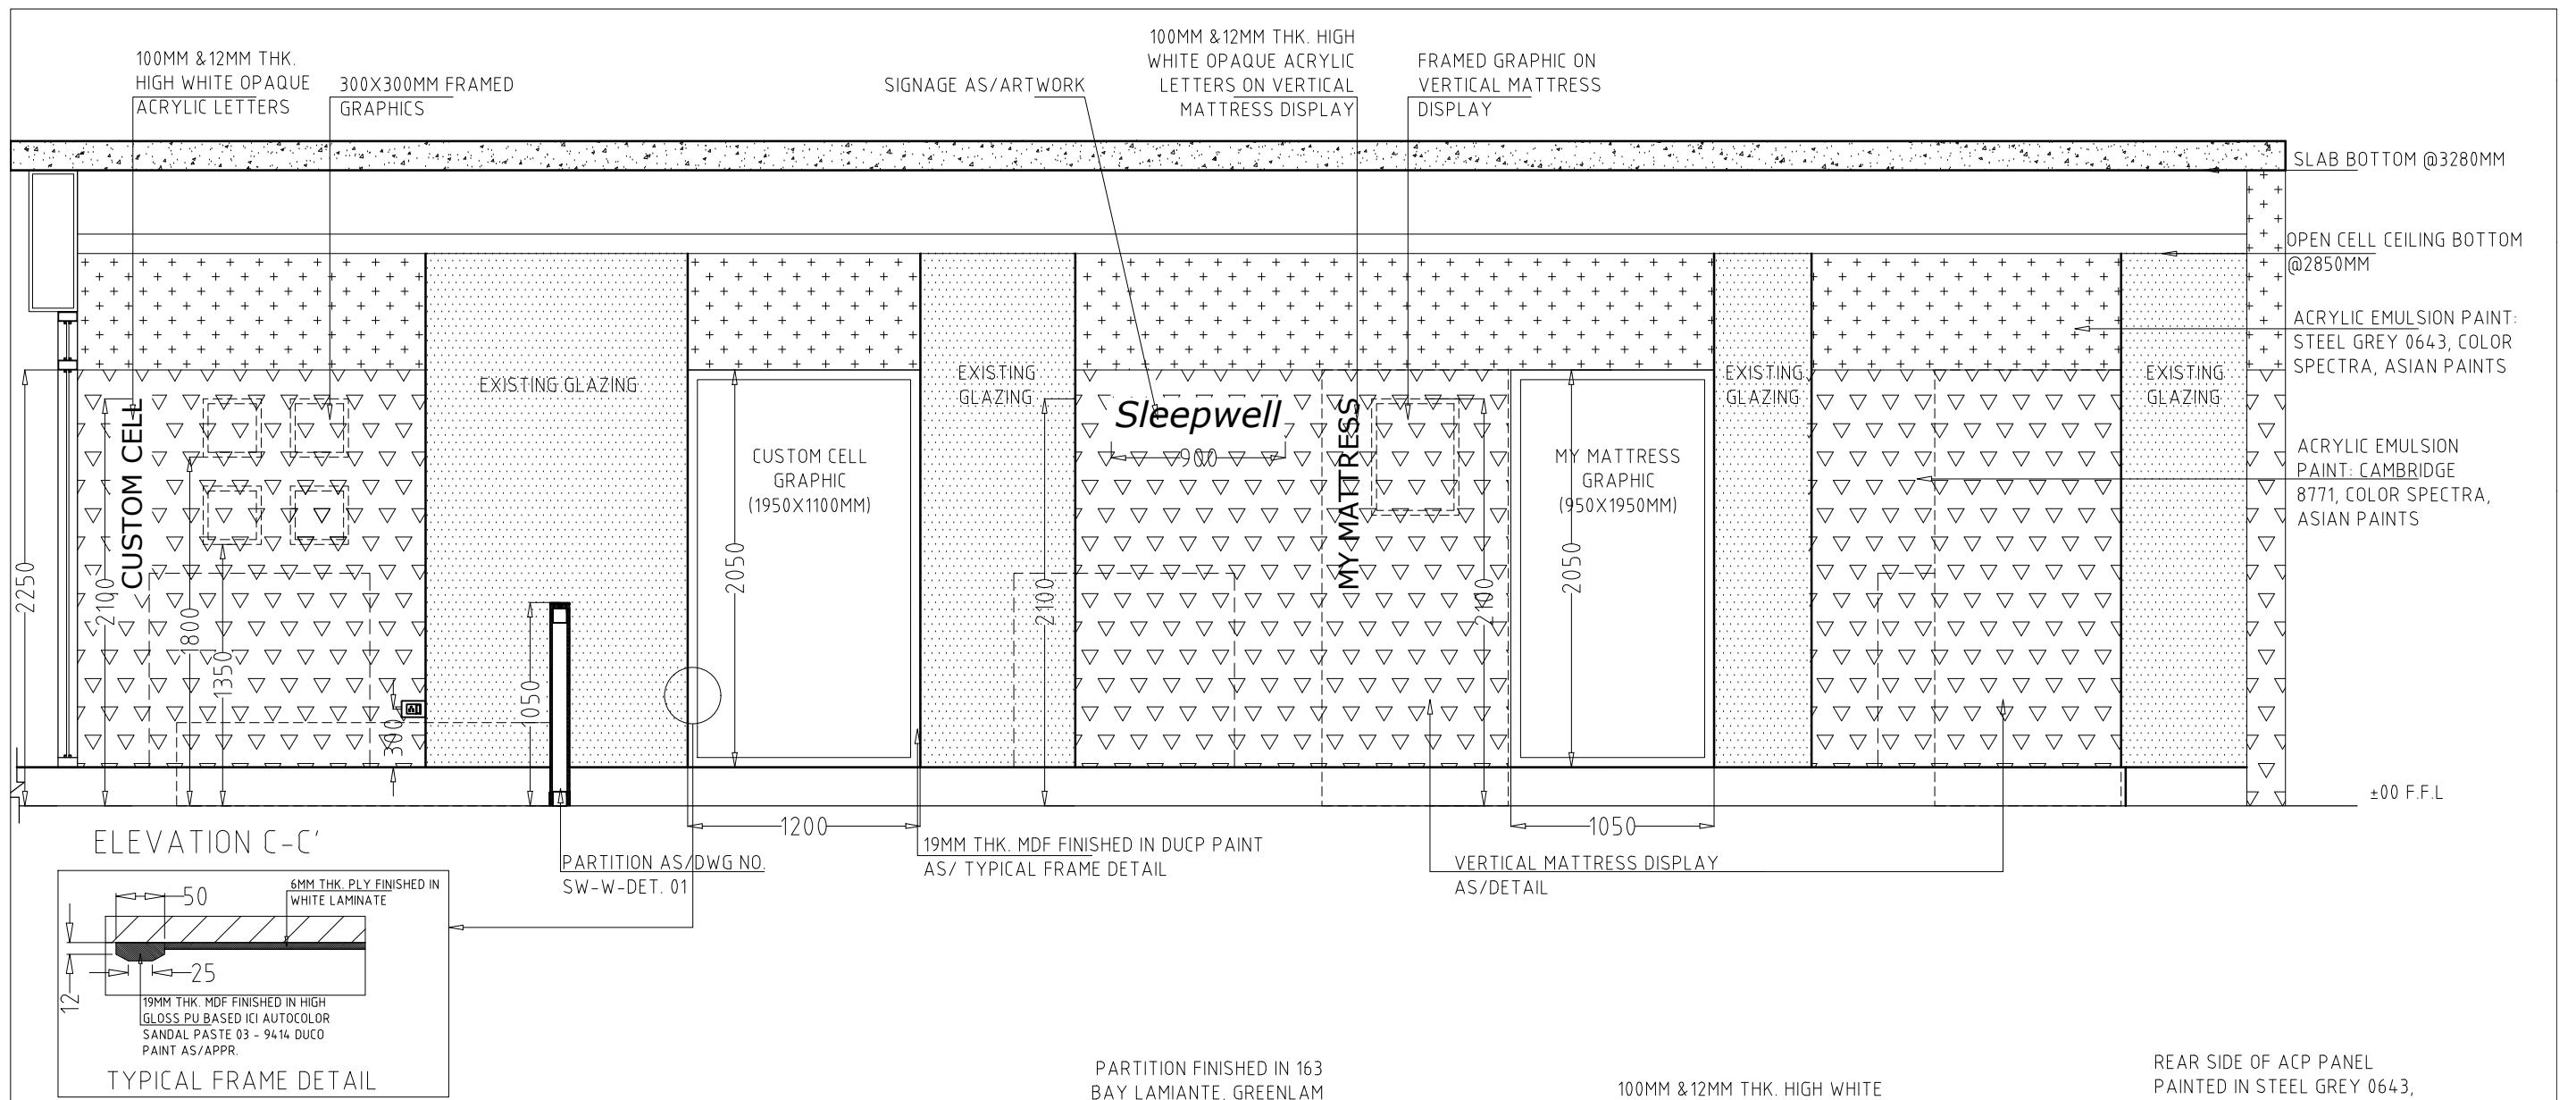

Sleepwell

Gallery

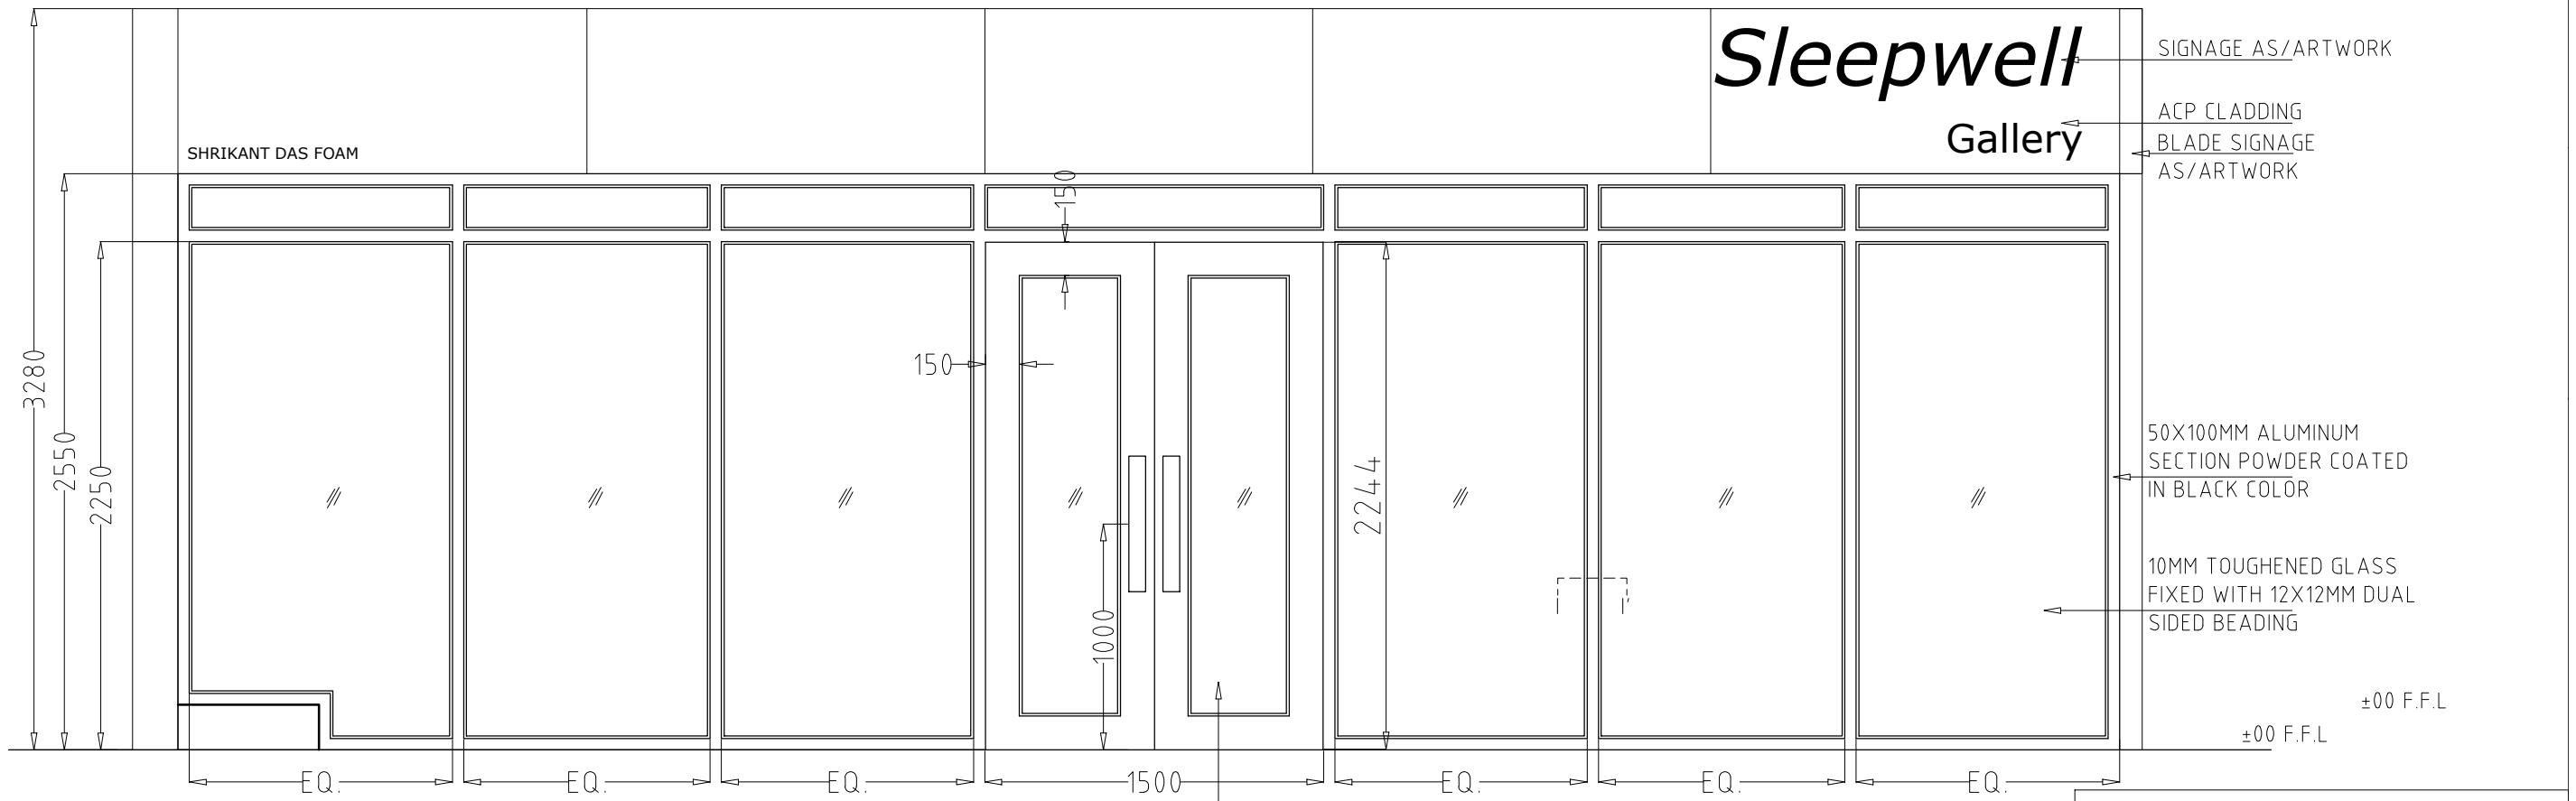

40MM THK. SEASONED OAK WOOD DOOR FINISHED WITH CLEAR PU COAT AS/APPR. POLISH FIXED ON FLOOR SPRING, OZONE MAKE AS/DWG NO. SW-W -DET. 04

