



CONSTRUCTION DRAWINGS




INTERIOR DESIGN | ARCHITECTURE

Paytm

Corporate Workplace Design

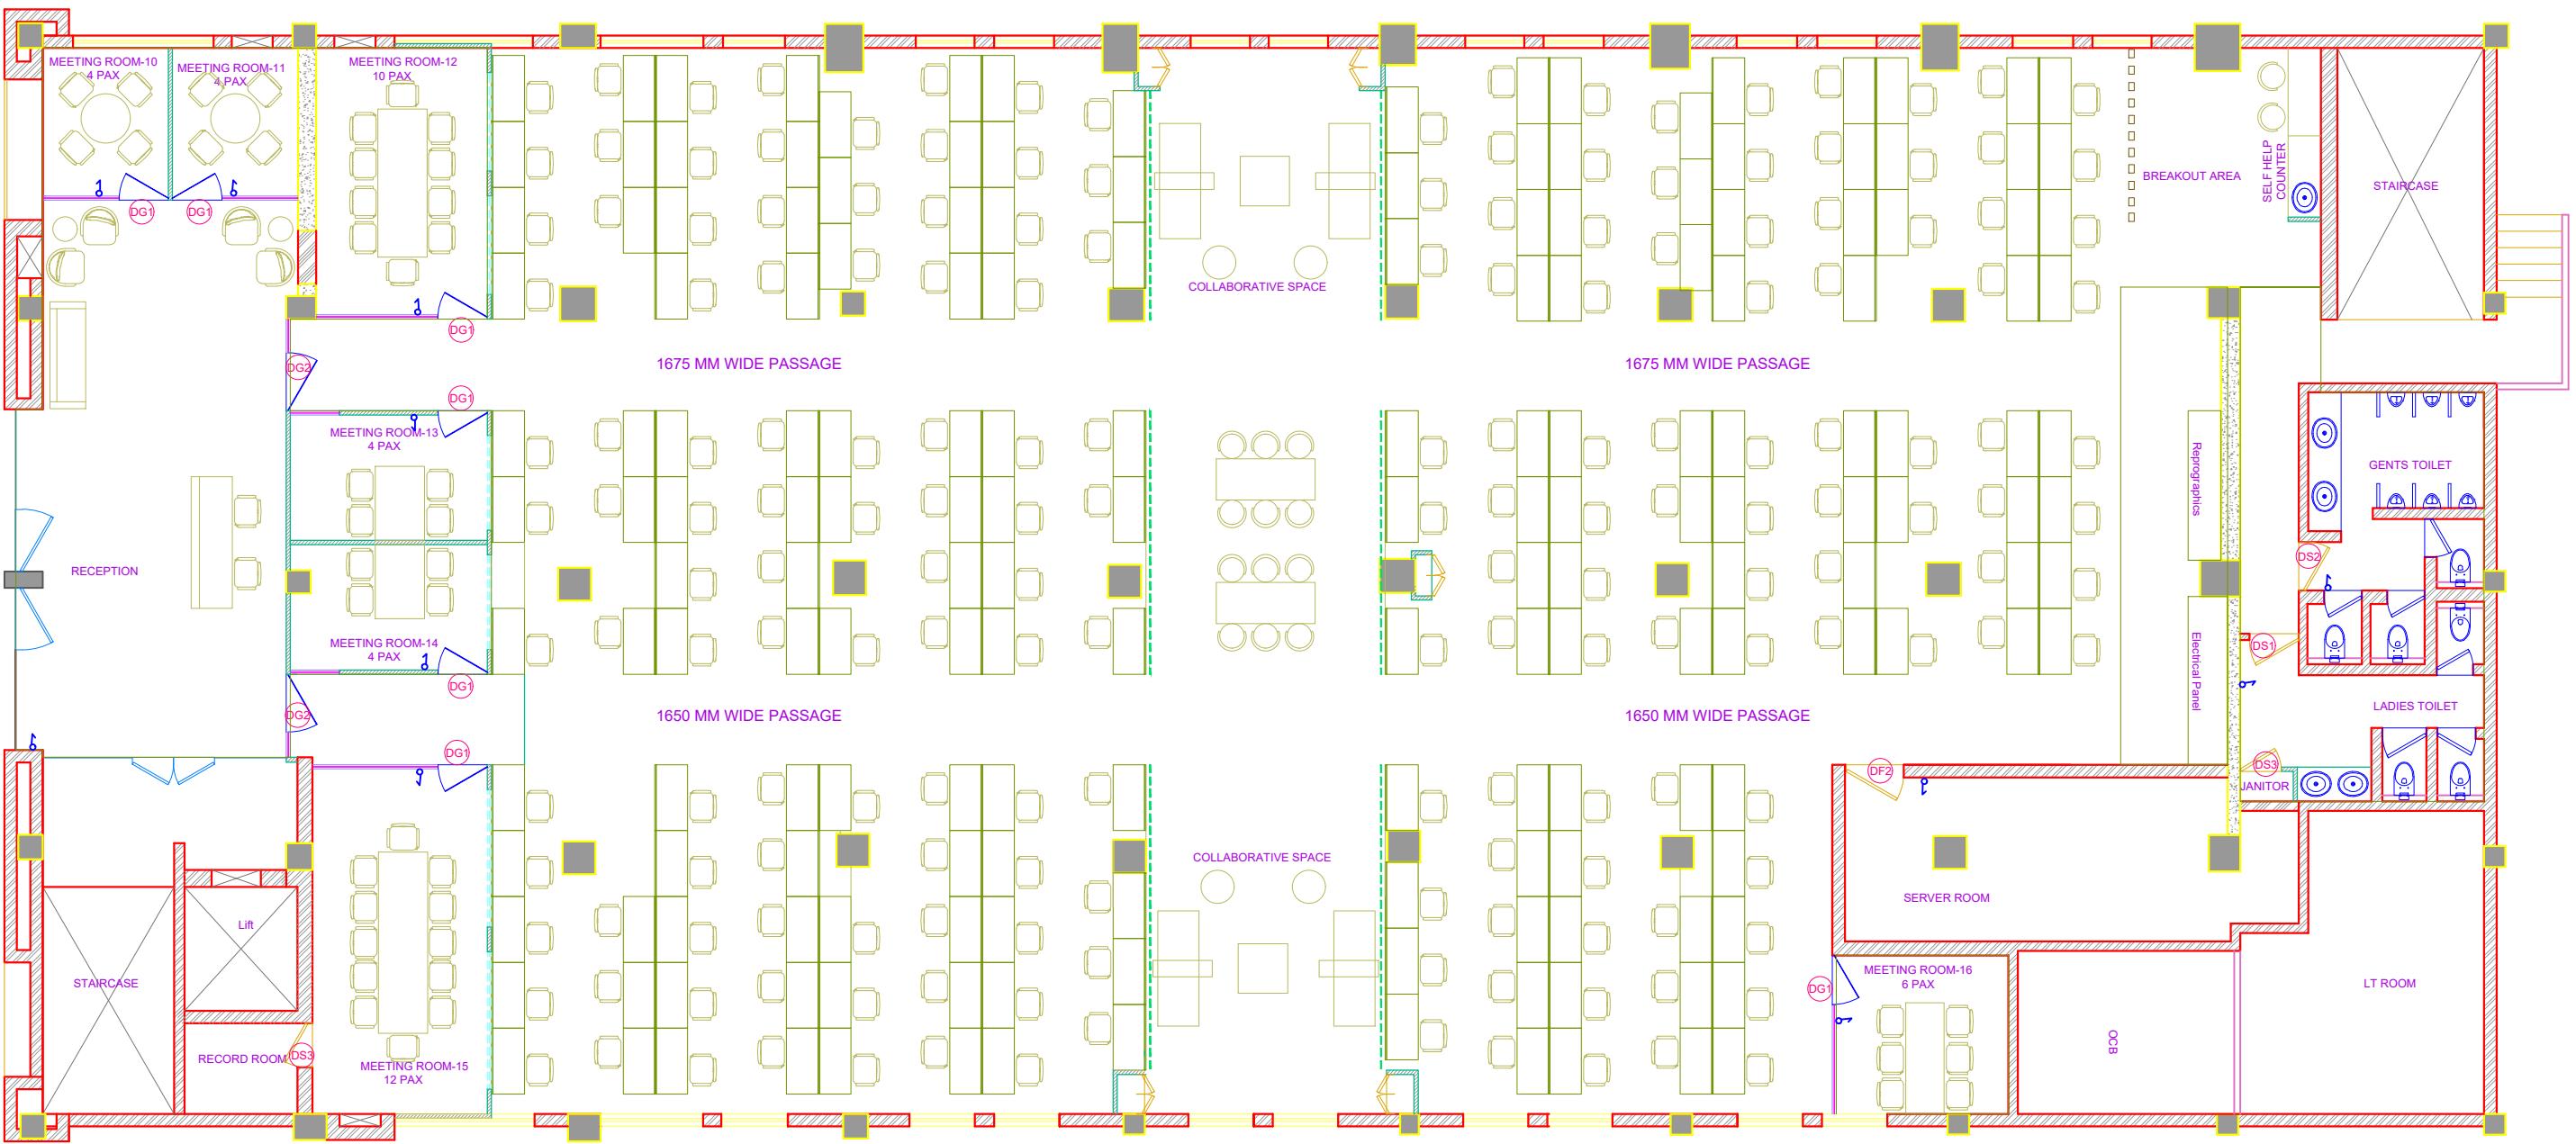


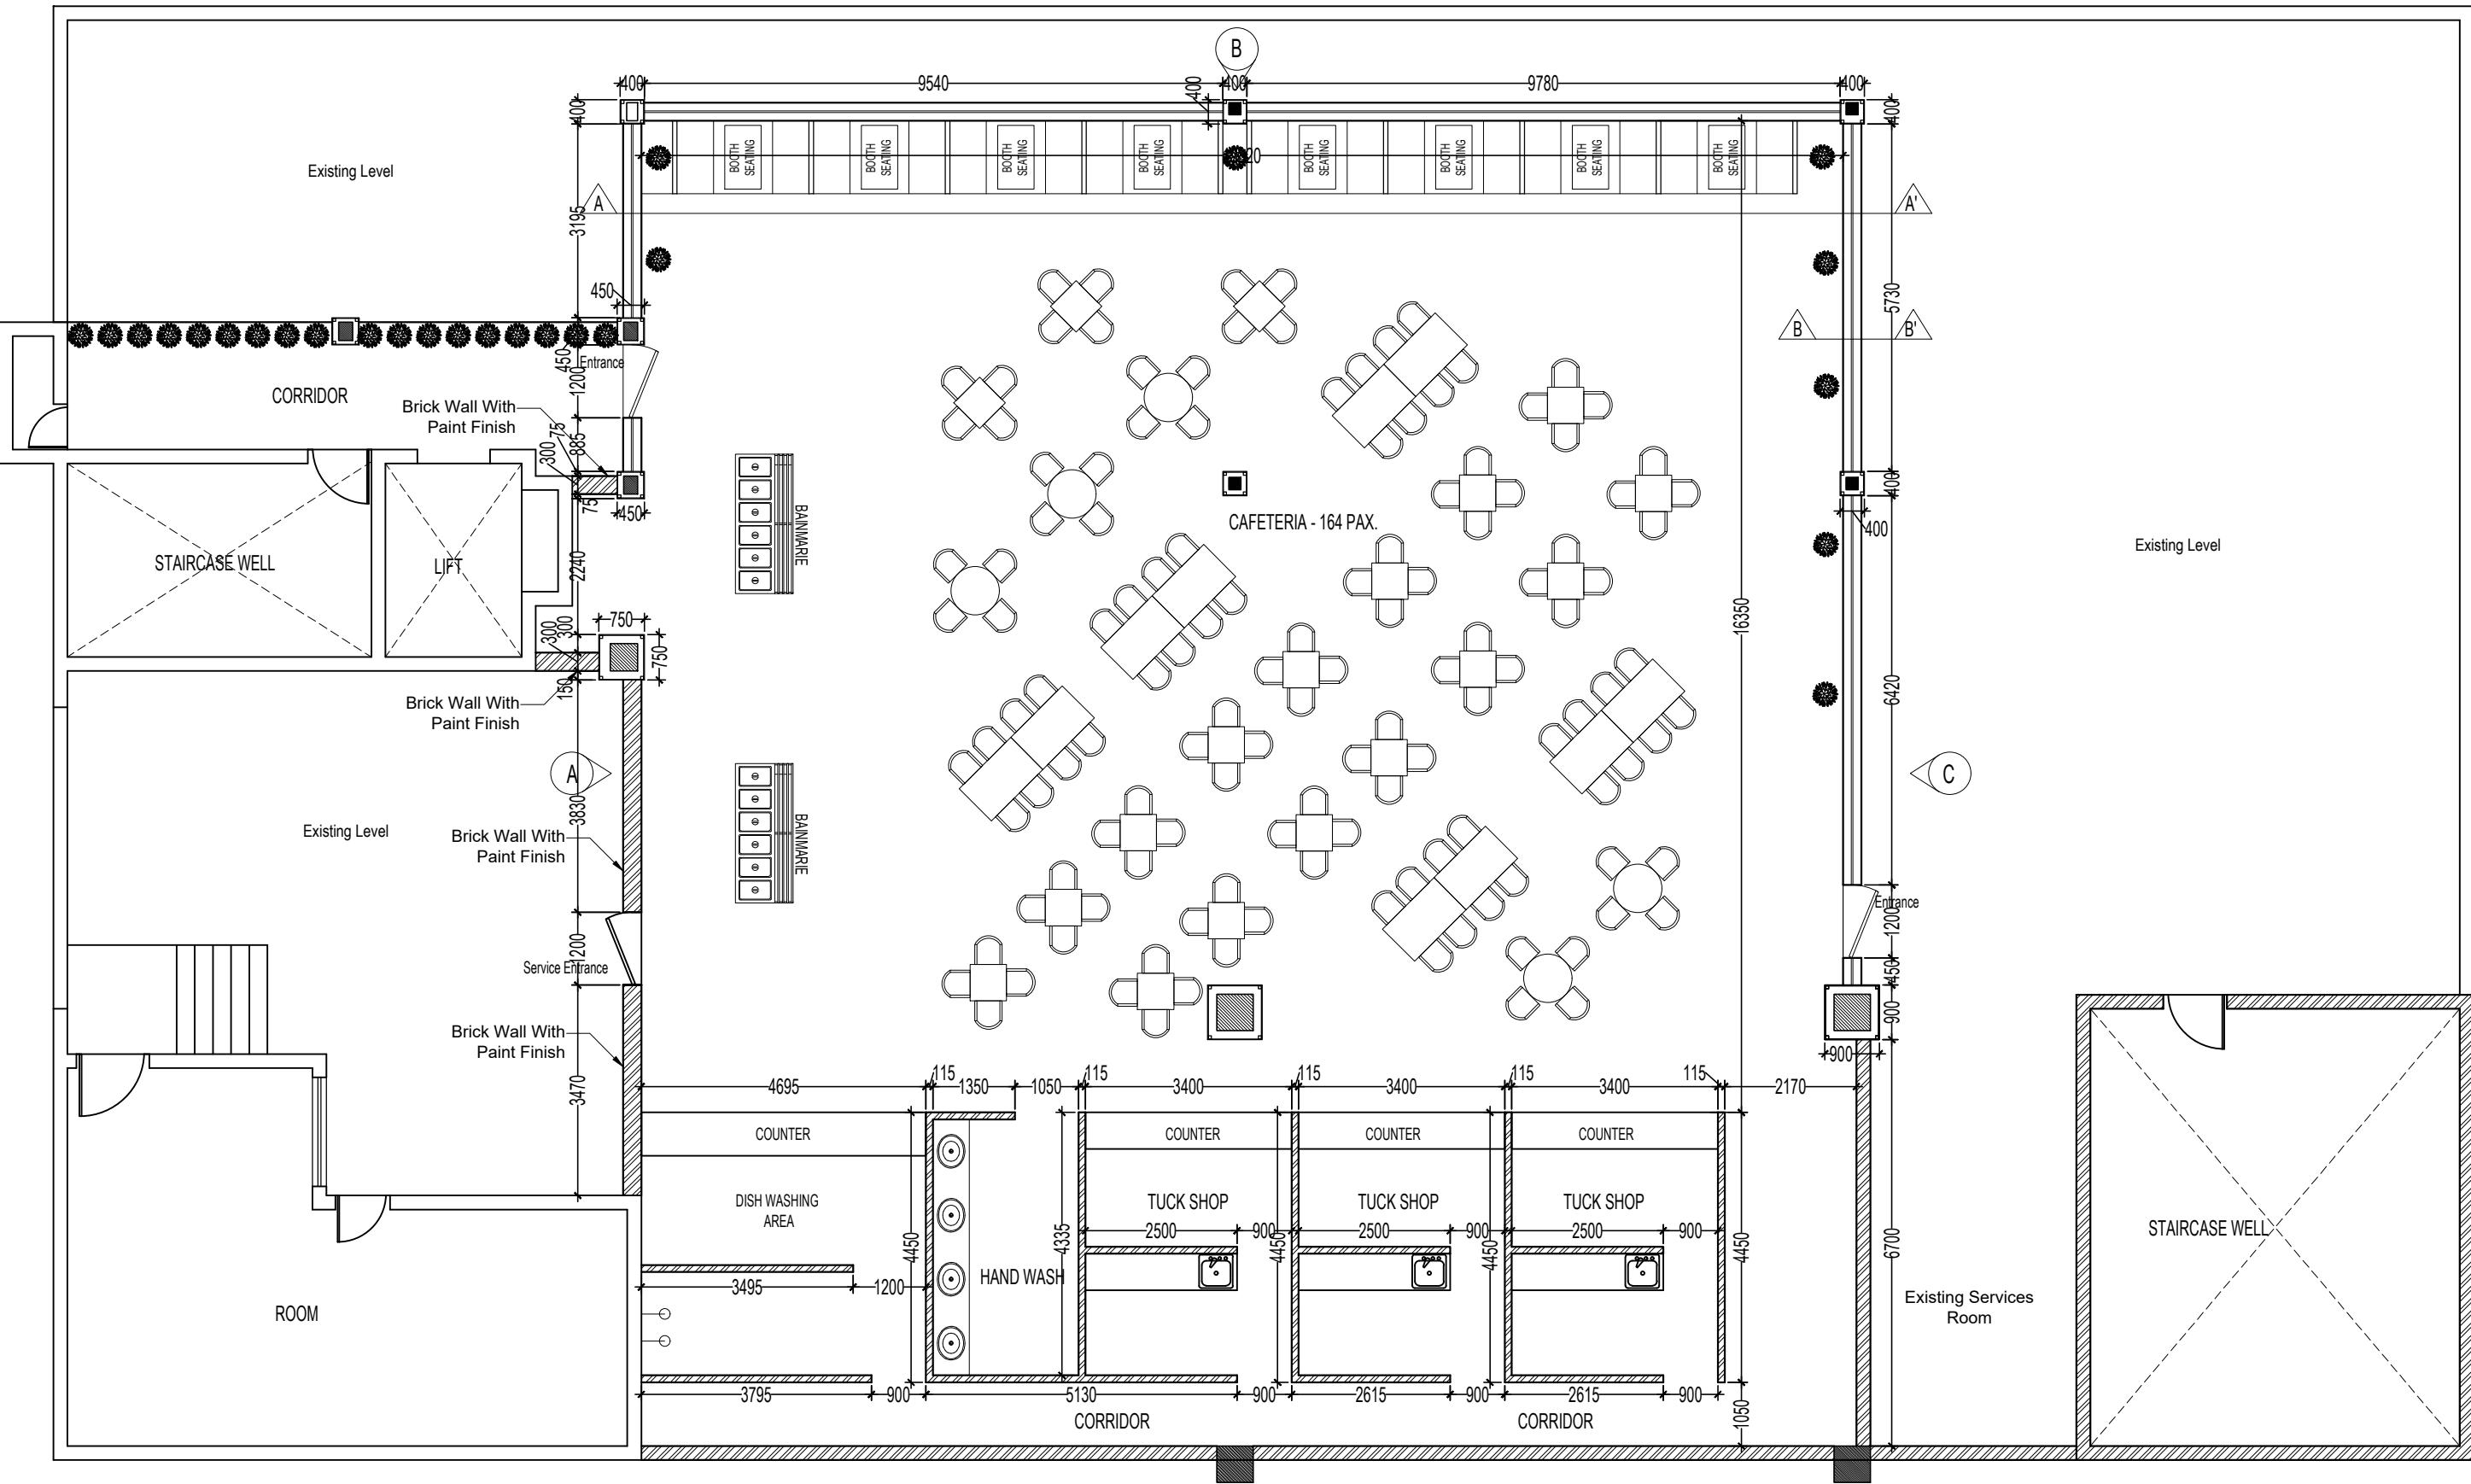


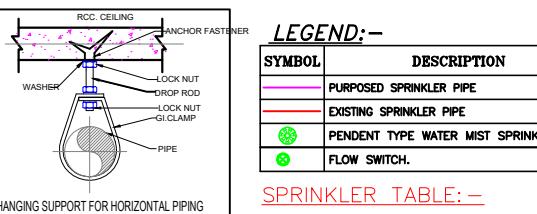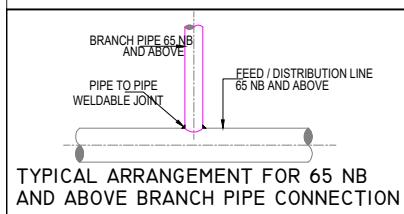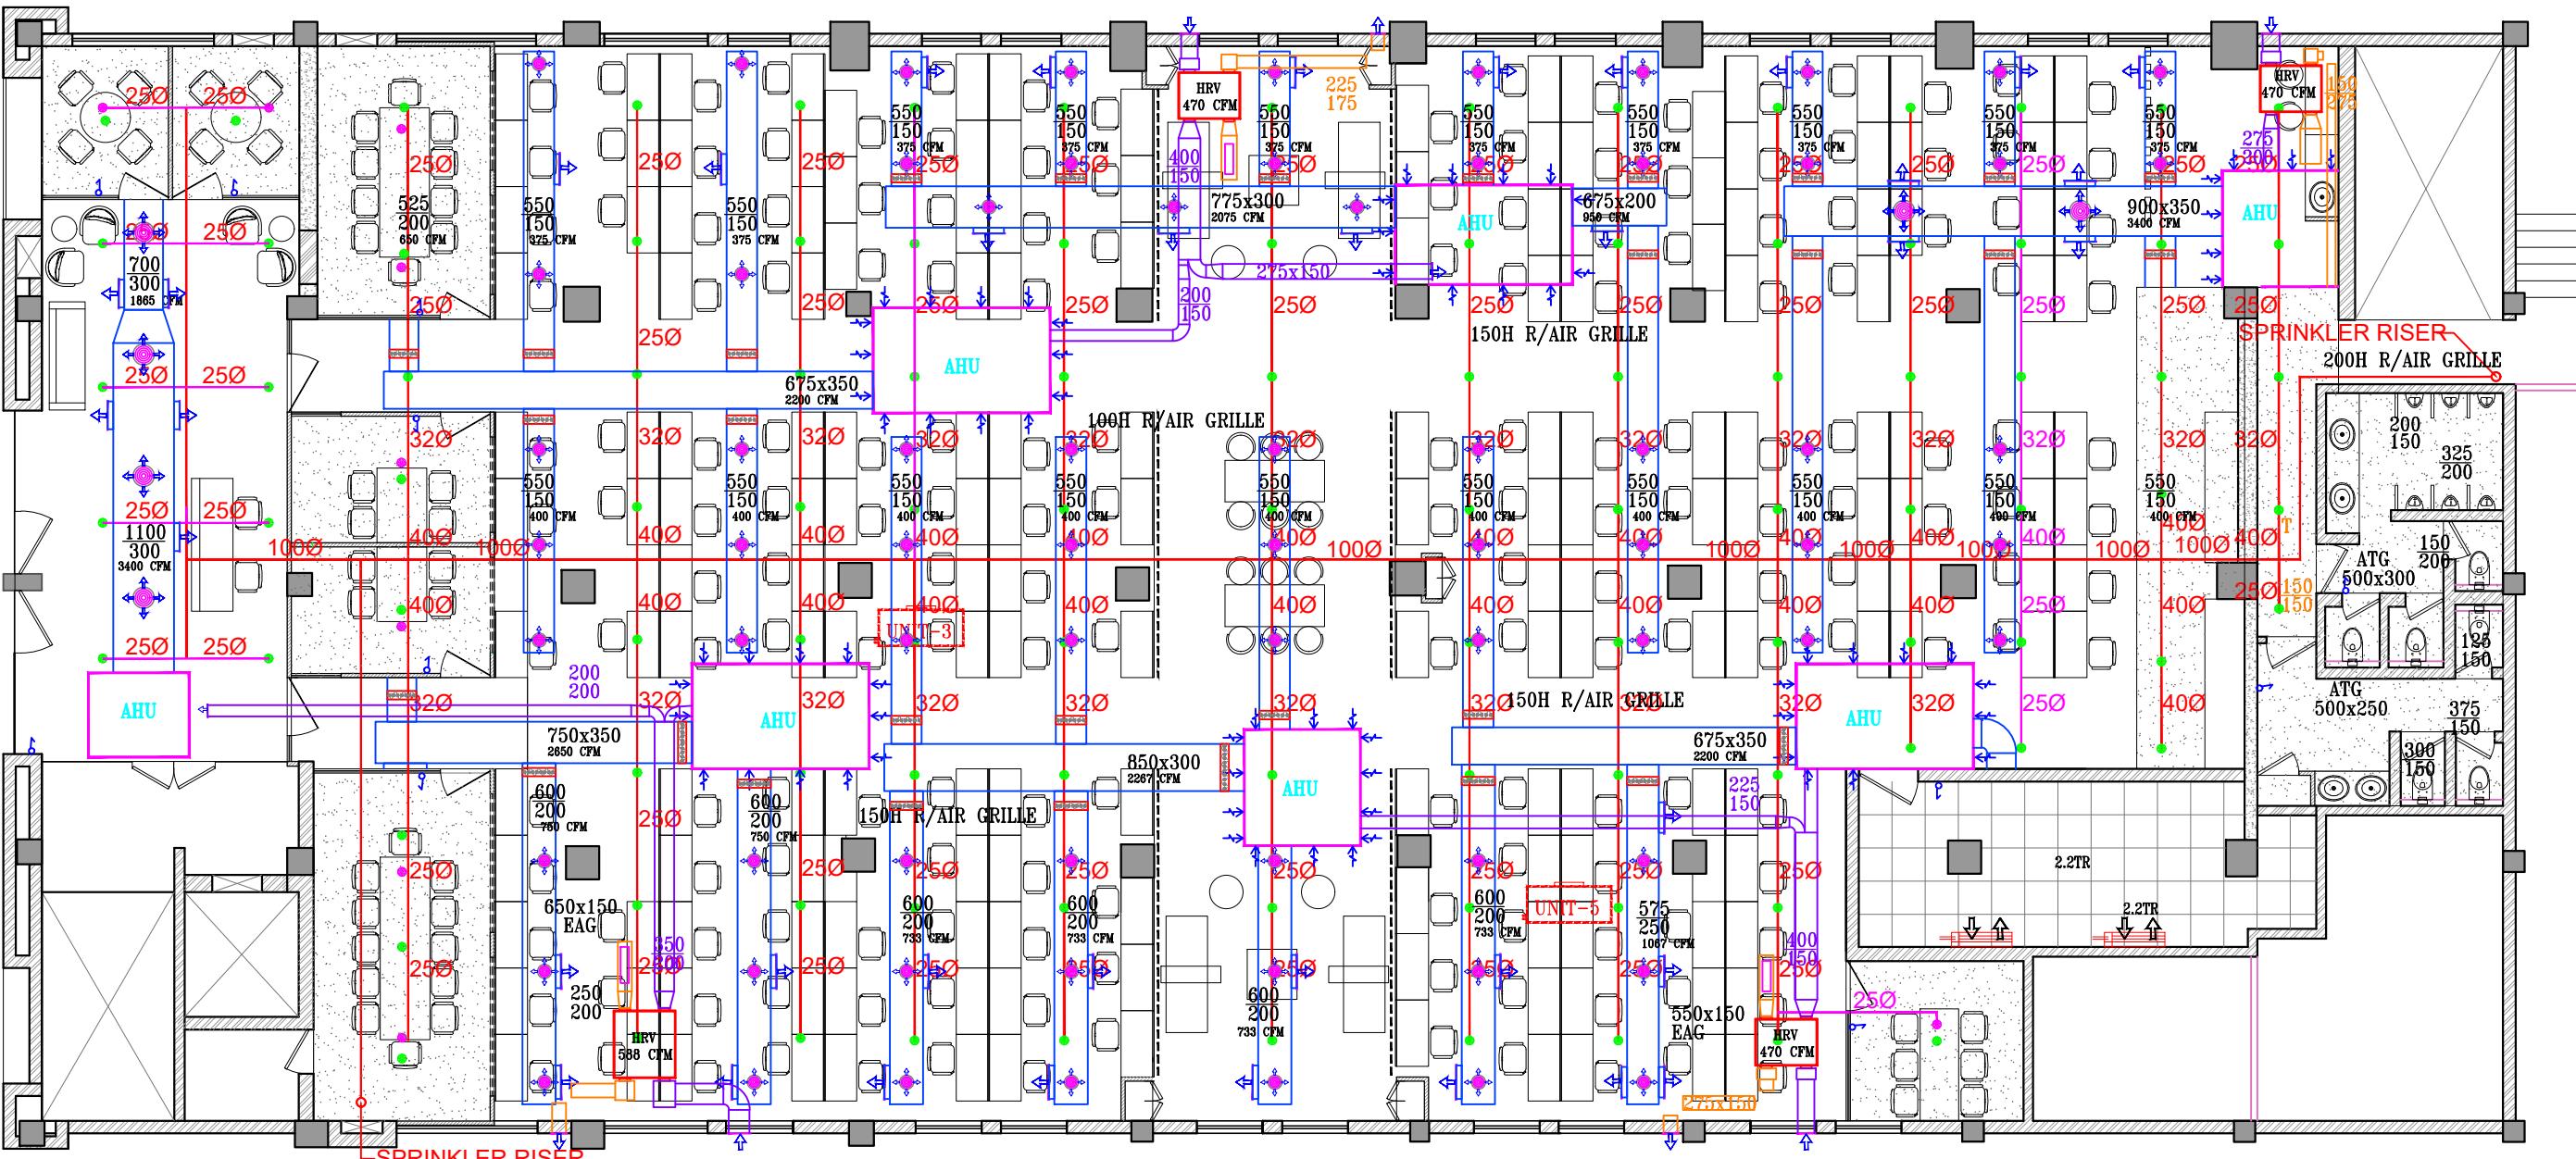

ER **LEGEND**


DESCRIPTION
OVERPOSED SPRINKLER PIPE
EXISTING SPRINKLER PIPE
INDENT TYPE WATER MIST SPRINKLER
LOW SWITCH


SPRINKLER TABLE

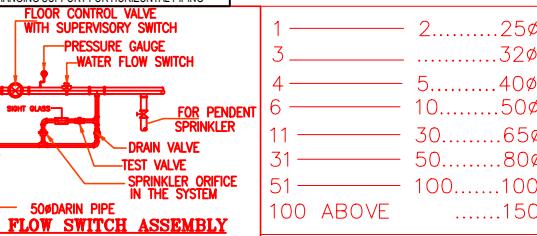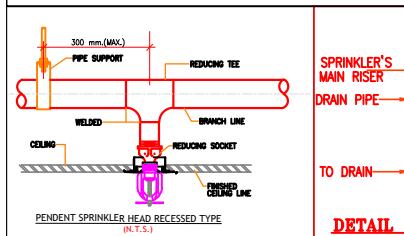

HANGING SUPPORT FOR HORIZONTAL PIPING

PIPE DIA(MIN.)	CLAMP DIM (mm.)	DROP ROD DIM (mm.)	ANCHOR DIM (mm.)	SPACING FOR SUPPORT.(M)
25Ø	20x1.2	6mm	M6x40	2.0
32Ø	20.1.2	8mm	M8x40	2.4
40Ø	20x1.2	8mm	M8x40	2.4
50Ø	25x2.0	8mm	M8x40	2.4
65Ø	25X2.0	8mm	M8x40	2.4
80Ø	25X2.5	10mm	M10x50	2.7
100Ø	25X2.5	10mm	M10x50	2.7
150Ø	25X2.5	12mm	M12x50	3.0

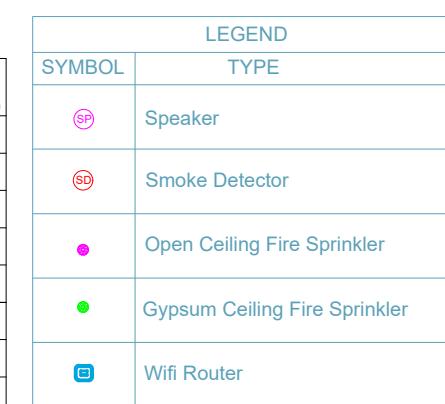


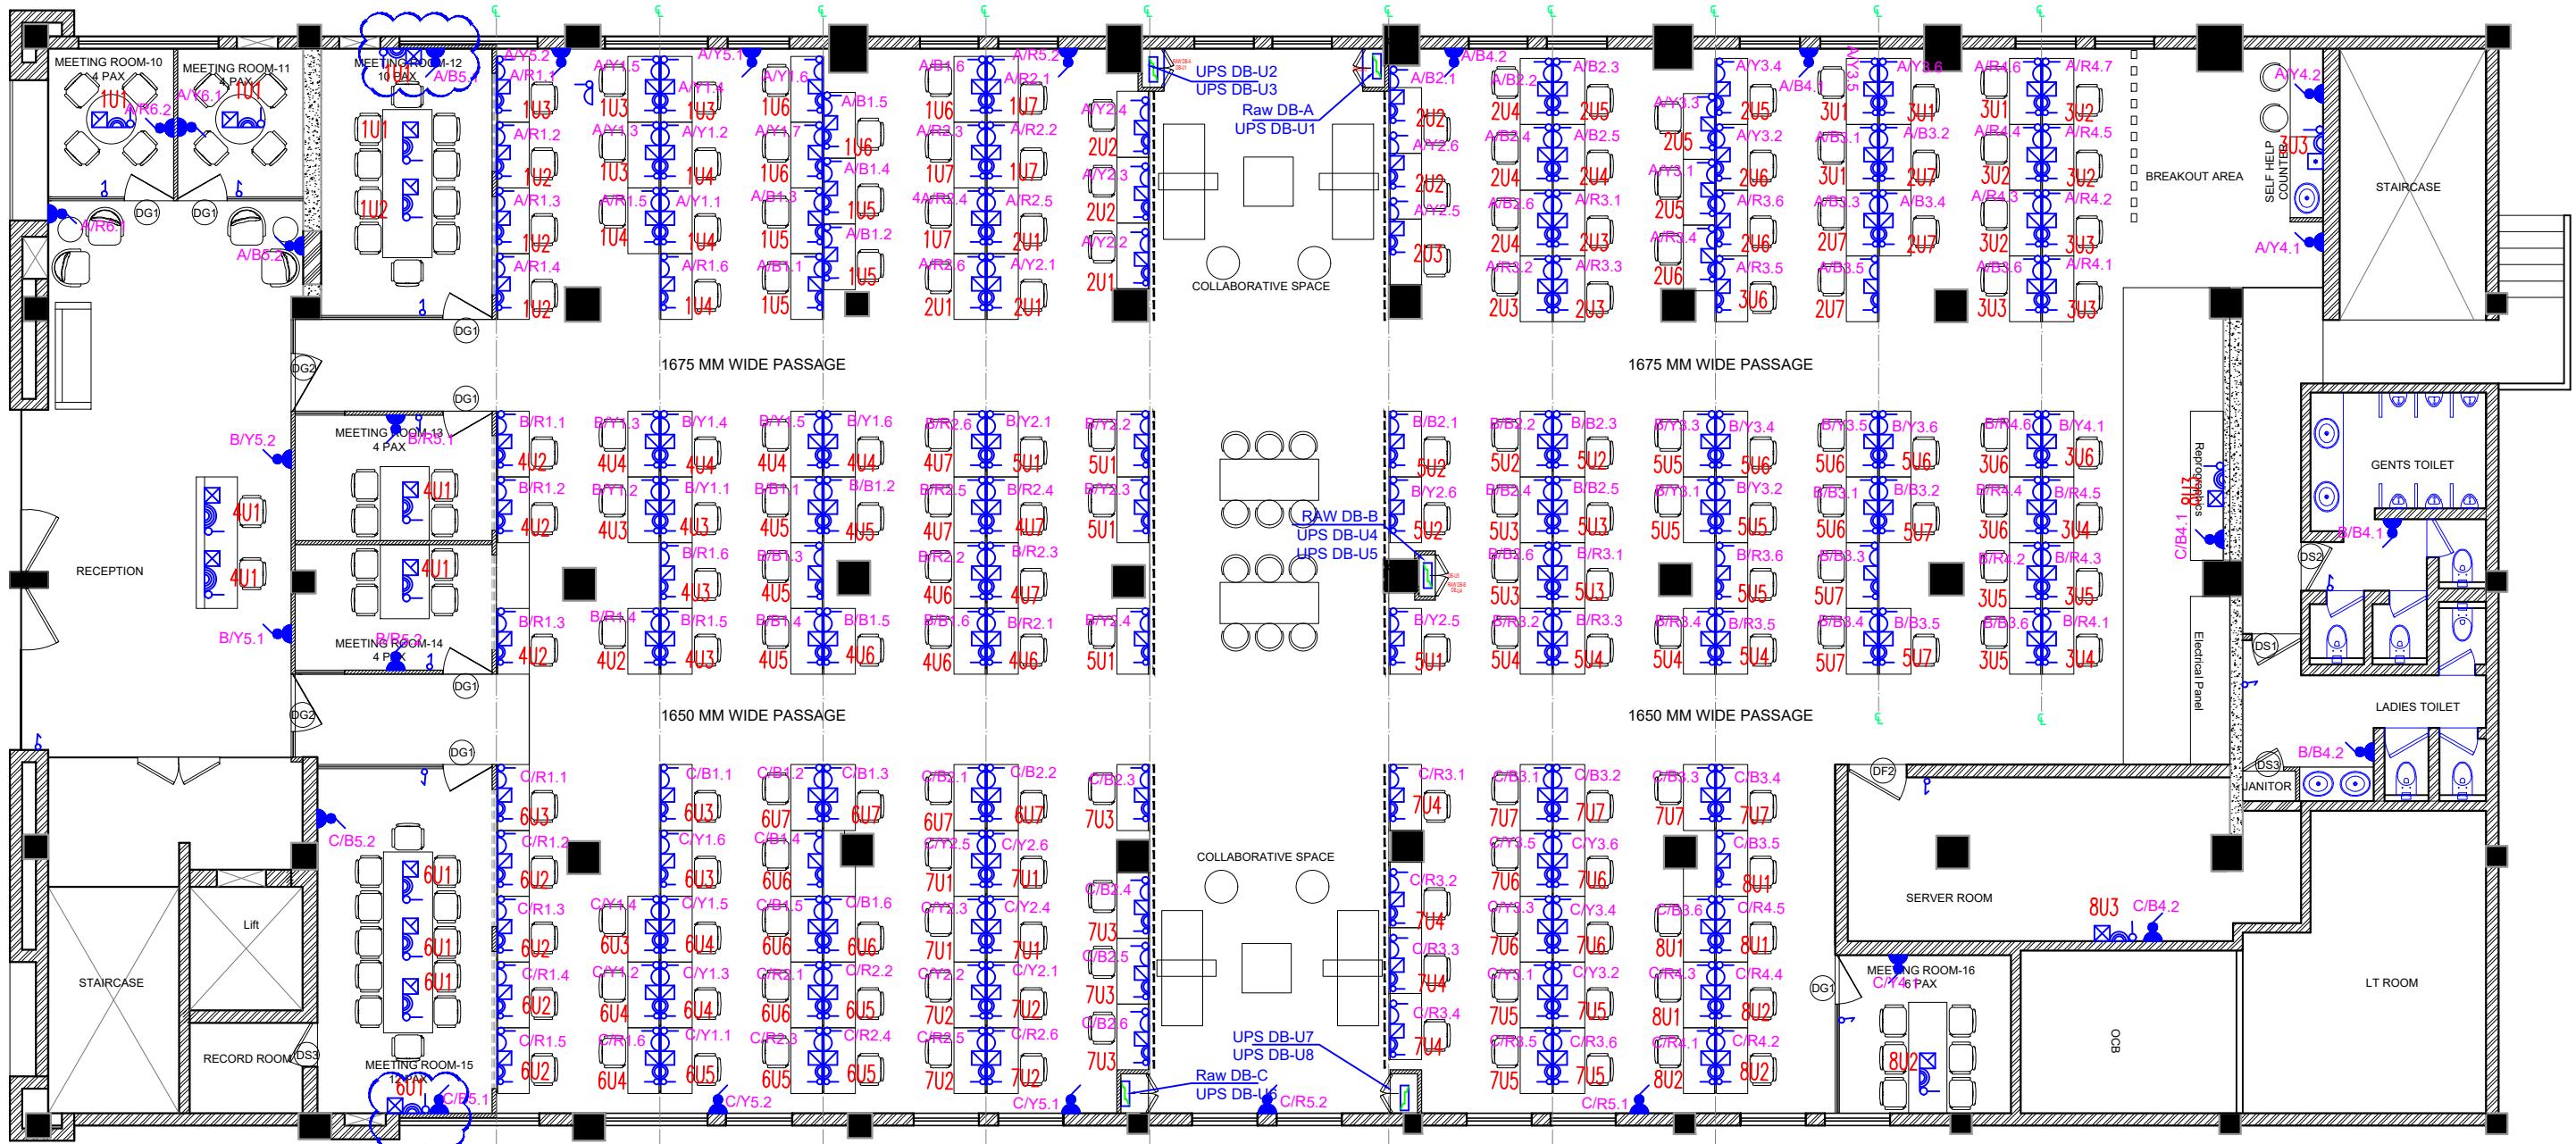

LEGENDS:-


S.NO	SYMBOL	POWER	DESCRIPTION
1	■●	1 NODE	VOICE or DATA
2	■□	2 NODE	VOICE or DATA
3	■△	3 NODE	VOICE or DATA
4	■×	4 NODE	VOICE or DATA
5	○—○	RAW POWER	1 NO UNIVERSAL SOCKET CONTROLLED BY 1 NO 5 AMP SWITCH
6	○—○	UPS POWER	2 NO UNIVERSAL SOCKET CONTROLLED BY 1 NO 15 AMP SWITCH
7	○—○		BULK HEAD

8	■●	UPS POWER	3 NO UNIVERSAL SOCKET CONTROLLED BY 1 NO 15 AMP SWITCH
9	■●	UPS POWER	3 Nos 15 AMP SOCKET CONTROLLED BY 1 NO 15 AMP SWITCH
10	■●	UPS POWER	1.NO 15 AMP SOCKET CONTROLLED BY 1 NO. 15 AMP SWITCH ON CEILING
11	○—○	RAW POWER	1 Nos UNIVERSAL SOCKET CONTROLLED BY 1 NO 15 AMP SWITCH
12	○—○	RAW POWER	1 Nos 15 AMP SOCKET CONTROLLED BY 1 NO 15 AMP SWITCH
13	○—○	RAW POWER	1.Nos 20 AMP1-P.industrial socket WITH 16 AMP.DP.MCB
14	~	TV POINT	
15	■●	UPS POWER	4 NO UNIVERSAL SOCKET CONTROLLED BY 1 NO 15 AMP SWITCH

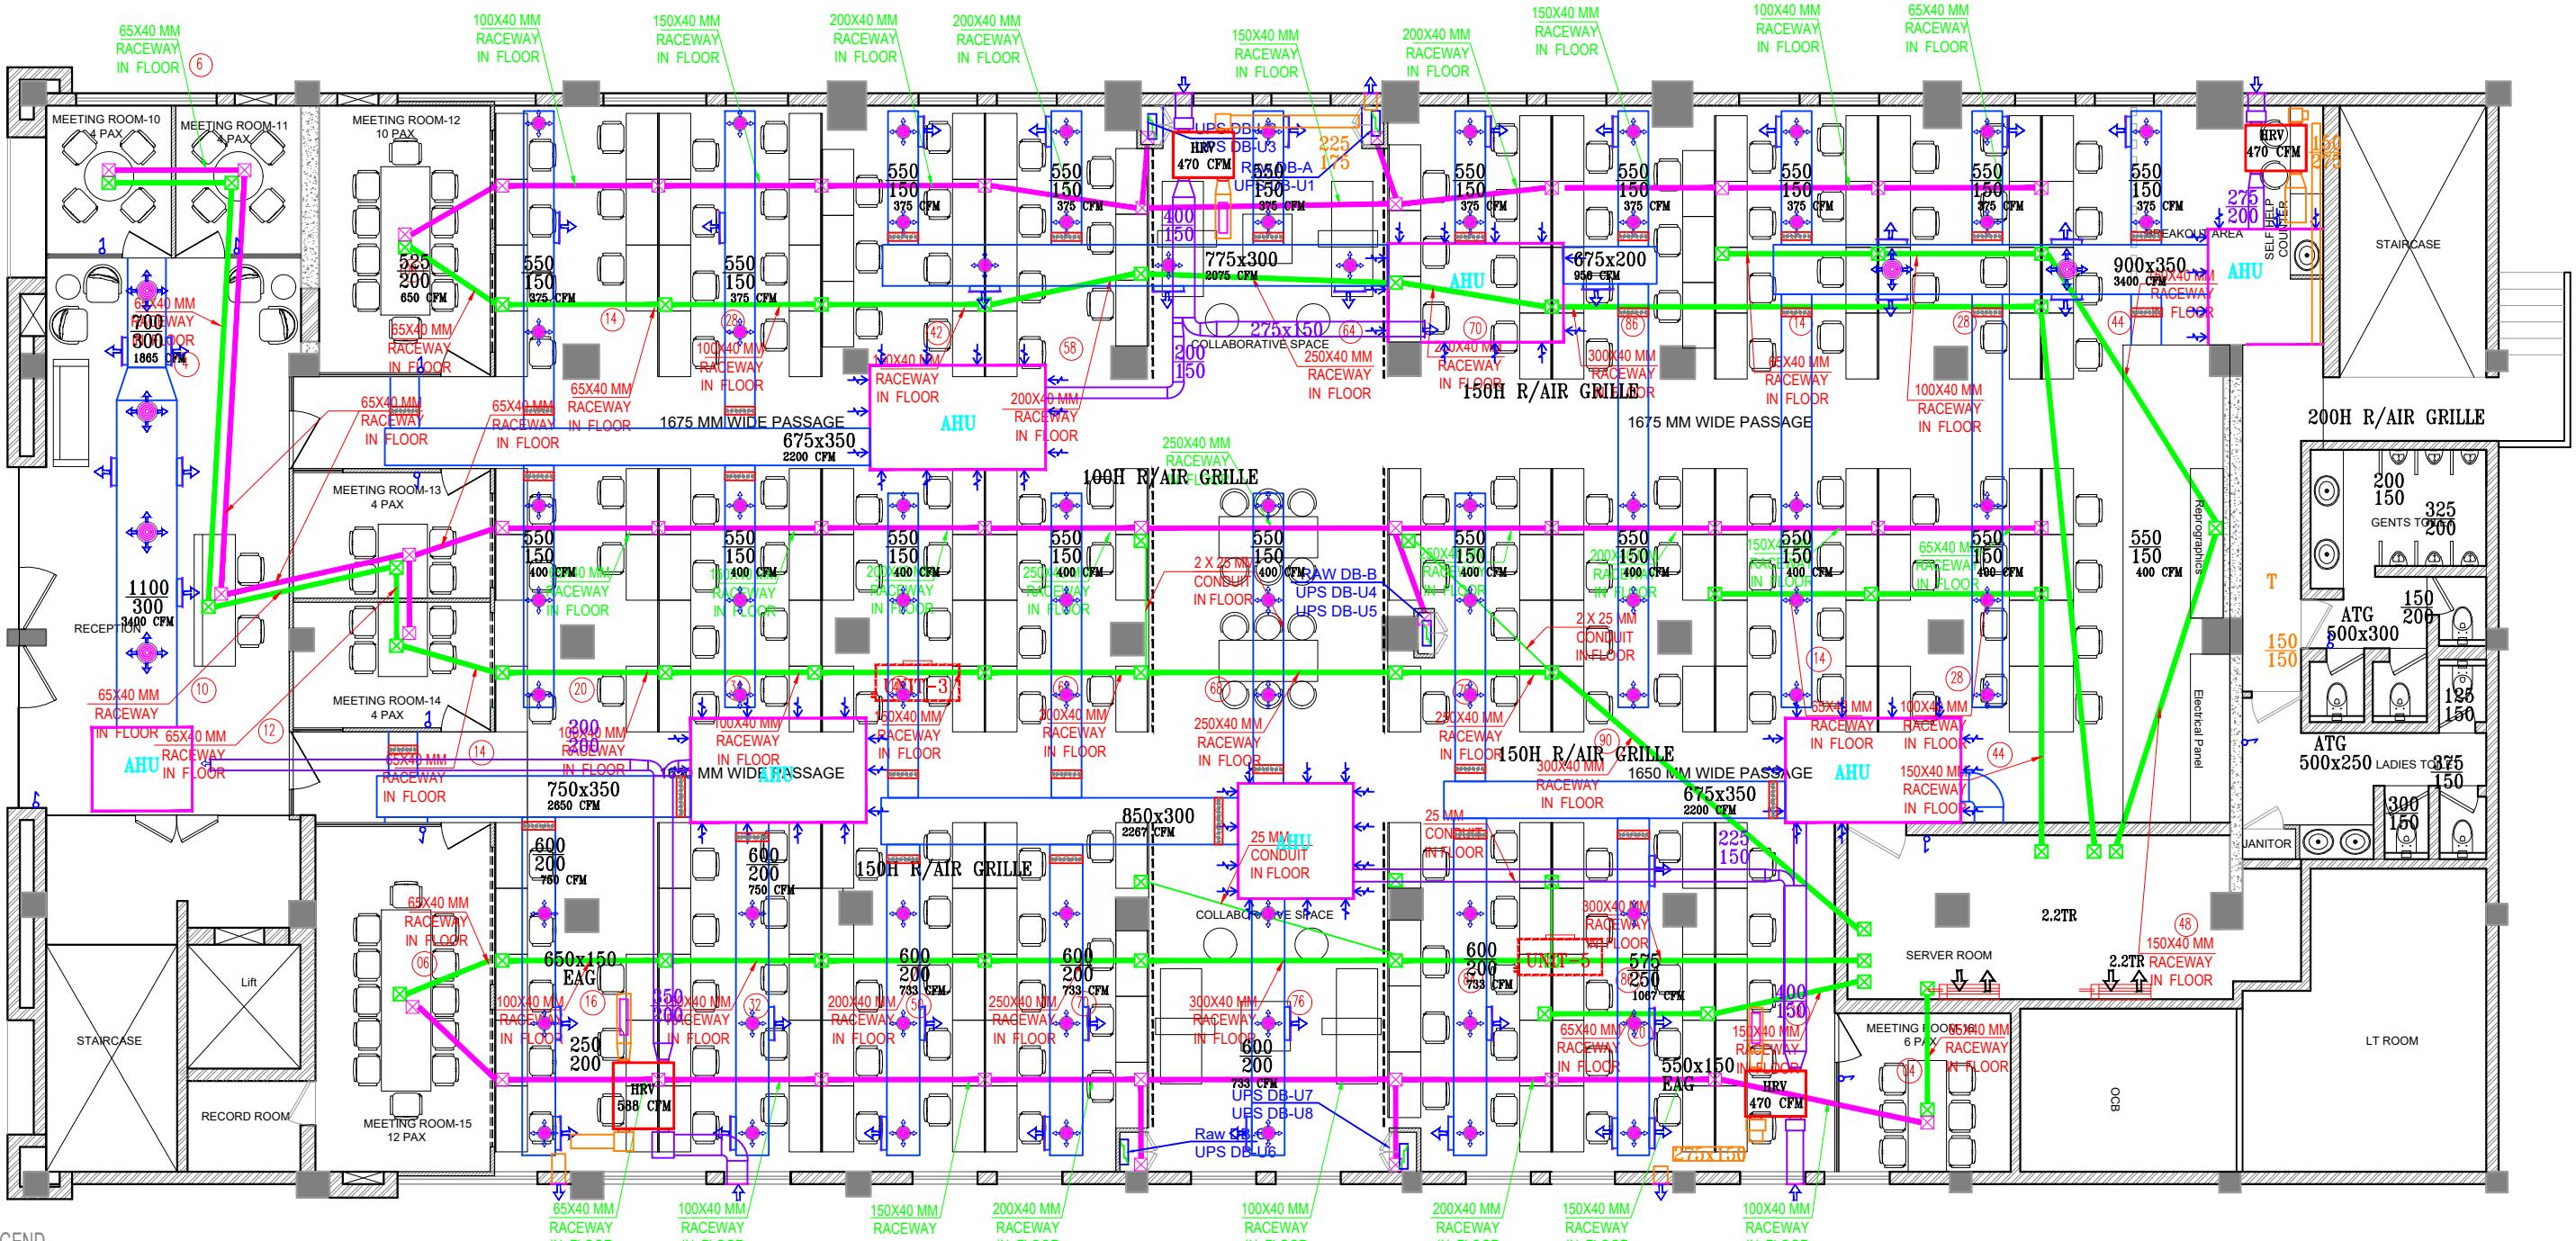

LEGEND



	TELEPHONE/COMPUTER(TRUNKING)
	POWER/UPS (TRUNKING)
	TRUNKING IN CEILING UPS / POWER
	TRUNKING IN CEILING DATA
	CONDUIT IN FLOOR/CEILING UPS POWER
	CONDUIT IN FLOOR/CEILING DATA/VOICE
	JUNCTION BOX DATA
	JUNCTION BOX POWER


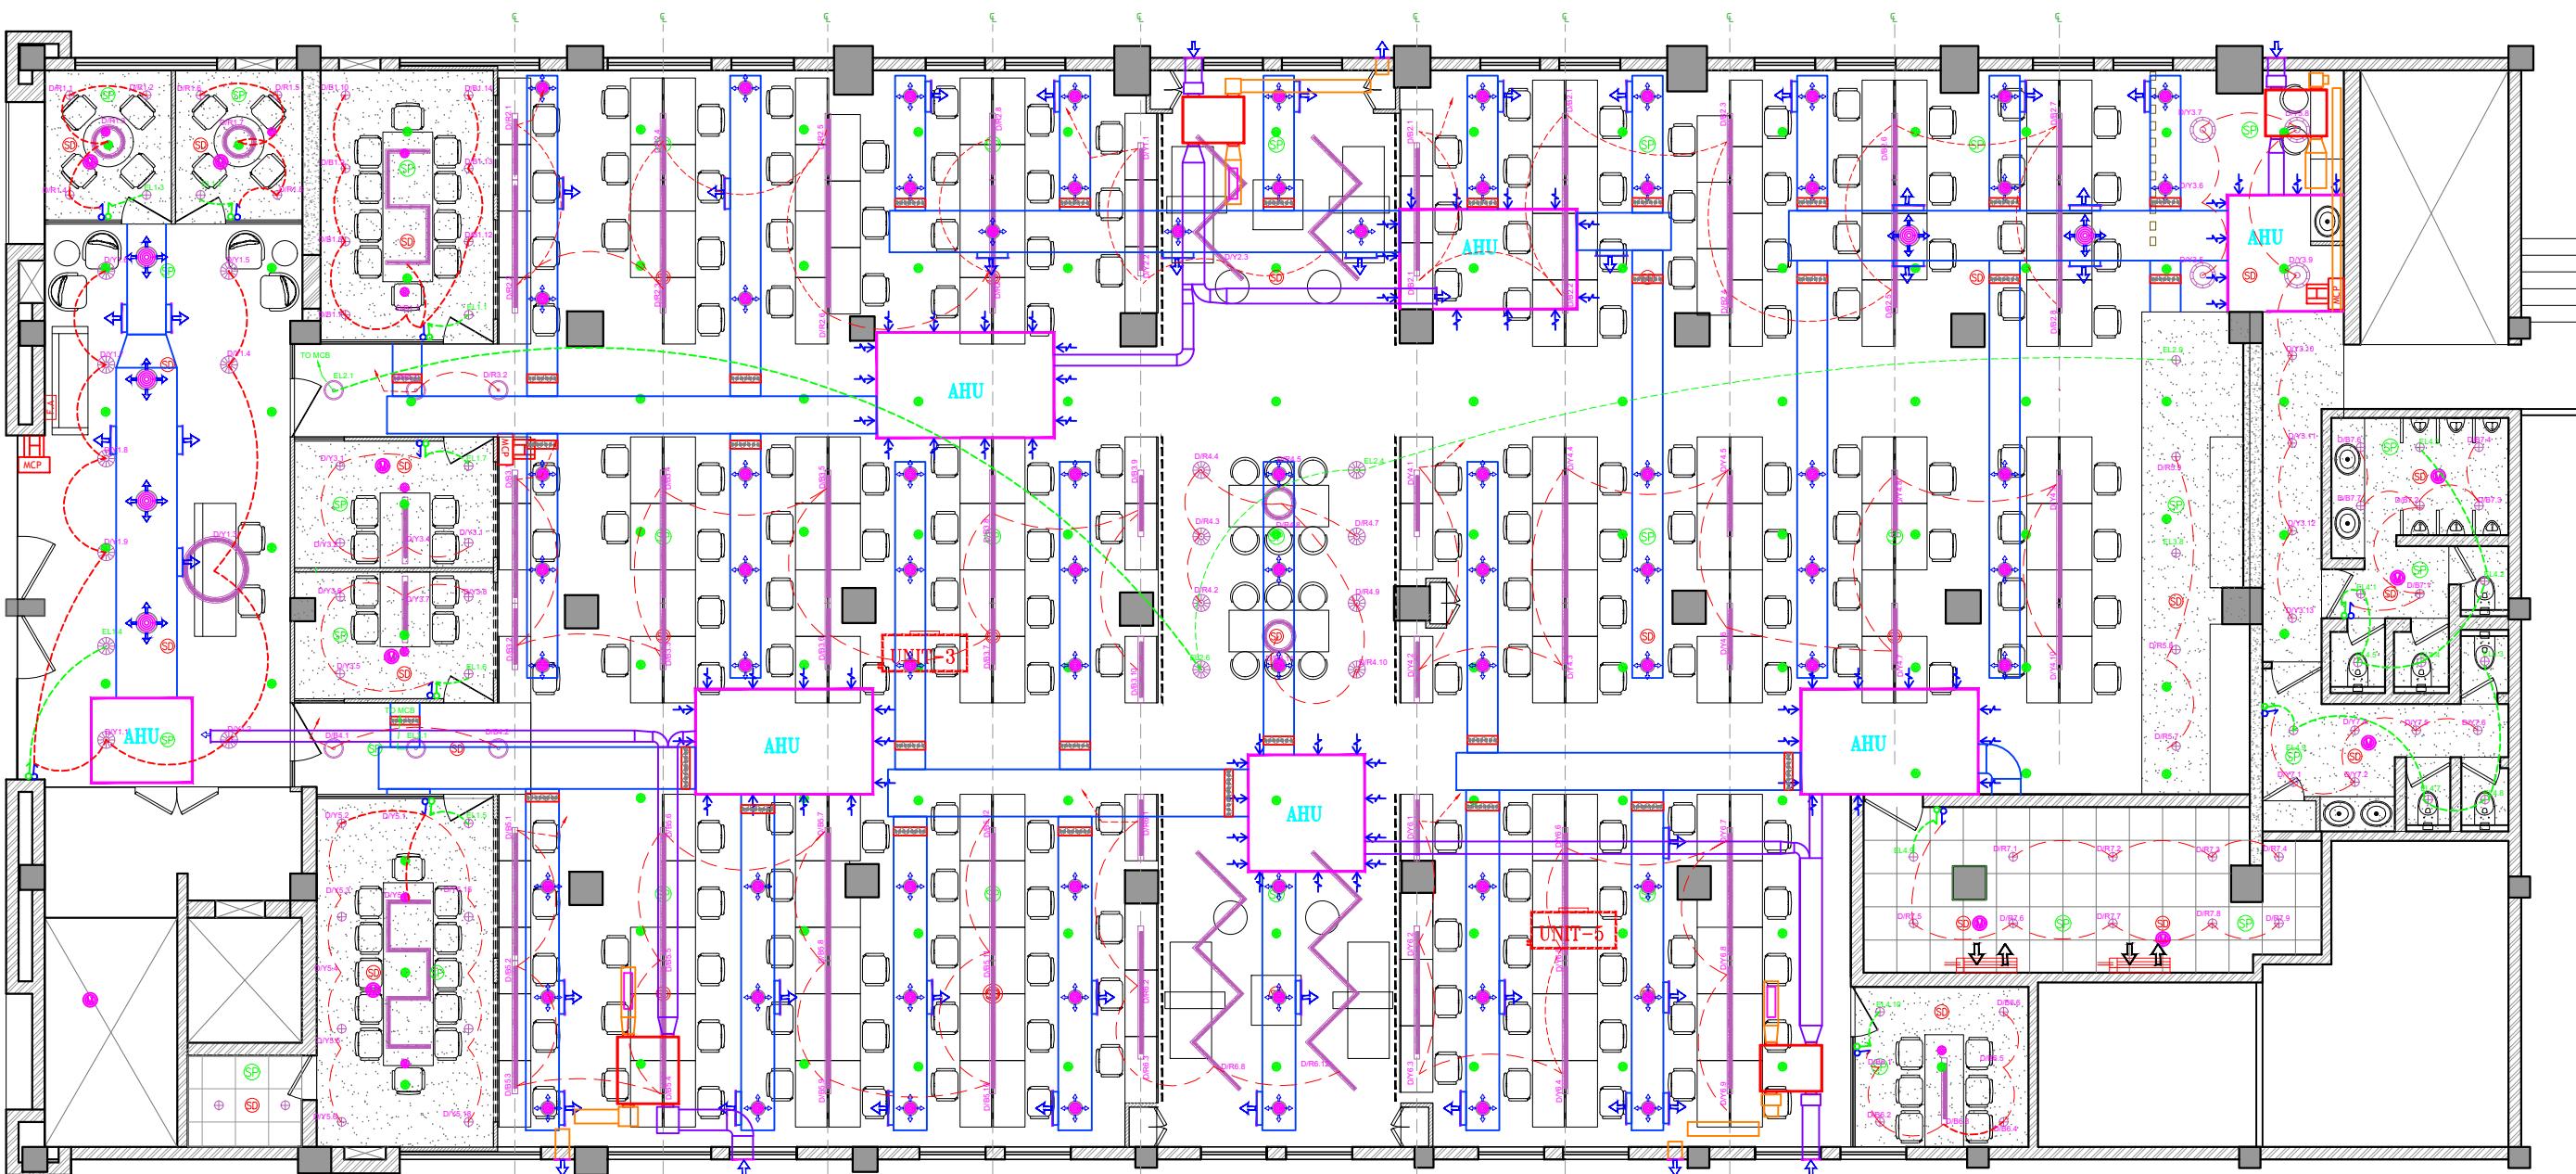


LIGHTING LEGEND				LIGHTING LEGEND			
SYMBOL	TYPE	LOCATION	QTY.	SYMBOL	TYPE	LOCATION	QTY.
	Hanging Light - Type 1	Reception	03		Hanging Light - Type 6	Cafetaria	
	Hanging Light - Type 2	Reception			Downlighter / Hanging Light	All areas	
	Hanging Light - Type 3	Meeting Rooms			2'X2' downlight	Server room	
	Downlighter - Round	All areas			Spotlight	Rafters	
	Hanging Light - Type 4	Workhall + Cabin			Wall Light	Reception / Workhall	
	Ceiling Mounted Light	Board room			Access control	All areas	
	Hanging Light - Type 5	Workhall			Camera	All areas	6 NO

LEGEND	
SYMBOL	TYPE
	Speaker
	Smoke Detector
	Open Ceiling Fire Sprinkler
	Gypsum Ceiling Fire Sprinkler
	Wifi Router


Gypsum ceiling

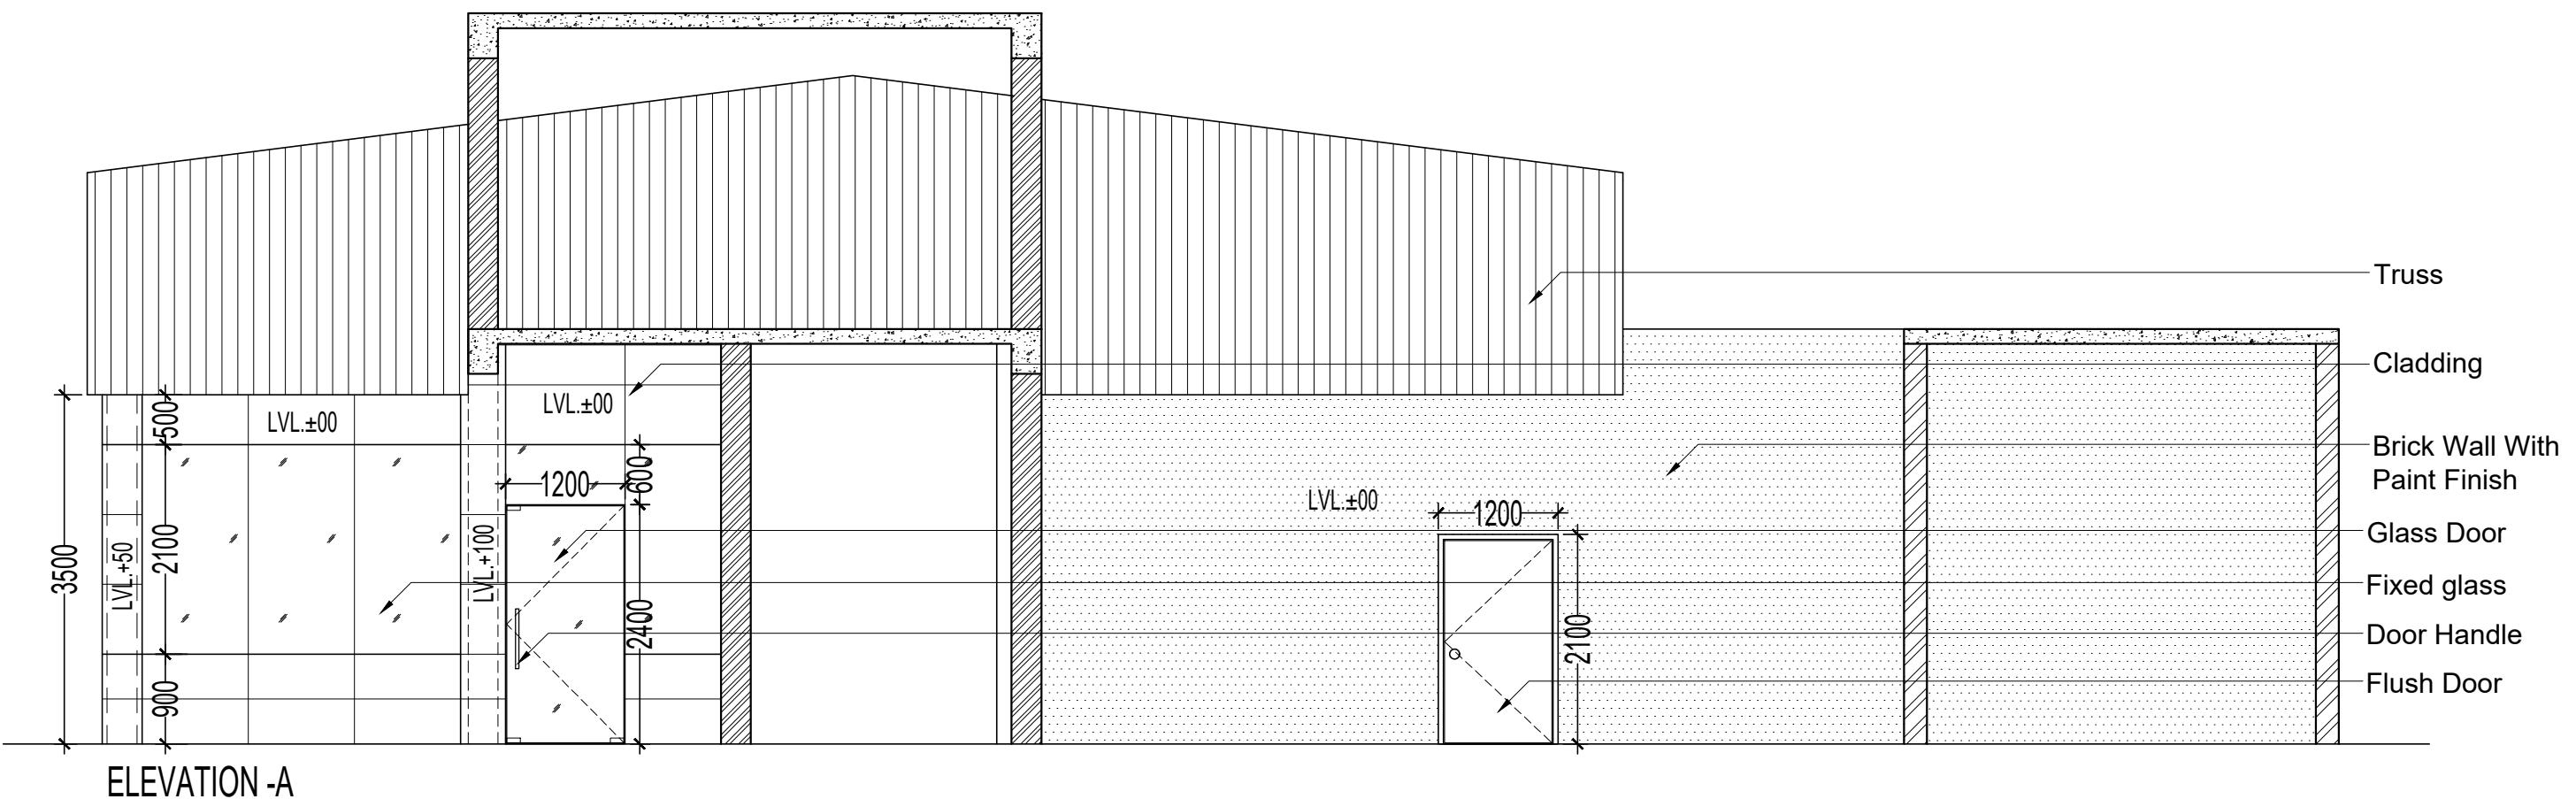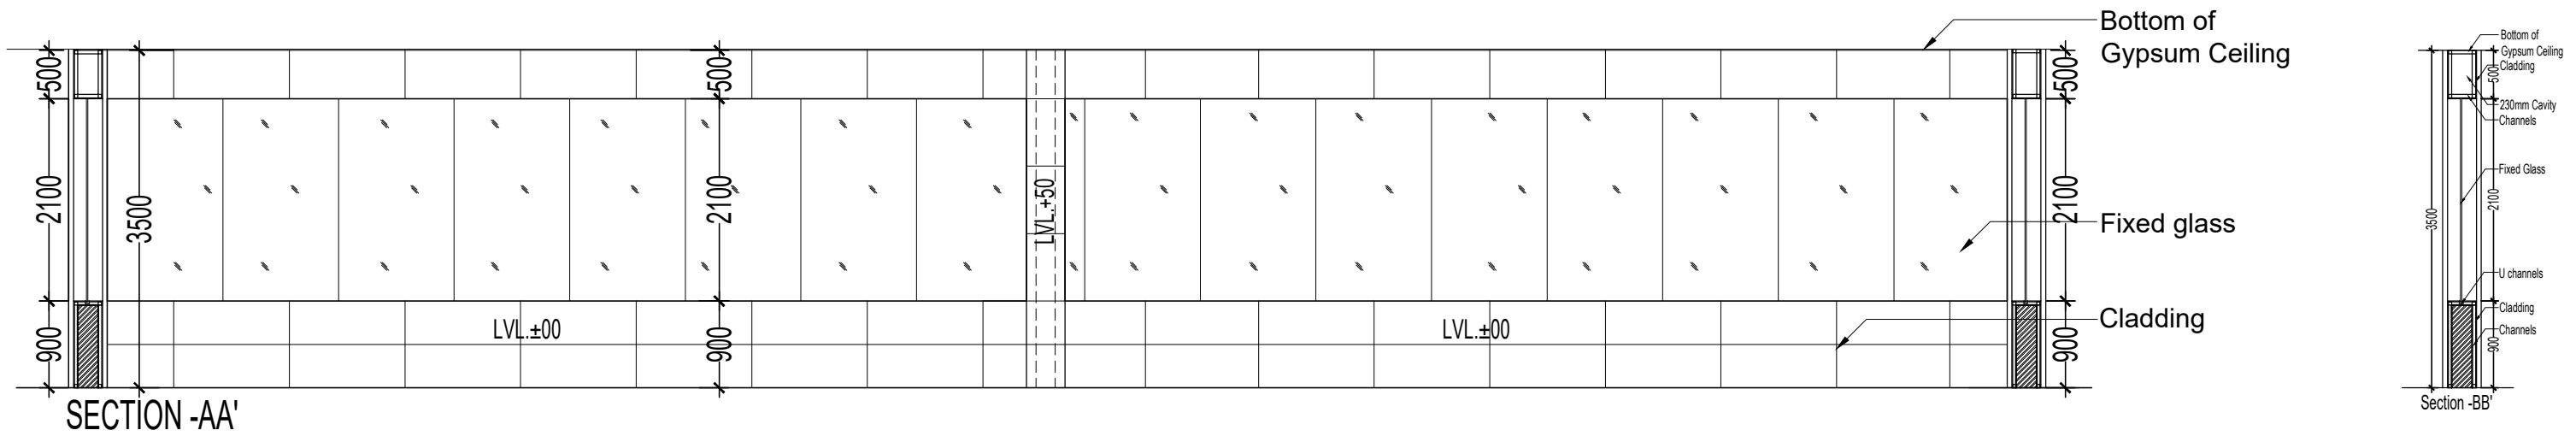

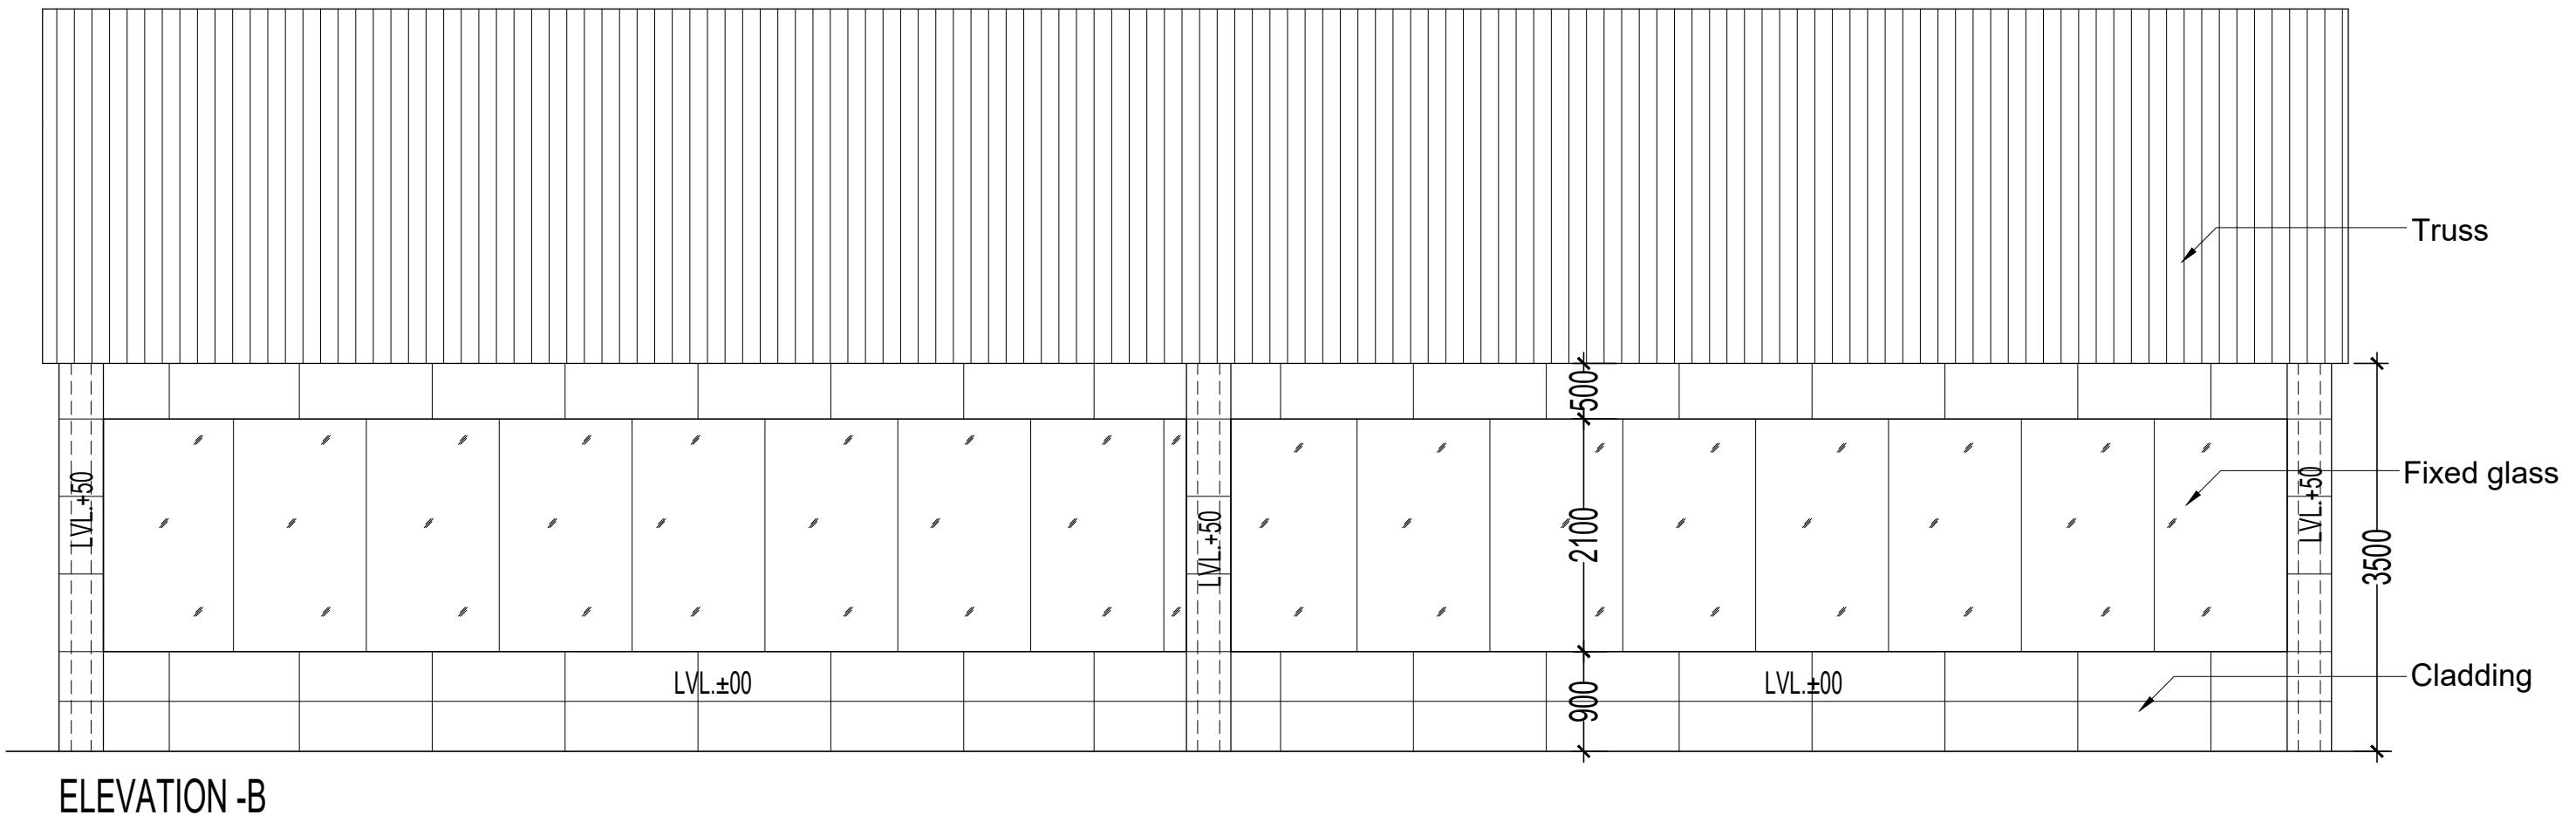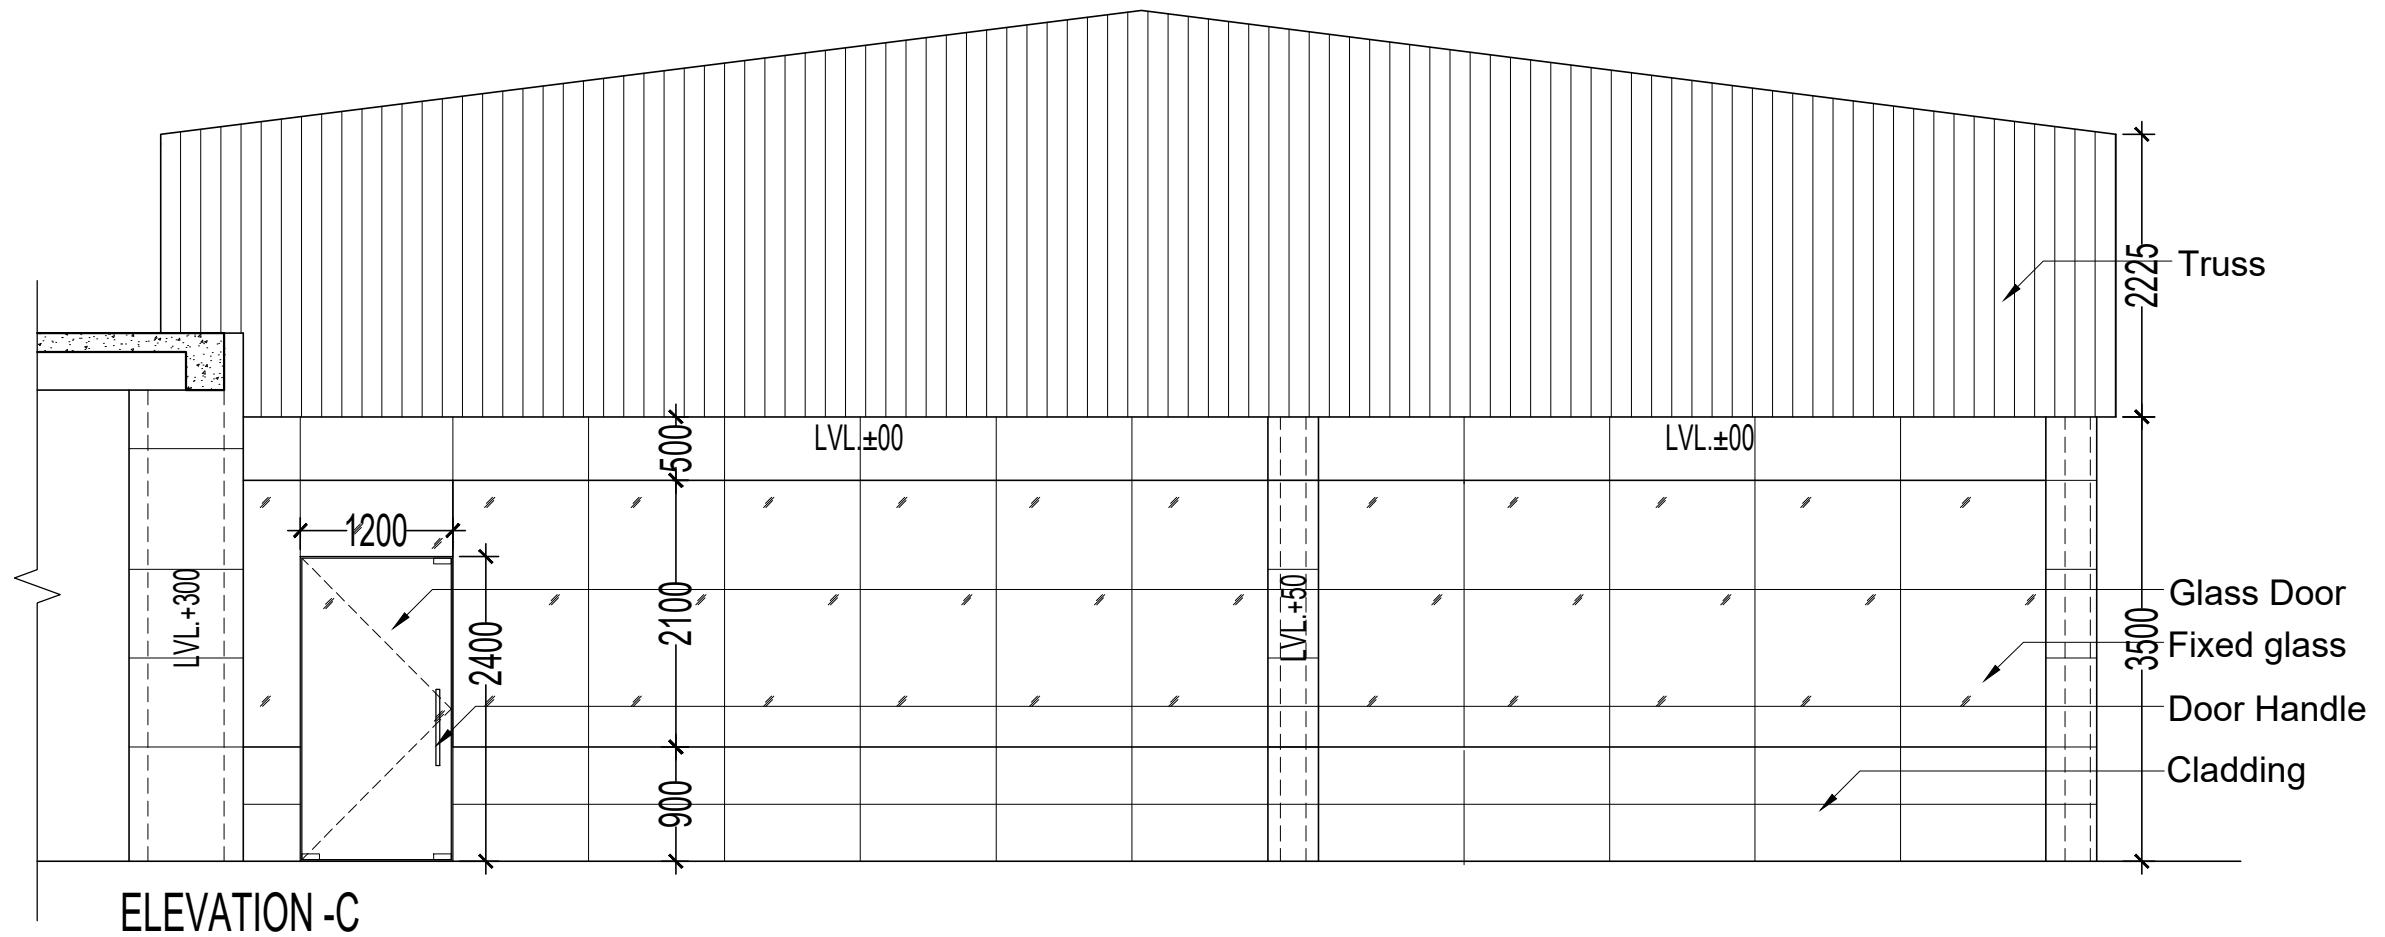

LG ELECTRONICS

Corporate Workplace Design

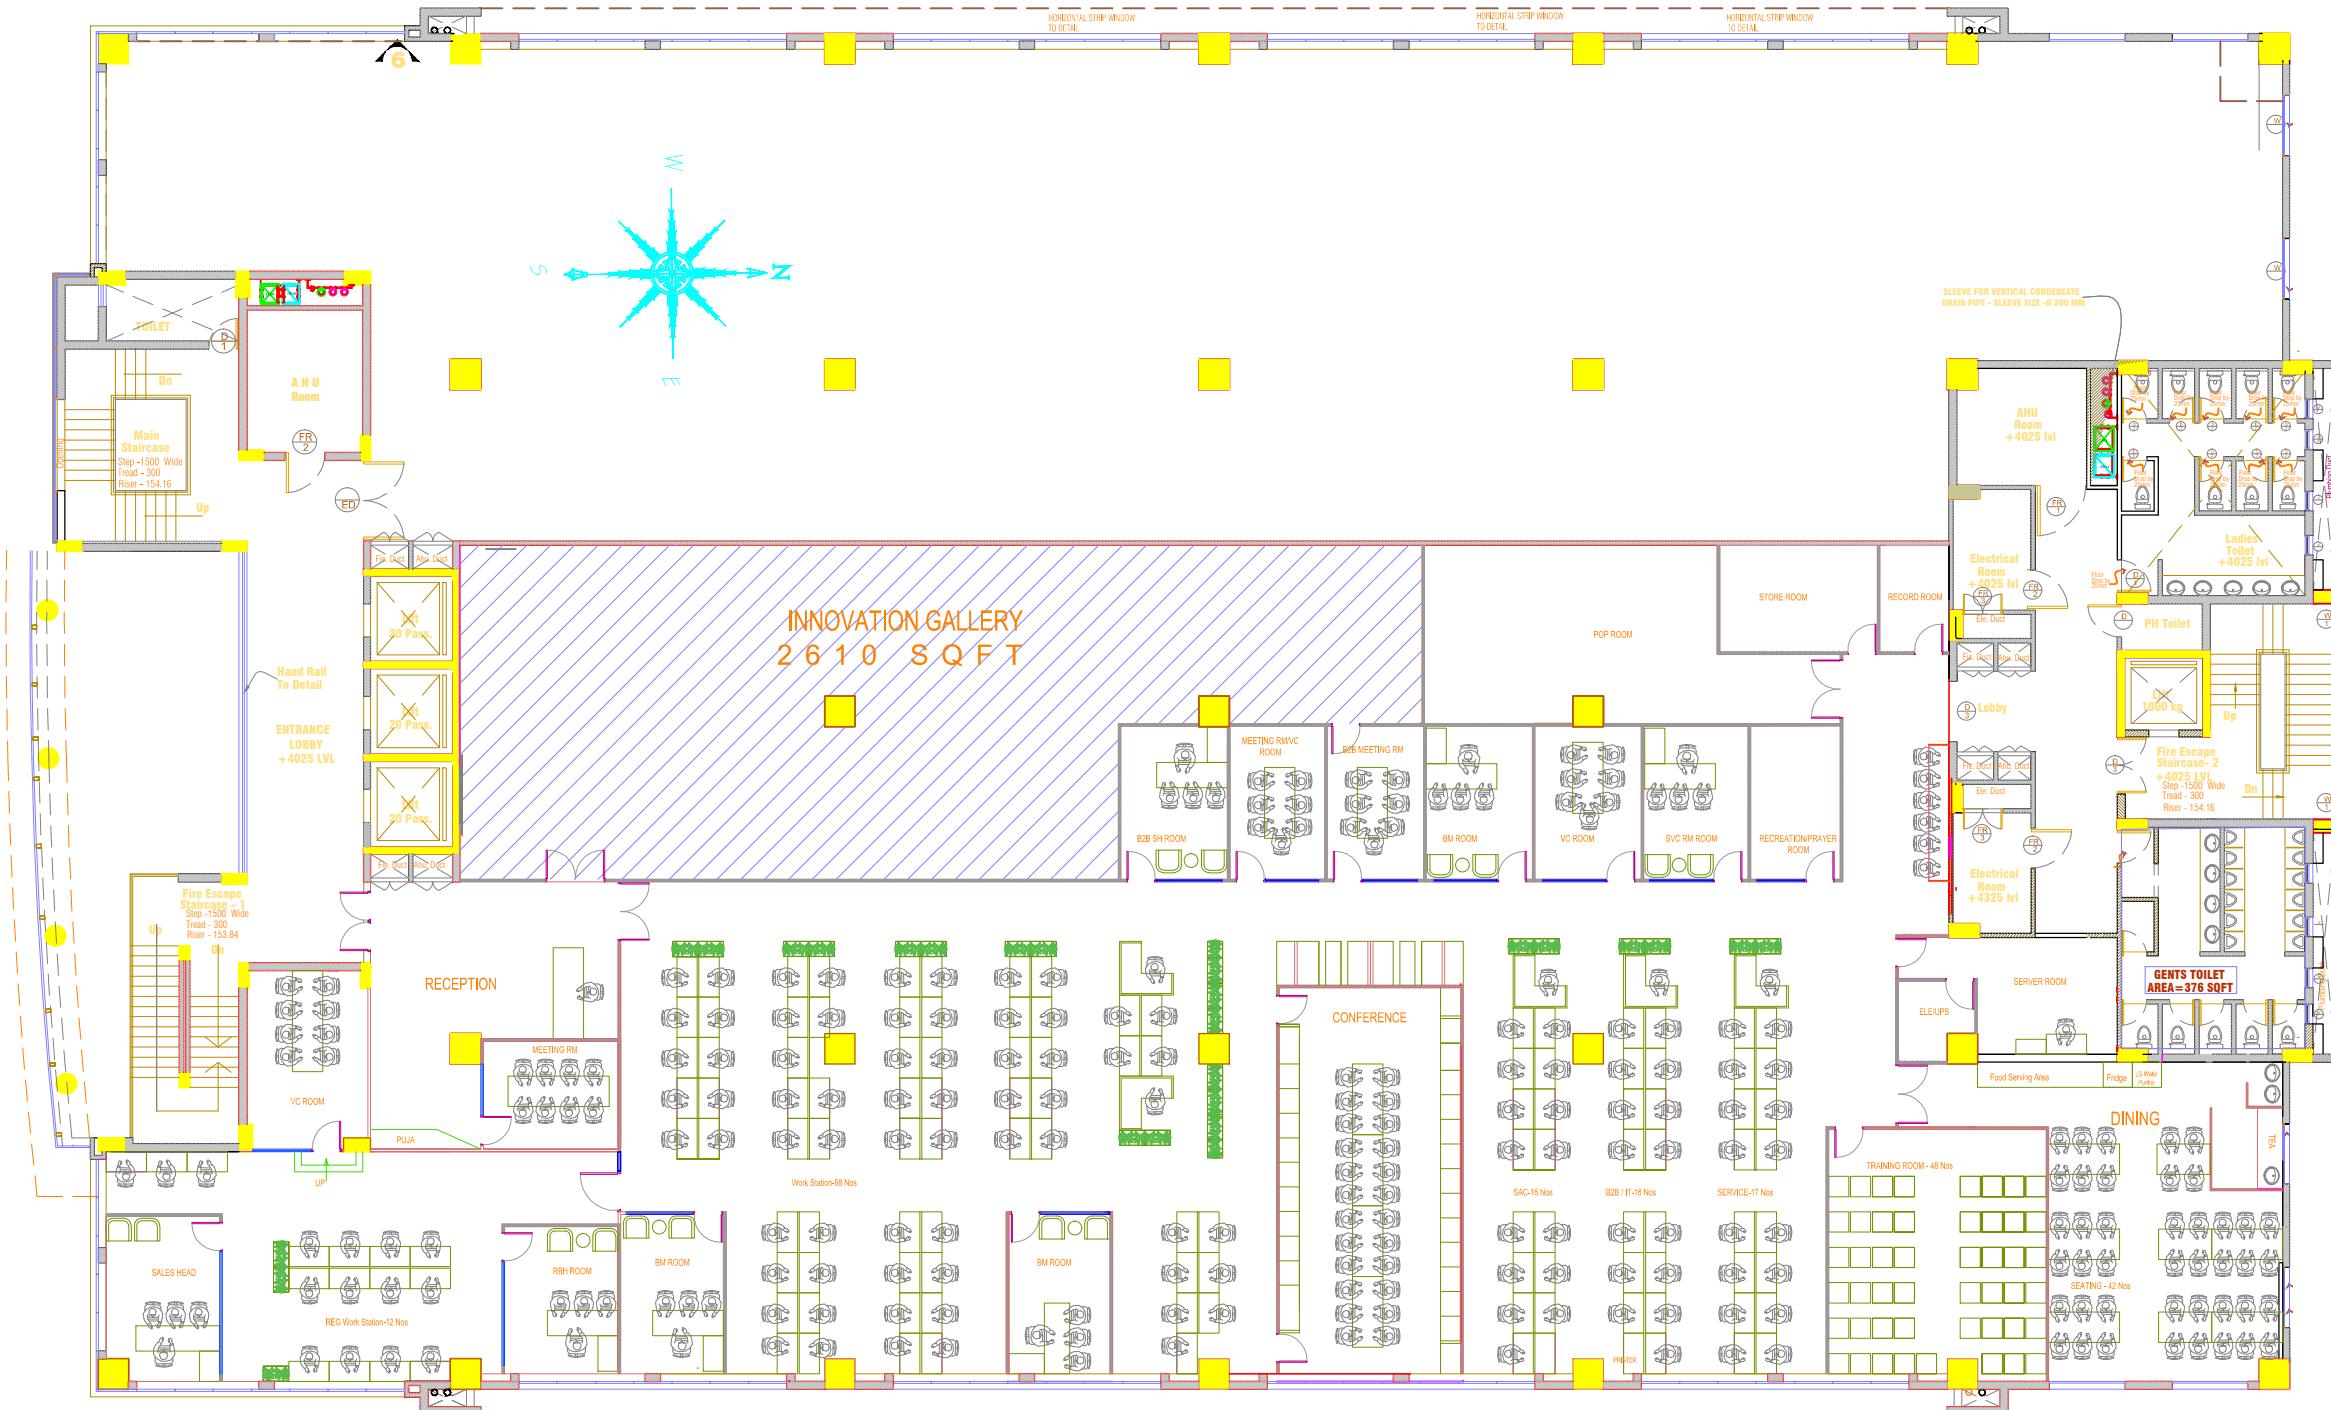

OFFICE AREA: 11298 + 182 (server Room) = 11480 SQFT.

Innovation Gallery: 2610 SQFT.

Total Carpet Area: 14090 SQFT.

Total Seating Capacity: 135 pax

CLIENT

LG ELECTRONICS INDIA PVT. LTD.

PROJECT NAME :

CHENNAI BRANCH OF

DRAWING TITLE :

FLOOR PLAN

DRAWN BY	CHECKED BY
----------	------------

	DATE	SCALE
--	------	-------

05-07-2023 N.T.S.

<u>REVISION</u>	<u>PAPER SIZE</u>
-----------------	-------------------


RU A 3

NOTE :

ALL DIMENSION TO BE CHECKED ON SITE.
DO NOT SCALE FROM THIS DRAWING.

DO NOT SCALE FROM THIS DRAWING.

HS Ad GIIR Communications India Pvt. Ltd.
KP Towers, Tower D, 12th Floor, Plot
No. C-001B, Sector-16B,
Noida, Uttar Pradesh-201301.

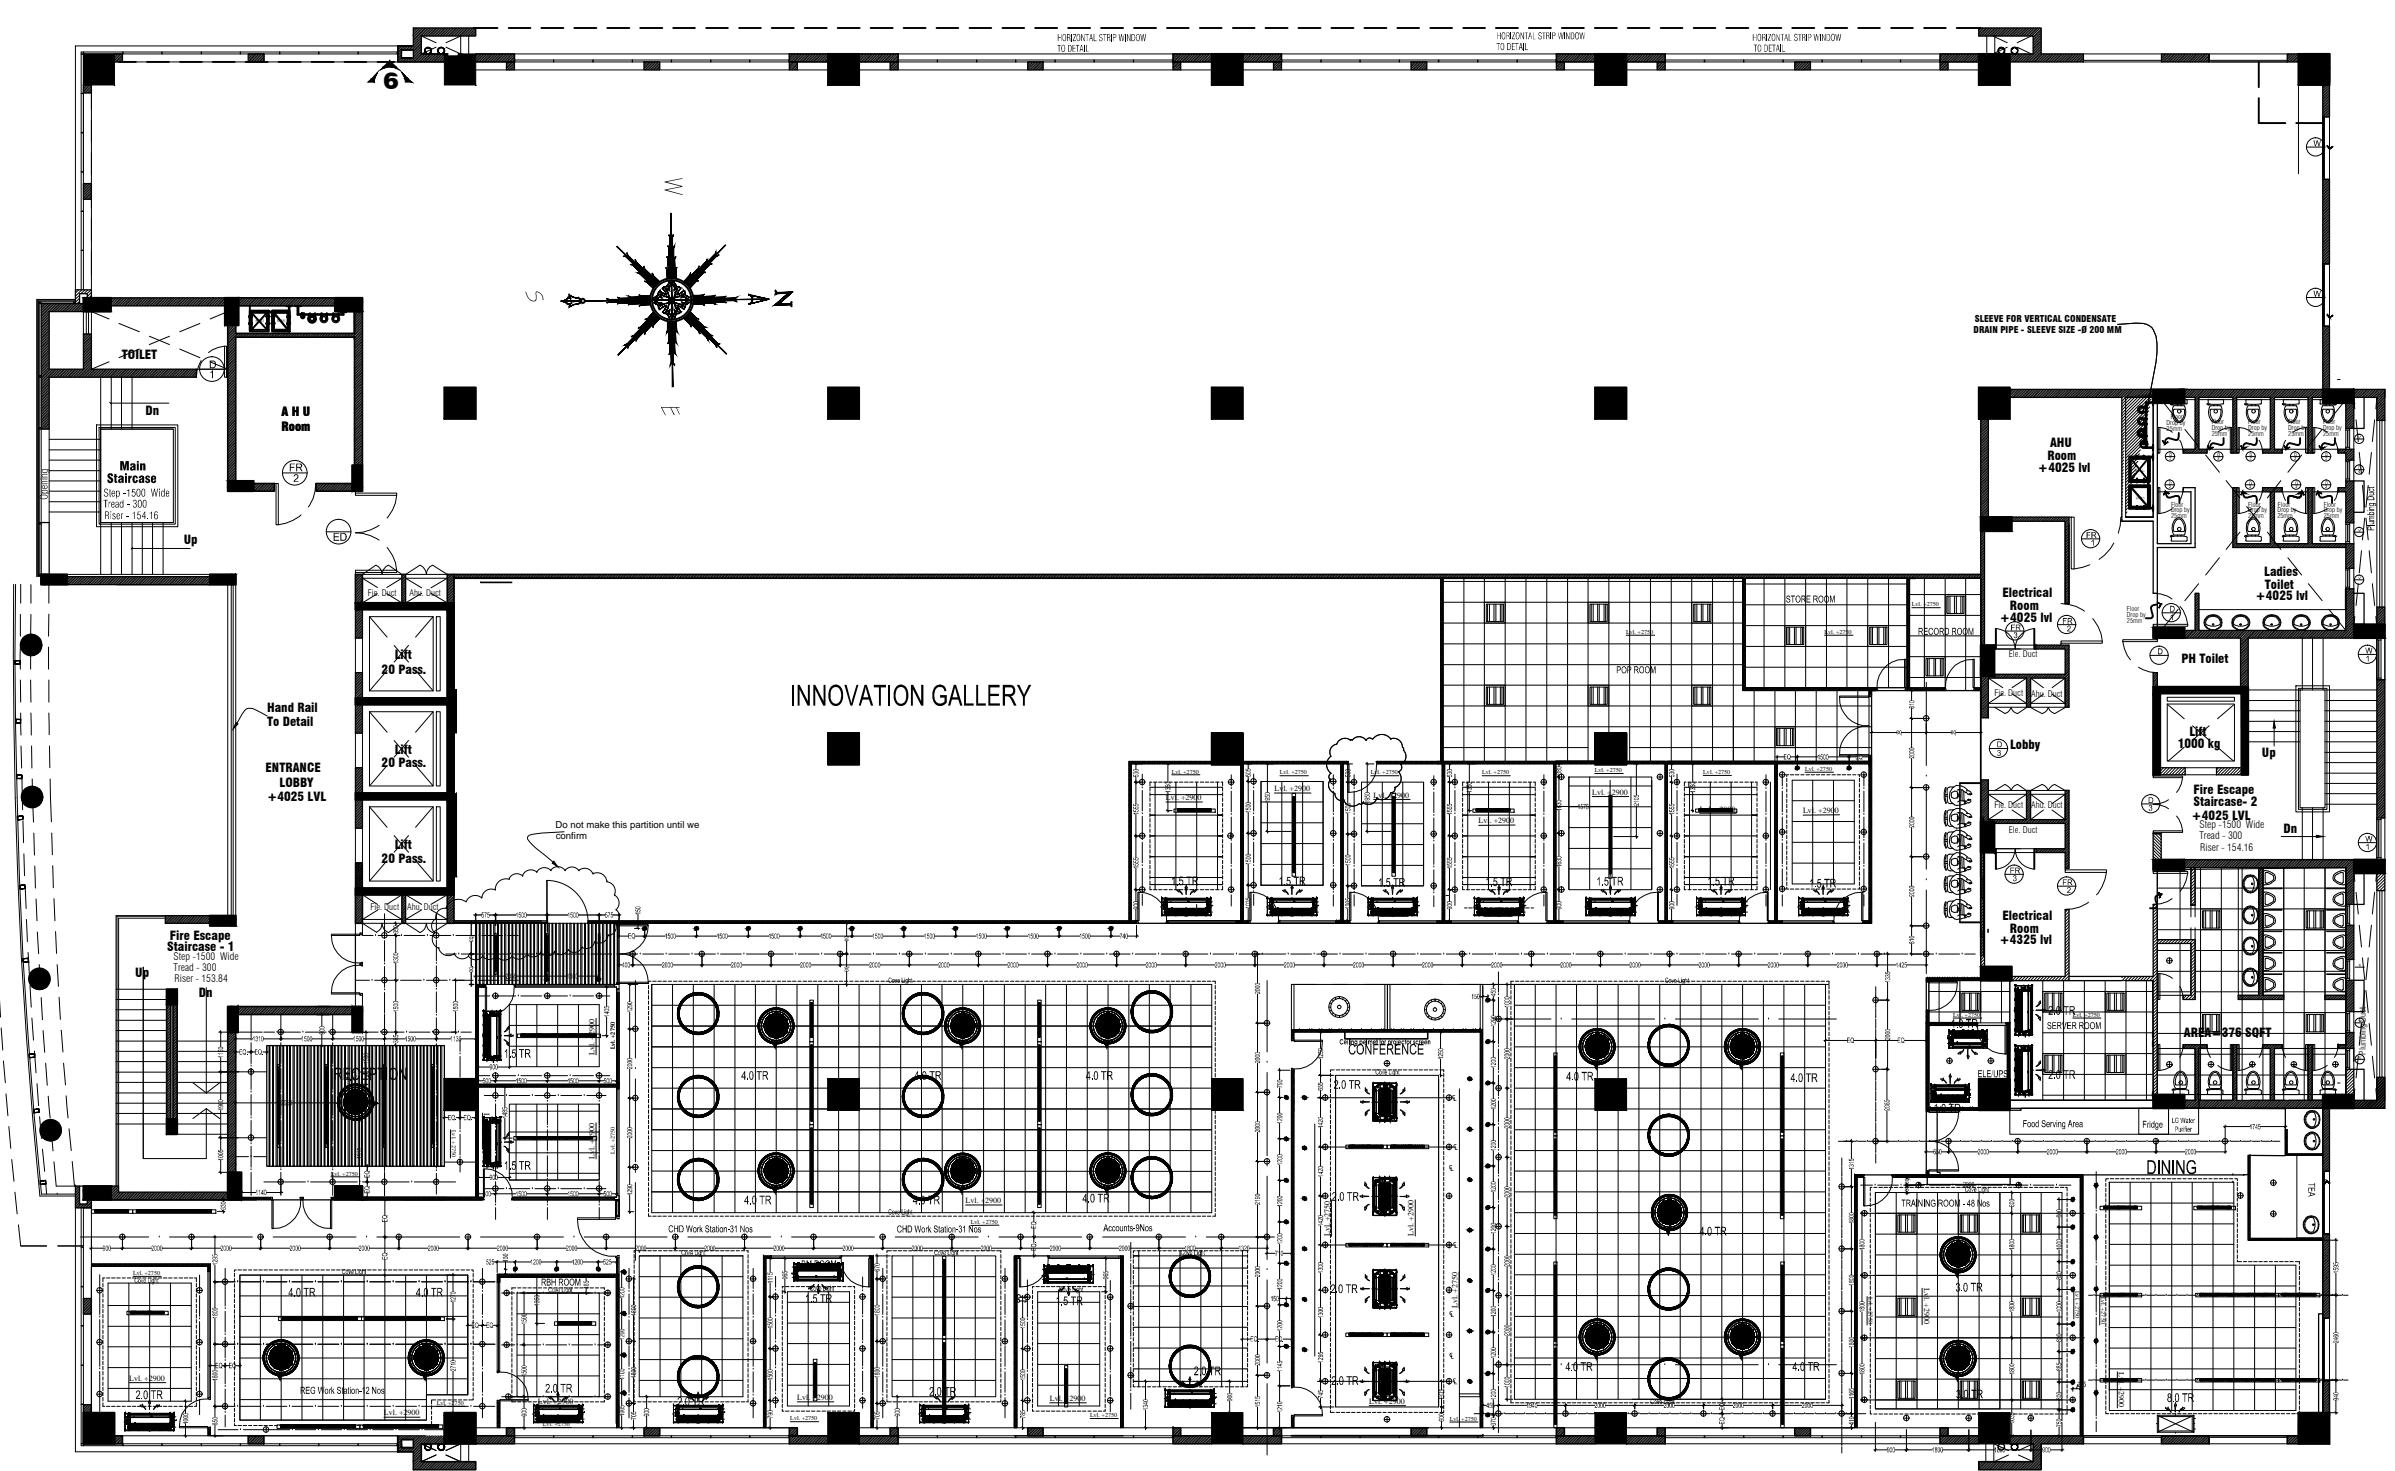

LIGHTING LEGEND			
SYMBOL	TYPE	LOCATION	QTY.
	Hanging Light - Type 1	Reception	02
	Hanging Light - Type 2	Collaborative Space	02
	Hanging Light - Type 3	Open Seating Area	18
	Hanging Light - Type 4	Workhall+Reception + Cabin+Board Room+Entry Pooja lobby	85
	Downlighter - 4' Dia Round	Working Hall (Seating)+ Walkway+Reception	107
	Downlighter - 6' Dia Round	Rest All Area	110
	Spot Light	Training room+TT room+Break Out+Workhall+Board meeting	57
	2X2' downlight	Kitchen+Server Room +ELE/UPS+TT+POP+Record	24
	Access control	All areas	05
	Camera	All areas	12

CLIENT:

PROJECT NAME :
CHENNAI BRANCH OFFICE

DRAWING TITLE :


LIGHTING LAYOUT

DRAWN BY	CHECKED BY
----------	------------

<u>DATE</u> 27-06-2023	<u>SCALE</u> N.T.S.
<u>REVISION</u> R0	<u>PAPER SIZE</u> A 3

NOTE :


ALL DIMENSION TO BE CHECKED ON SITE.
DO NOT SCALE FROM THIS DRAWING.

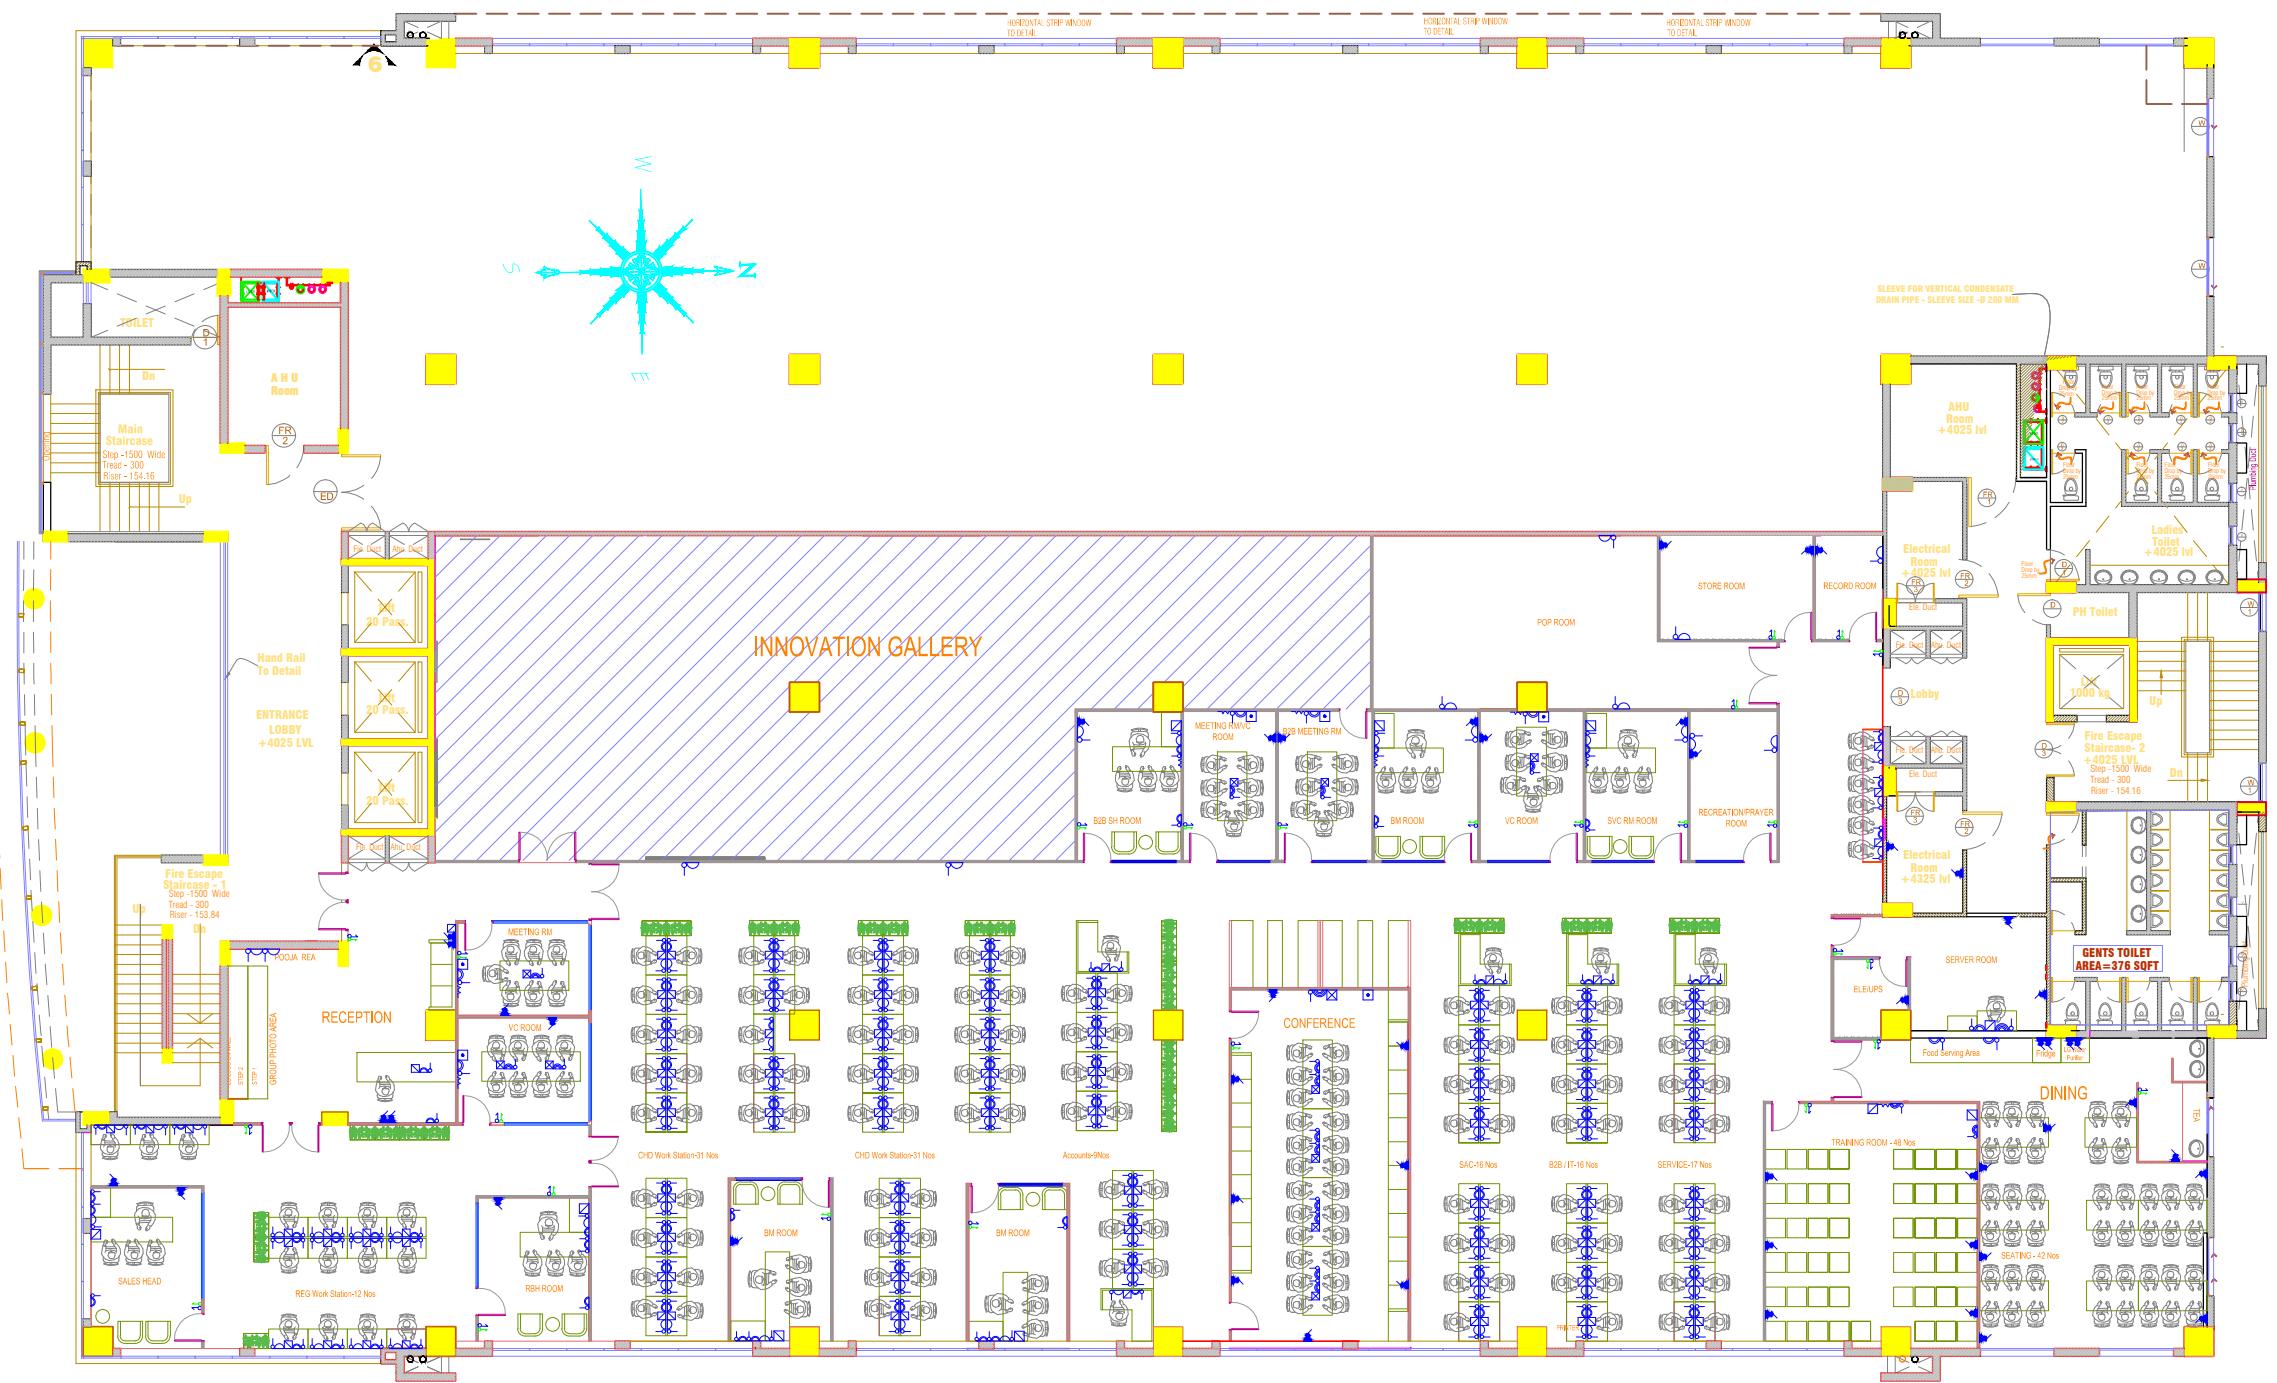

CLIENT:	
LG ELECTRONICS INDIA PVT. LTD.	
PROJECT NAME :	
CHENNAI BRANCH OFFICE	
DRAWING TITLE :	
POWER LAYOUT	
DRAWN BY	CHECKED BY
DATE	SCALE
14-04-2023	N.T.S.
REVISION	PAPER SIZE
R0	A 3

NOTE :
ALL DIMENSION TO BE CHECKED ON SITE.
DO NOT SCALE FROM THIS DRAWING.

HS Ad
GIIR Communications India Pvt. Ltd.
KP Towers, Tower D, 12th Floor, Plot
No. C-001B, Sector-16B,
Noida, Uttar Pradesh-201301.

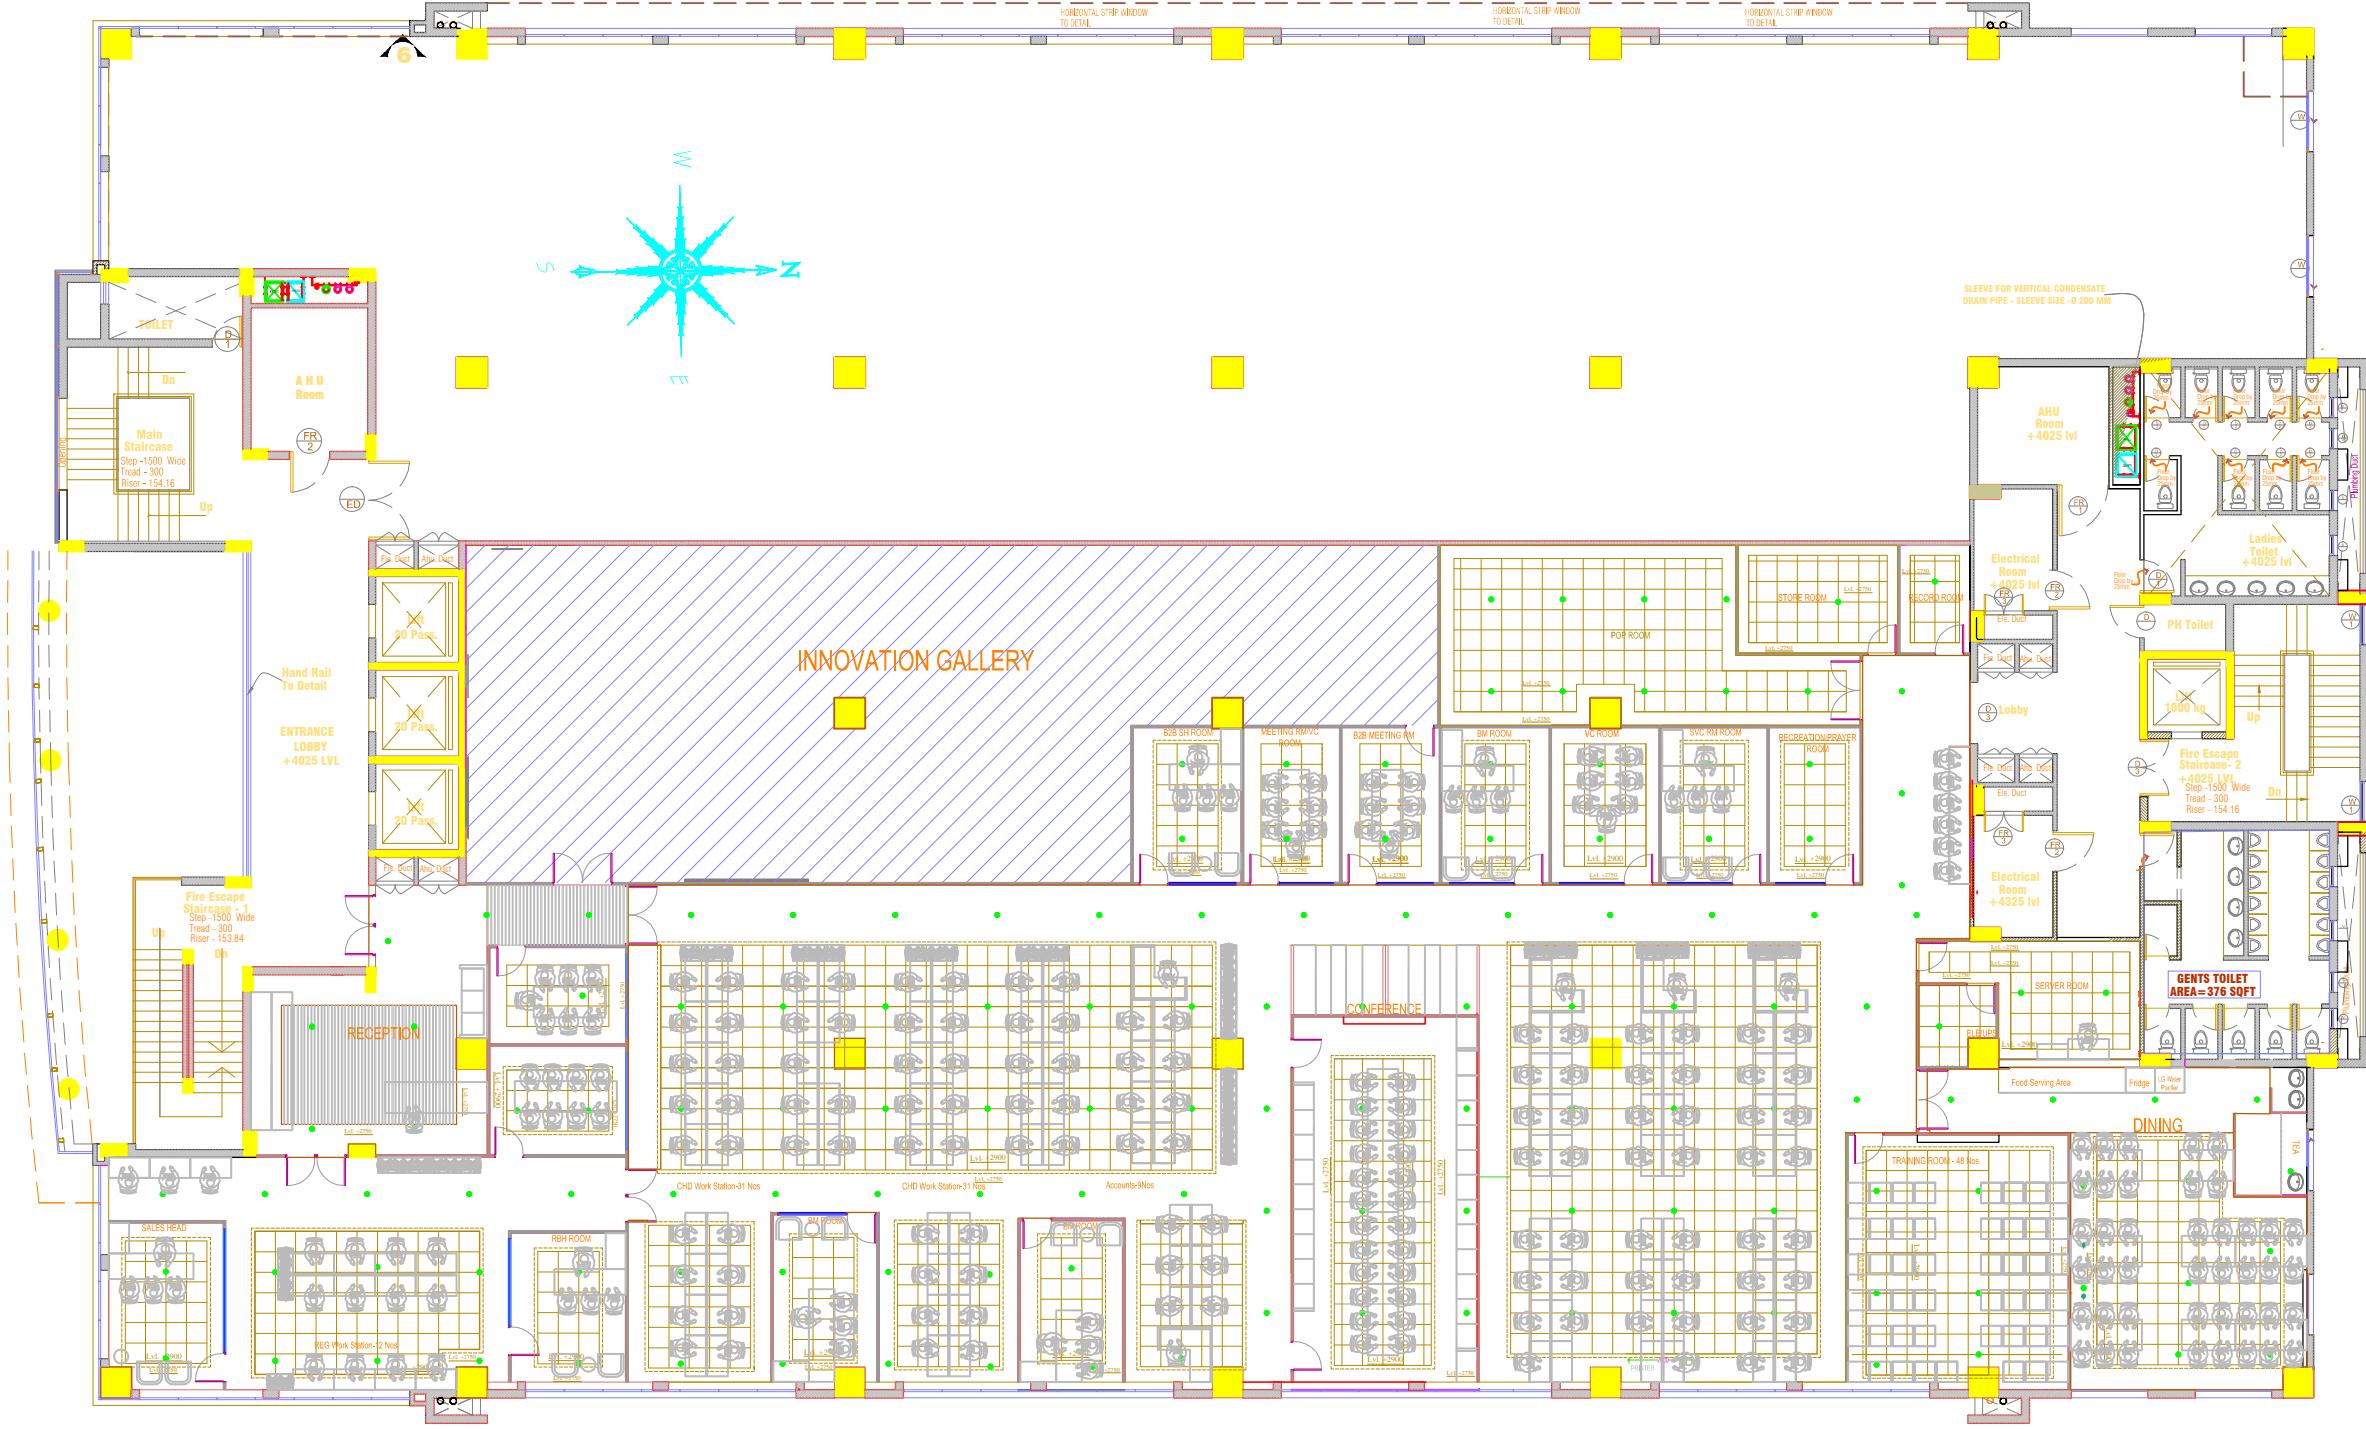


CLIENT:	
LG ELECTRONICS INDIA PVT. LTD.	
PROJECT NAME :	
CHENNAI BRANCH OFFICE	
DRAWING TITLE :	
FIRE SPRINKLER LAYOUT	
DRAWN BY	CHECKED BY
DATE	SCALE
14-04-2023	N.T.S.
REVISION	PAPER SIZE
R0	A 3

NOTE :

ALL DIMENSION TO BE CHECKED ON SITE.
DO NOT SCALE FROM THIS DRAWING.


GIIR Communications India Pvt. Ltd.
KP Towers, Tower D, 12th Floor, Plot
No. C-001B, Sector-16B,
Noida, Uttar Pradesh-201301.

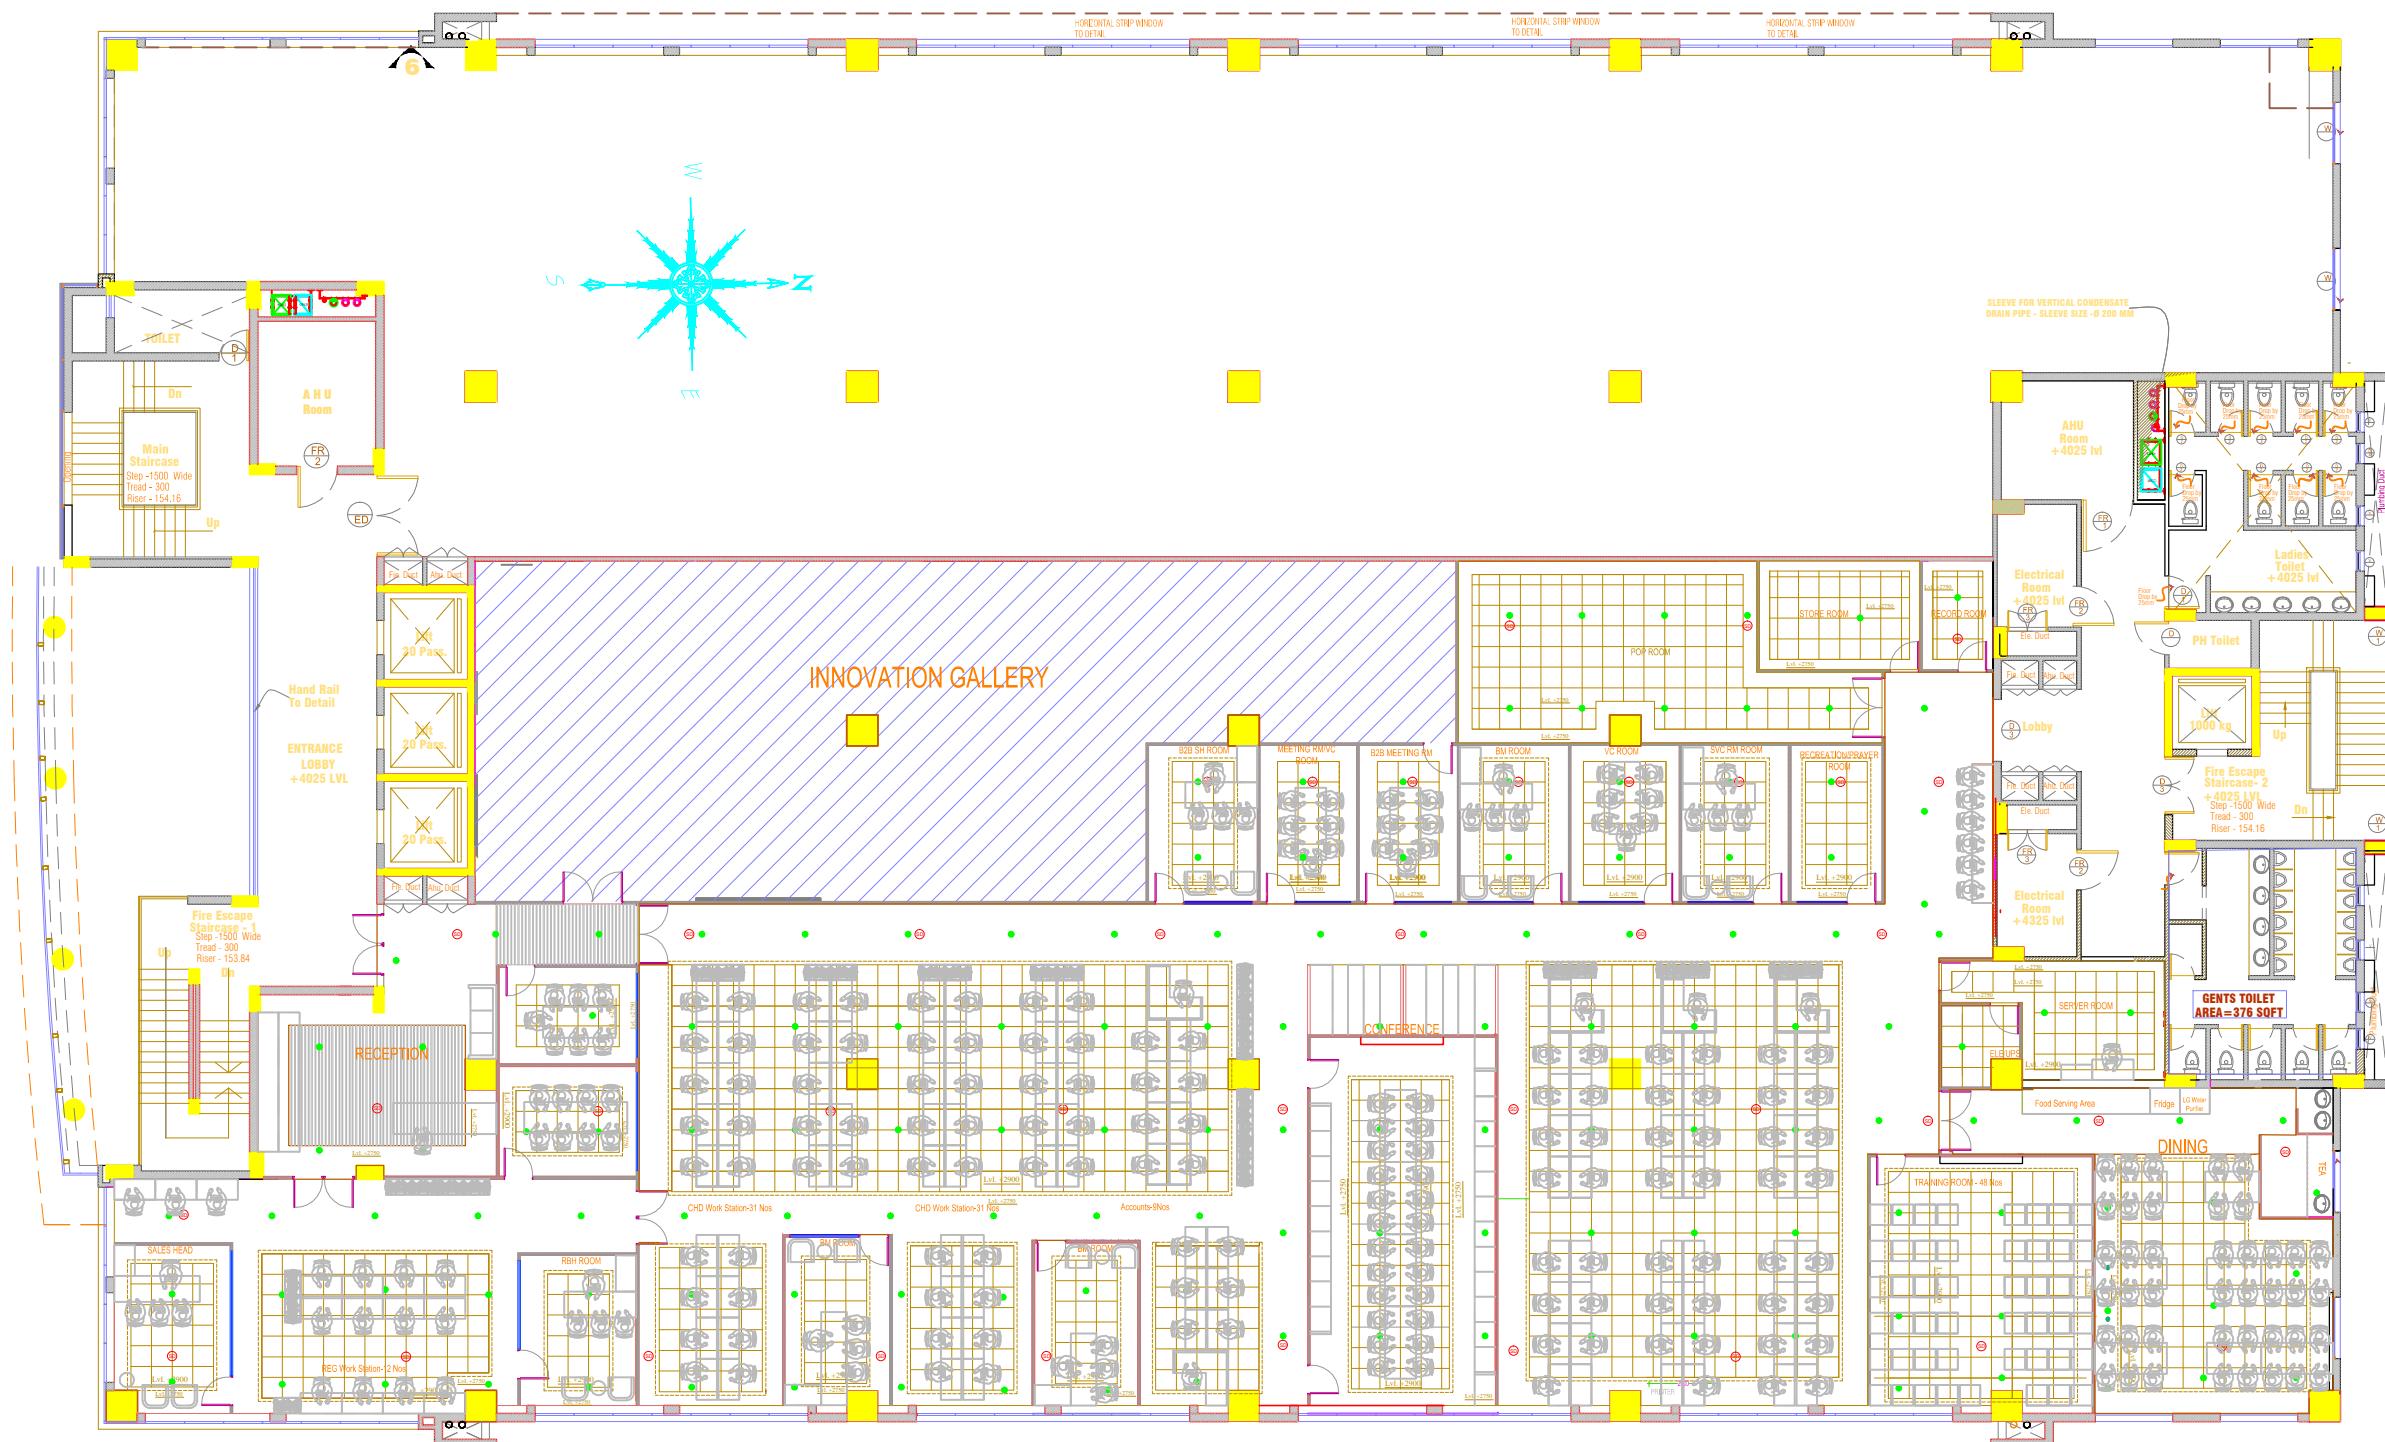

CLIENT:	
LG ELECTRONICS INDIA PVT. LTD.	
PROJECT NAME:	
CHENNAI BRANCH OFFICE	
DRAWING TITLE:	FIRE LAYOUT
DRAWN BY	CHECKED BY
DATE	SCALE
14-04-2023	N.T.S.
REVISION	PAPER SIZE
R0	A 3

NOTE :

ALL DIMENSION TO BE CHECKED ON SITE.
DO NOT SCALE FROM THIS DRAWING.


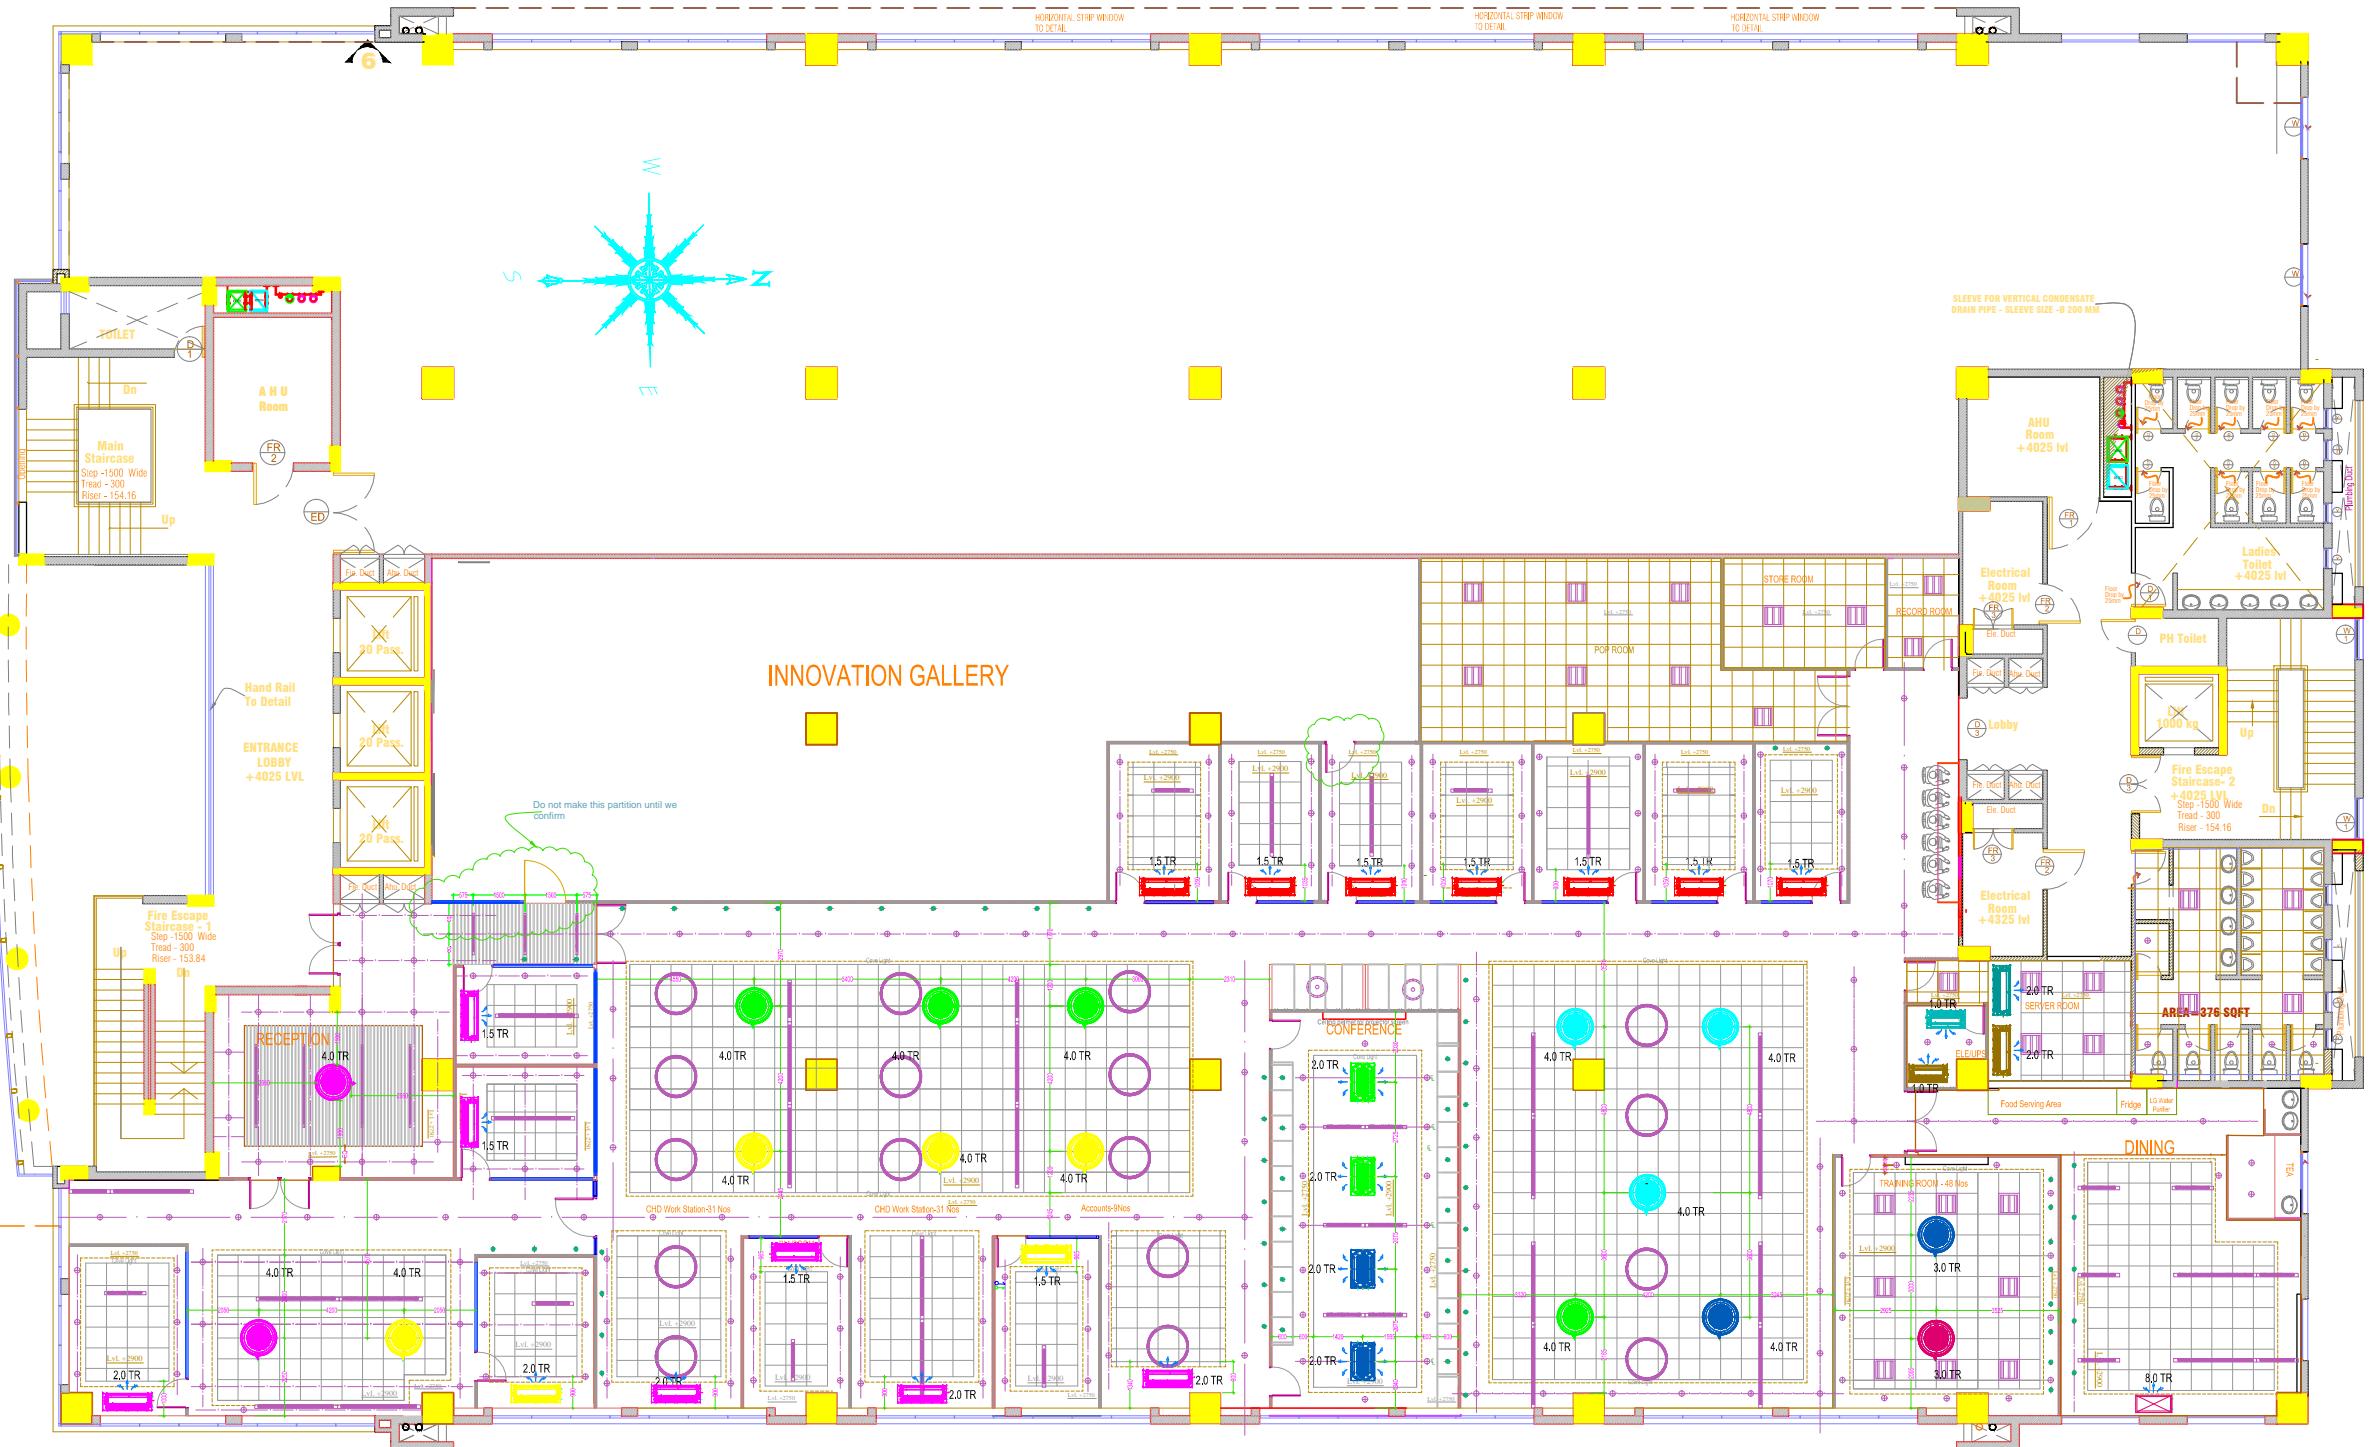


CLIENT:	
LG ELECTRONICS INDIA PVT. LTD.	
PROJECT NAME:	
CHENNAI BRANCH OFFICE	
DRAWING TITLE:	REFLECTED CEILING PLAN
DRAWN BY	CHECKED BY
DATE	SCALE
27-06-2023	N.T.S.
REVISION	PAPER SIZE
R0	A 3

NOTE :

ALL DIMENSION TO BE CHECKED ON SITE.
DO NOT SCALE FROM THIS DRAWING.

HS Ad	GIIR Communications India Pvt. Ltd. KP Towers, Tower D, 12th Floor, Plot No. C-001B, Sector-16B, Noida, Uttar Pradesh-201301.
-------	--

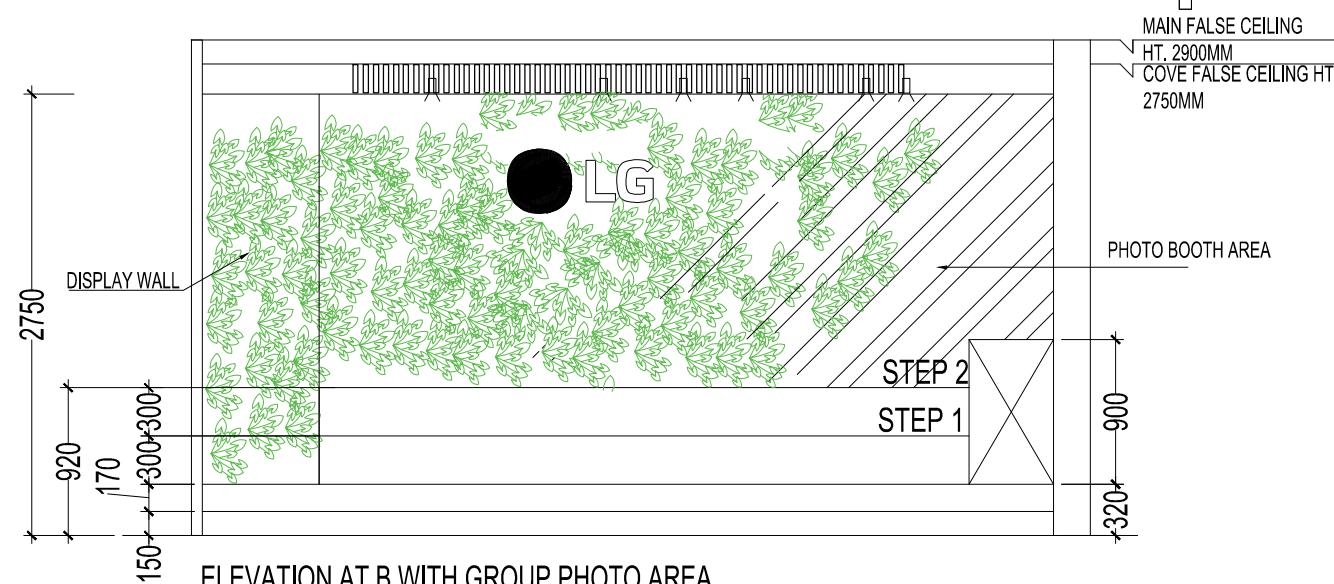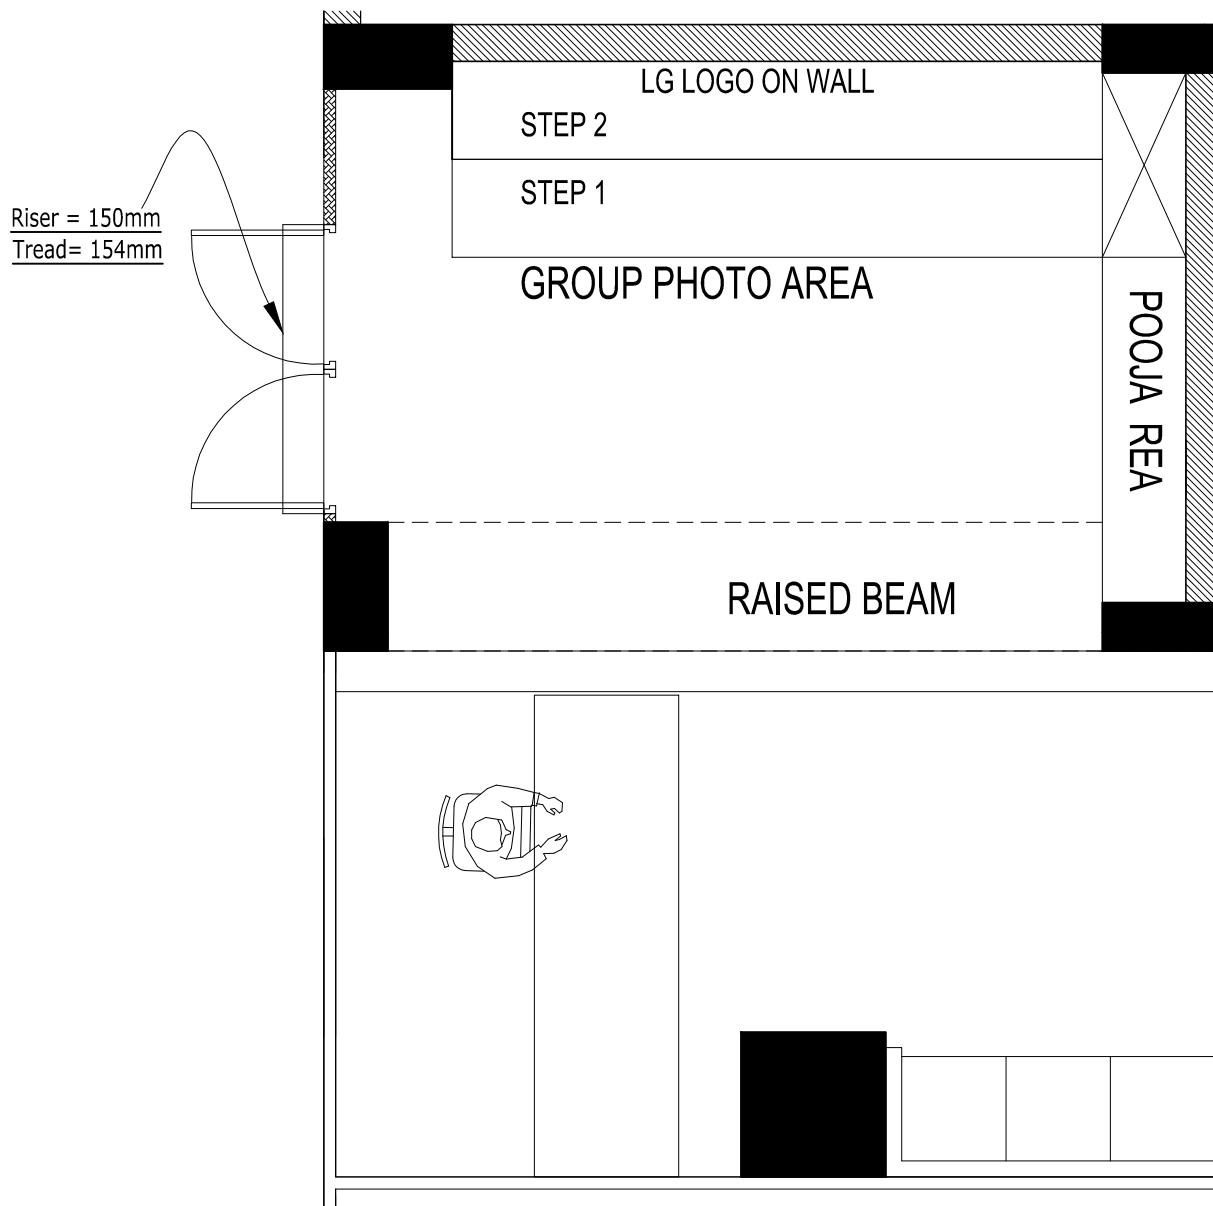




DATE	REV.	DESCRIPTION

CLIENT:	LG ELECTRONICS INDIA PVT. LTD.
PROJECT NAME:	CHENNAI BRANCH OFFICE
DRAWING TITLE:	GROUP PHOTO SHOOT AREA
DRAWN BY	CHECKED BY

DATE	SCALE
26-04-2023	N.T.S.
REVISION	PAPER SIZE
R0	A 3

NOTE :
ALL DIMENSION TO BE CHECKED ON SITE. DO NOT SCALE FROM THIS DRAWING.

HS Ad	GIIR Communications India Pvt. Ltd. KP Towers, Tower D, 12th Floor, Plot No. C-001B, Sector-16B, Noida, Uttar Pradesh-201301.
-------	--

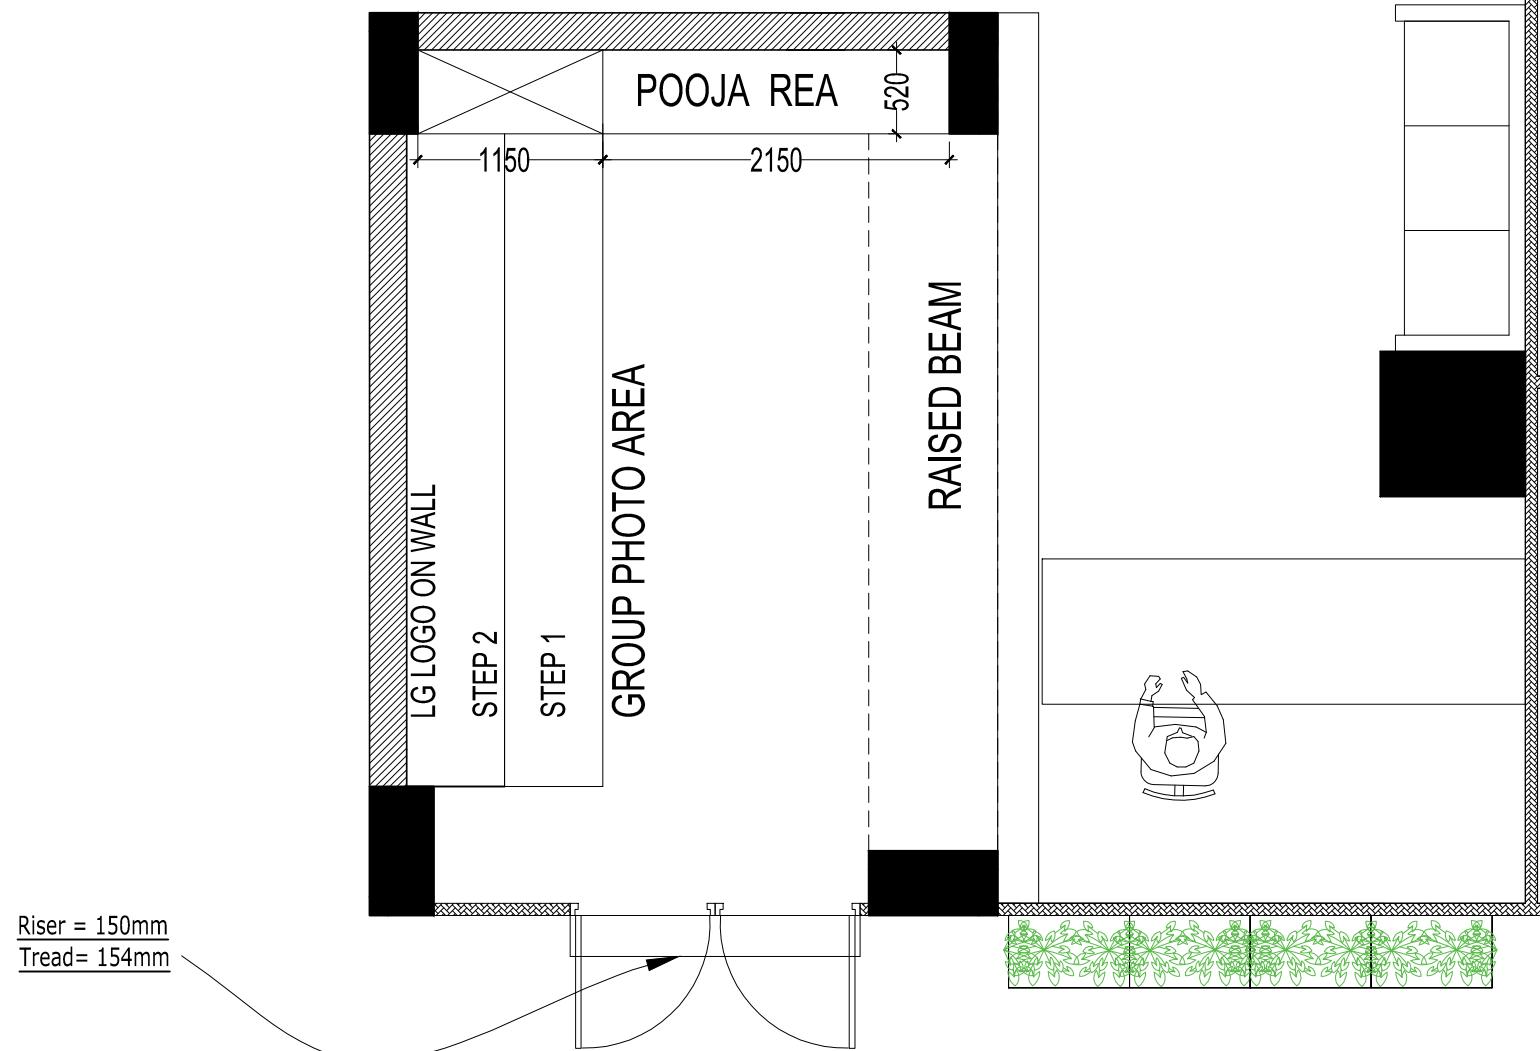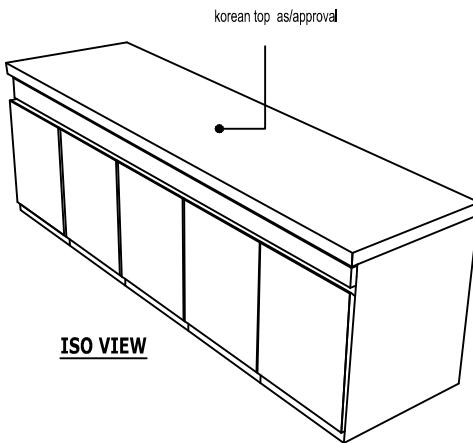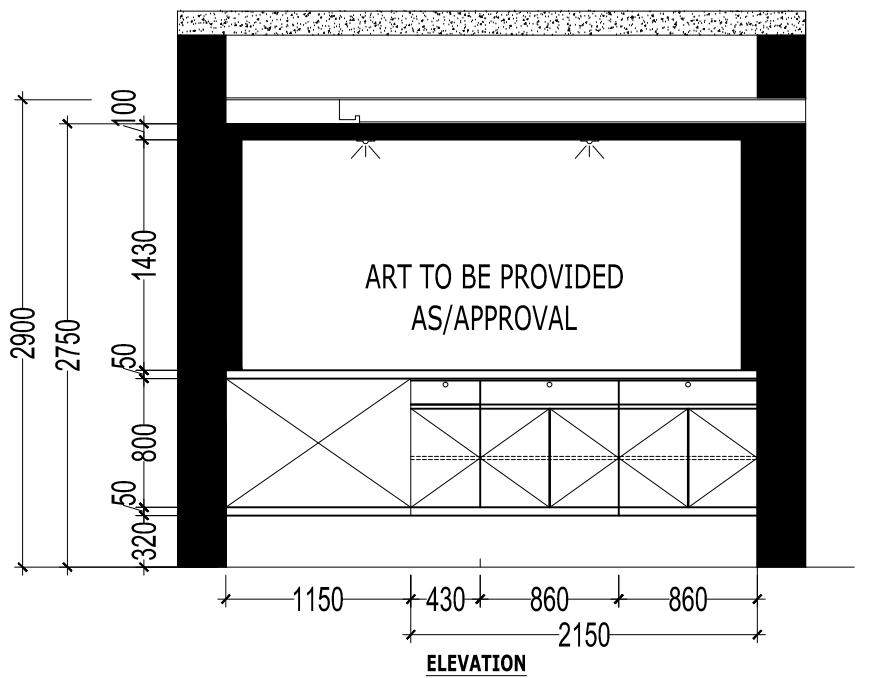


DATE	REV.	DESCRIPTION


CLIENT:	LG ELECTRONICS INDIA PVT. LTD.
PROJECT NAME:	CHENNAI BRANCH OFFICE
DRAWING TITLE:	POOJA AREA ELEVATION
DRAWN BY	CHECKED BY
DATE	SCALE
26-04-2023	N.T.S.
REVISION	PAPER SIZE
R0	A 3

DATE	SCALE
26-04-2023	N.T.S.
REVISION	PAPER SIZE
R0	A 3
NOTE :	
ALL DIMENSION TO BE CHECKED ON SITE. DO NOT SCALE FROM THIS DRAWING.	


HS Ad	GIIR Communications India Pvt. Ltd. KP Towers, Tower D, 12th Floor, Plot No. C-001B, Sector-16B, Noida, Uttar Pradesh-201301.
-------	--

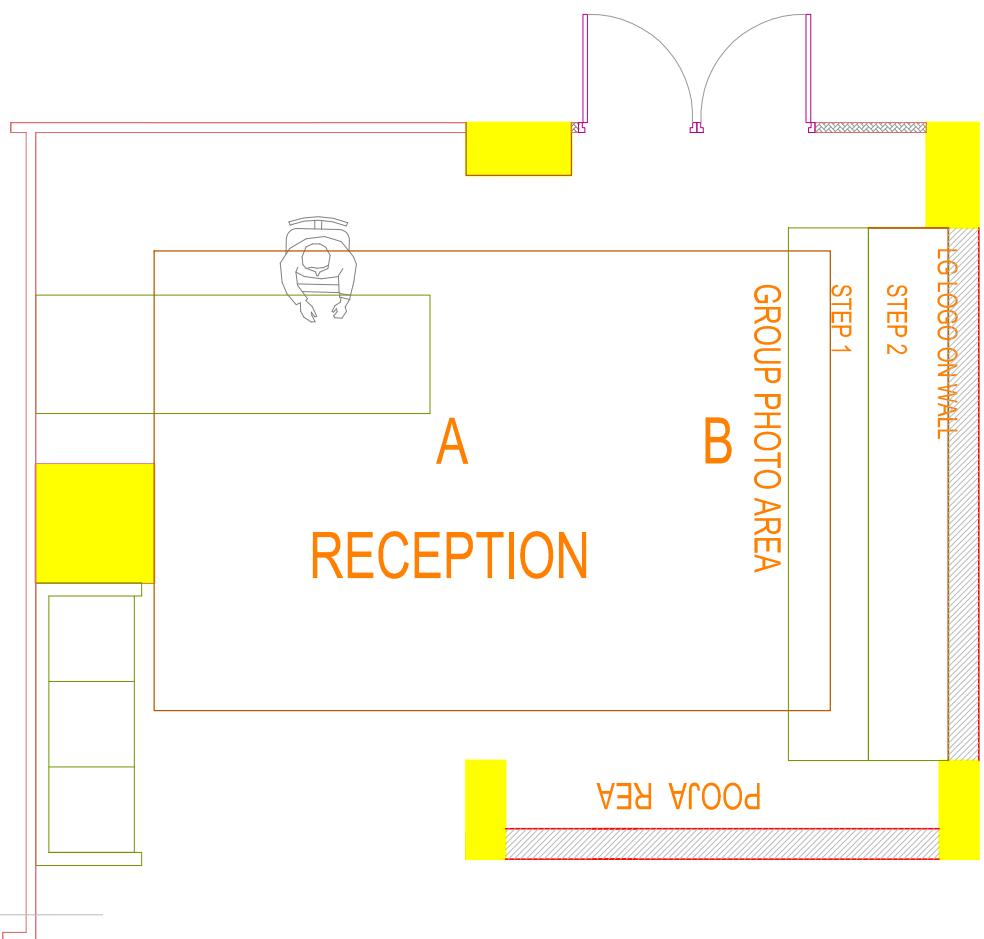

RECEPTION

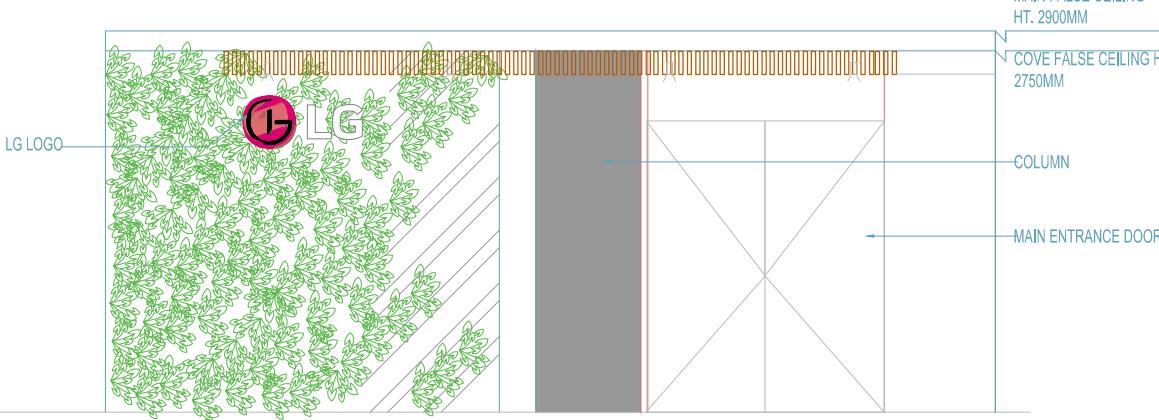

ELEVATION AT A WITHOUT RECEPTION COUNTER

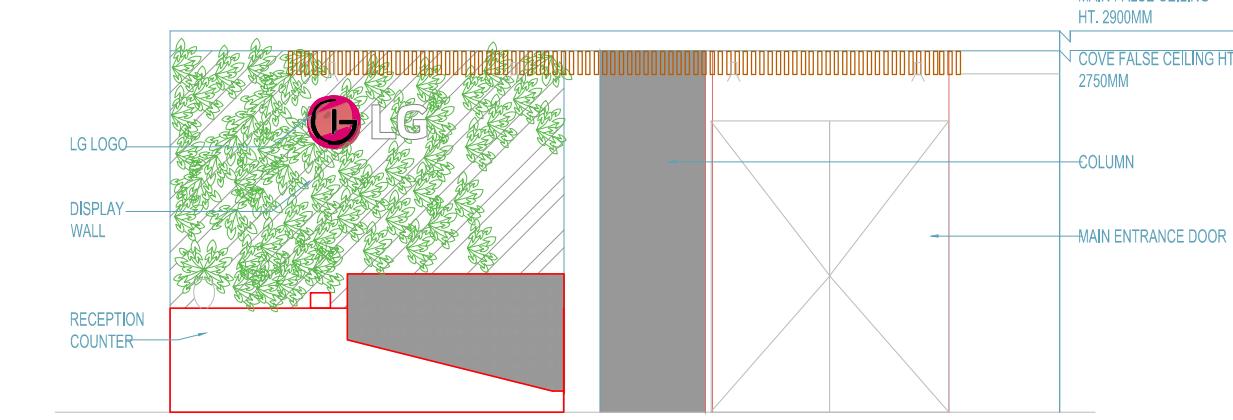

ELEVATION AT A WITH RECEPTION COUNTER

CLIENT:

LG ELECTRONICS INDIA PVT. LTD.

PROJECT NAME :

CHENNAI BRANCH OFFICE

DRAWING TITLE :

SALES HEAD ROOM ELEVATION

DRAWN BY CHECKED BY

DATE SCALE



14-04-2023 N.I.S.

REVISION _____ PAPER SIZE _____


NOTE

NOTE:
ALL DIMENSION TO BE CHECKED ON SITE.
DO NOT SCALE FROM THIS DRAWING.

HS Ad

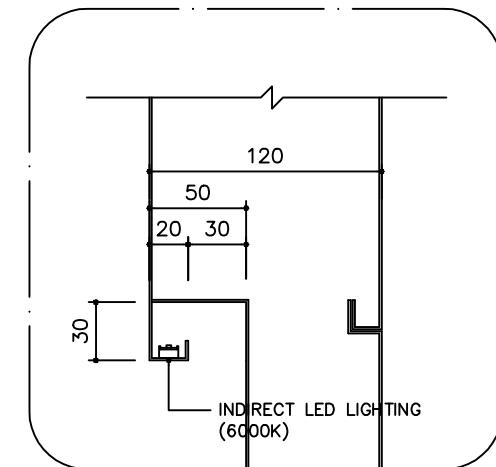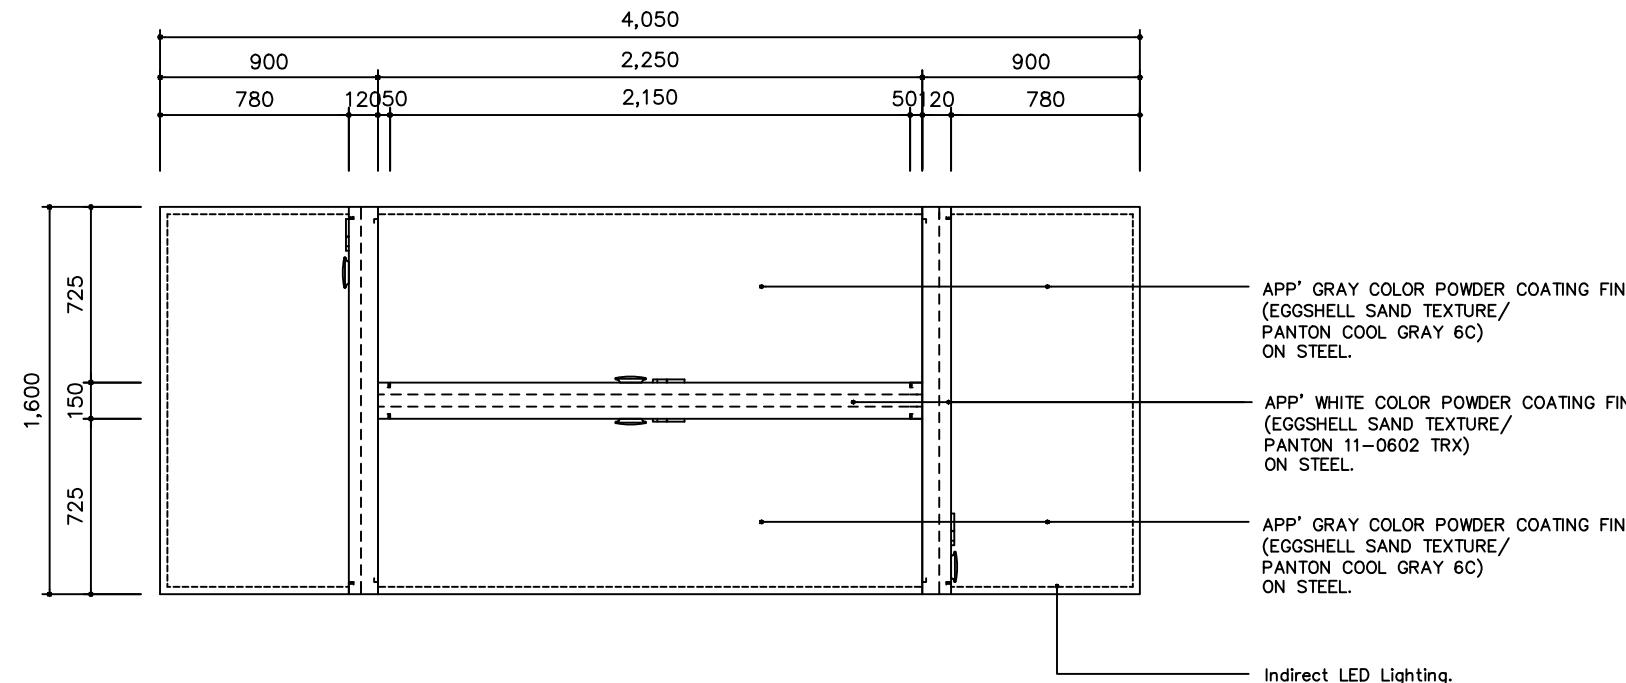


[DETAIL.A]

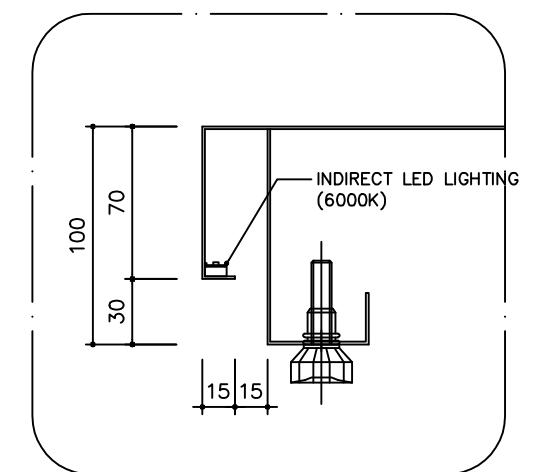


[DETAIL.B]


TOP VIEW
1/30

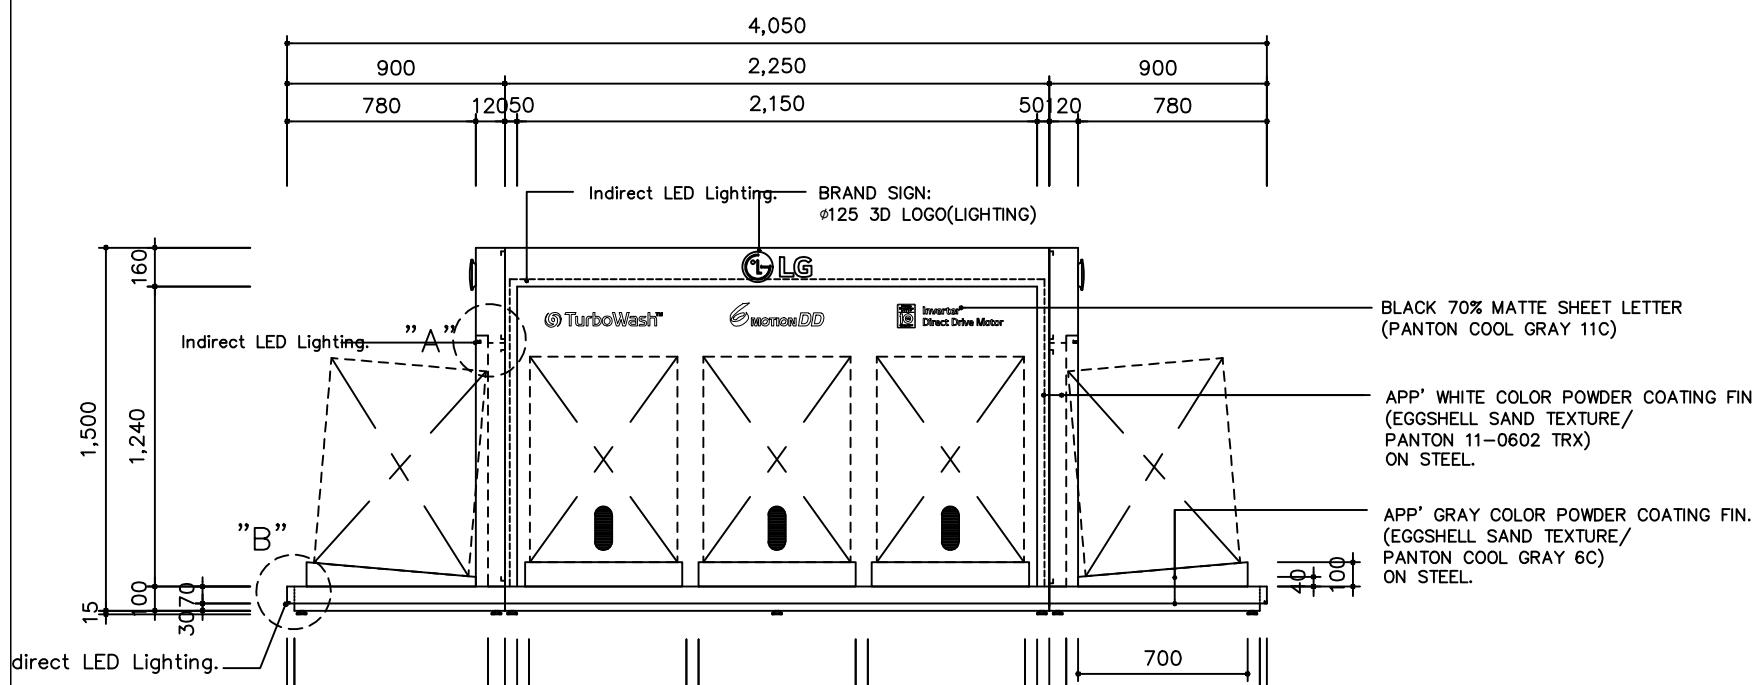



FRONT VIEW
1/30

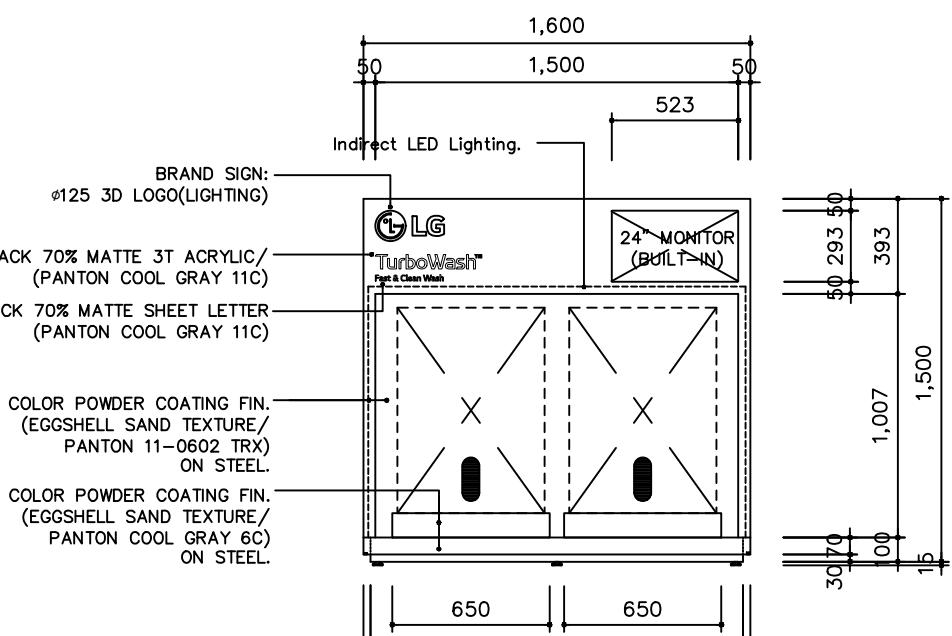


SIDE VIEW
1/30

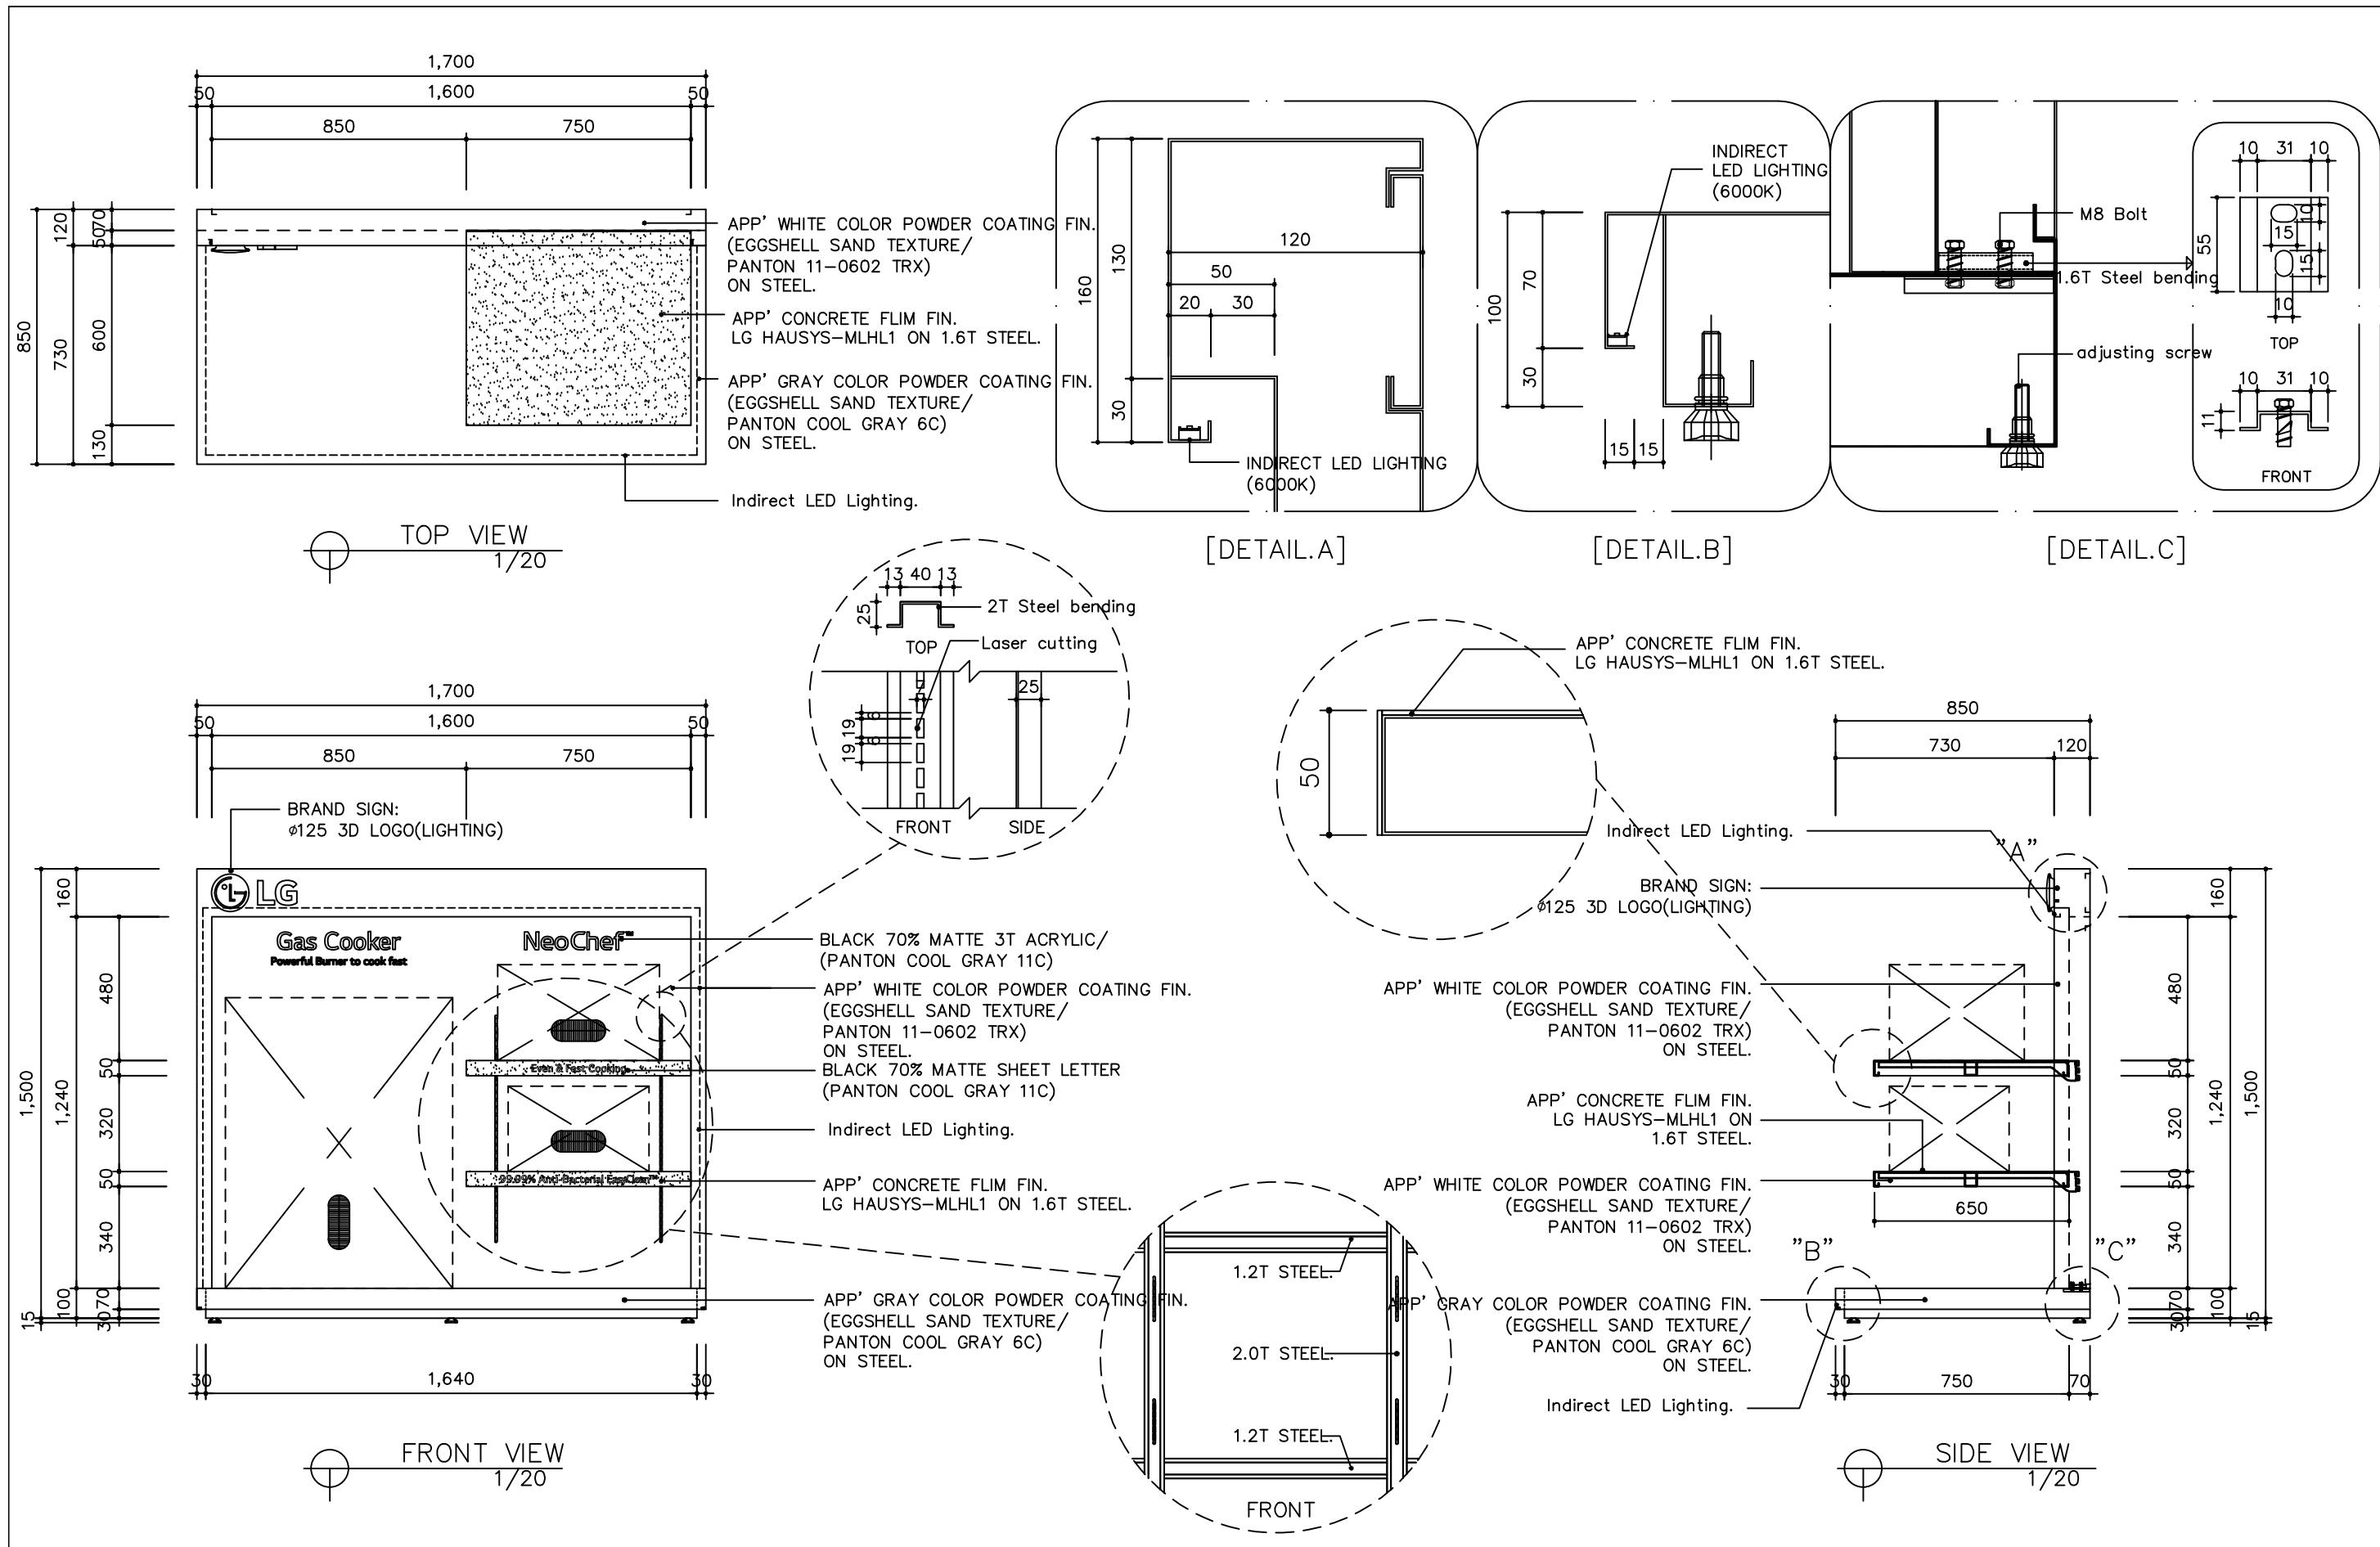



*Ceiling_full lighting type

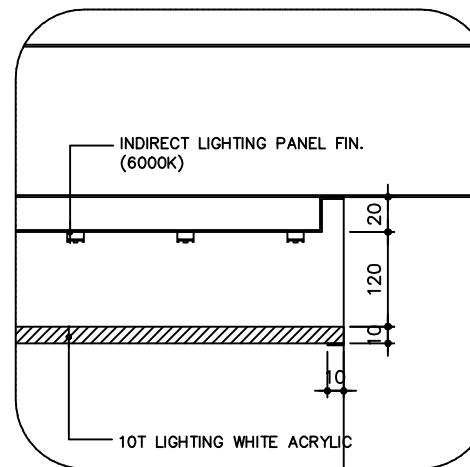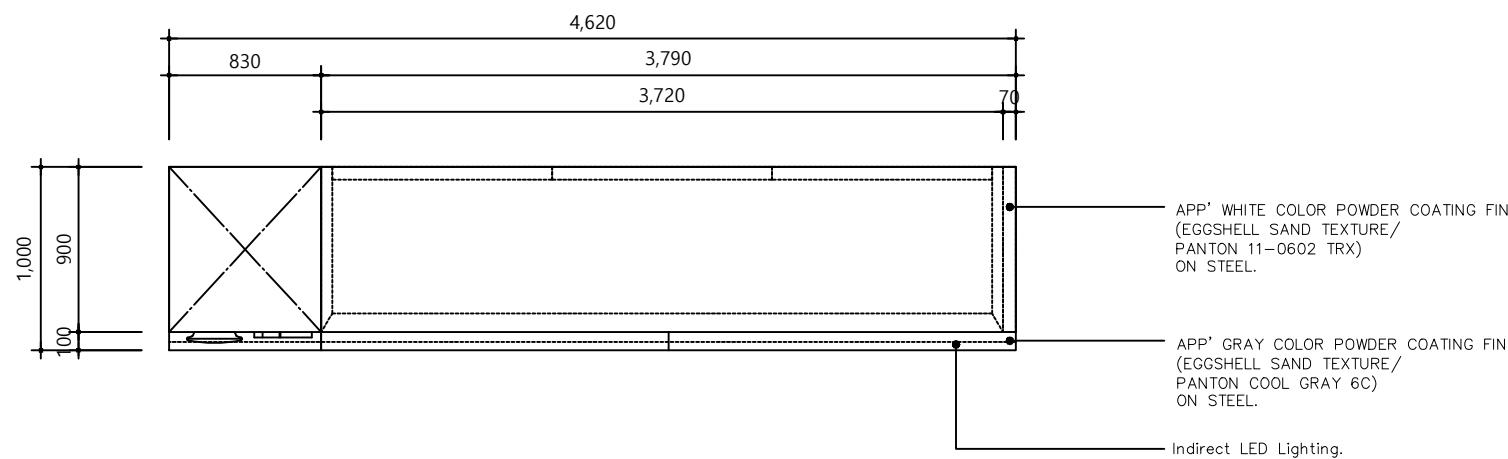


[DETAIL.A]

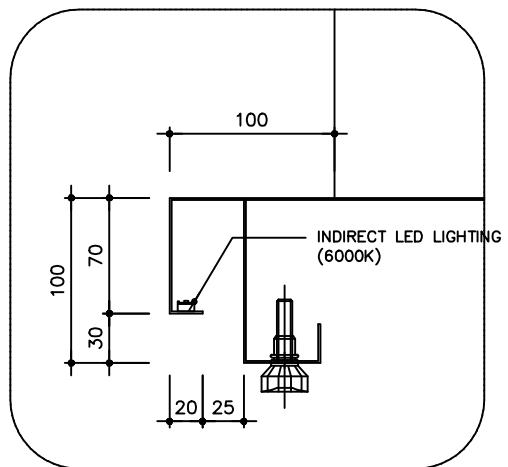


[DETAIL.B]

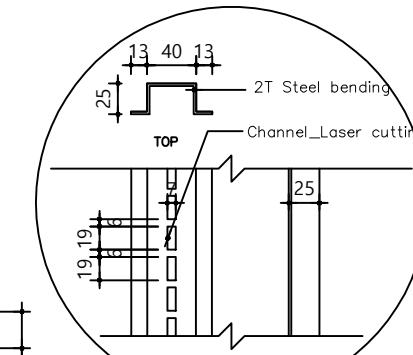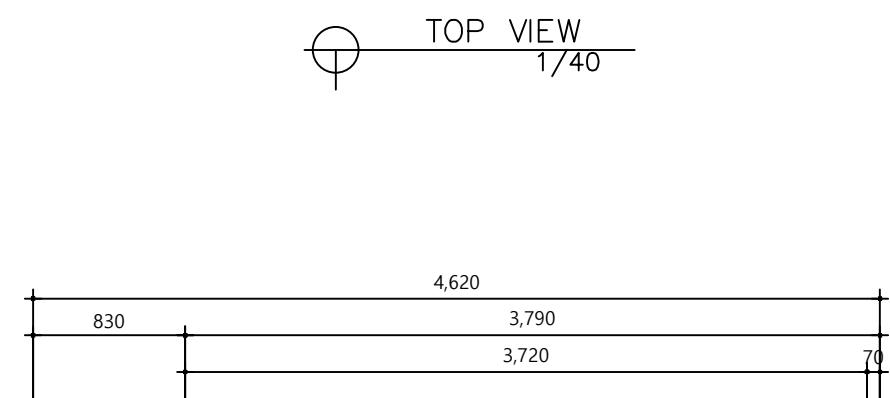


[DETAIL.C]

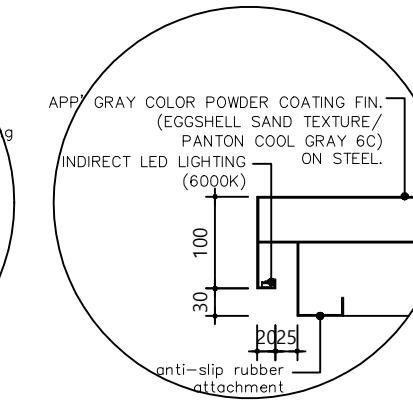

[DETAIL.D]

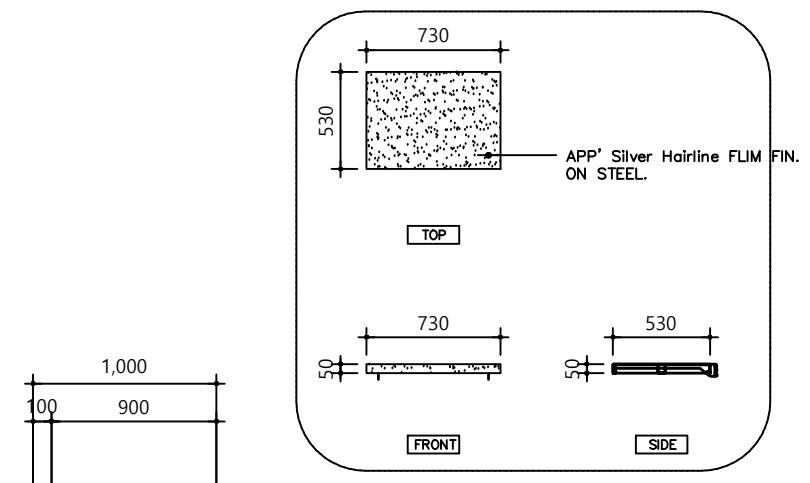

[MWO_SHELF]

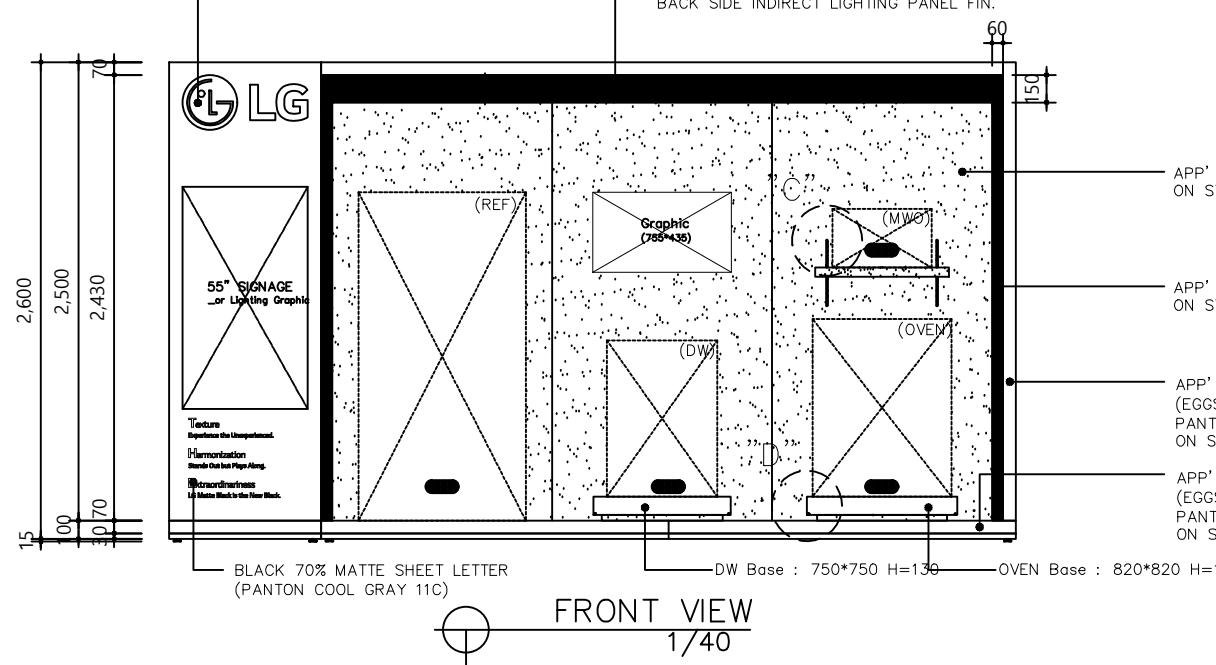

APP' Silver Hairline FLIM FIN. ON STEEL.

APP' Black Hairline FLIM FIN. ON STEEL.


APP' WHITE COLOR POWDER COATING FIN. (EGGHELL SAND TEXTURE/ PANTON 11-0602 TRX) ON STEEL.

APP' GRAY COLOR POWDER COATING FIN. (EGGHELL SAND TEXTURE/ PANTON COOL GRAY 6C) ON STEEL.

APP' WHITE COLOR POWDER COATING FIN. (EGGHELL SAND TEXTURE/ PANTON 11-0602 TRX) ON STEEL.

APP' GRAY COLOR POWDER COATING FIN. (EGGHELL SAND TEXTURE/ PANTON COOL GRAY 6C) ON STEEL.


Indirect LED Lighting

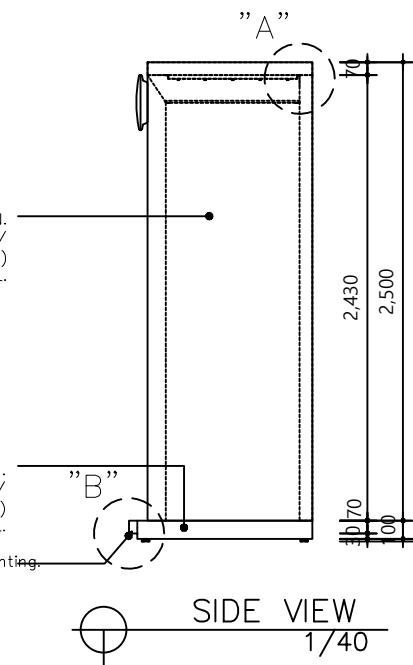


SIDE VIEW
1/40

OZONE


GYM & SPA

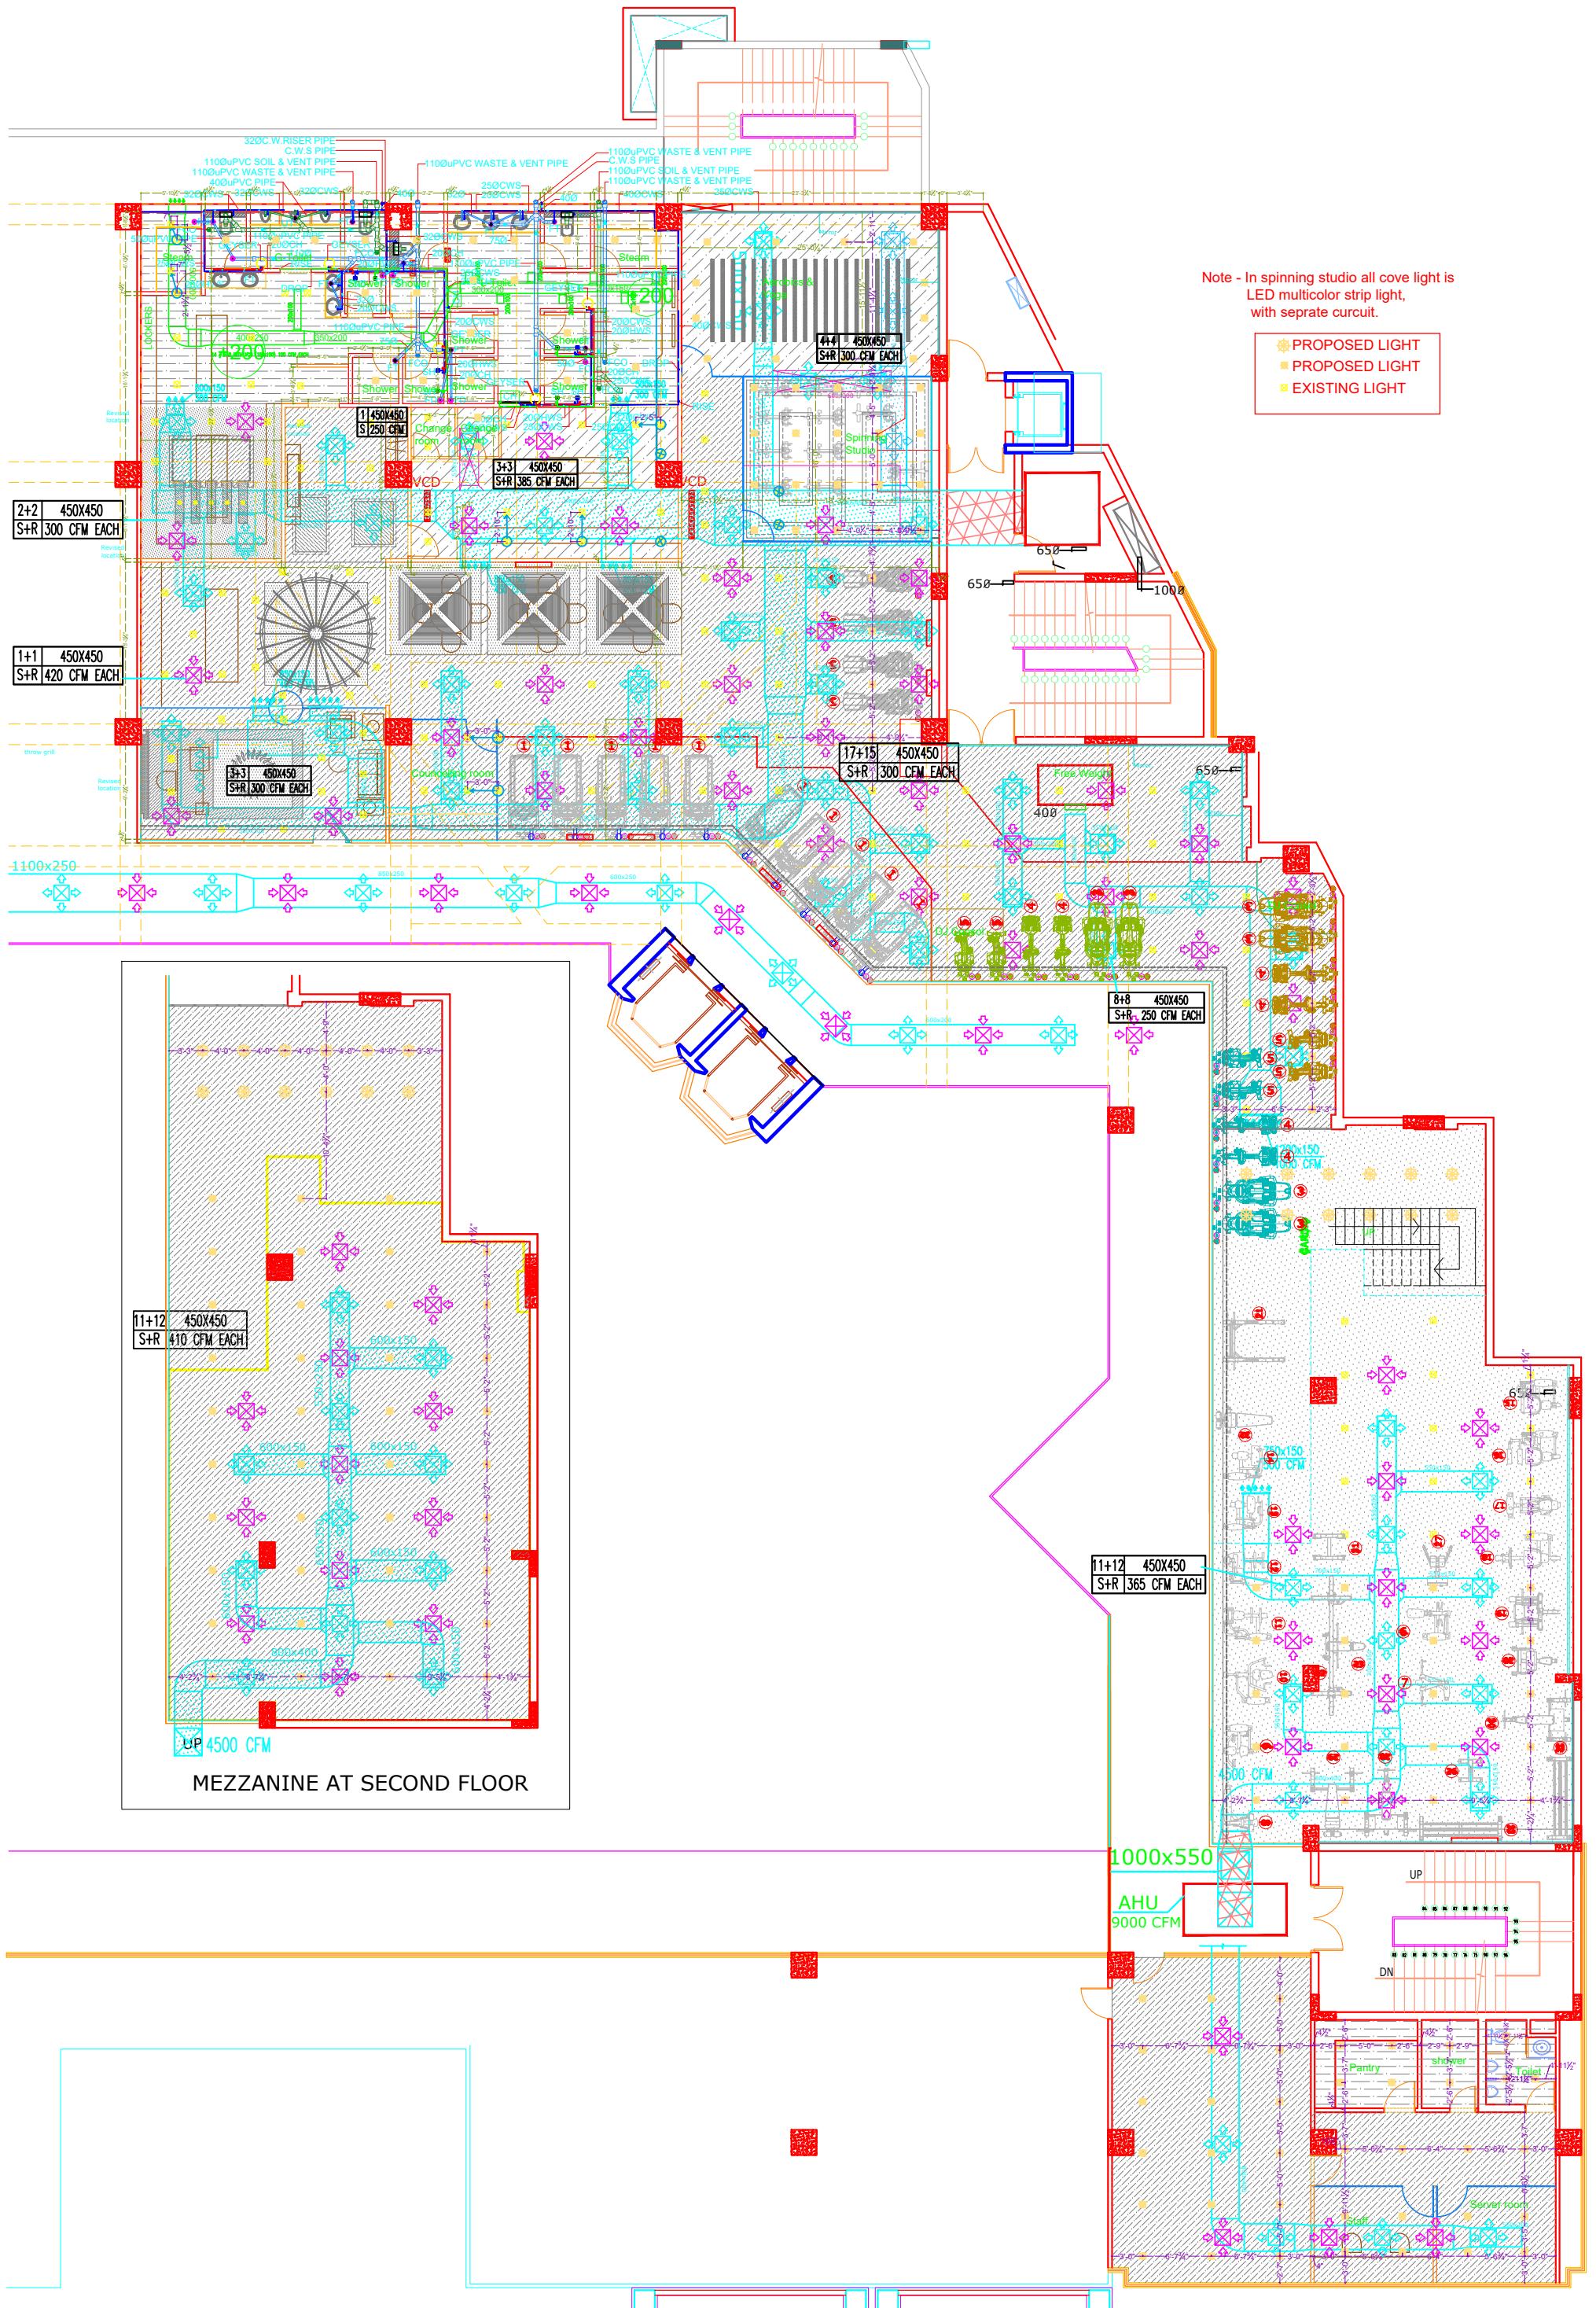


Note- All lintel at 7'-6"

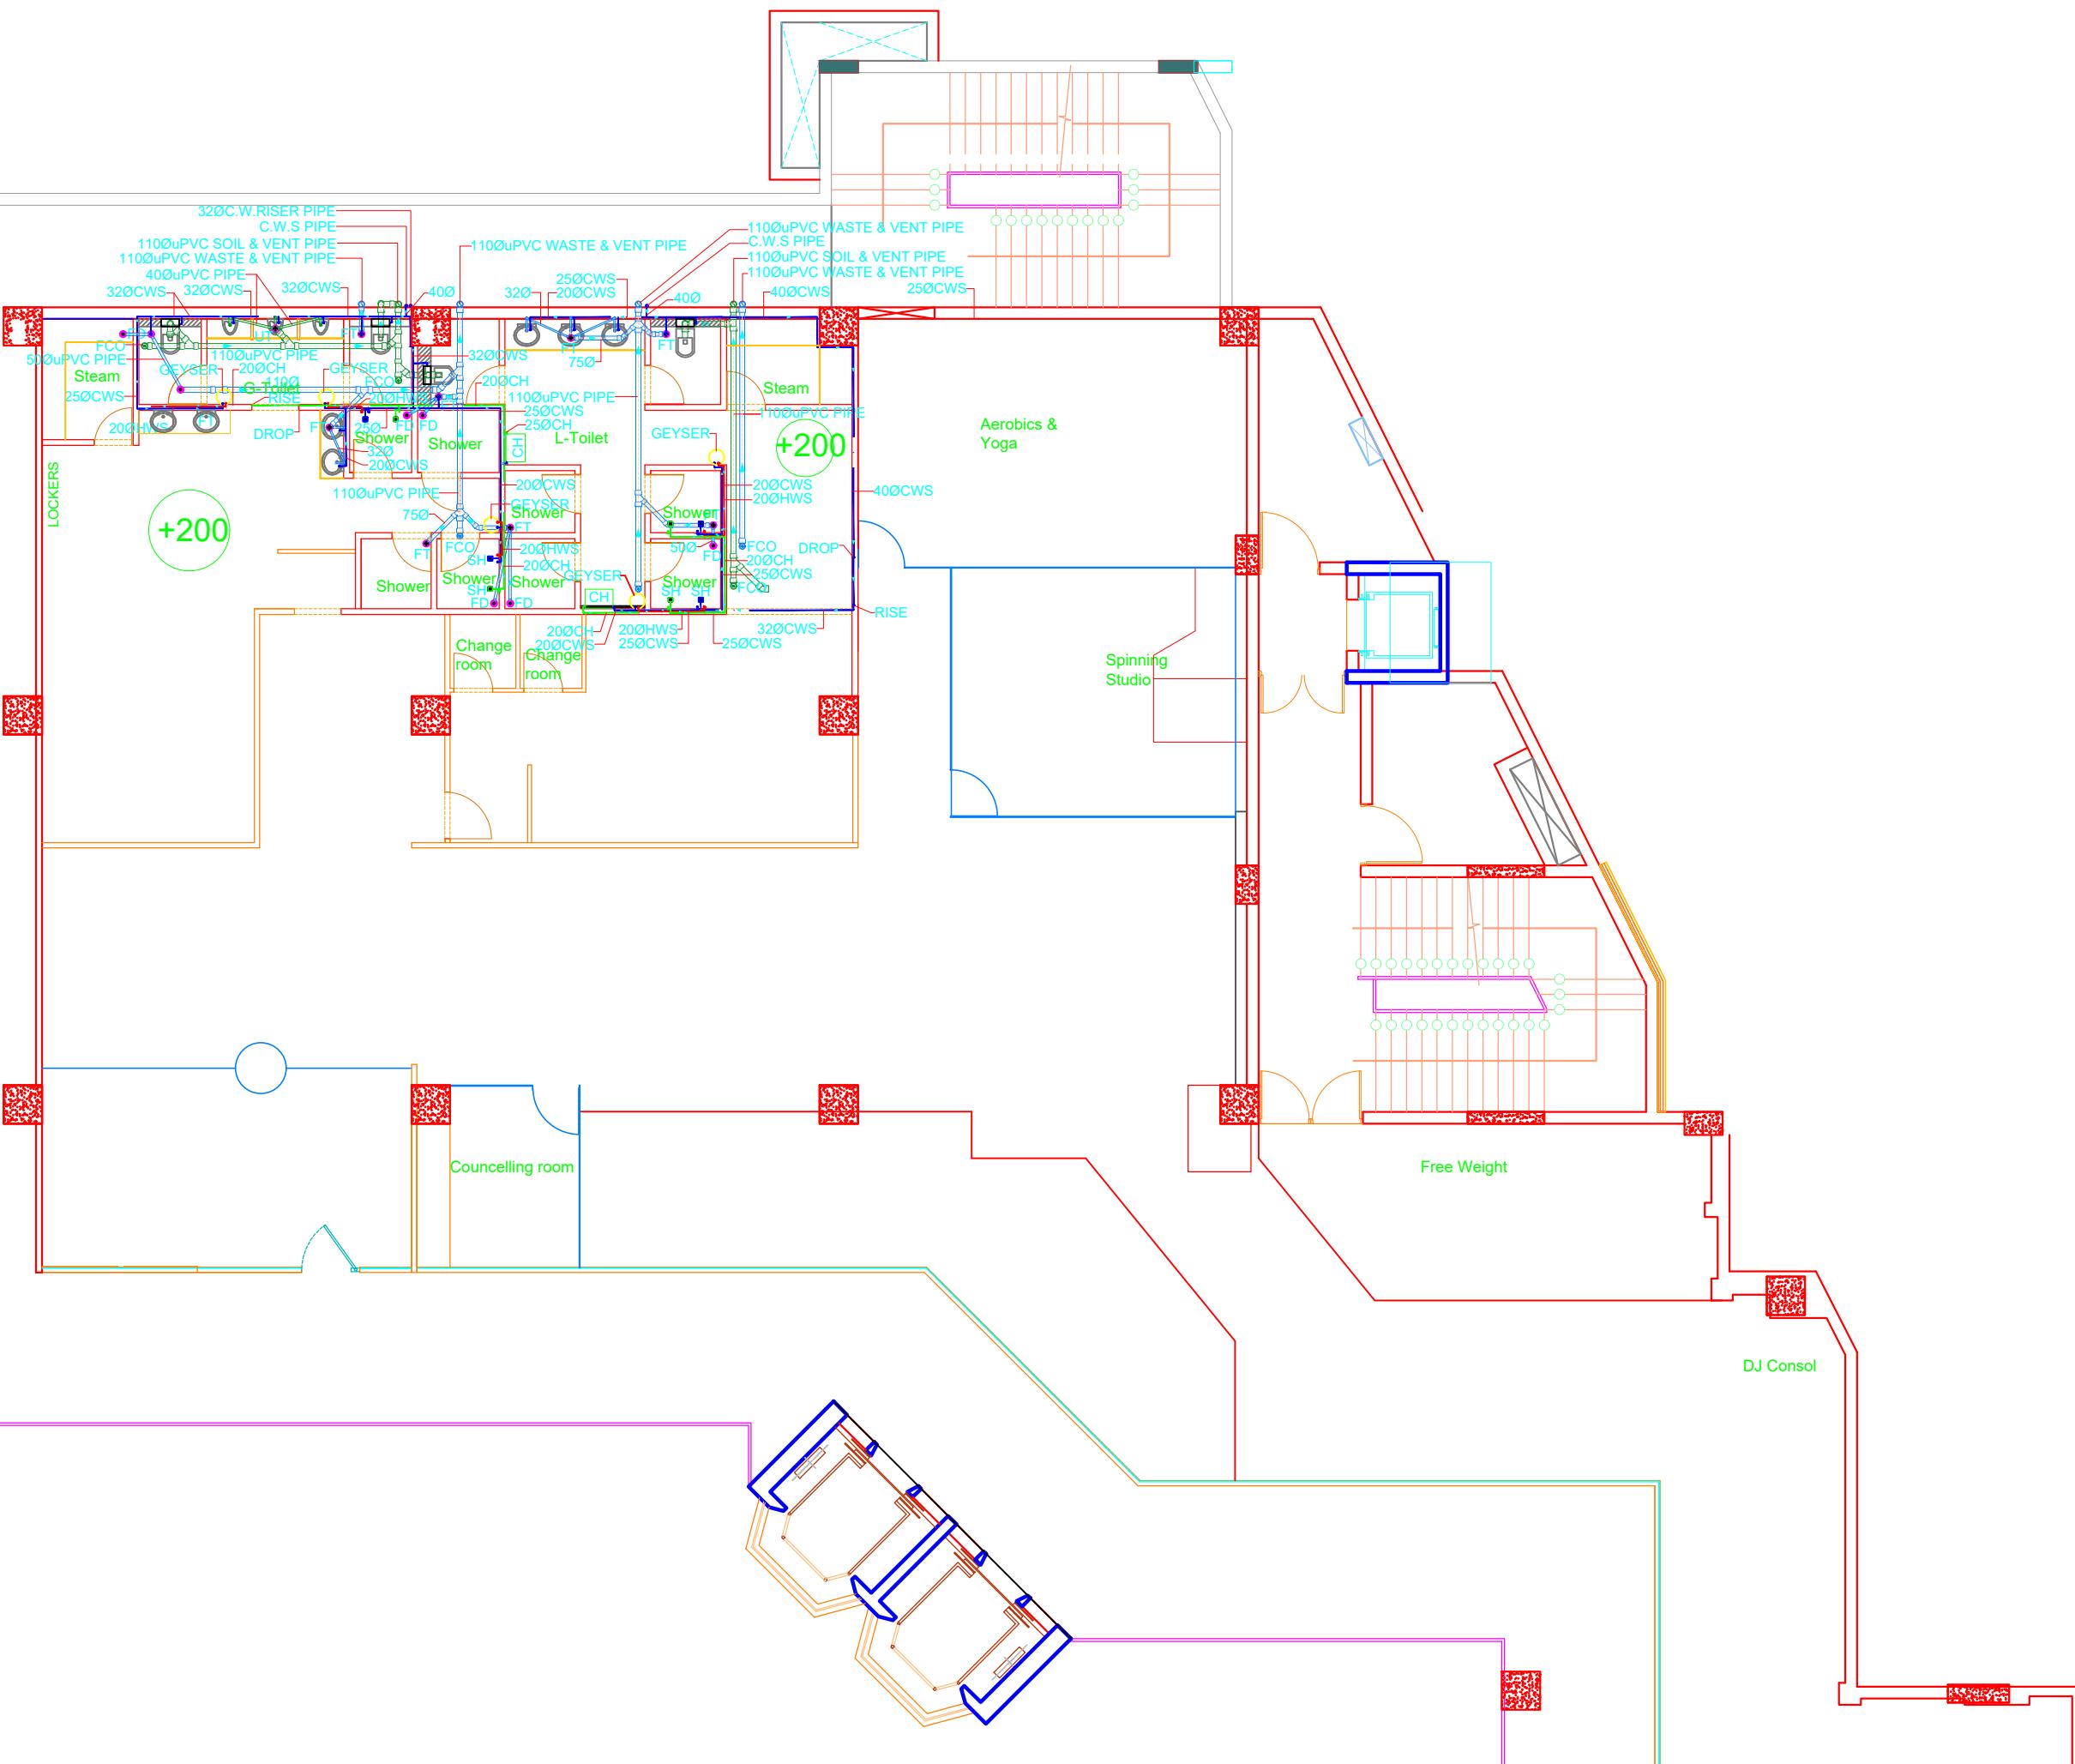



THE COTTAGE' AT TDI MALL

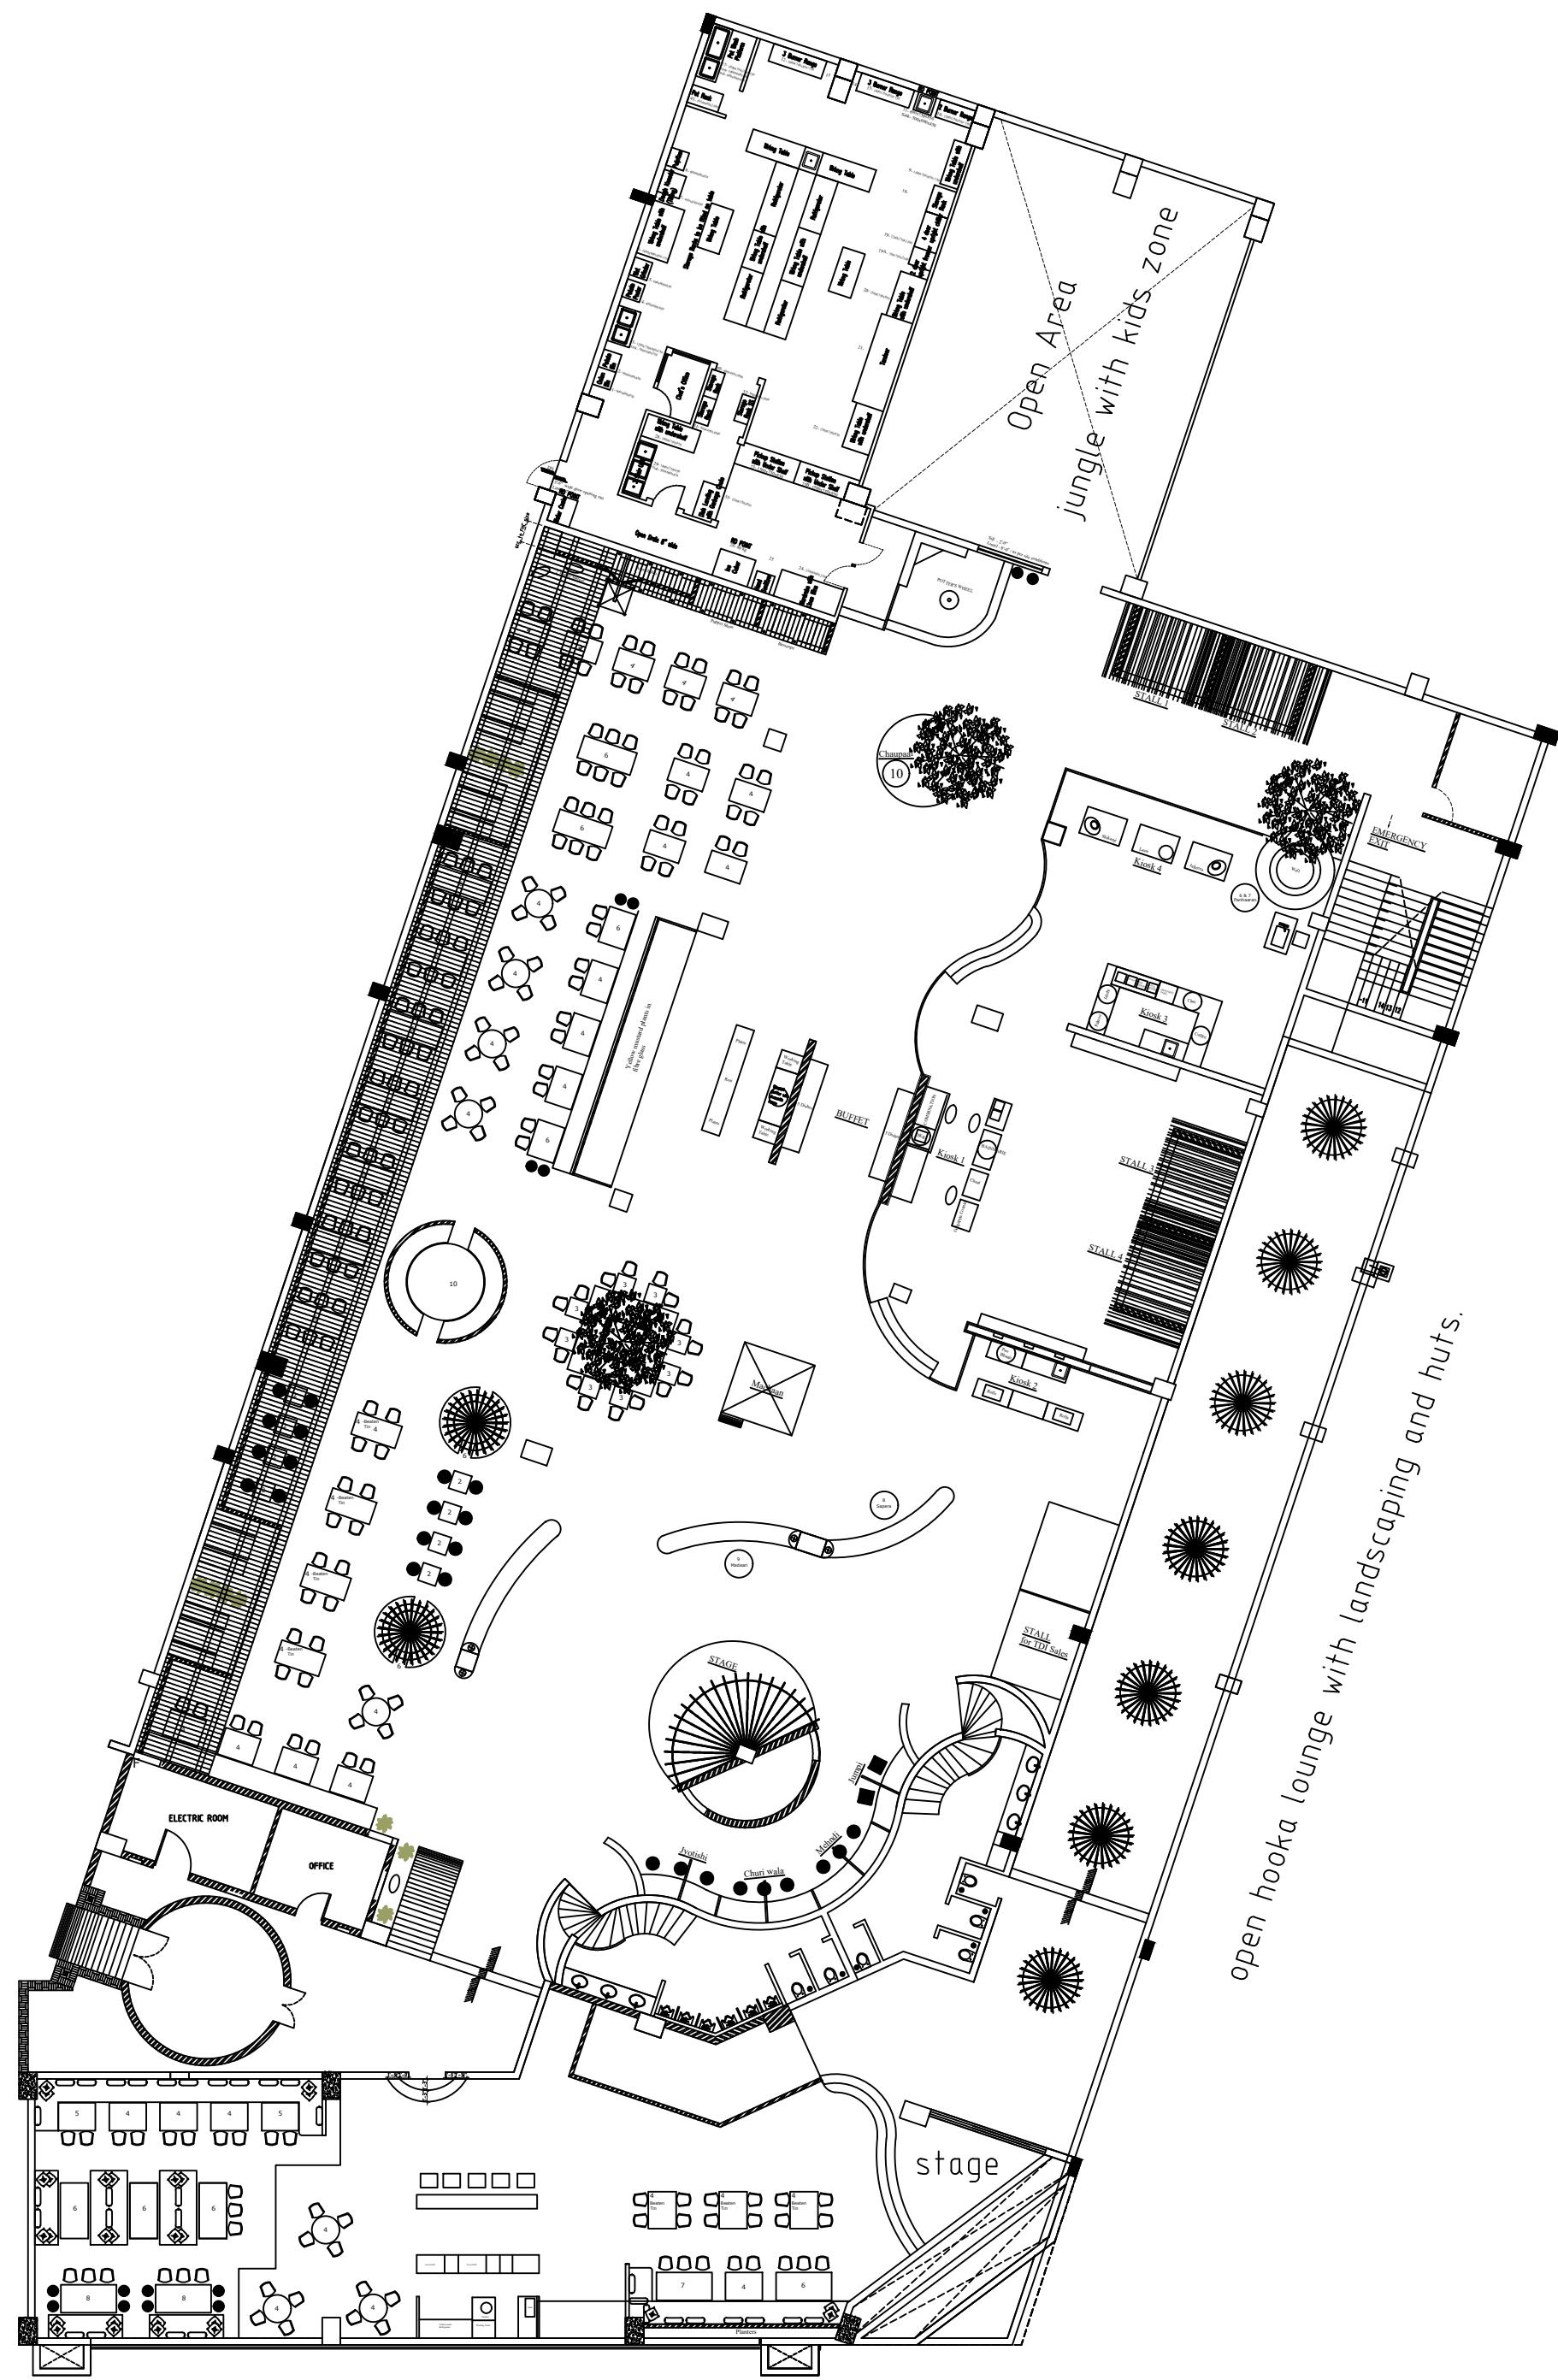

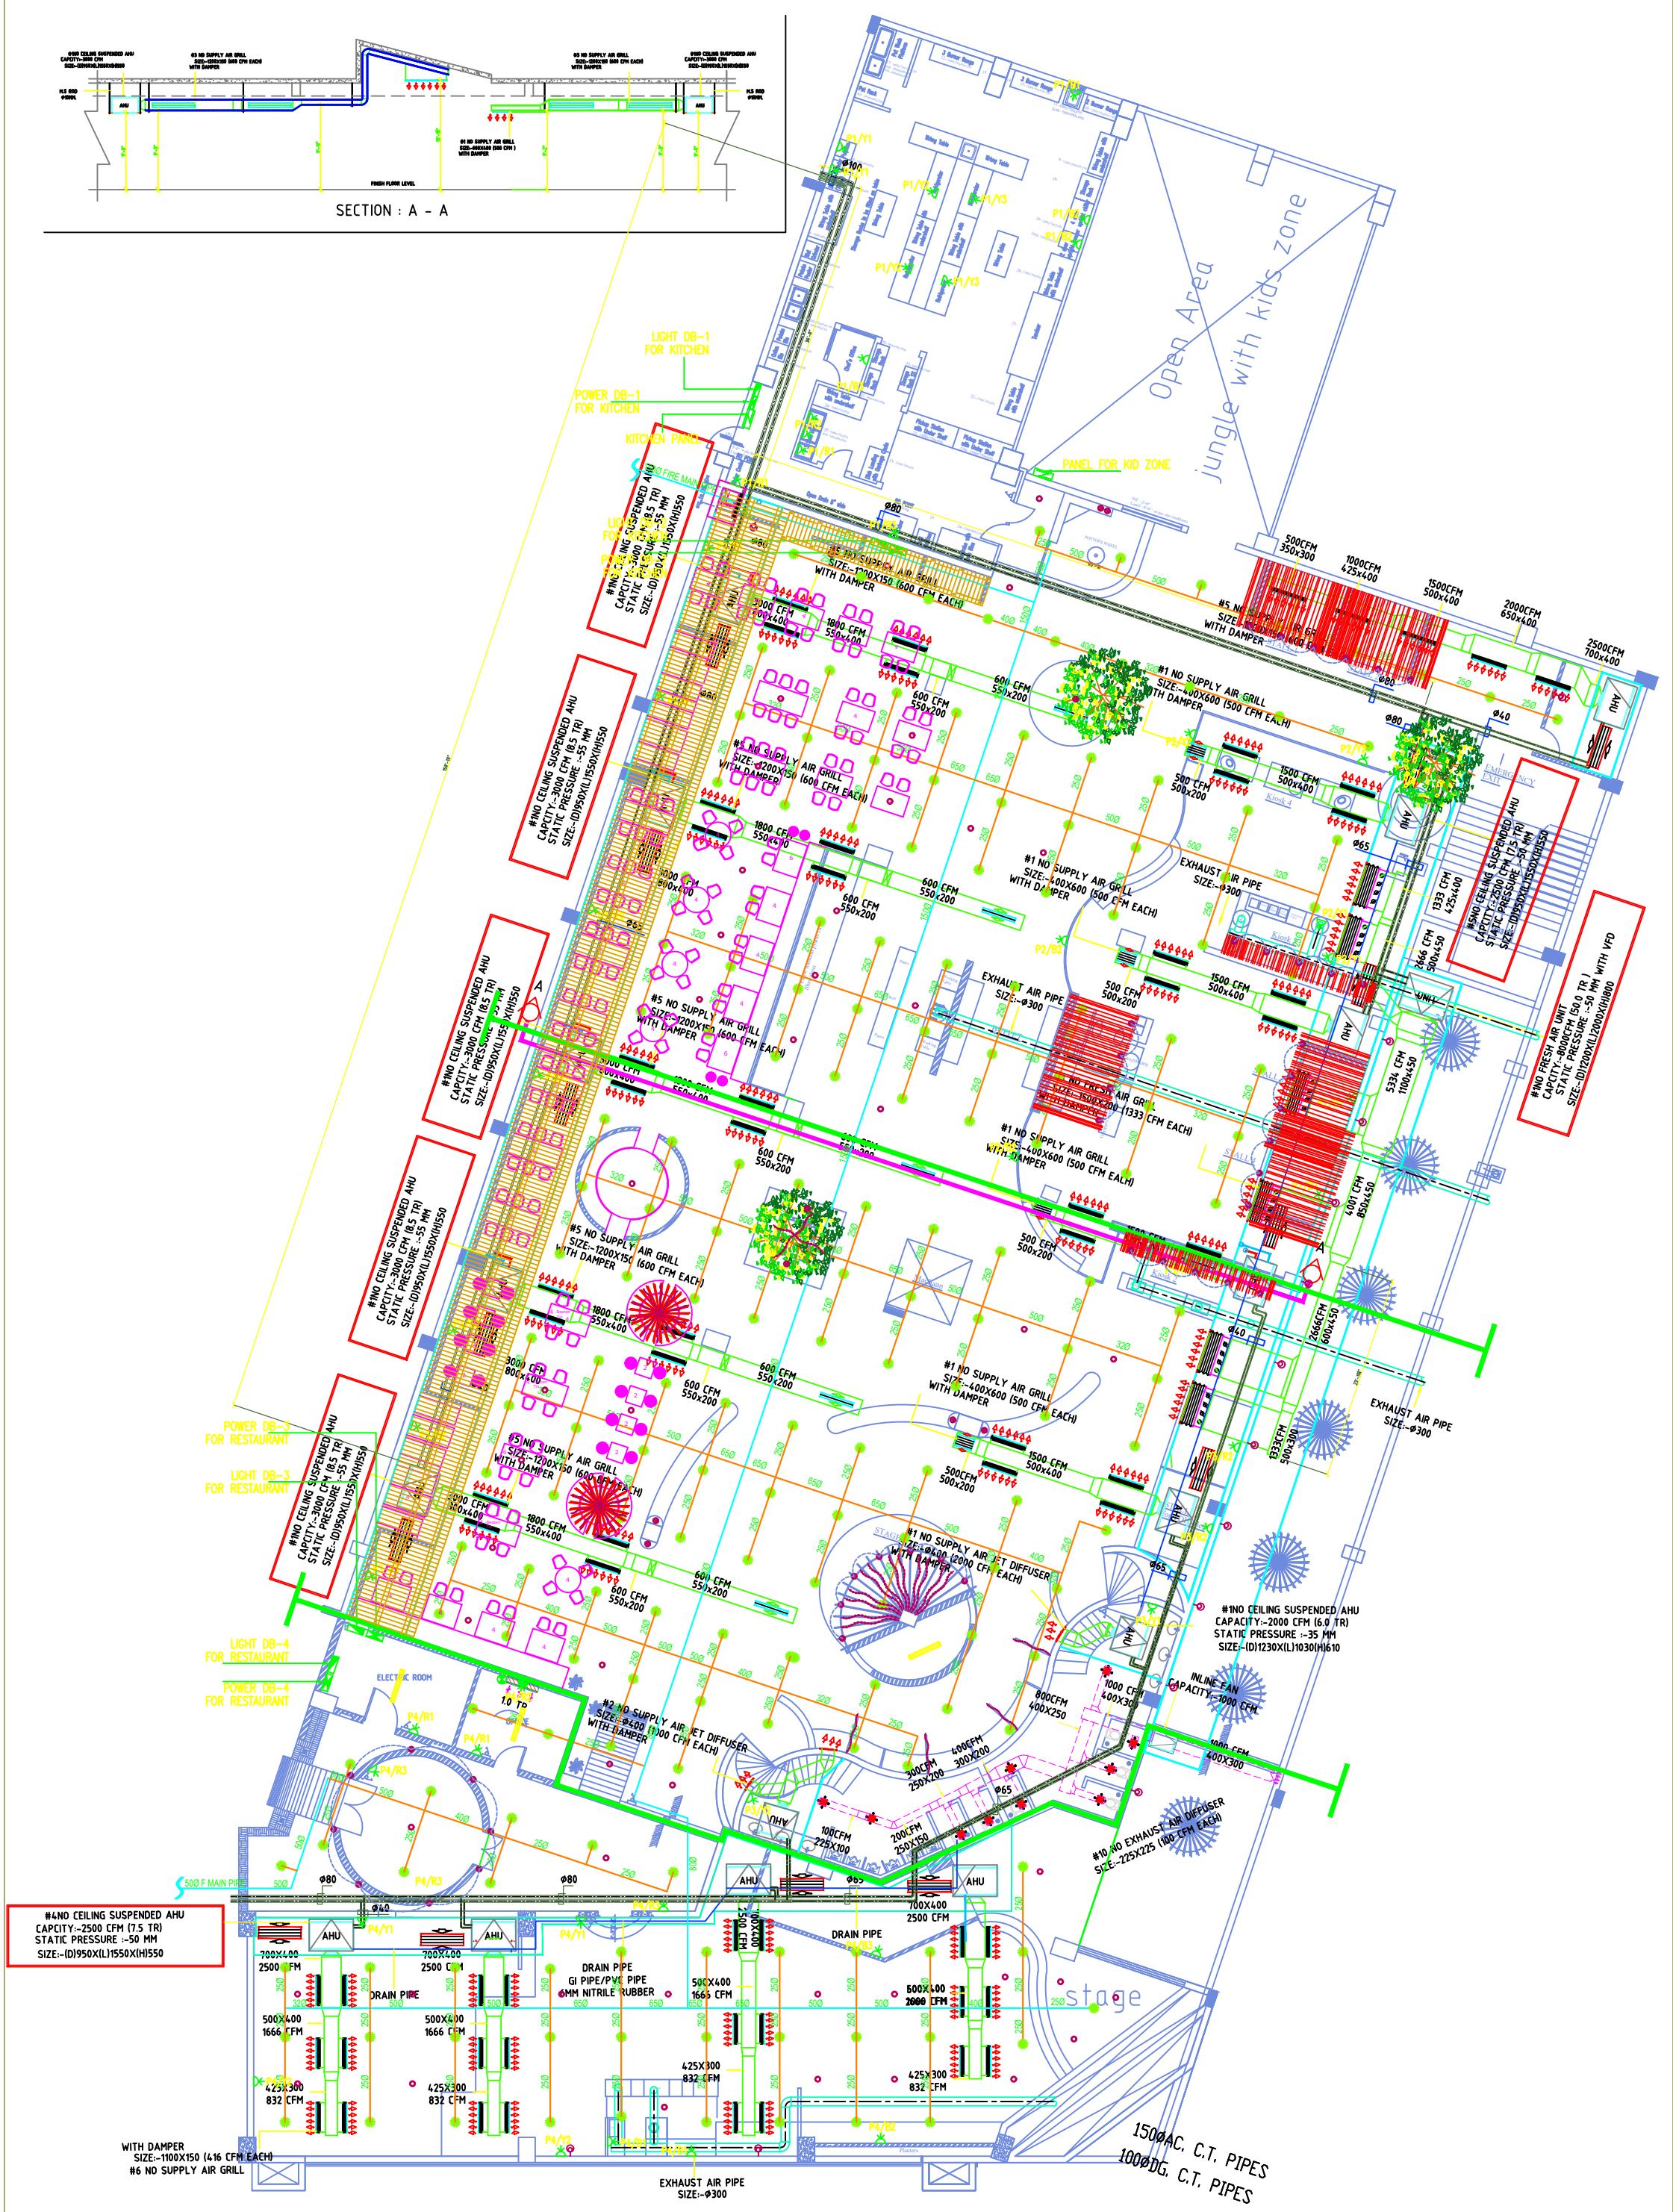


NOTE:-
1. OUTSIDE RUNNING DUCT WITH INSULATION 25 MM THICK .
2. INSIDE RUNNING DUCT WITH INSULATION 12 MM THICK .

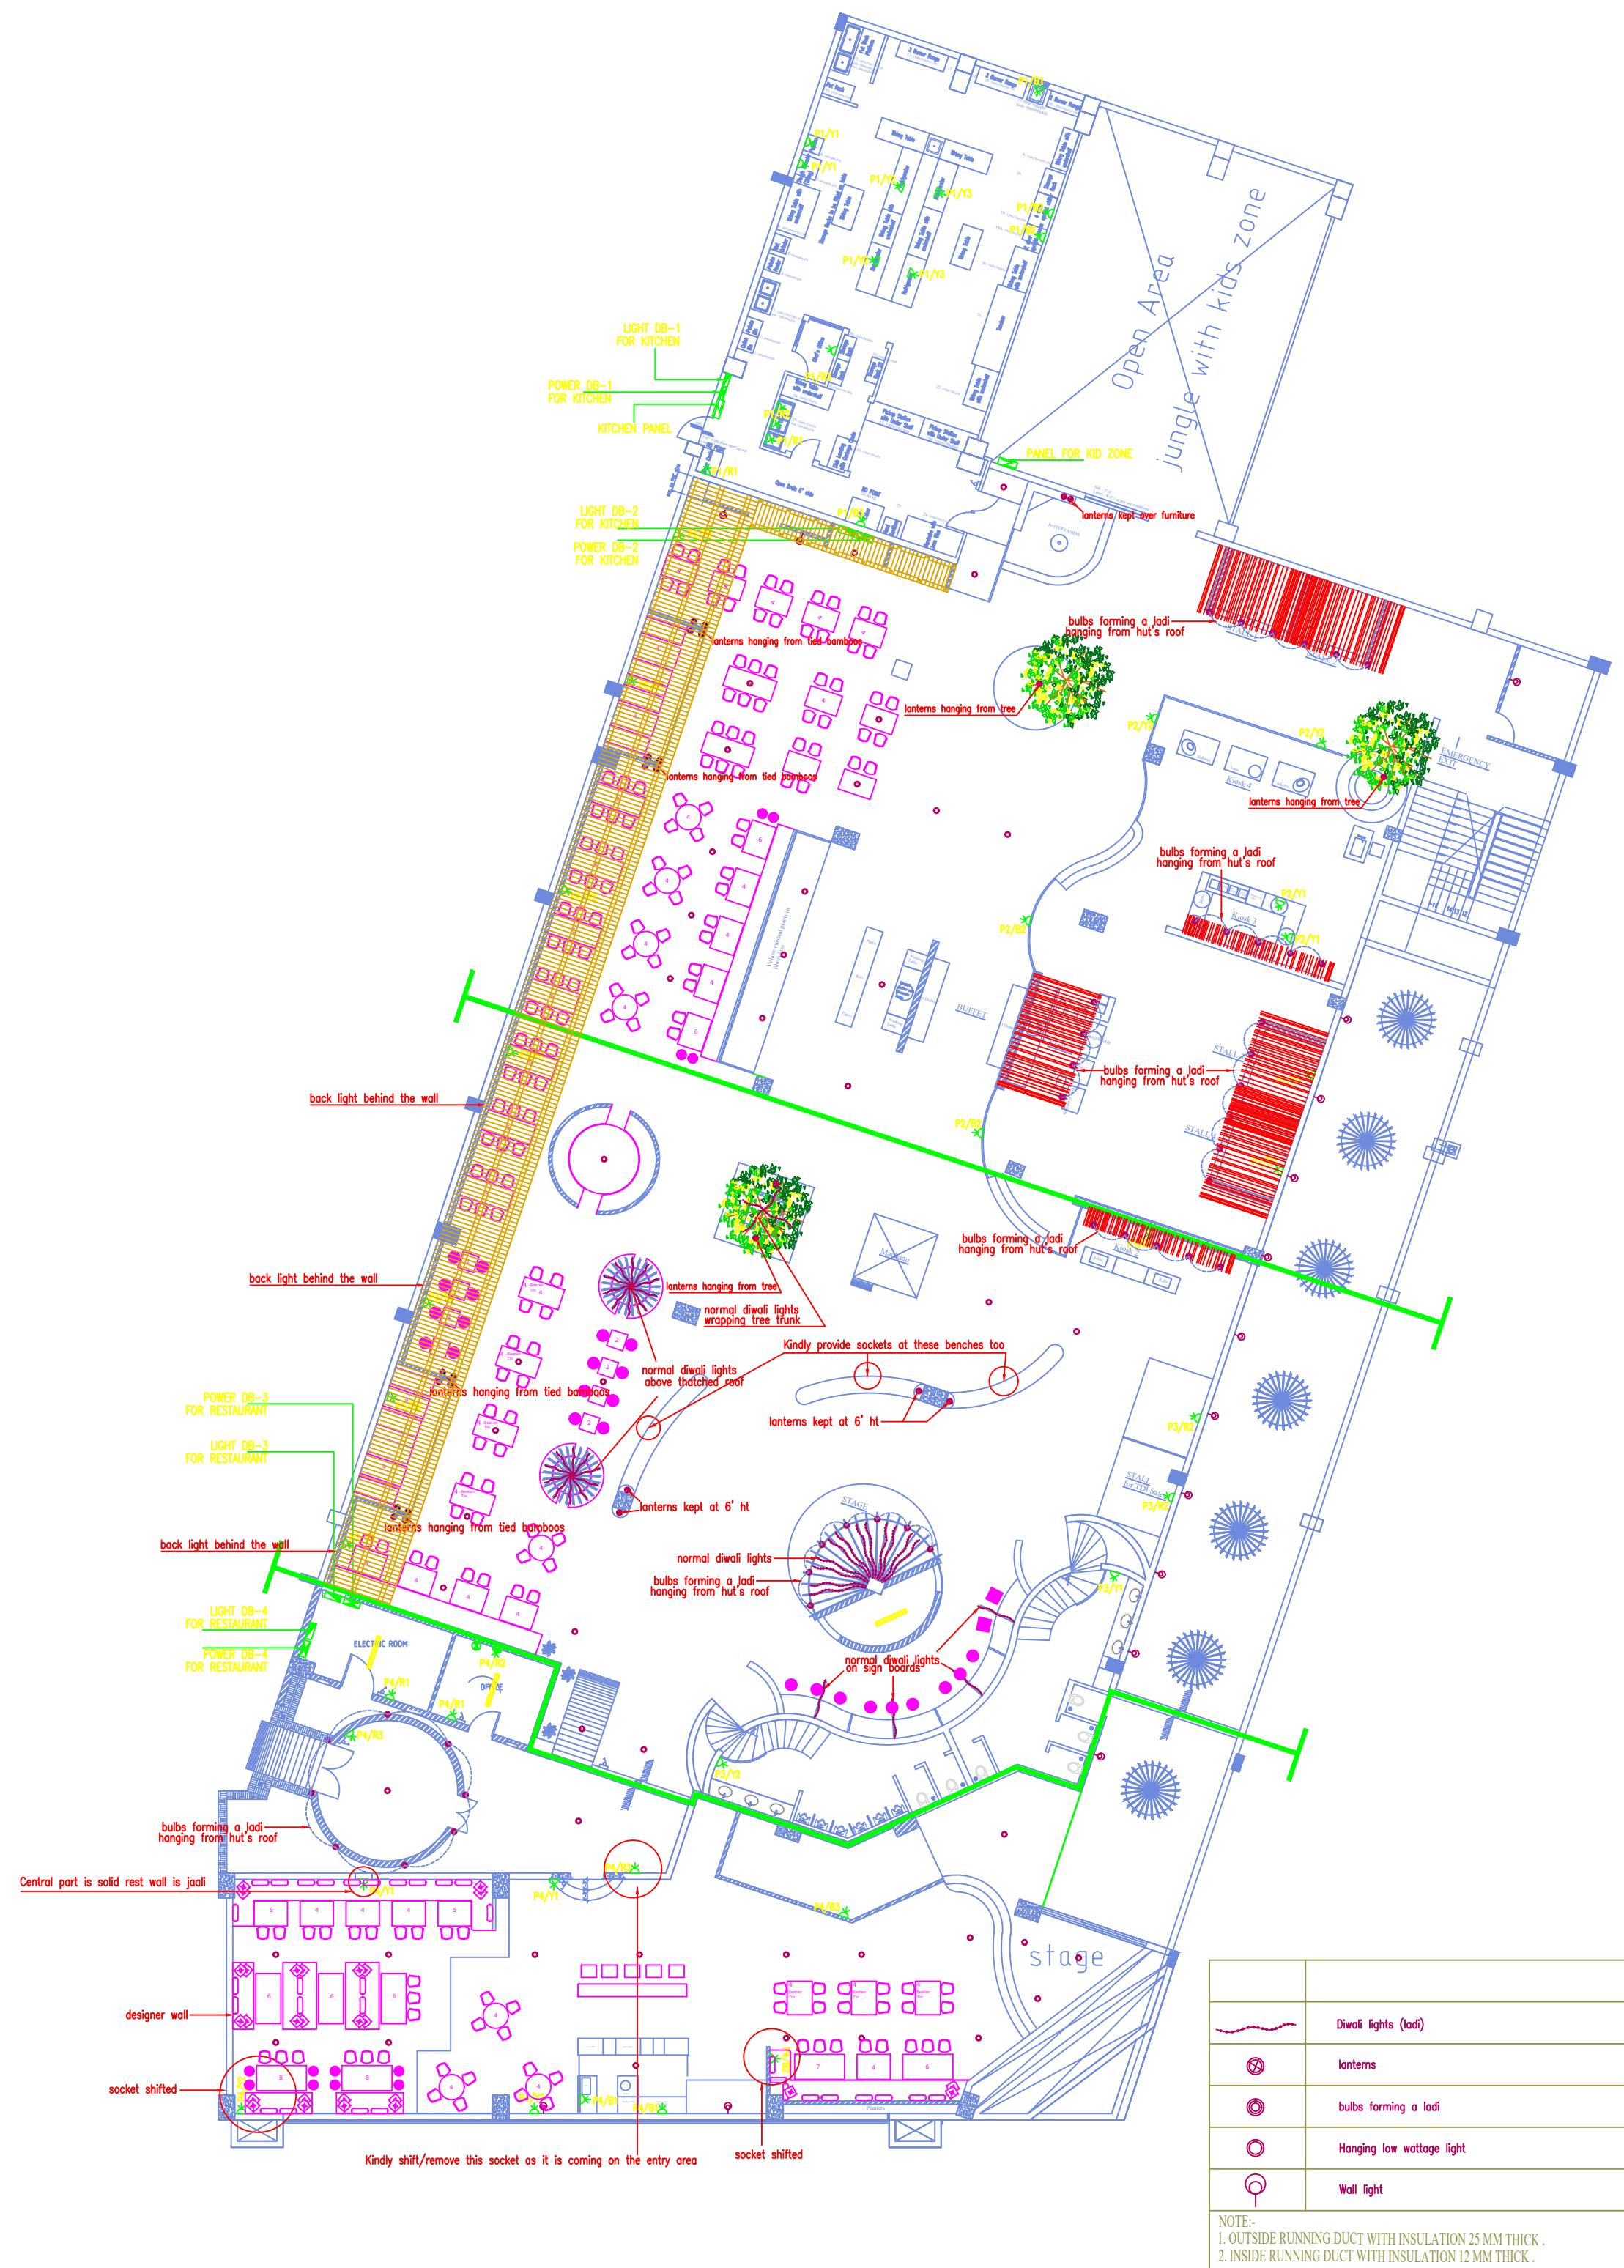

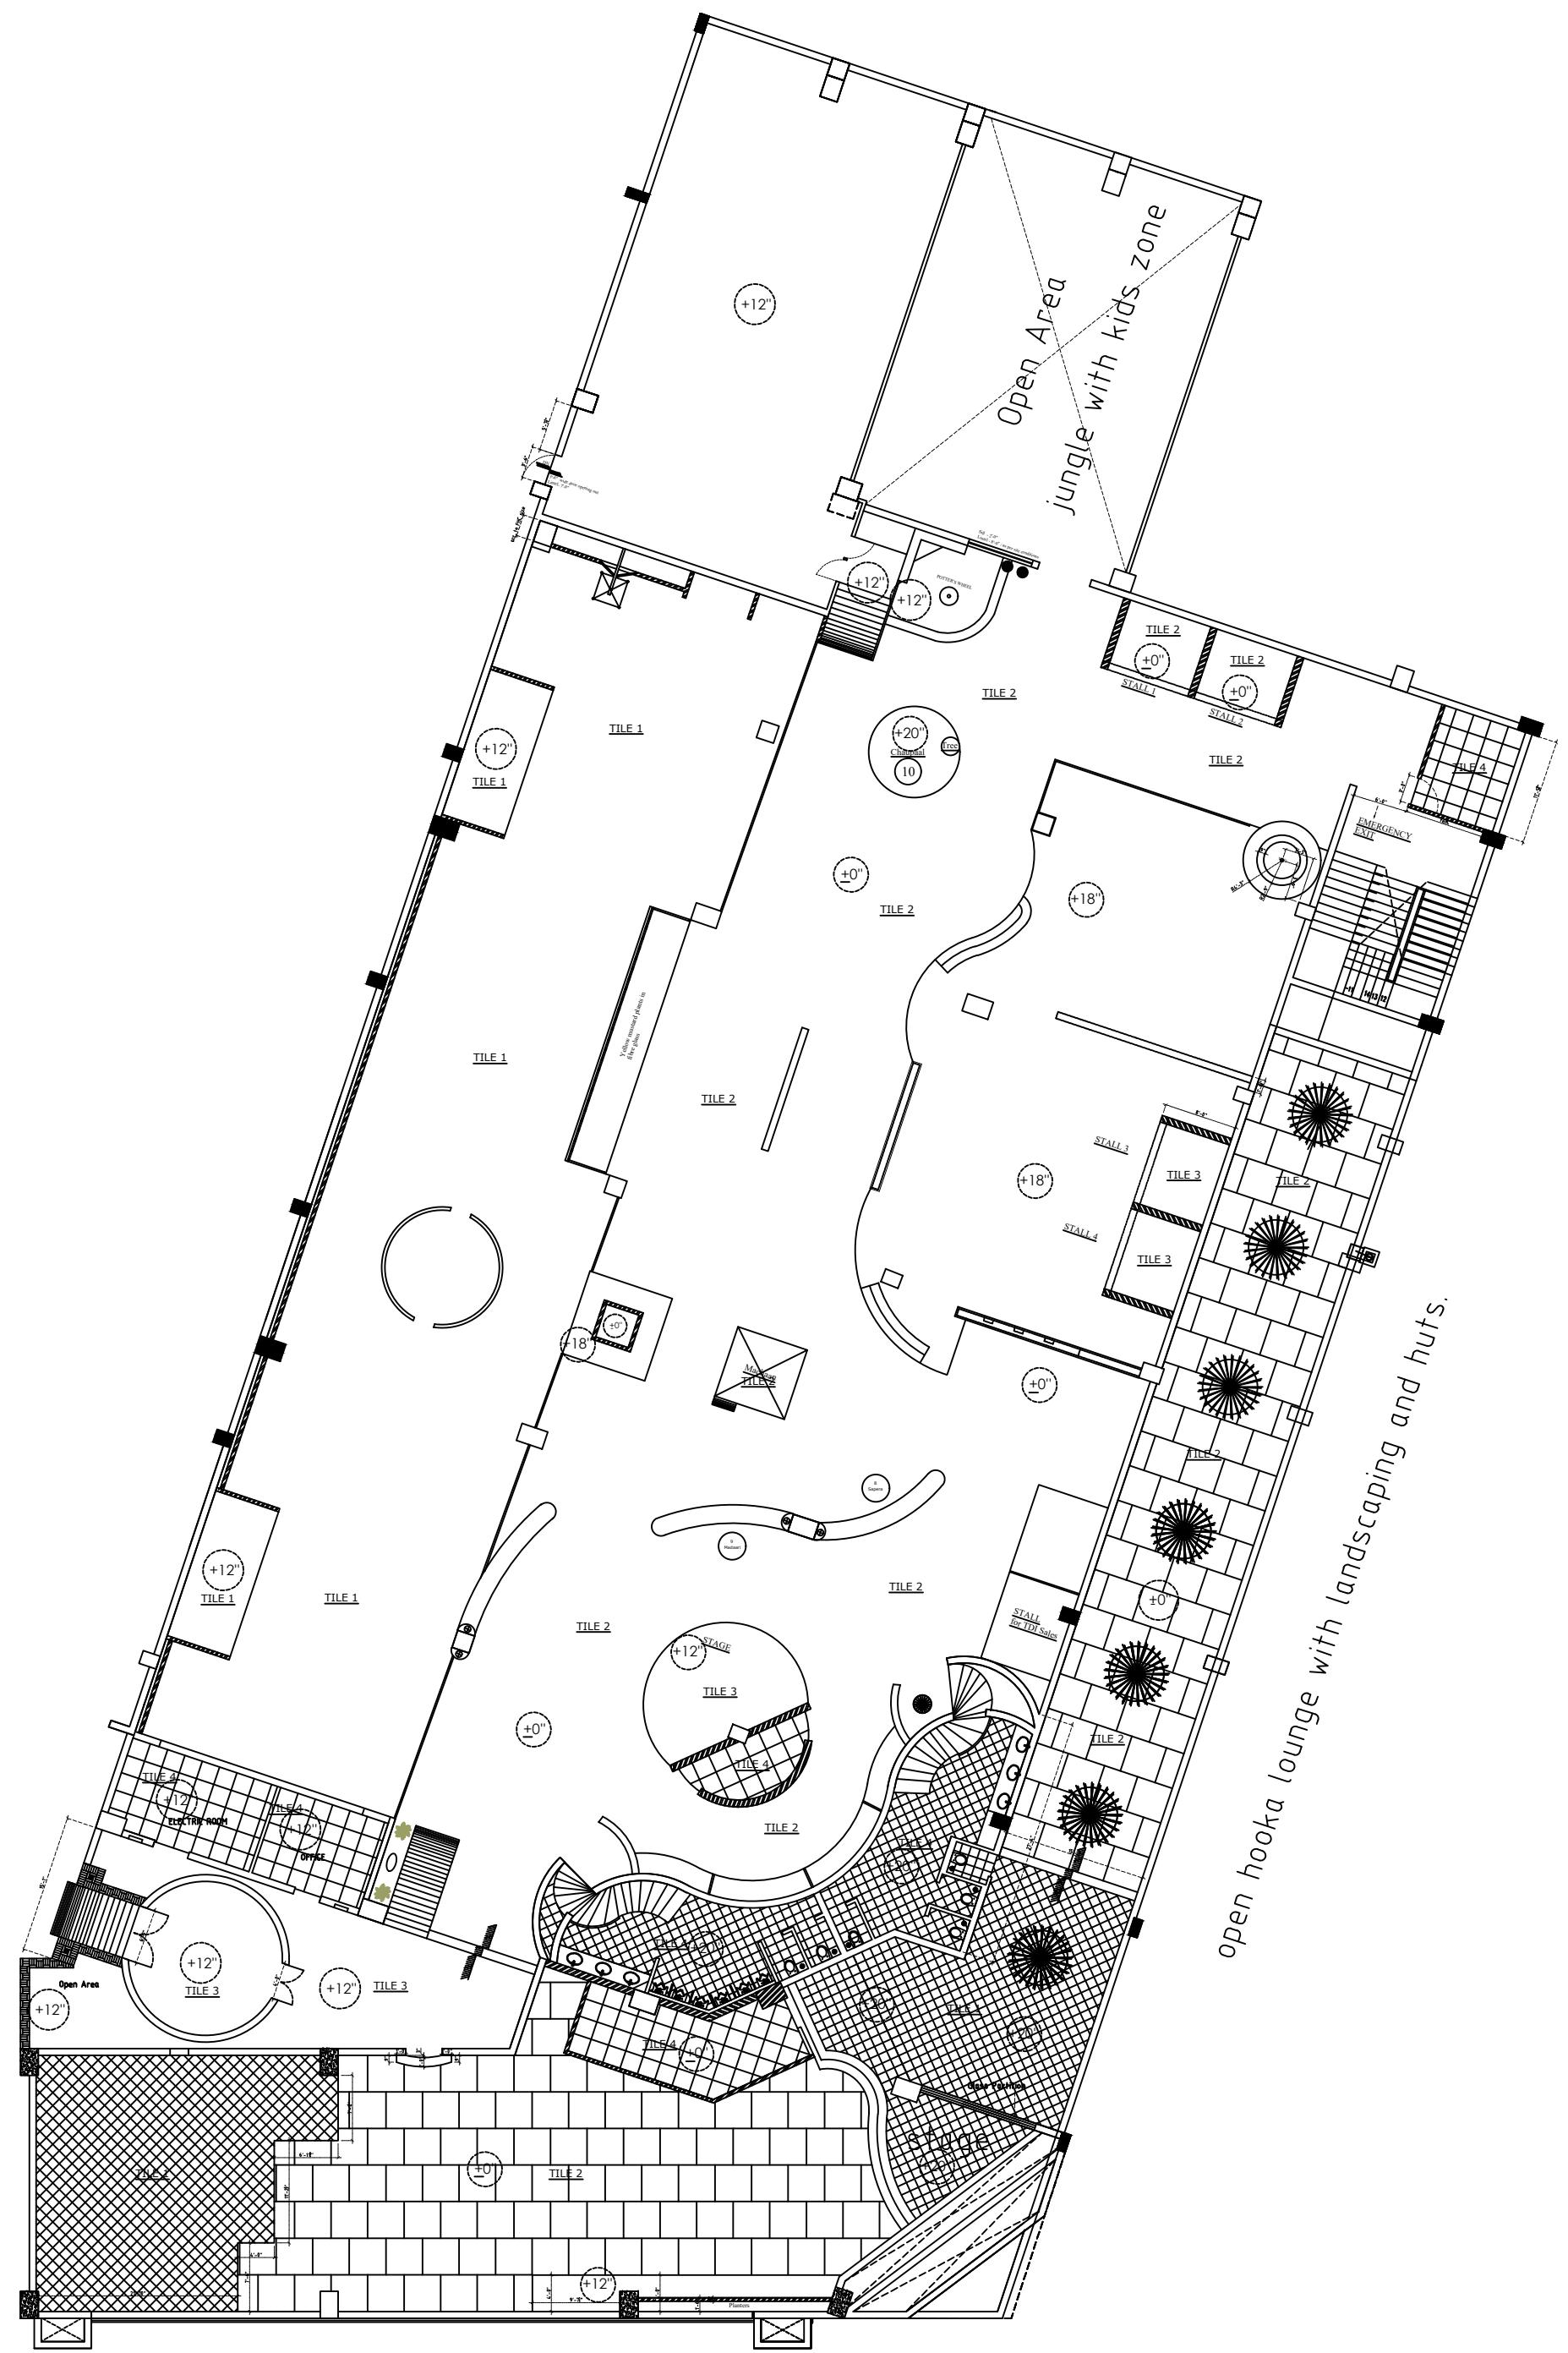


A


A

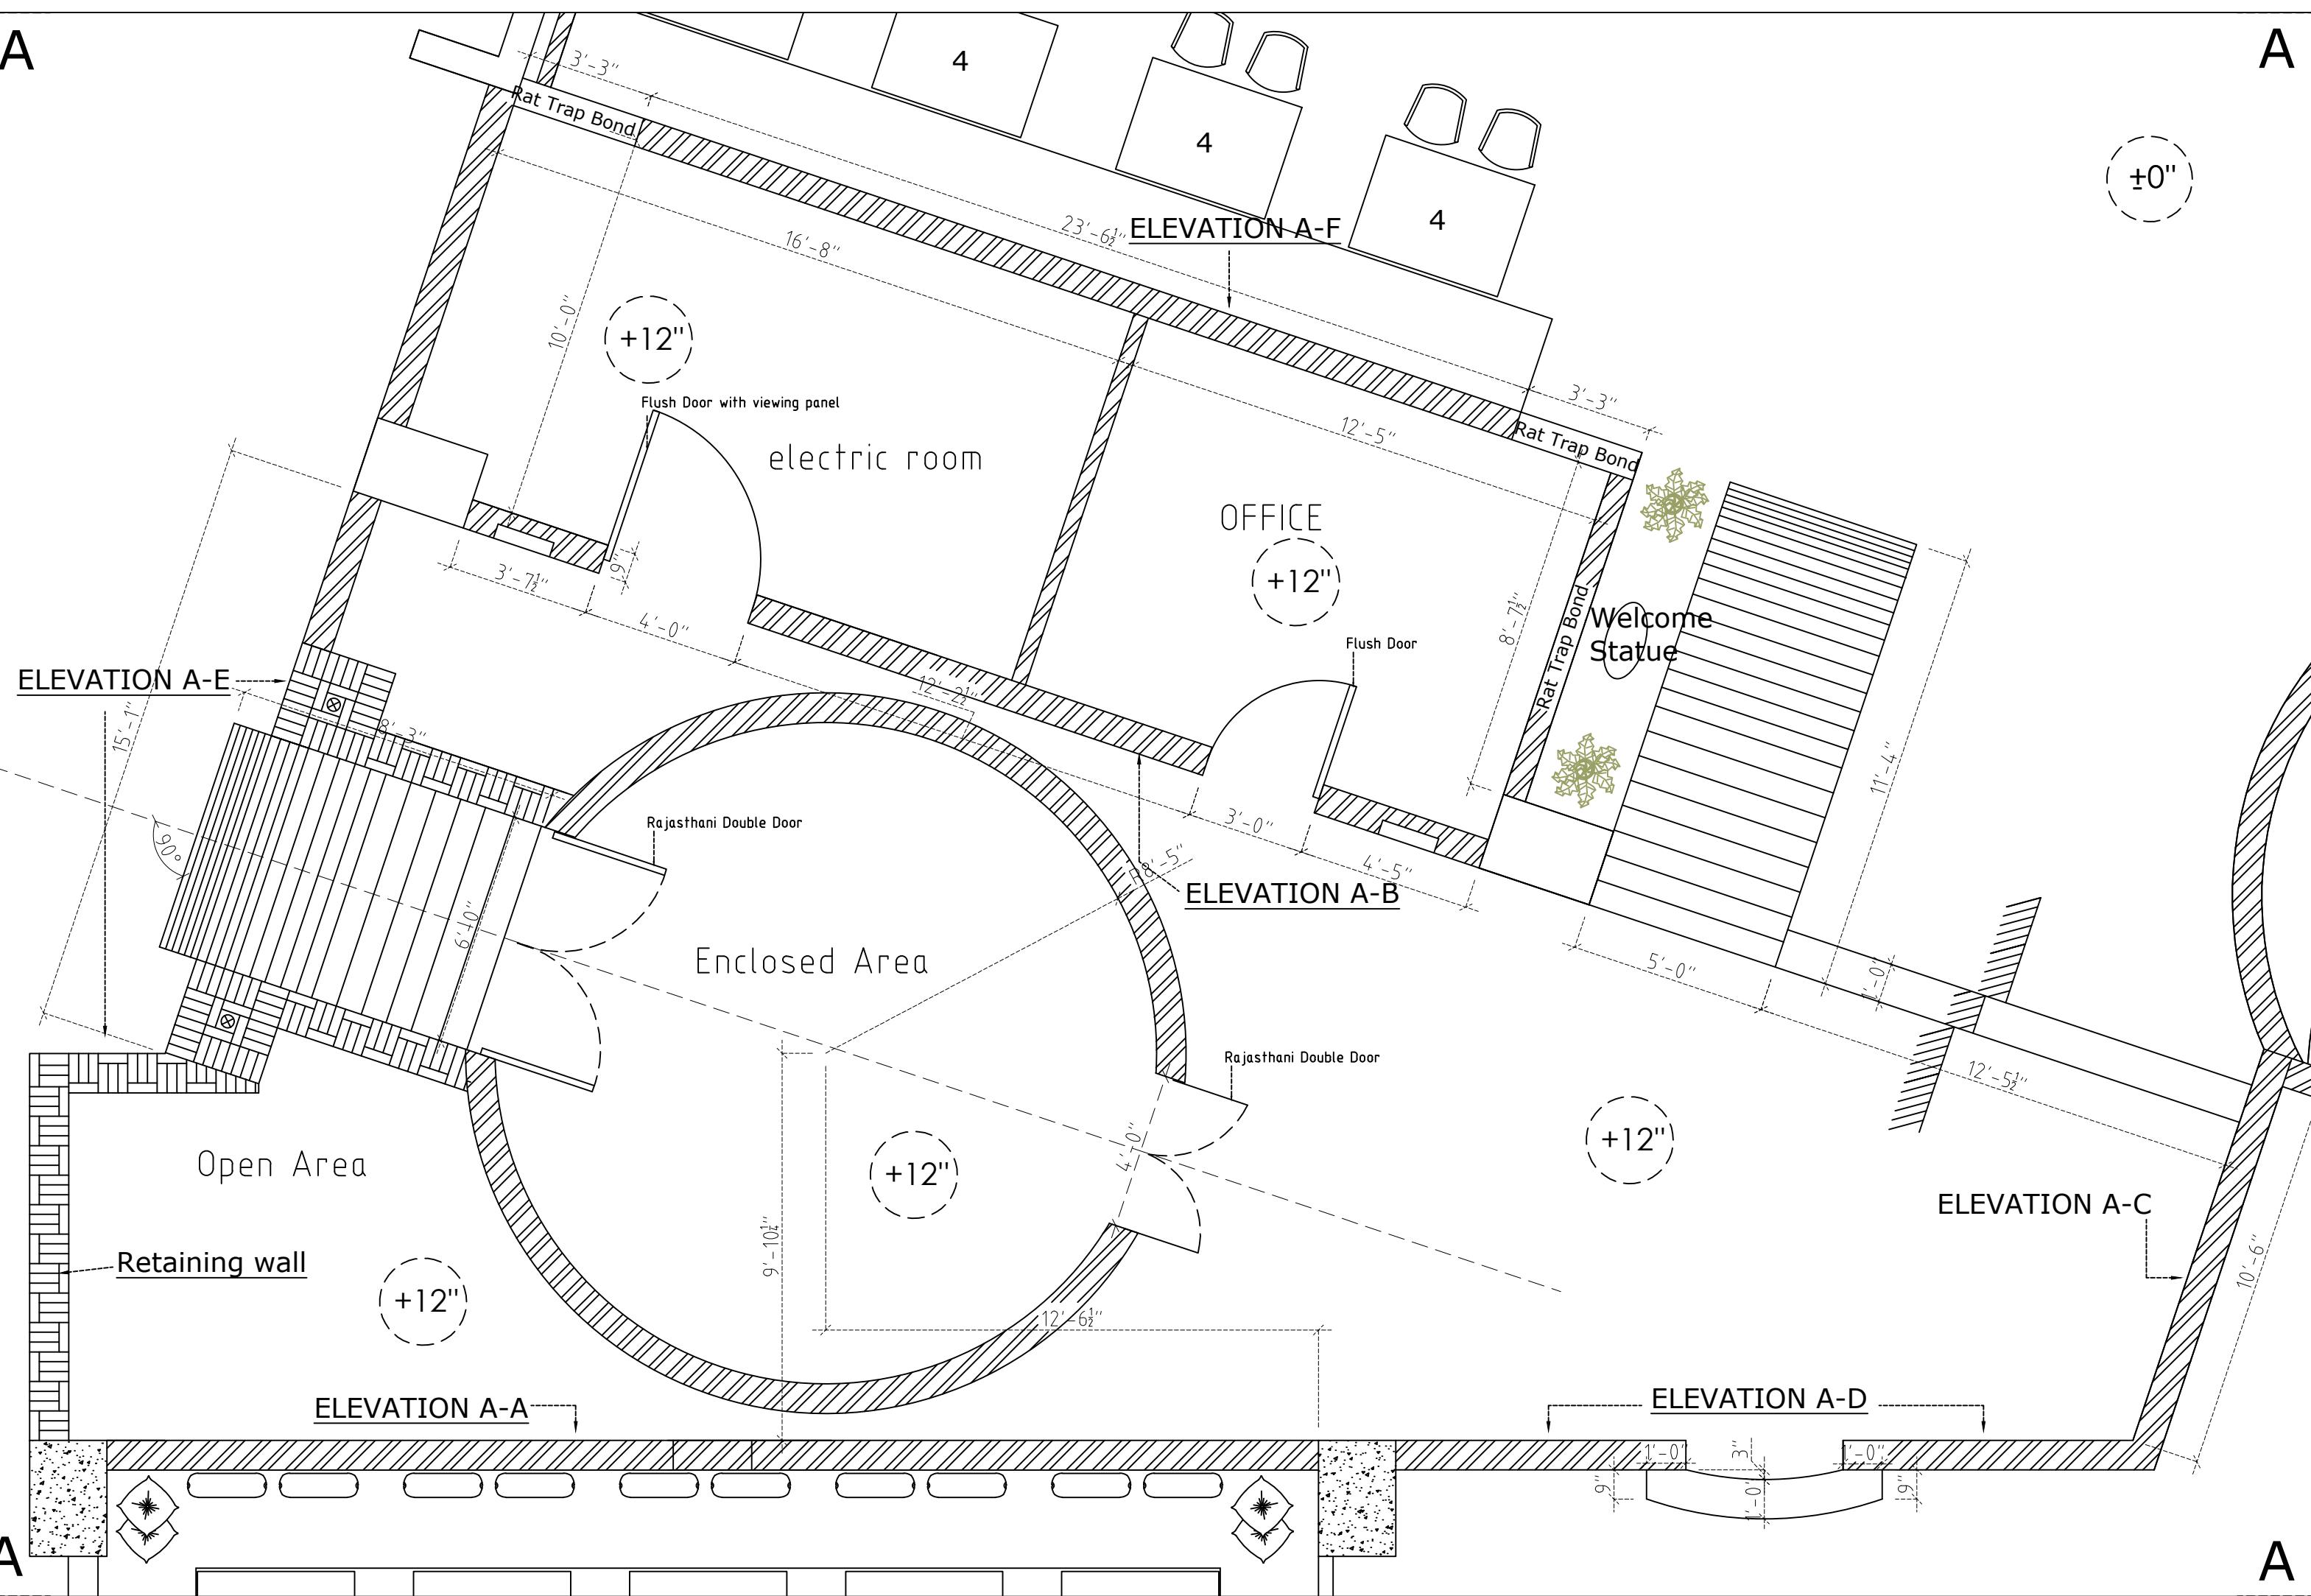

*Start Brickwork from here
by counting bricks*

*Start Brickwork from here
by counting bricks*

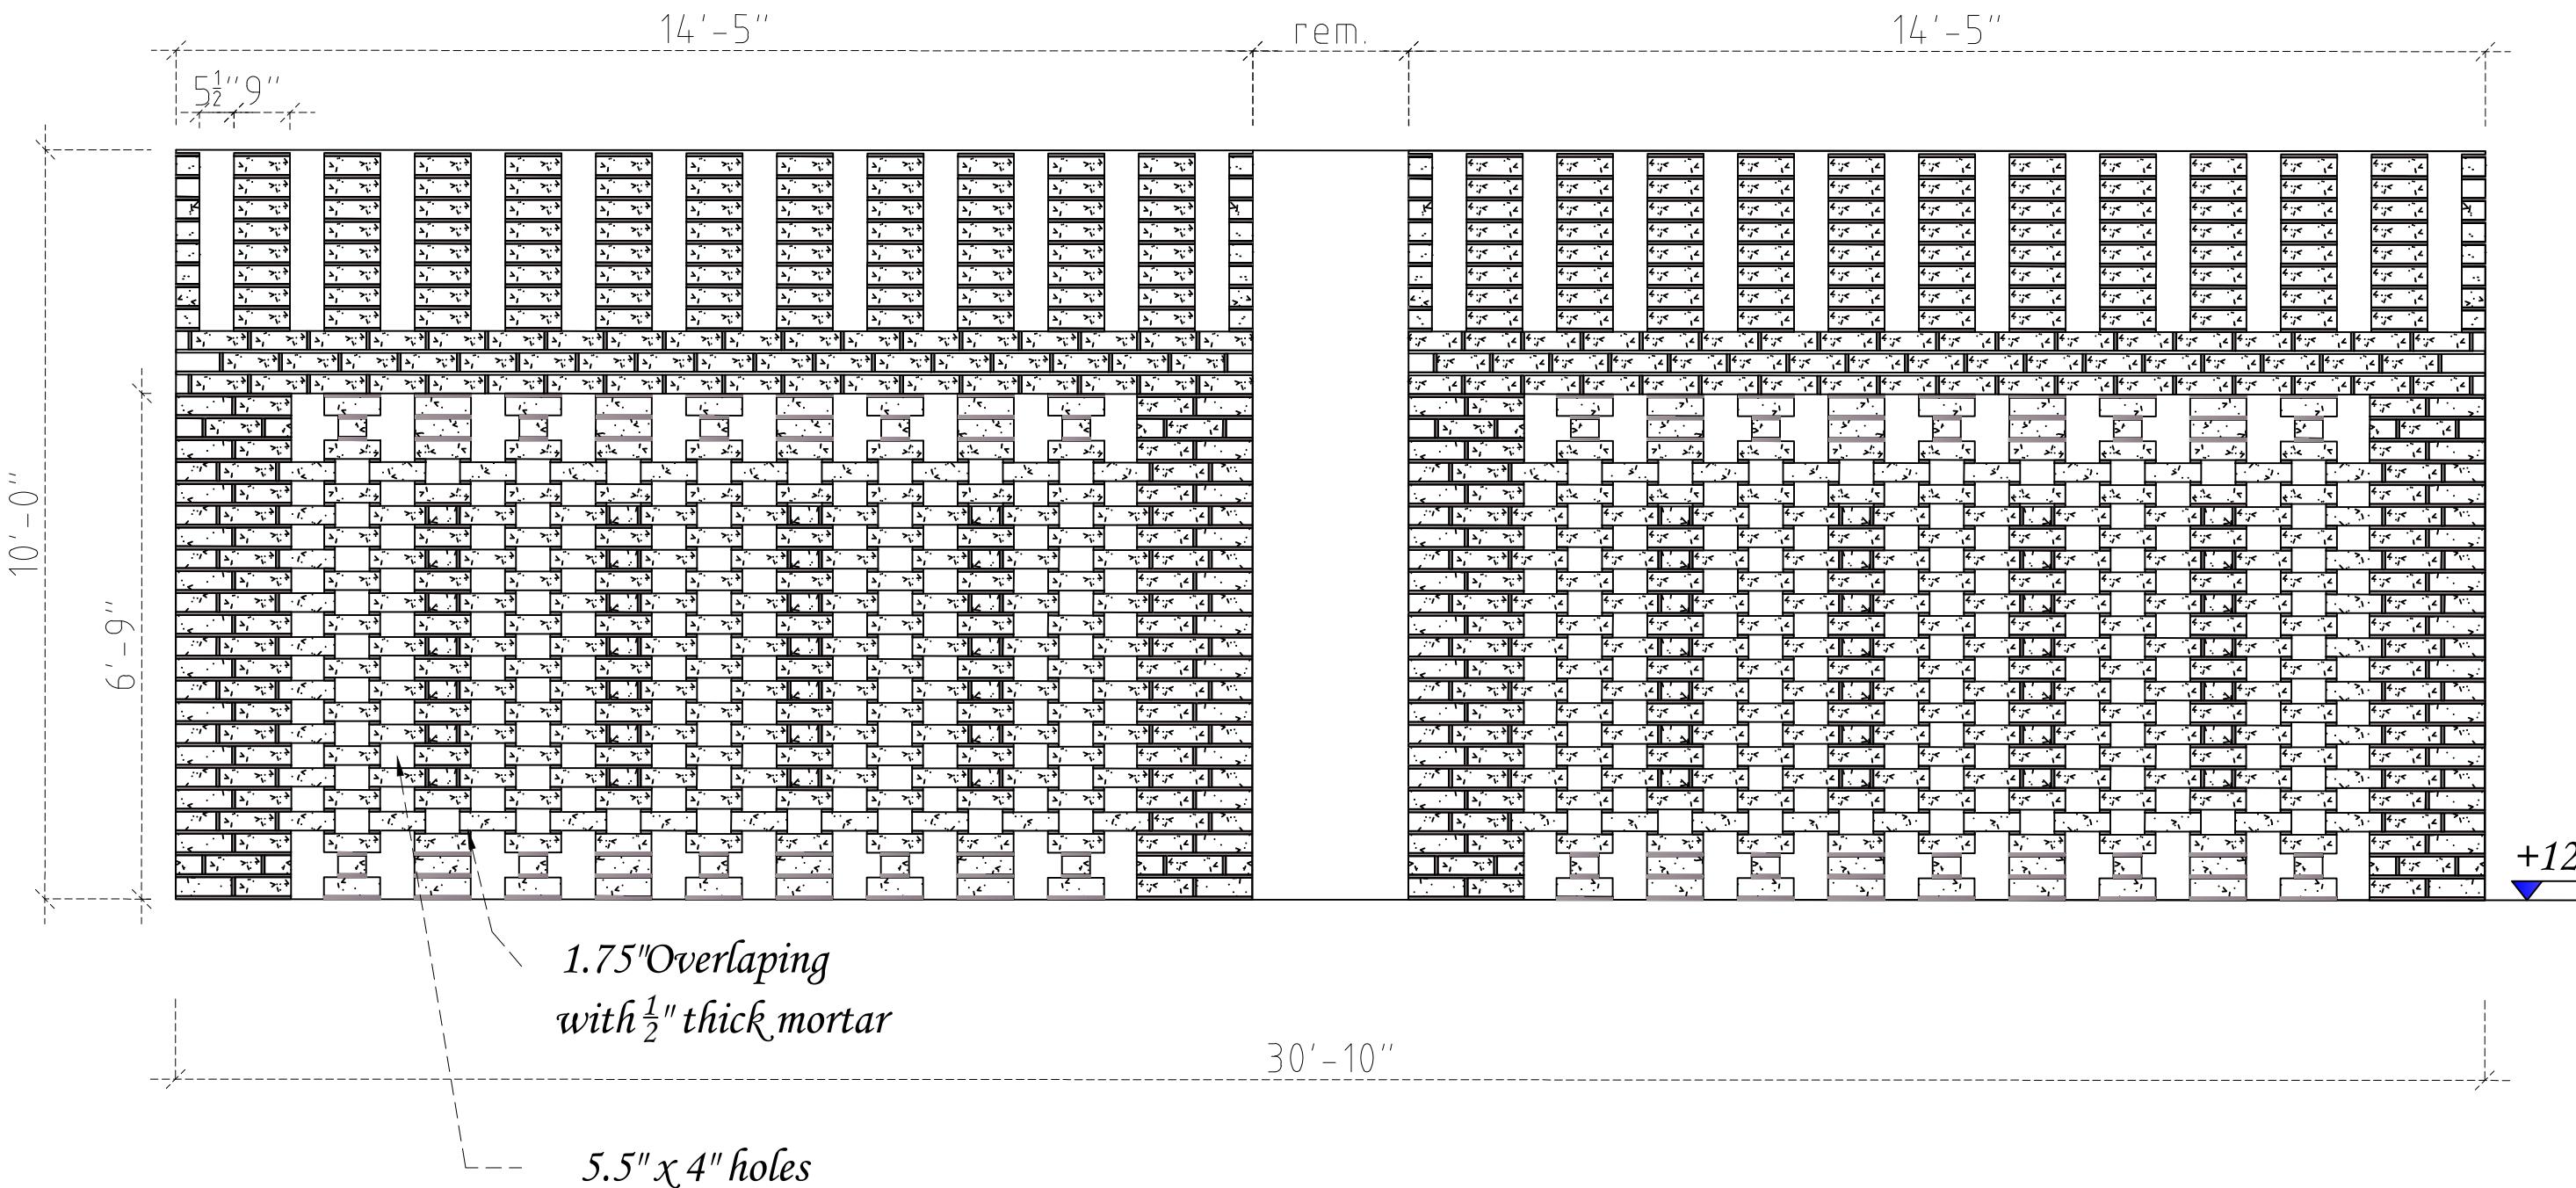


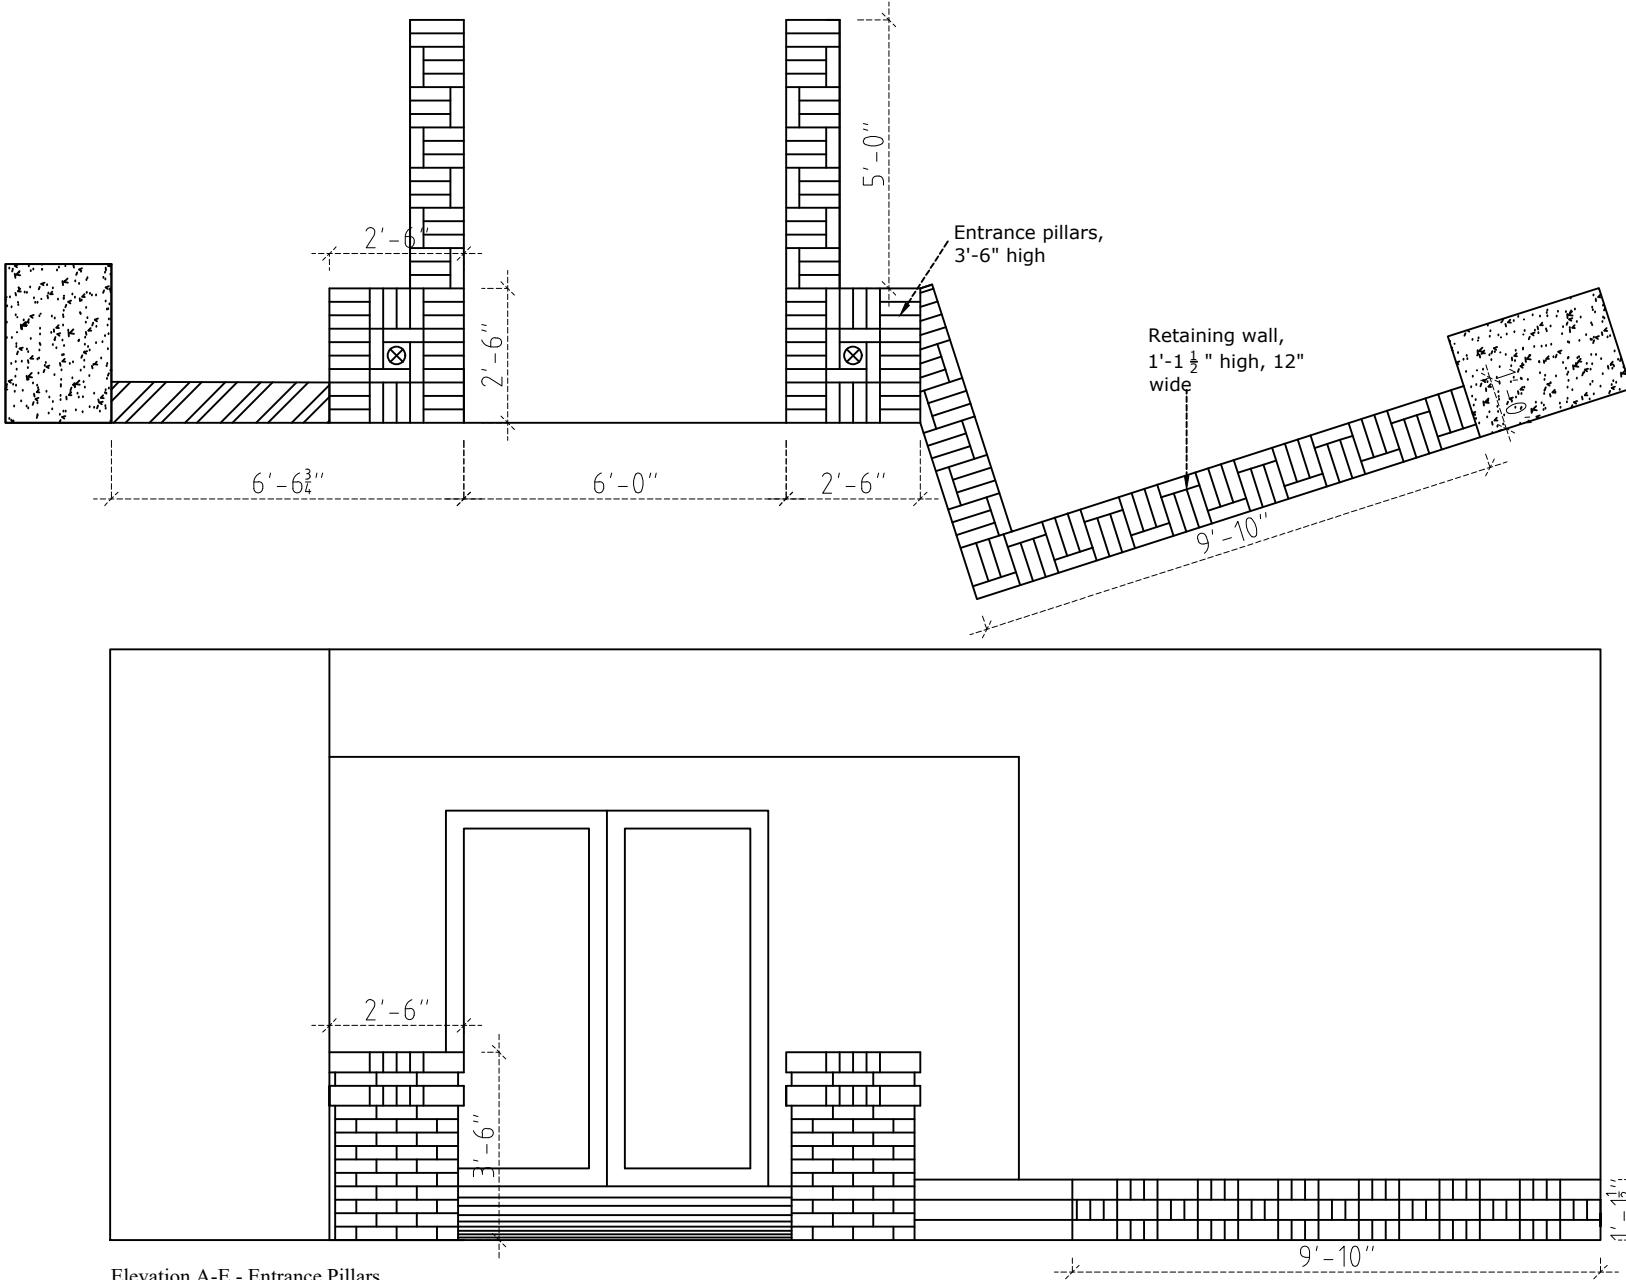

Elevation A-E - Entrance Pillars

C

D

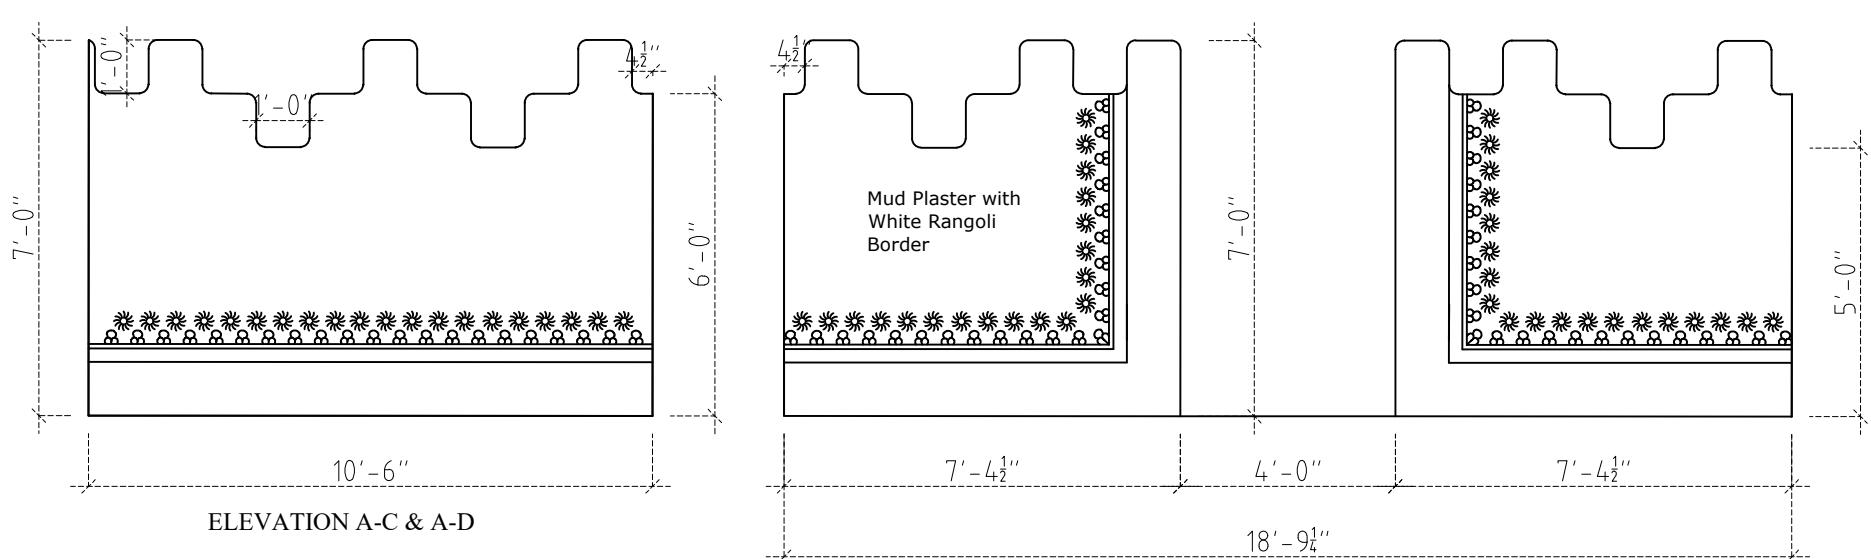

ELEVATION A-C & A-D

